


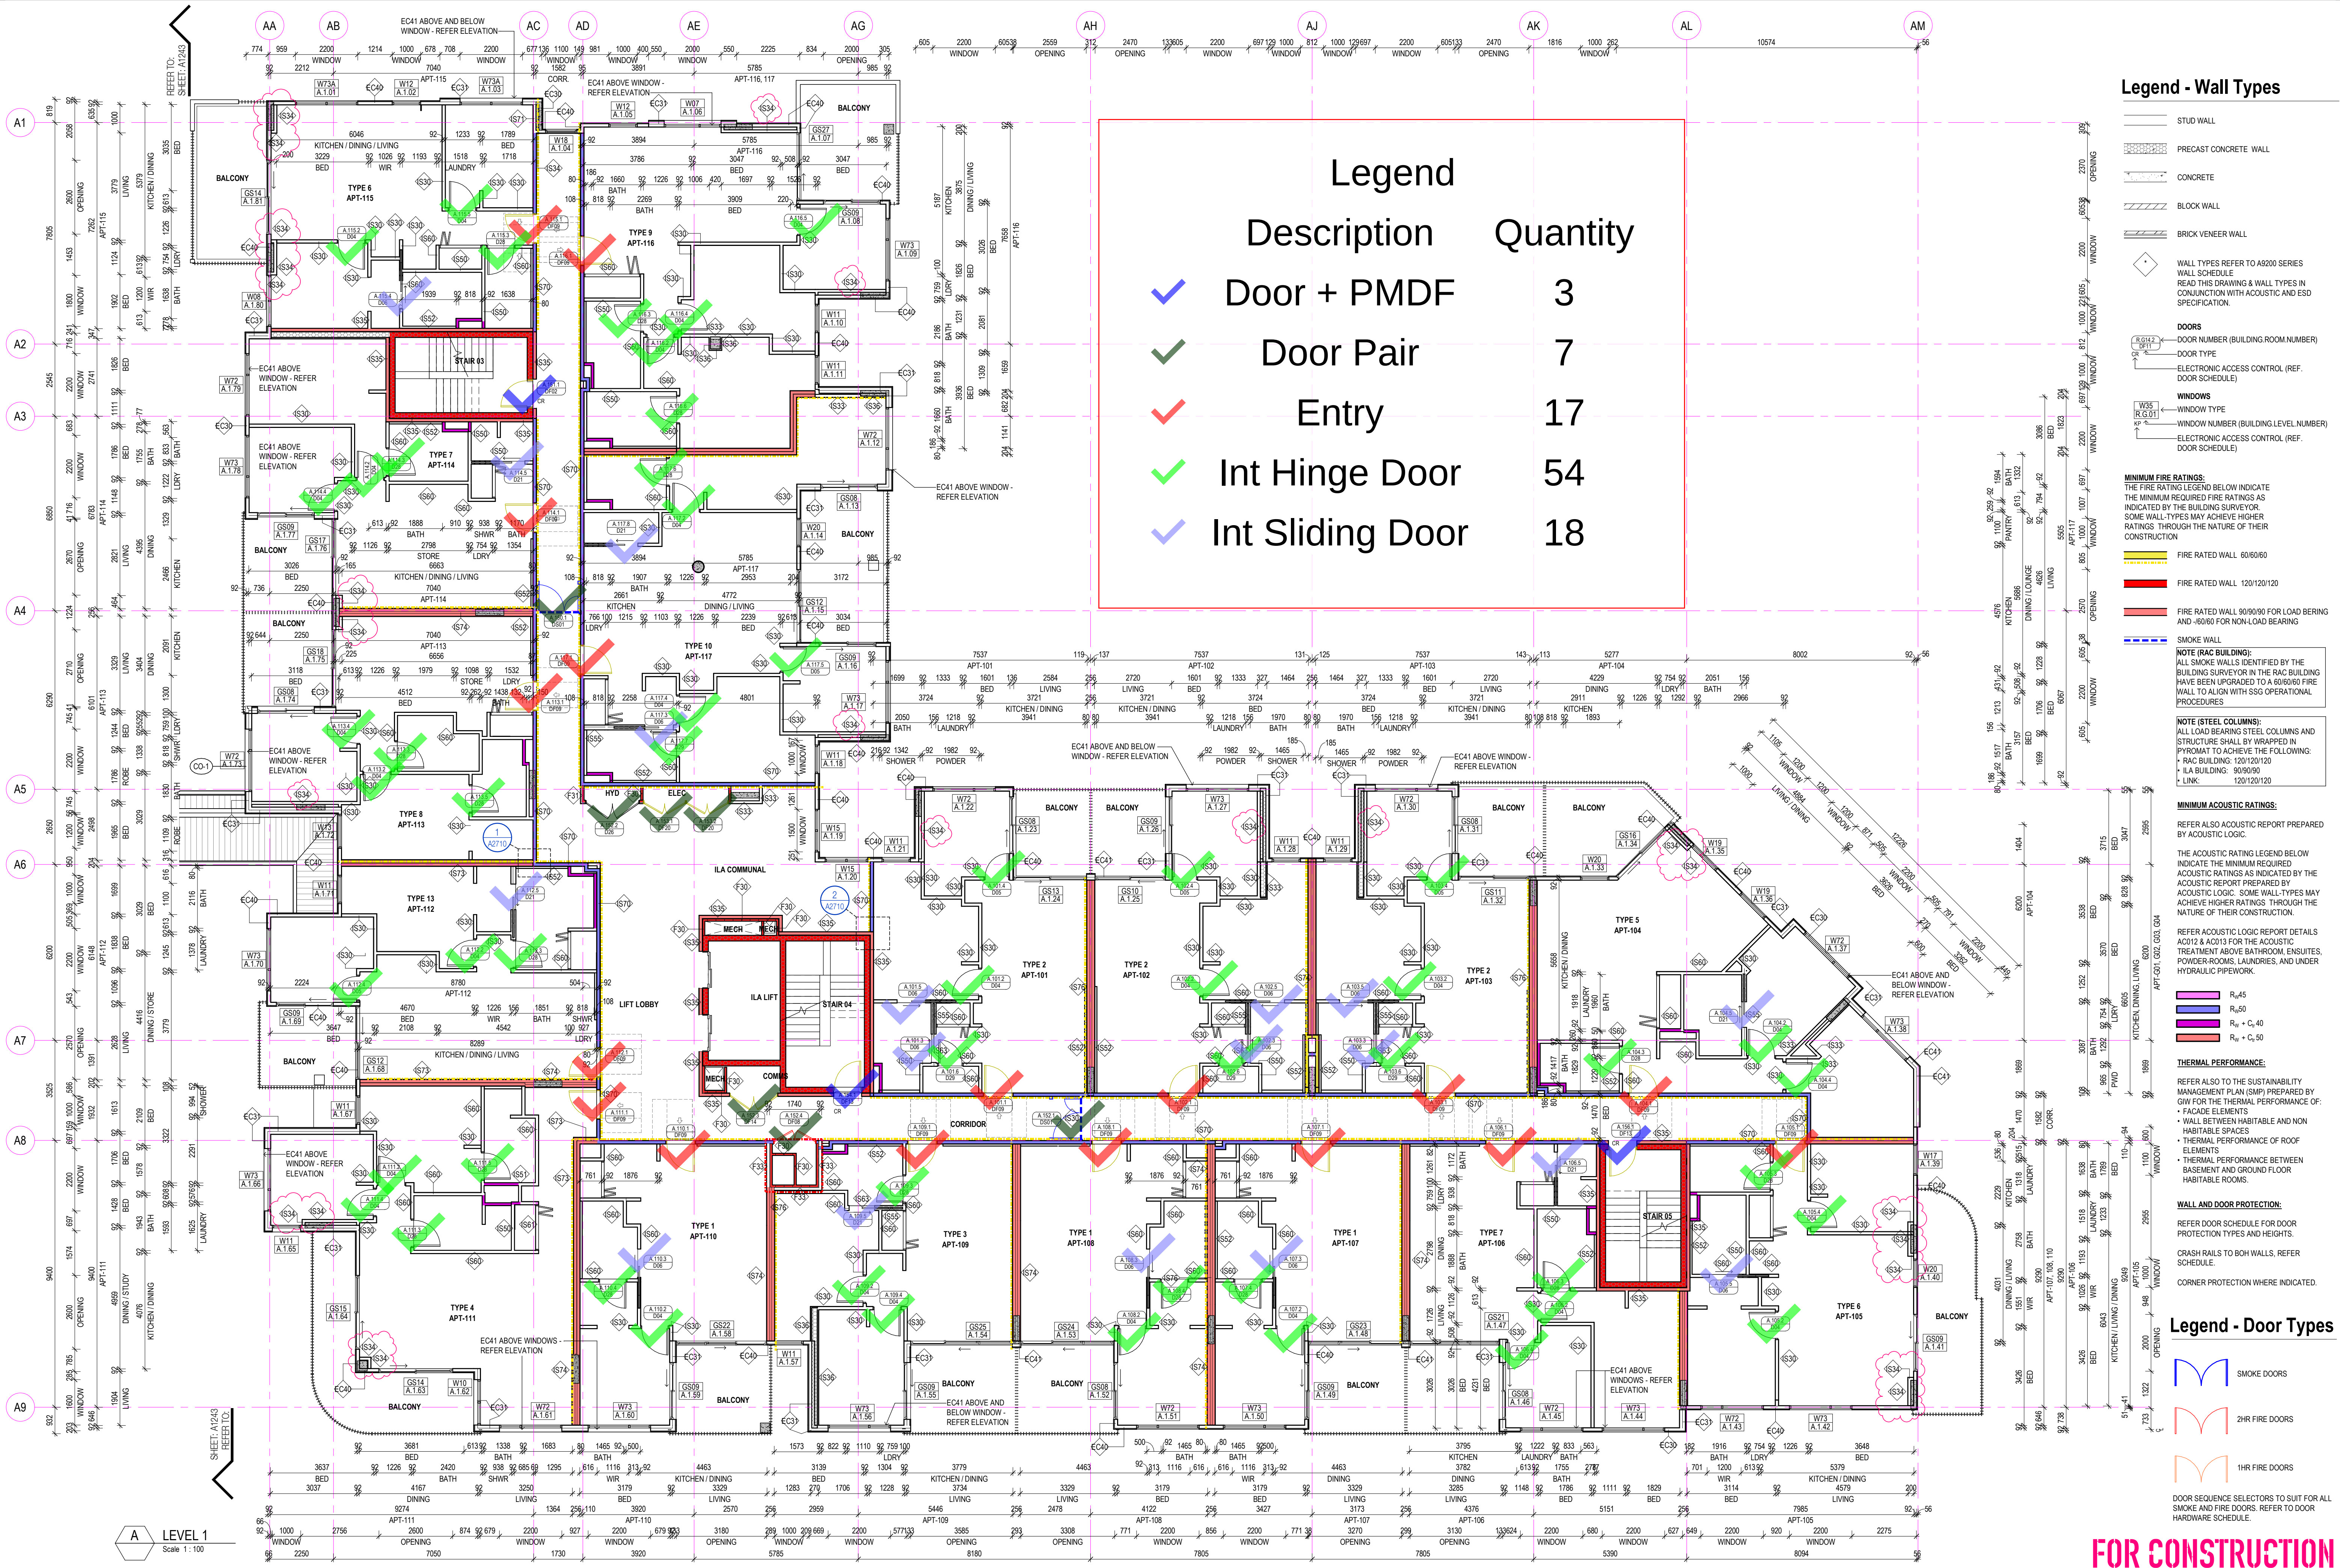

Legend - Wall Types

- STUD WALL
- PRECAST CONCRETE WALL
- CONCRETE
- BLOCK WALL
- BRICK VENEER WALL
- WALL TYPES REFER TO A9200 SERIES WALL SCHEDULE. READ THIS DRAWING & WALL TYPES IN CONJUNCTION WITH ACOUSTIC AND ESD SPECIFICATION.
- DOORS**
 - DOOR NUMBER (BUILDING ROOM NUMBER)
 - DOOR TYPE
 - ELECTRONIC ACCESS CONTROL (REF. DOOR SCHEDULE)
- WINDOWS**
 - WINDOW TYPE
 - WINDOW NUMBER (BUILDING LEVEL NUMBER)
 - ELECTRONIC ACCESS CONTROL (REF. DOOR SCHEDULE)
- MINIMUM FIRE RATINGS:**
 - THE FIRE RATING LEGEND BELOW INDICATE THE MINIMUM REQUIRED FIRE RATINGS AS INDICATED BY THE BUILDING SURVEYOR. SOME WALL TYPES MAY ACHIEVE HIGHER RATINGS THROUGH THE NATURE OF THEIR CONSTRUCTION.
 - FIRE RATED WALL 60/60/60
 - FIRE RATED WALL 120/120/120
 - FIRE RATED WALL 90/90/90 FOR LOAD BEARING AND /60/60 FOR NON-LOAD BEARING
 - SMOKE WALL
- NOTE (RAC BUILDING):**
 - ALL SMOKE WALLS IDENTIFIED BY THE BUILDING SURVEYOR IN THE RAC BUILDING HAVE BEEN UPGRADED TO A 60/60/60 FIRE WALL TO ALIGN WITH SSG OPERATIONAL PROCEDURES.
- NOTE (STEEL COLUMNS):**
 - ALL LOAD BEARING STEEL COLUMNS AND STRUCTURE SHALL BE WRAPPED IN PYROMAT TO ACHIEVE THE FOLLOWING:
 - RAC BUILDING: 120/120/120
 - ILA BUILDING: 90/90/90
 - LINK: 120/120/120
- MINIMUM ACOUSTIC RATINGS:**
 - REFER ALSO ACOUSTIC REPORT PREPARED BY ACOUSTIC LOGIC.
 - THE ACOUSTIC RATING LEGEND BELOW INDICATE THE MINIMUM REQUIRED ACOUSTIC RATINGS AS INDICATED BY THE ACOUSTIC LOGIC. SOME WALL TYPES MAY ACHIEVE HIGHER RATINGS THROUGH THE NATURE OF THEIR CONSTRUCTION.
 - REFER ACOUSTIC LOGIC REPORT DETAILS AC012 & AC013 FOR THE ACOUSTIC TREATMENT ABOVE BATHROOM, ENSUITE, POWDER ROOMS, LAUNDRIES, AND UNDER HYDRAULIC PIPEWORK.
 - R_w 45
 - R_w 50
 - R_w + C_w 40
 - R_w + C_w 50
- THERMAL PERFORMANCE:**
 - REFER ALSO TO THE SUSTAINABILITY MANAGEMENT PLAN (SMP) PREPARED BY GW FOR THE THERMAL PERFORMANCE OF:
 - FAÇADE ELEMENTS
 - WALL BETWEEN HABITABLE AND NON HABITABLE SPACES
 - THERMAL PERFORMANCE OF ROOF
 - ELEMENTS
 - THERMAL PERFORMANCE BETWEEN BASEMENT AND GROUND FLOOR HABITABLE ROOMS.
- WALL AND DOOR PROTECTION:**
 - REFER DOOR SCHEDULE FOR DOOR PROTECTION TYPES AND HEIGHTS.
 - CRASH RAILS TO BOH WALLS, REFER SCHEDULE.
 - CORNER PROTECTION WHERE INDICATED.

Legend - Door Types

- SMOKE DOORS
- 2HR FIRE DOORS
- 1HR FIRE DOORS
- DOOR SEQUENCE SELECTORS TO SUIT FOR ALL SMOKE AND FIRE DOORS. REFER TO DOOR HARDWARE SCHEDULE.

FOR CONSTRUCTION