


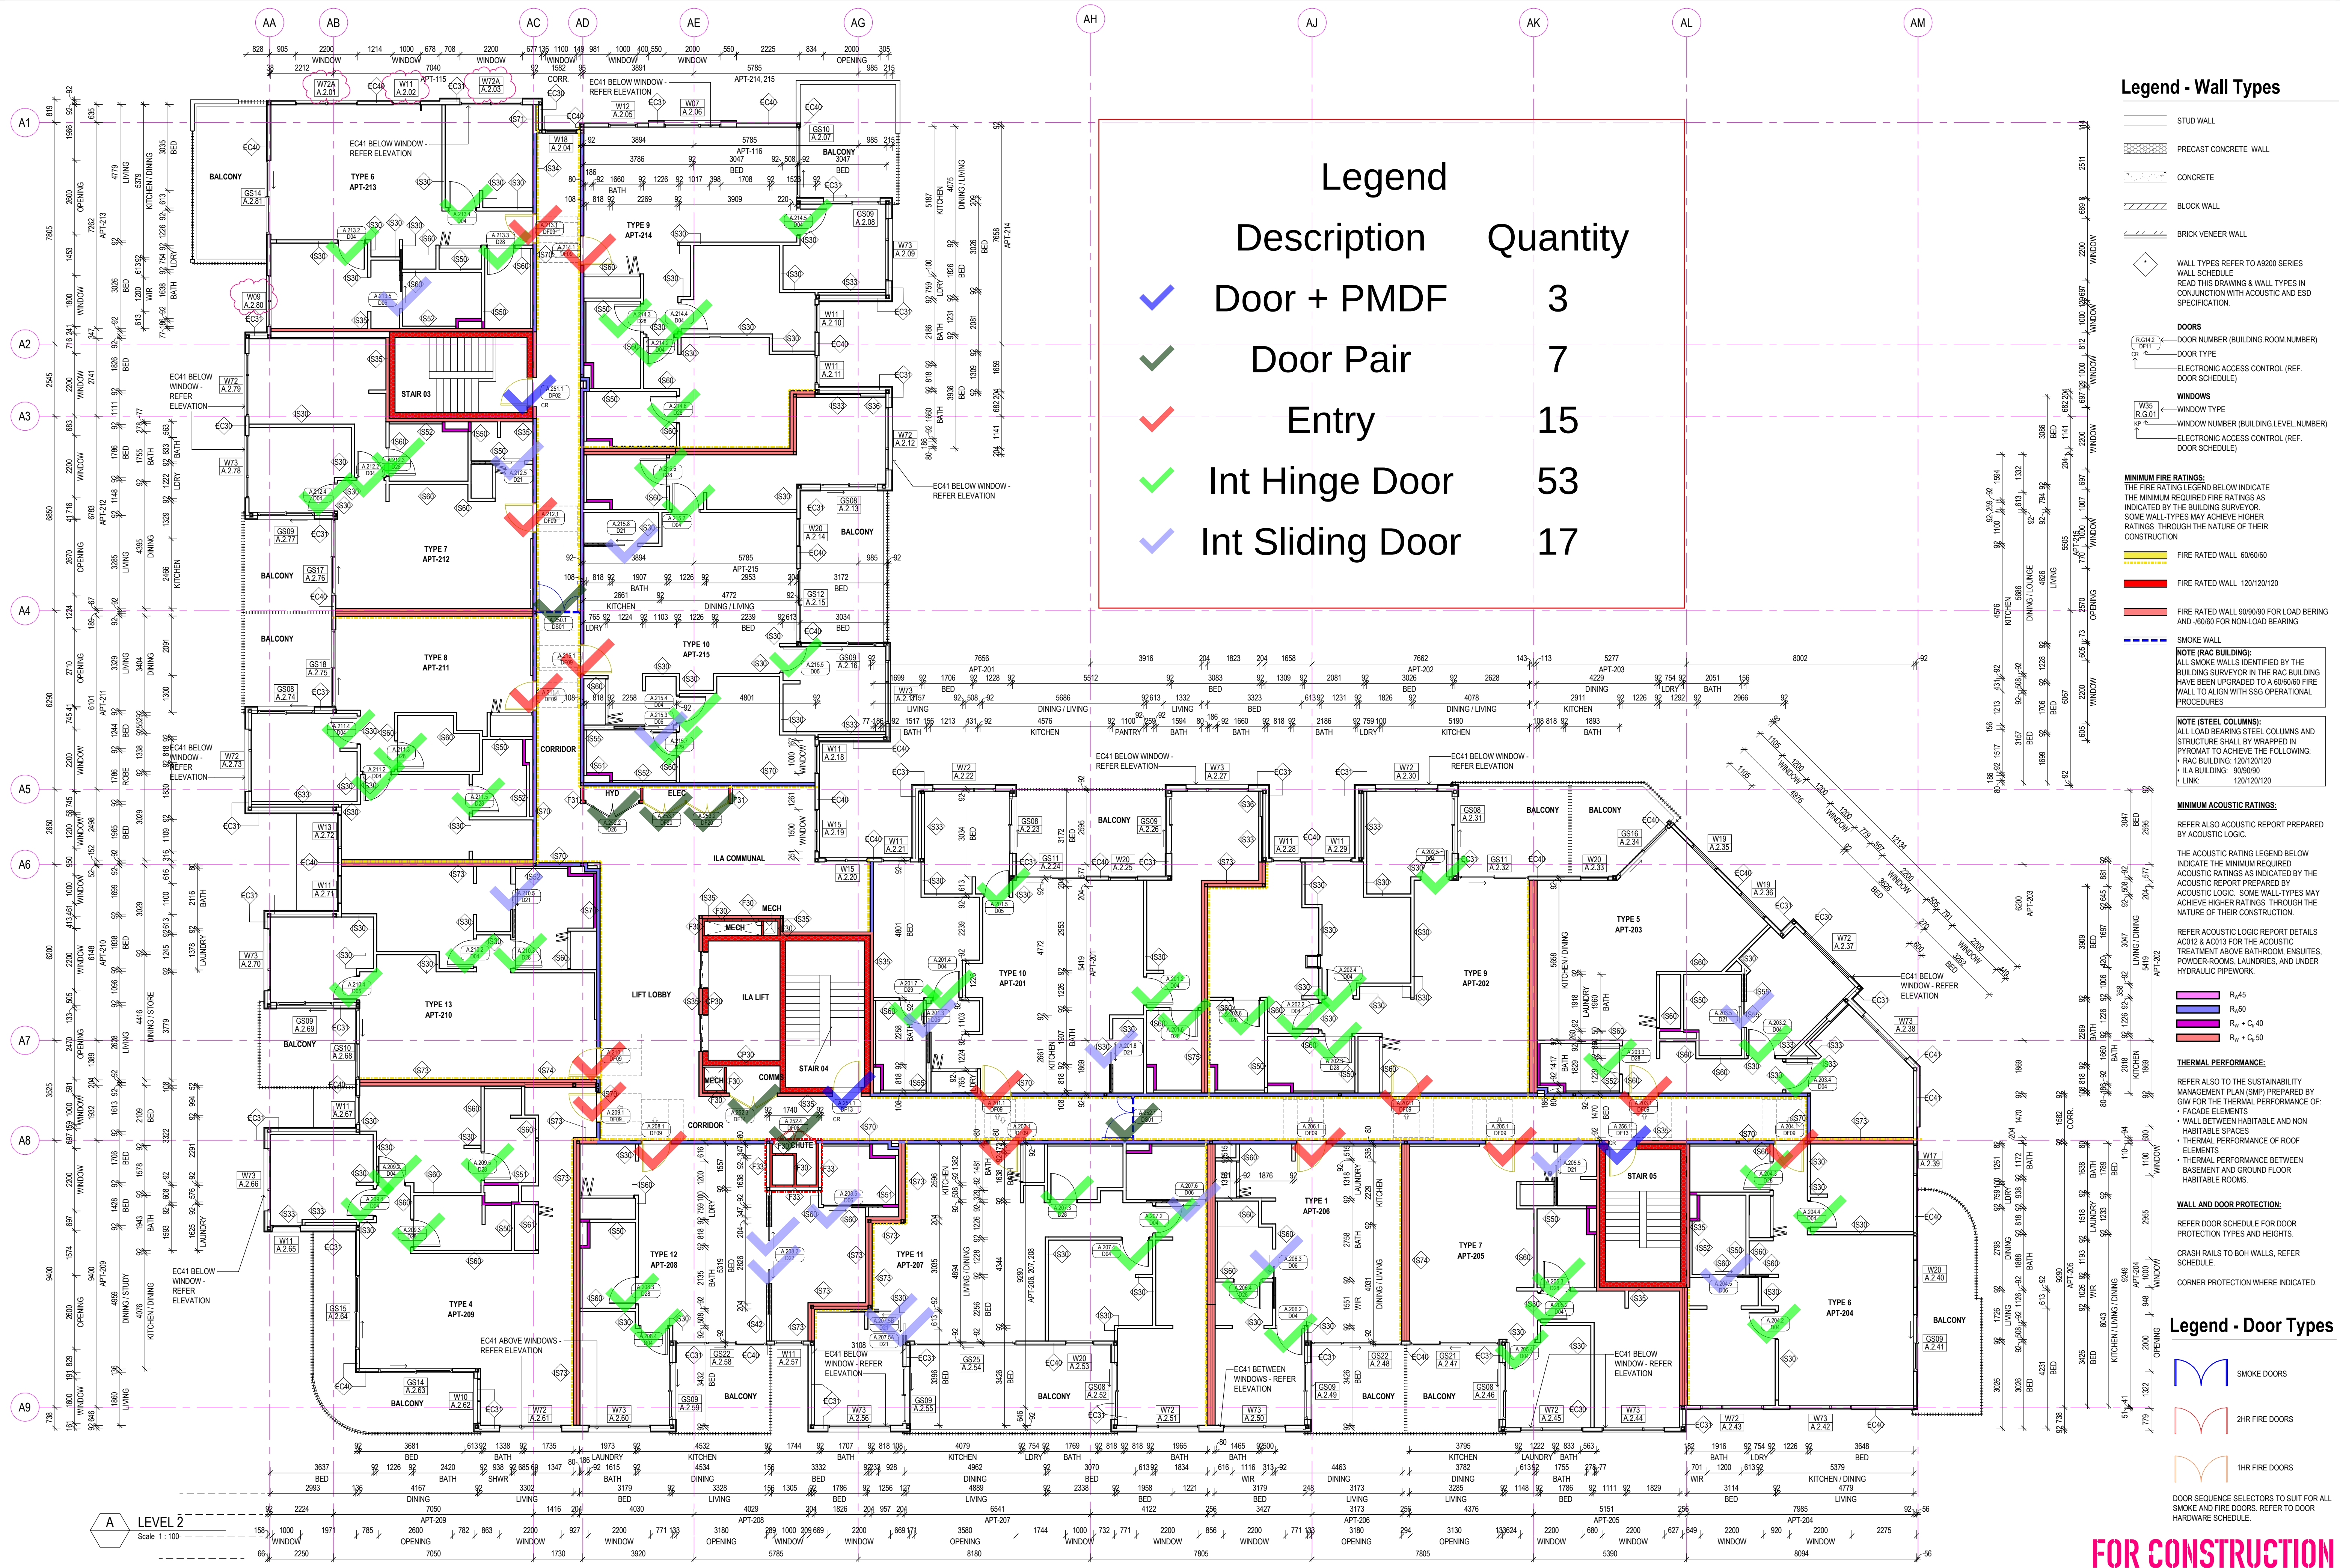

Legend - Wall Types

- STUD WALL
- PRECAST CONCRETE WALL
- CONCRETE
- BLOCK WALL
- BRICK VENEER WALL
- WALL TYPES REFER TO A9200 SERIES WALL SCHEDULE. READ THIS DRAWING & WALL TYPES IN CONJUNCTION WITH ACOUSTIC AND ESD SPECIFICATION.
- DOORS**
 - DOOR NUMBER (BUILDING ROOM NUMBER)
 - DOOR TYPE
 - ELECTRONIC ACCESS CONTROL (REF. DOOR SCHEDULE)
- WINDOWS**
 - WINDOW TYPE
 - WINDOW NUMBER (BUILDING LEVEL NUMBER)
 - ELECTRONIC ACCESS CONTROL (REF. DOOR SCHEDULE)
- MINIMUM FIRE RATINGS:**
 - THE FIRE RATING LEGEND BELOW INDICATE THE MINIMUM REQUIRED FIRE RATINGS AS INDICATED BY THE BUILDING SURVEYOR. SOME WALL-TYPES MAY ACHIEVE HIGHER RATINGS THROUGH THE NATURE OF THEIR CONSTRUCTION
 - FIRE RATED WALL 60/60/60
 - FIRE RATED WALL 120/120/120
 - FIRE RATED WALL 90/90/90 FOR LOAD BEARING AND -60/60 FOR NON-LOAD BEARING
 - SMOKE WALL
- NOTE (RAC BUILDING):**
 - ALL SMOKE WALLS IDENTIFIED BY THE BUILDING SURVEYOR IN THE RAC BUILDING HAVE BEEN UPGRADED TO A 60/60/60 FIRE WALL TO ALIGN WITH SSG OPERATIONAL PROCEDURES
- NOTE (STEEL COLUMNS):**
 - ALL LOAD BEARING STEEL COLUMNS AND STRUCTURE SHALL BE WRAPPED IN PYROMAT TO ACHIEVE THE FOLLOWING:
 - RAC BUILDING: 120/120/120
 - ILA BUILDING: 90/90/90
 - LINK: 120/120/120
- MINIMUM ACOUSTIC RATINGS:**
 - REFER ALSO ACOUSTIC REPORT PREPARED BY ACOUSTIC LOGIC.
 - THE ACOUSTIC RATING LEGEND BELOW INDICATE THE MINIMUM REQUIRED ACOUSTIC RATINGS AS INDICATED BY THE ACOUSTIC LOGIC. SOME WALL-TYPES MAY ACHIEVE HIGHER RATINGS THROUGH THE NATURE OF THEIR CONSTRUCTION.
 - REFER ACOUSTIC LOGIC REPORT DETAILS AC012 & AC013 FOR THE ACOUSTIC TREATMENT ABOVE BATHROOM, ENSUITES, POWDER-ROOMS, LAUNDRIES, AND UNDER HYDRAULIC PIPEWORK.
 - R_w45
 - R_w50
 - R_w + C_w40
 - R_w + C_w50
- THERMAL PERFORMANCE:**
 - REFER ALSO TO THE SUSTAINABILITY MANAGEMENT PLAN (SMP) PREPARED BY GW FOR THE THERMAL PERFORMANCE OF:
 - FAÇADE ELEMENTS
 - WALL BETWEEN HABITABLE AND NON HABITABLE SPACES
 - THERMAL PERFORMANCE OF ROOF ELEMENTS
 - THERMAL PERFORMANCE BETWEEN BASEMENT AND GROUND FLOOR HABITABLE ROOMS.
- WALL AND DOOR PROTECTION:**
 - REFER DOOR SCHEDULE FOR DOOR PROTECTION TYPES AND HEIGHTS.
 - CRASH RAILS TO BOH WALLS, REFER SCHEDULE.
 - CORNER PROTECTION WHERE INDICATED.

Legend - Door Types

- SMOKE DOORS
- 2HR FIRE DOORS
- 1HR FIRE DOORS
- DOOR SEQUENCE SELECTORS TO SUIT FOR ALL SMOKE AND FIRE DOORS. REFER TO DOOR HARDWARE SCHEDULE.

FOR CONSTRUCTION

Revision/Issue	Date
C3 ISSUE FOR CONSTRUCTION	2026.03.24
C4 ISSUE FOR CONSTRUCTION	2026.04.17
C5 ISSUE FOR CONSTRUCTION	2026.05.06
C6 ISSUE FOR CONSTRUCTION - ESD NOTES	2026.05.20

Clarke Hopkins Clarke
Melbourne | Wurundjeri
L3, Melbourne Connect
700 Swarston Street
Carlton VIC 3063
Telephone (03) 9419 4340
Email studio@chc.com.au
www.chc.com.au

Sydney | Gadigal Country
Suite 3, Ground Floor
91 Campbell Street
Surry Hills NSW 2010
Telephone (02) 9221 9200
Email studio@chc.com.au
www.chc.com.au

Scale	1 : 100 @ A1
Date	01/03/2024
Drawn	AC
Architect	EL



Project
Summerset Oakleigh
52 Golf Road, Oakleigh South, VIC

Drawing
Wall Set out Plan - Second Floor

Drawing No.
230185/A2242
C6