


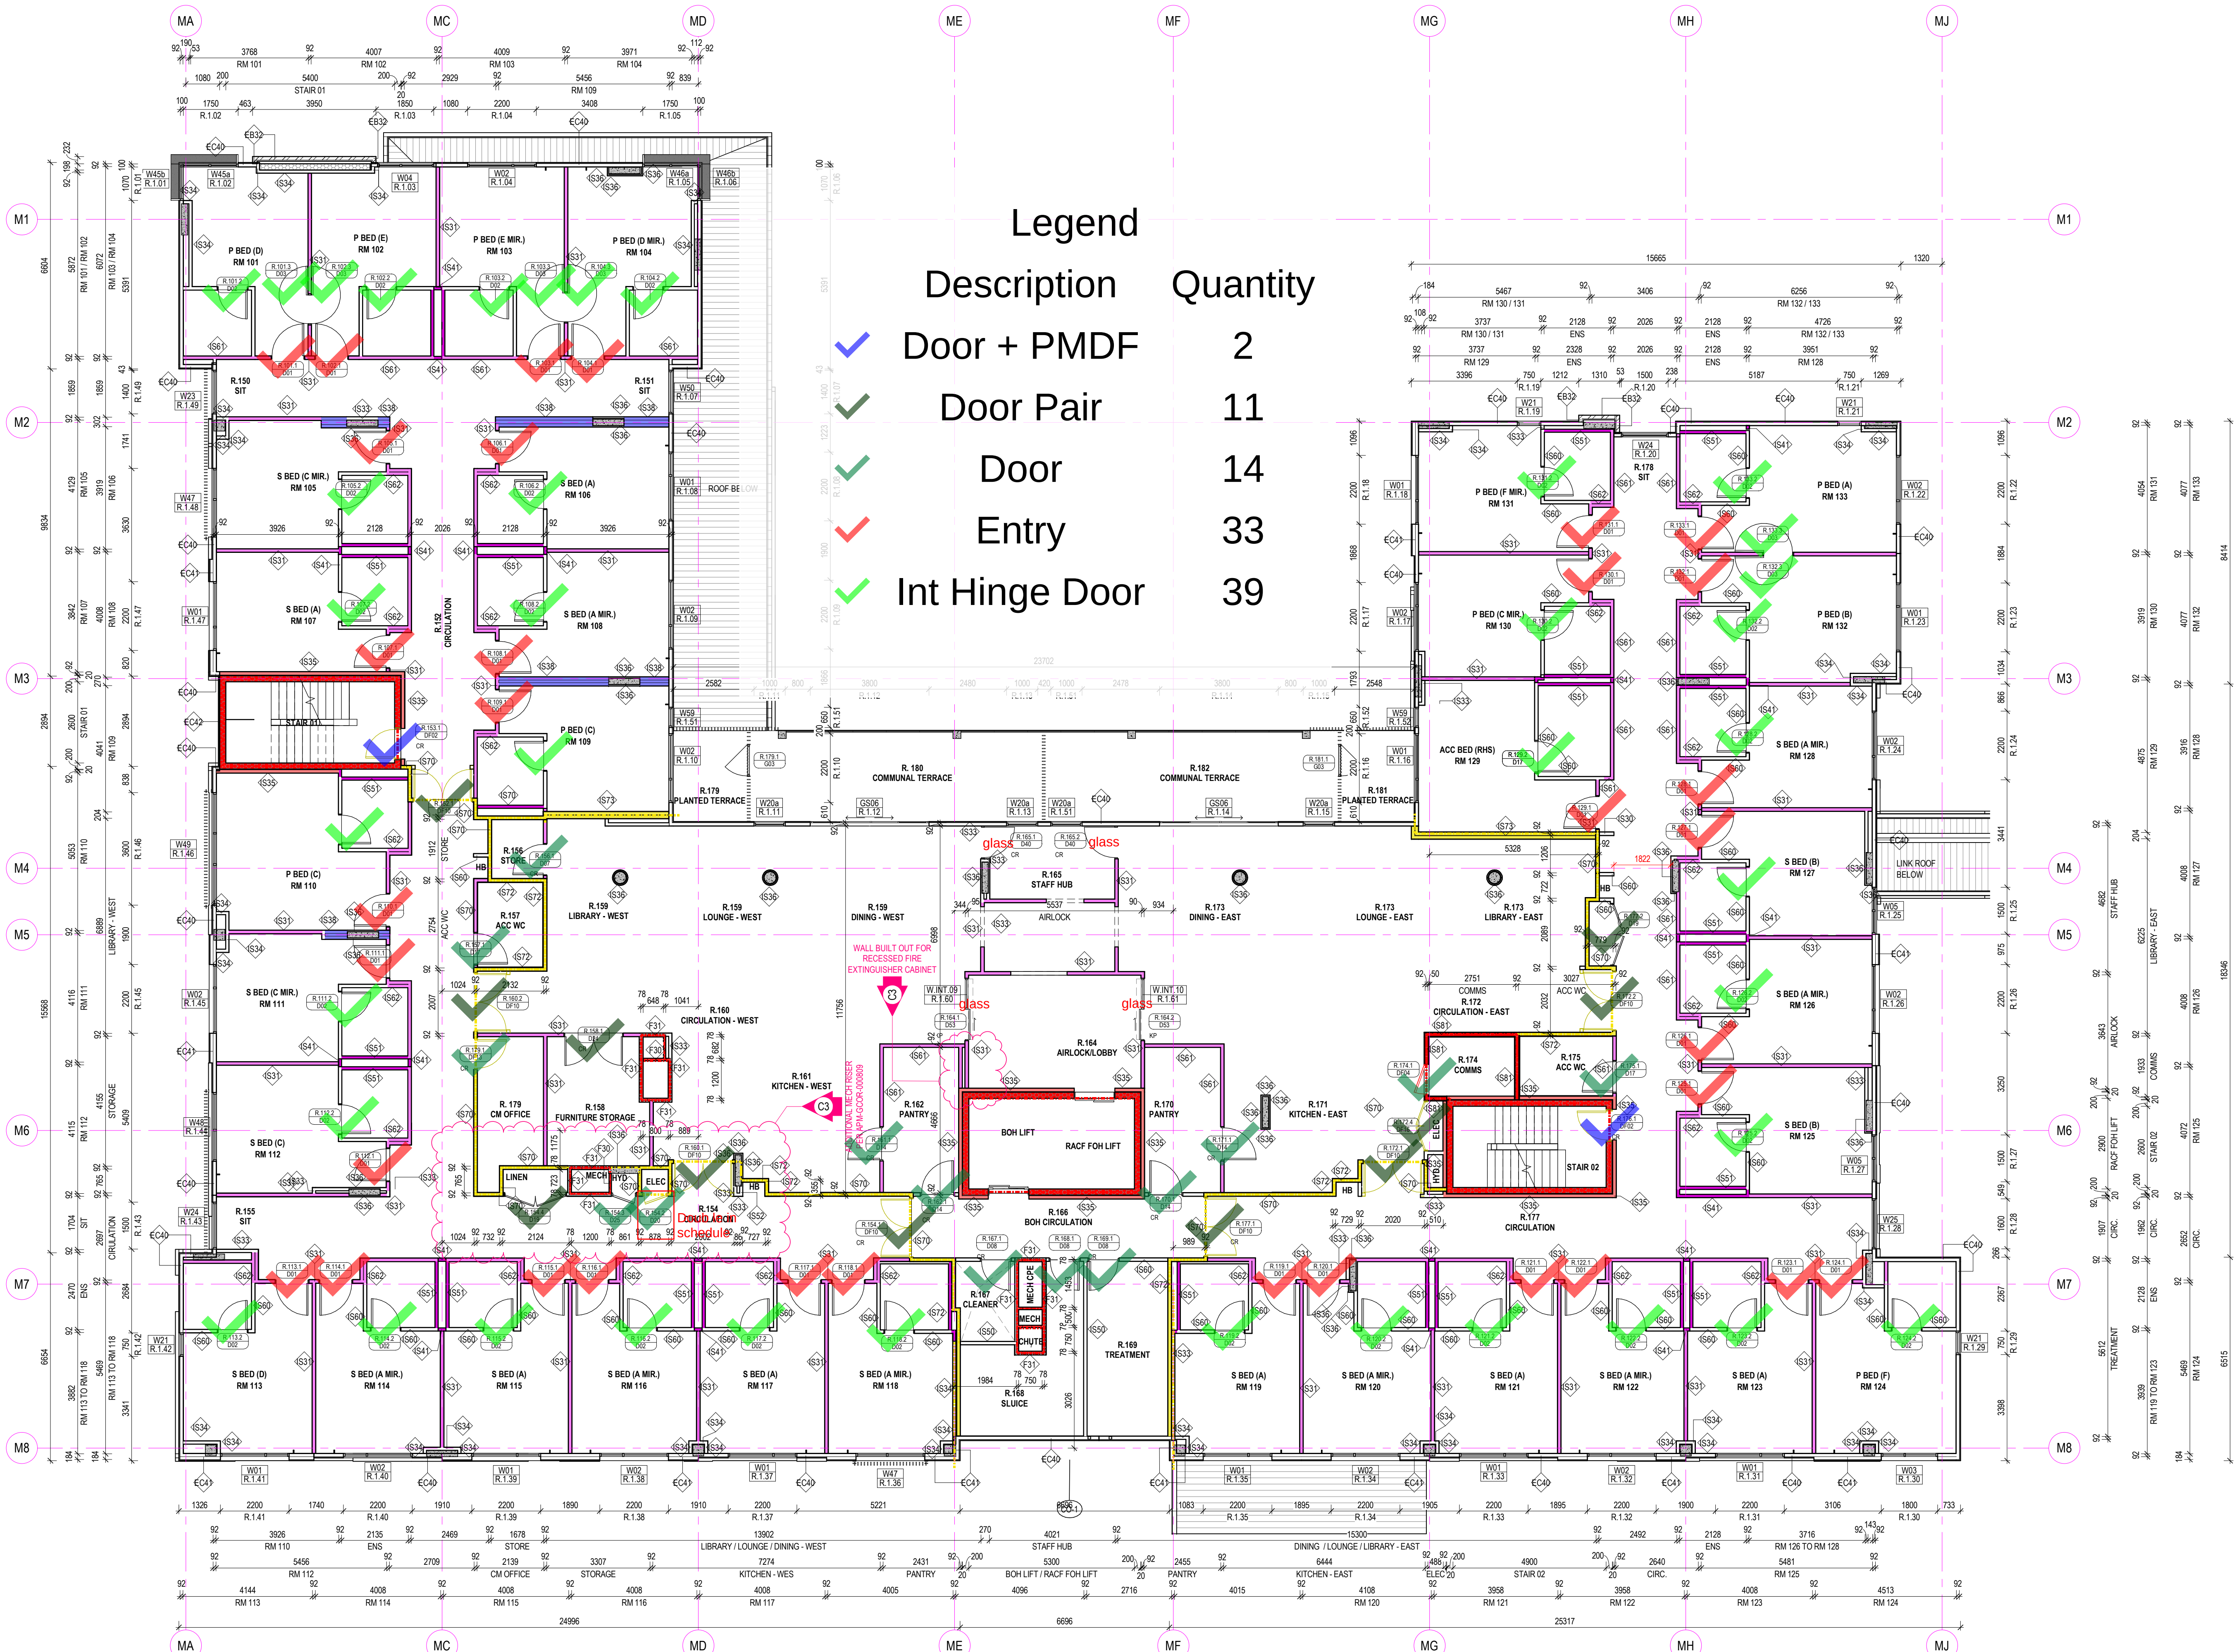

Legend		
Description	Quantity	
Door + PMDF	2	
Door Pair	11	
Door Entry	14	
Int Hinge Door	33	
	39	

Legend - Wall Types

- STUD WALL
- PRECAST CONCRETE WALL
- CONCRETE
- BLOCK WALL
- BRICK VENEER WALL

WALL TYPES REFER TO A9200 SERIES
READ THIS DRAWING & WALL TYPES IN
CONJUNCTION WITH ACOUSTIC AND ESD
SPECIFICATION.

DOORS

DOOR NUMBER (BUILDING ROOM NUMBER)
DOOR TYPE
ELECTRONIC ACCESS CONTROL (REF.
DOOR SCHEDULE)

WINDOWS

WINDOW TYPE
WINDOW NUMBER (BUILDING LEVEL NUMBER)
ELECTRONIC ACCESS CONTROL (REF.
DOOR SCHEDULE)

MINIMUM FIRE RATINGS:

THE FIRE RATING LEGEND BELOW INDICATE
THE MINIMUM REQUIRED FIRE RATINGS AS
INDICATED BY THE BUILDING SURVEYOR.
SOME WALL TYPES MAY ACHIEVE HIGHER
RATINGS THROUGH THE NATURE OF THEIR
CONSTRUCTION

- FIRE RATED WALL 60/60/60
- FIRE RATED WALL 120/120/120
- FIRE RATED WALL 90/90/90 FOR LOAD BEARING
AND /60/60 FOR NON-LOAD BEARING
- SMOKE WALL

NOTE (RAC BUILDING):
ALL SMOKE WALLS IDENTIFIED BY THE
BUILDING SURVEYOR IN THE RAC BUILDING
HAVE BEEN UPGRADED TO A 60/60/60 FIRE
WALL TO ALIGN WITH SSG OPERATIONAL
PROCEDURES

NOTE (STEEL COLUMNS):
ALL LOAD BEARING STEEL COLUMNS AND
STRUCTURE SHALL BE WRAPPED IN
PYROMAT TO ACHIEVE THE FOLLOWING:
• RAC BUILDING: 120/120/120
• LA BUILDING: 90/90/90
• LINK: 120/120/120

MINIMUM ACOUSTIC RATINGS:

REFER ALSO ACOUSTIC REPORT PREPARED
BY ACOUSTIC LOGIC.

THE ACOUSTIC RATING LEGEND BELOW
INDICATE THE MINIMUM REQUIRED
ACOUSTIC RATINGS AS INDICATED BY THE
ACOUSTIC REPORT PREPARED BY
ACOUSTIC LOGIC. SOME WALL TYPES MAY
ACHIEVE HIGHER RATINGS THROUGH THE
NATURE OF THEIR CONSTRUCTION.

REFER ACOUSTIC LOGIC REPORT DETAILS
AC012 & AC013 FOR THE ACOUSTIC
TREATMENT ABOVE BATHROOM, ENSUITE,
POWDER-ROOMS, LAUNDRIES, AND UNDER
HYDRAULIC PIPEWORK.

- R_w45
- R_w50
- R_w + C_w40
- R_w + C_w50

THERMAL PERFORMANCE:

REFER ALSO TO THE SUSTAINABILITY
MANAGEMENT PLAN (SMP) PREPARED BY
GIW FOR THE THERMAL PERFORMANCE OF:
• FACADE ELEMENTS
• WALL BETWEEN HABITABLE AND NON
HABITABLE SPACES
• THERMAL PERFORMANCE OF ROOF
ELEMENTS
• THERMAL PERFORMANCE BETWEEN
BASEMENT AND GROUND FLOOR
HABITABLE ROOMS.

WALL AND DOOR PROTECTION:

REFER DOOR SCHEDULE FOR DOOR
PROTECTION TYPES AND HEIGHTS.

CRASH RAILS TO BOH WALLS, REFER
SCHEDULE.

CORNER PROTECTION WHERE INDICATED.

Legend - Door Types

- SMOKE DOORS
- 2HR FIRE DOORS
- 1HR FIRE DOORS

DOOR SEQUENCE SELECTORS TO SUIT FOR ALL SMOKE AND
FIRE DOORS. REFER TO DOOR HARDWARE SCHEDULE.

FOR CONSTRUCTION