


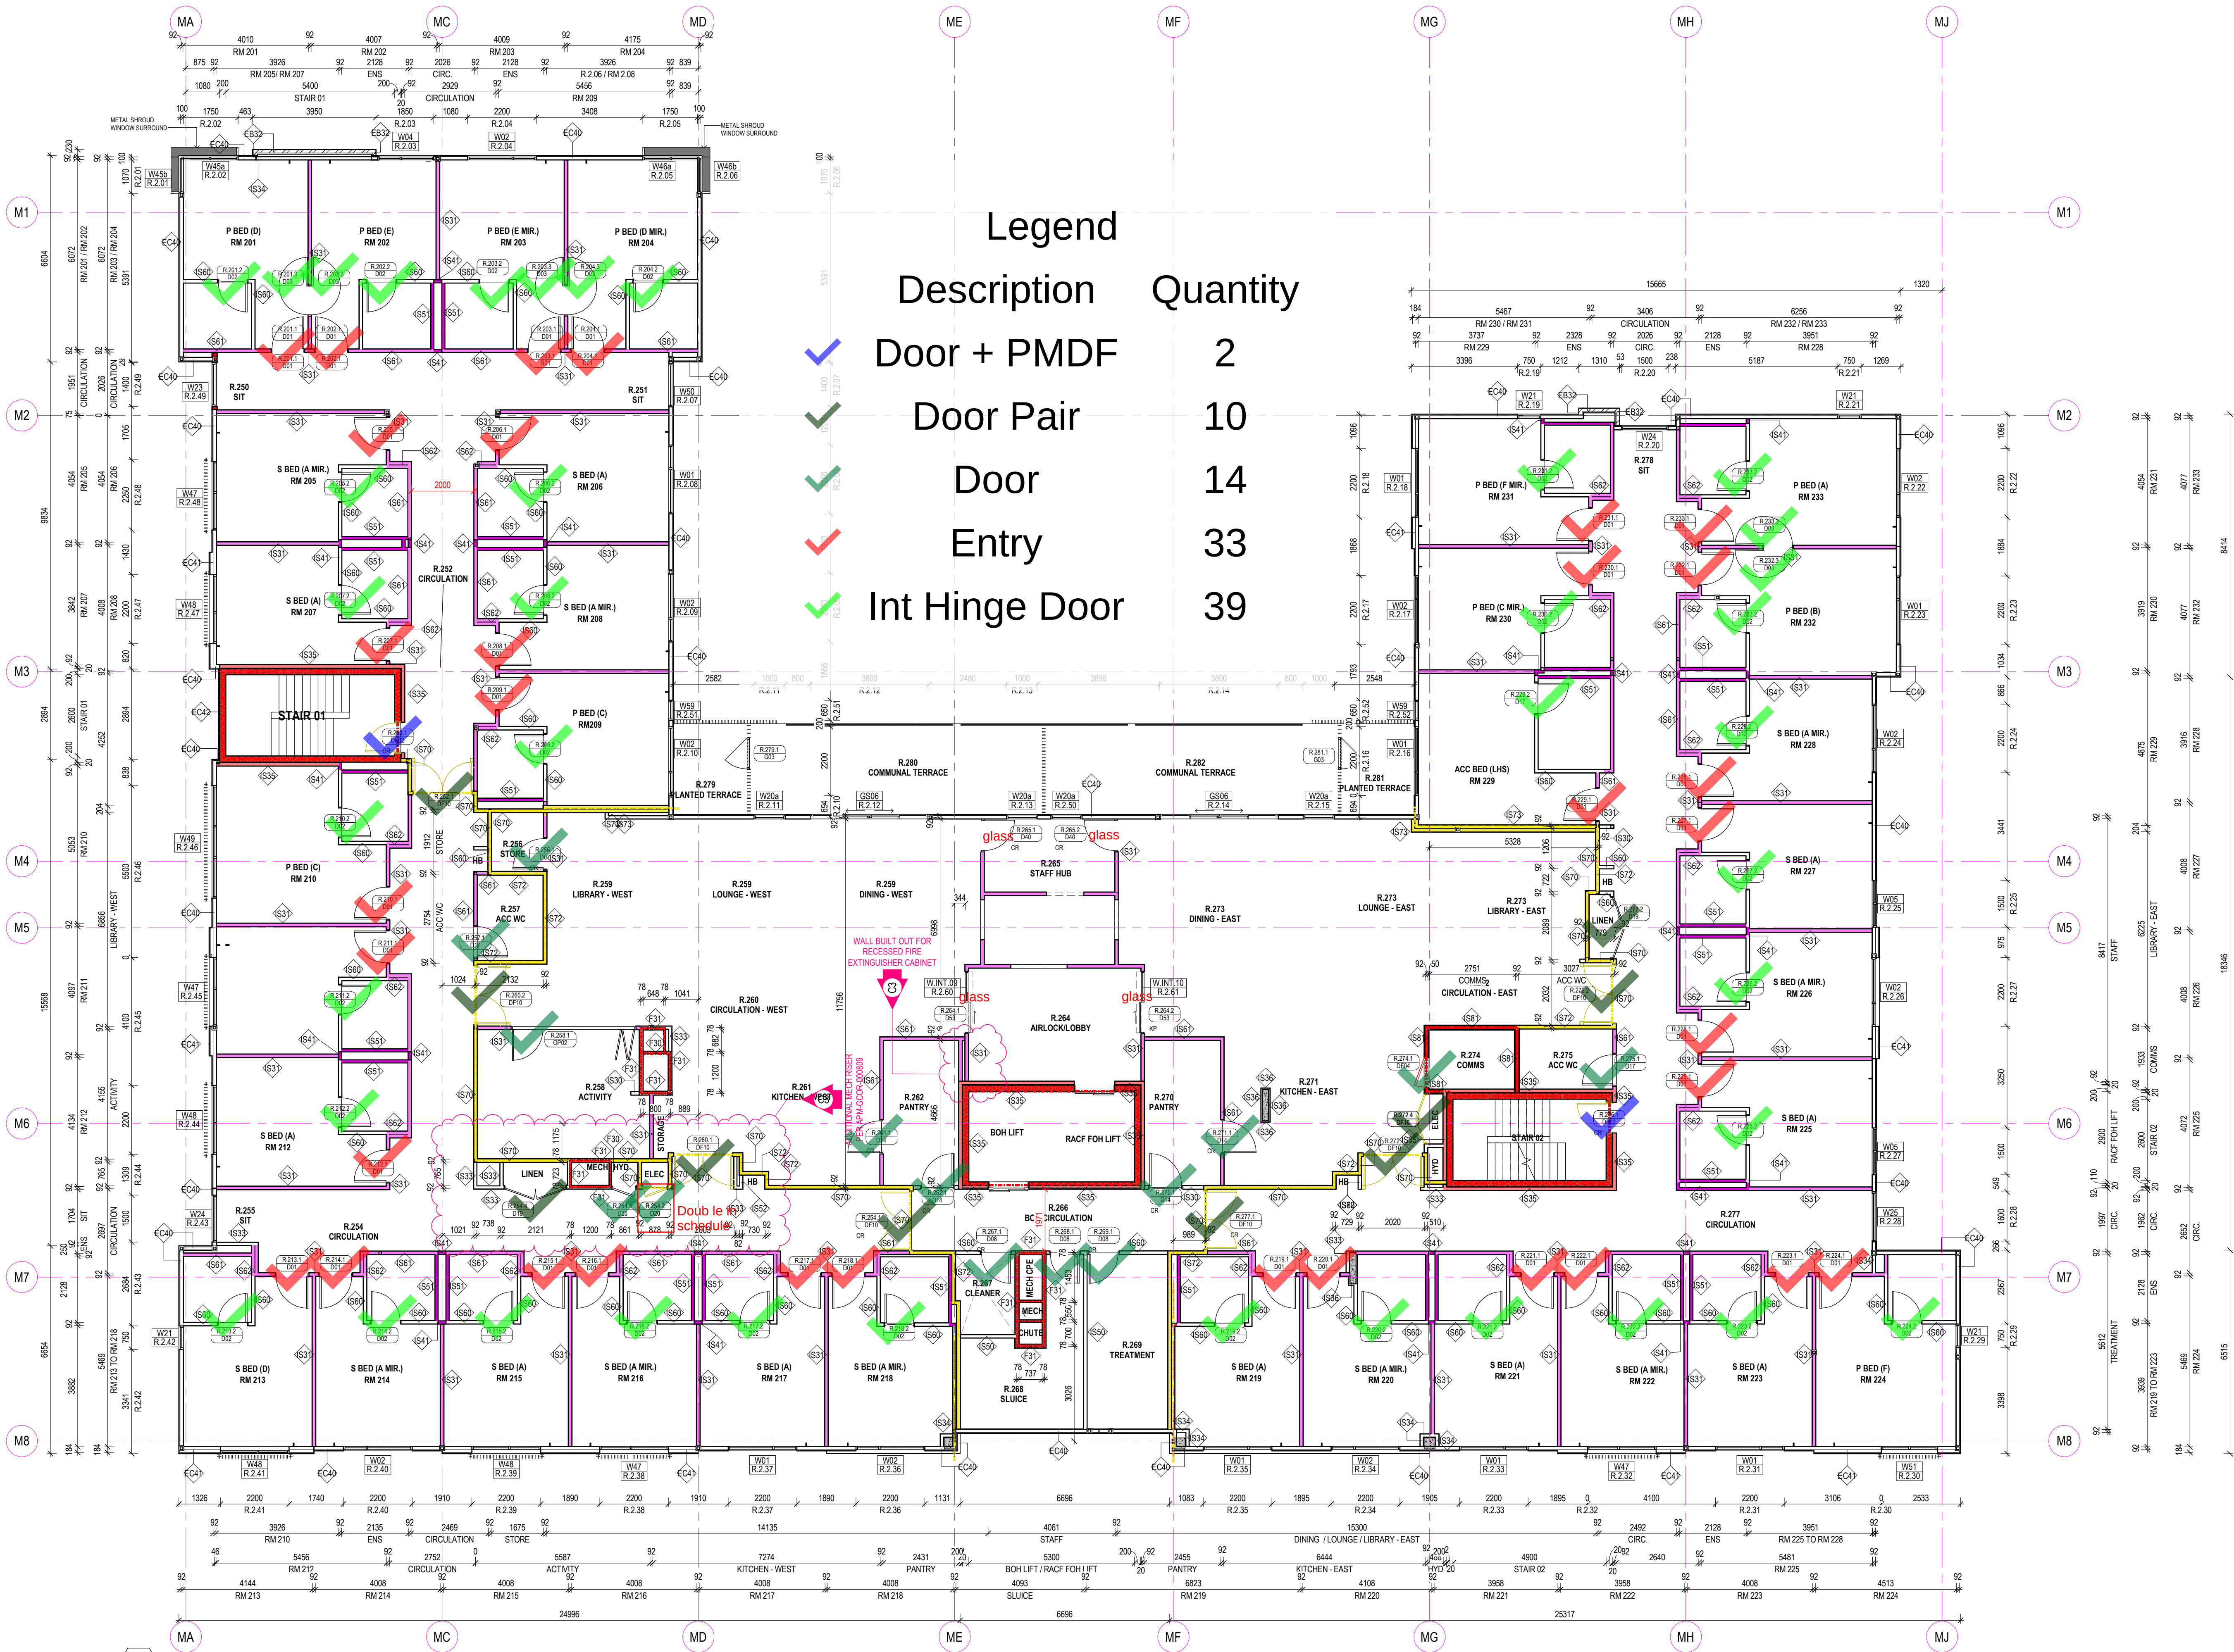

Legend		
Description	Quantity	
Door + PMDF	2	
Door Pair	10	
Door	14	
Entry	33	
Int Hinge Door	39	

Legend - Wall Types

- STUD WALL
- PRECAST CONCRETE WALL
- CONCRETE
- BLOCK WALL
- BRICK VENEER WALL
- WALL TYPES REFER TO A9200 SERIES WALL SCHEDULE. READ THIS DRAWING & WALL TYPES IN CONJUNCTION WITH ACOUSTIC AND ESD SPECIFICATION.
- DOORS
 - DOOR NUMBER (BUILDING ROOM NUMBER)
 - DOOR TYPE
 - ELECTRONIC ACCESS CONTROL (REF. DOOR SCHEDULE)
- WINDOWS
 - WINDOW TYPE
 - WINDOW NUMBER (BUILDING LEVEL NUMBER)
 - ELECTRONIC ACCESS CONTROL (REF. DOOR SCHEDULE)

- MINIMUM FIRE RATINGS:**
THE FIRE RATING LEGEND BELOW INDICATE THE MINIMUM REQUIRED FIRE RATINGS AS INDICATED BY THE BUILDING SURVEYOR. SOME WALL TYPES MAY ACHIEVE HIGHER RATINGS THROUGH THE NATURE OF THEIR CONSTRUCTION.
- FIRE RATED WALL 60/60/60
 - FIRE RATED WALL 120/120/120
 - FIRE RATED WALL 90/90/90 FOR LOAD BEARING AND -60/60 FOR NON-LOAD BEARING
 - SMOKE WALL
- NOTE (RAC BUILDING):**
ALL LOAD BEARING STEEL COLUMNS AND STRUCTURE SHALL BE WRAPPED IN PYROMAT TO ACHIEVE THE FOLLOWING:
• RAC BUILDING: 120/120/120
• ILA BUILDING: 90/90/90
• LINK: 120/120/120
- NOTE (STEEL COLUMNS):**
ALL LOAD BEARING STEEL COLUMNS AND STRUCTURE SHALL BE WRAPPED IN PYROMAT TO ACHIEVE THE FOLLOWING:
• RAC BUILDING: 120/120/120
• ILA BUILDING: 90/90/90
• LINK: 120/120/120

- MINIMUM ACOUSTIC RATINGS:**
REFER ALSO ACOUSTIC REPORT PREPARED BY ACOUSTIC LOGIC.
- THE ACOUSTIC RATING LEGEND BELOW INDICATE THE MINIMUM REQUIRED ACOUSTIC RATINGS AS INDICATED BY THE ACOUSTIC REPORT PREPARED BY ACOUSTIC LOGIC. SOME WALL TYPES MAY ACHIEVE HIGHER RATINGS THROUGH THE NATURE OF THEIR CONSTRUCTION.
- REFER ACOUSTIC LOGIC REPORT DETAILS AC012 & AC013 FOR THE ACOUSTIC TREATMENT ABOVE BATHROOM, ENSUITE, POWDER-ROOMS, LAUNDRIES, AND UNDER HYDRAULIC PIPEWORK.
- R_w45
 - R_w50
 - R_w + C_w40
 - R_w + C_w50
- THERMAL PERFORMANCE:**
REFER ALSO TO THE SUSTAINABILITY MANAGEMENT PLAN (SMP) PREPARED BY GIW FOR THE THERMAL PERFORMANCE OF:
• FACADE ELEMENTS
• WALL BETWEEN HABITABLE AND NON HABITABLE SPACES
• THERMAL PERFORMANCE OF ROOF ELEMENTS
• THERMAL PERFORMANCE BETWEEN BASEMENT AND GROUND FLOOR HABITABLE ROOMS.
- WALL AND DOOR PROTECTION:**
REFER DOOR SCHEDULE FOR DOOR PROTECTION TYPES AND HEIGHTS.
CRASH RAILS TO BOH WALLS, REFER SCHEDULE.
CORNER PROTECTION WHERE INDICATED.

Legend - Door Types

- SMOKE DOORS
 - 2HR FIRE DOORS
 - 1HR FIRE DOORS
- DOOR SEQUENCE SELECTORS TO SUIT FOR ALL SMOKE AND FIRE DOORS. REFER TO DOOR HARDWARE SCHEDULE.

FOR CONSTRUCTION

Drawing No. 230185/A1244

Revision/Issue	Date
P5 ISSUE FOR CONTRACT	2025.10.10
C1 ISSUE FOR CONSTRUCTION	2025.12.19
C2 ISSUE FOR CONSTRUCTION - DOOR SCHEDULE	2026.03.16
C3 ISSUE FOR CONSTRUCTION	2026.03.24

Clarke Hopkins Clarke
Melbourne | Wurundjeri
L3, Melbourne Connect
700 Swanston Street
Carlton VIC 3065
Telephone (03) 9419 4340
Email studio@chc.com.au
www.chc.com.au

Sydney | Gadigal Country
Suite 3, Ground Floor
91 Campbell Street
Sunny Hills NSW 2010
Telephone (02) 9221 9200
Email studio@chc.com.au
www.chc.com.au

Scale	1:100 @ A1
Date	01/03/2024
Drawn	AC
Architect	EL

Project
Summerset Oakleigh
52 Golf Road, Oakleigh South, VIC

Drawing
Wall Set out Plan - Second Floor

Drawing No. 230185/A1244

C3