


EXTERNAL WALLS (FIRE RATED)

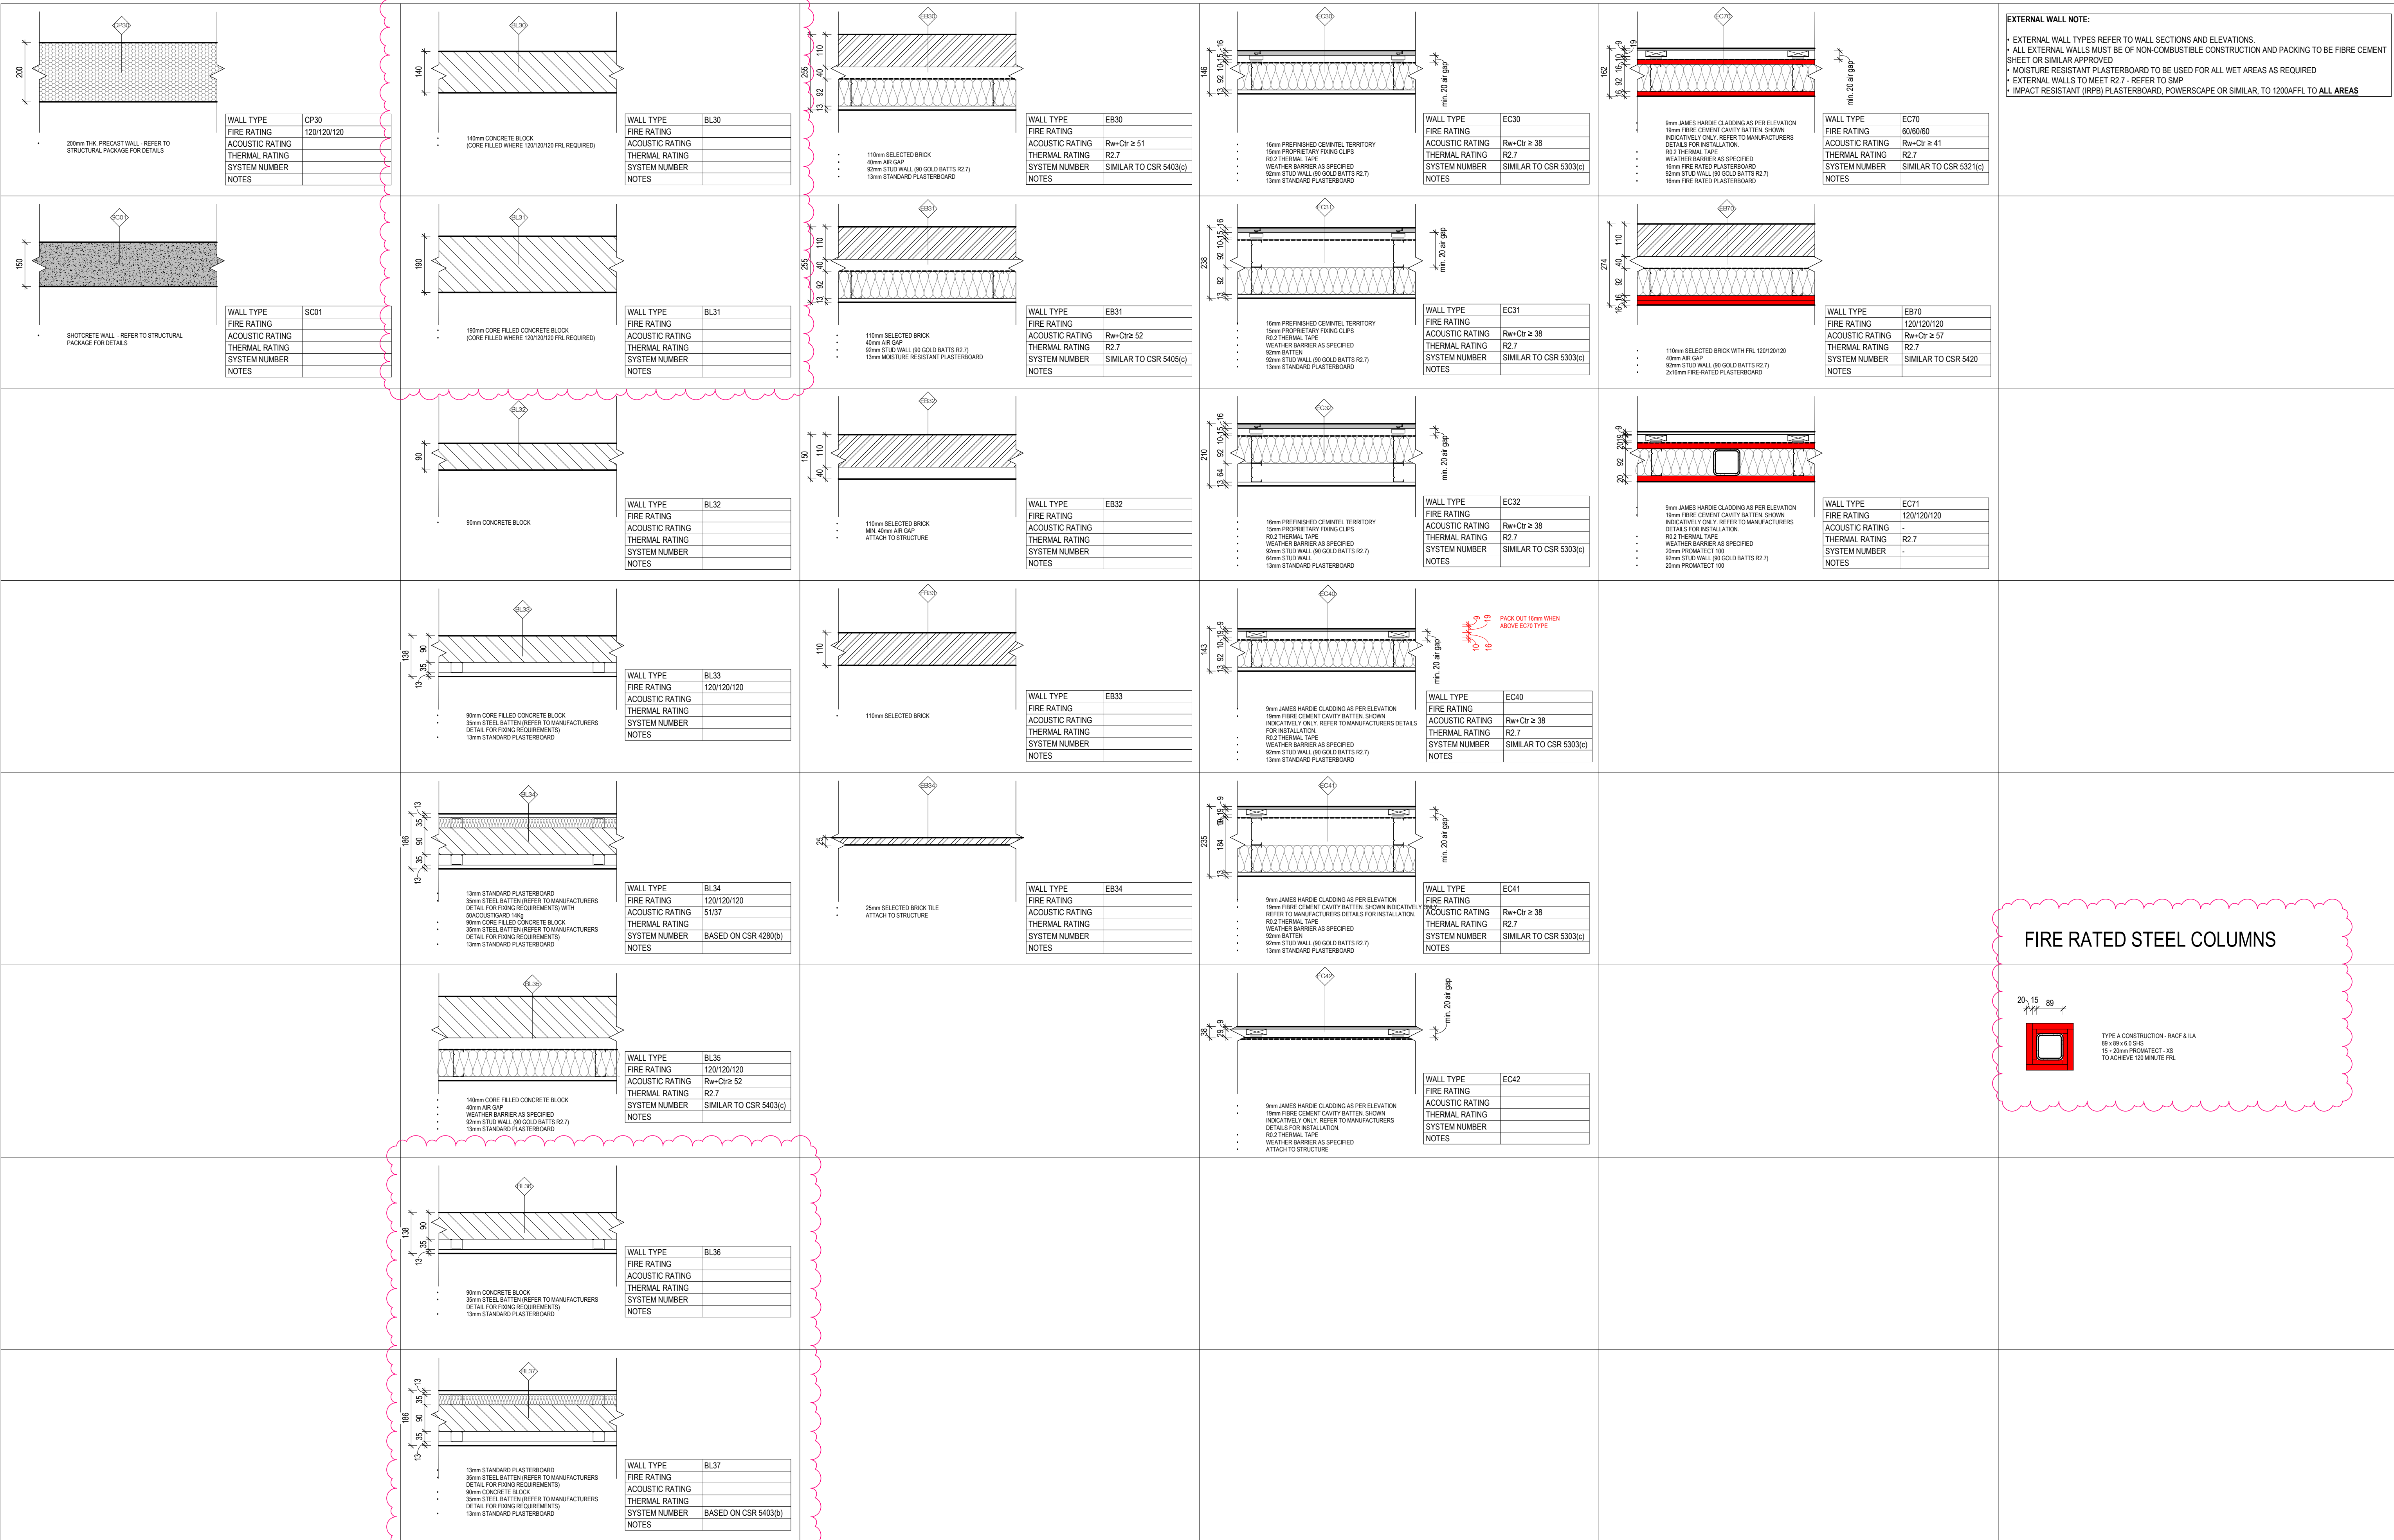

FOR CONSTRUCTION