




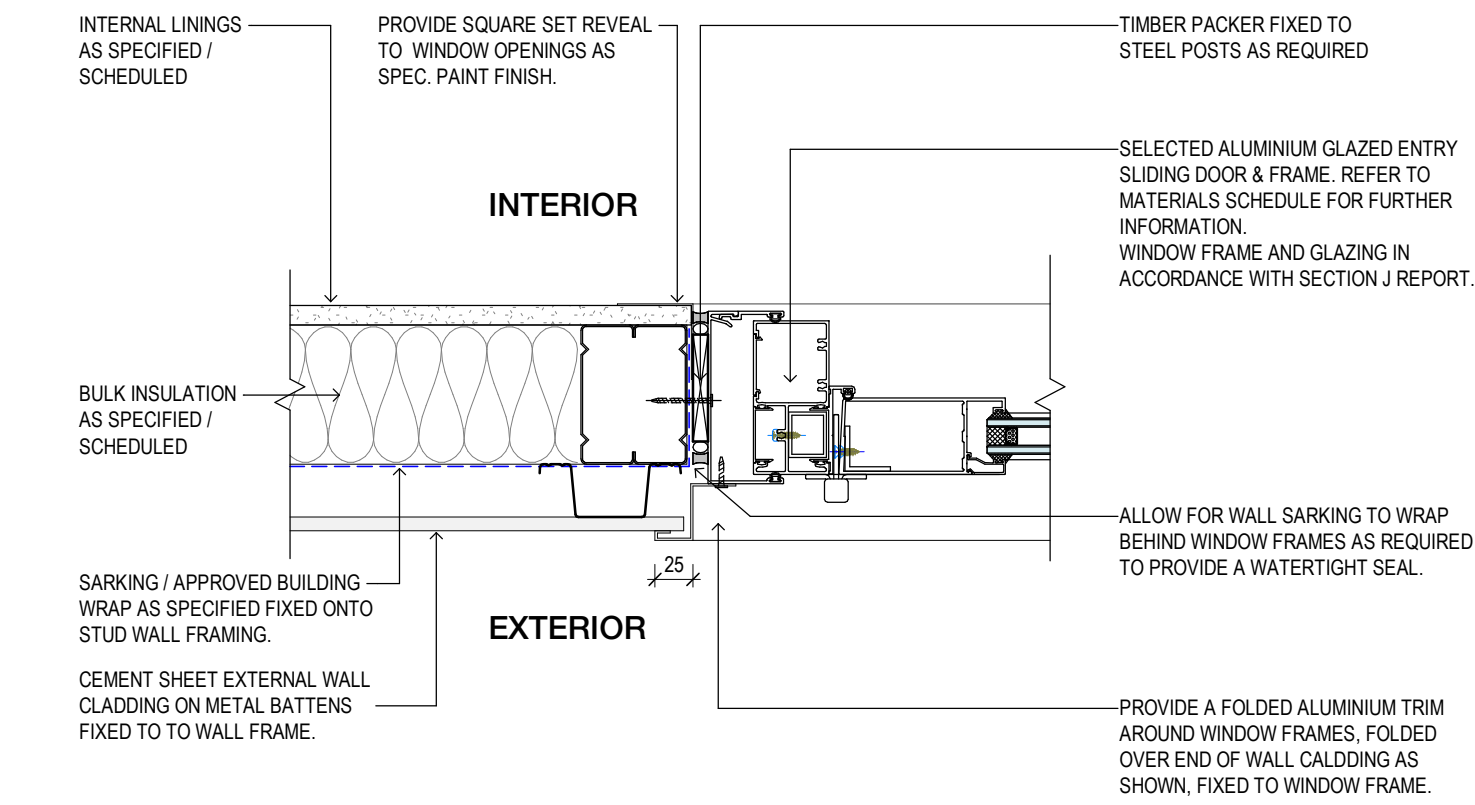


1 TYPICAL - EXTERNAL DOOR JAMB DETAIL - LIGHTWEIGHT WALL CLADDING
Scale 1:5

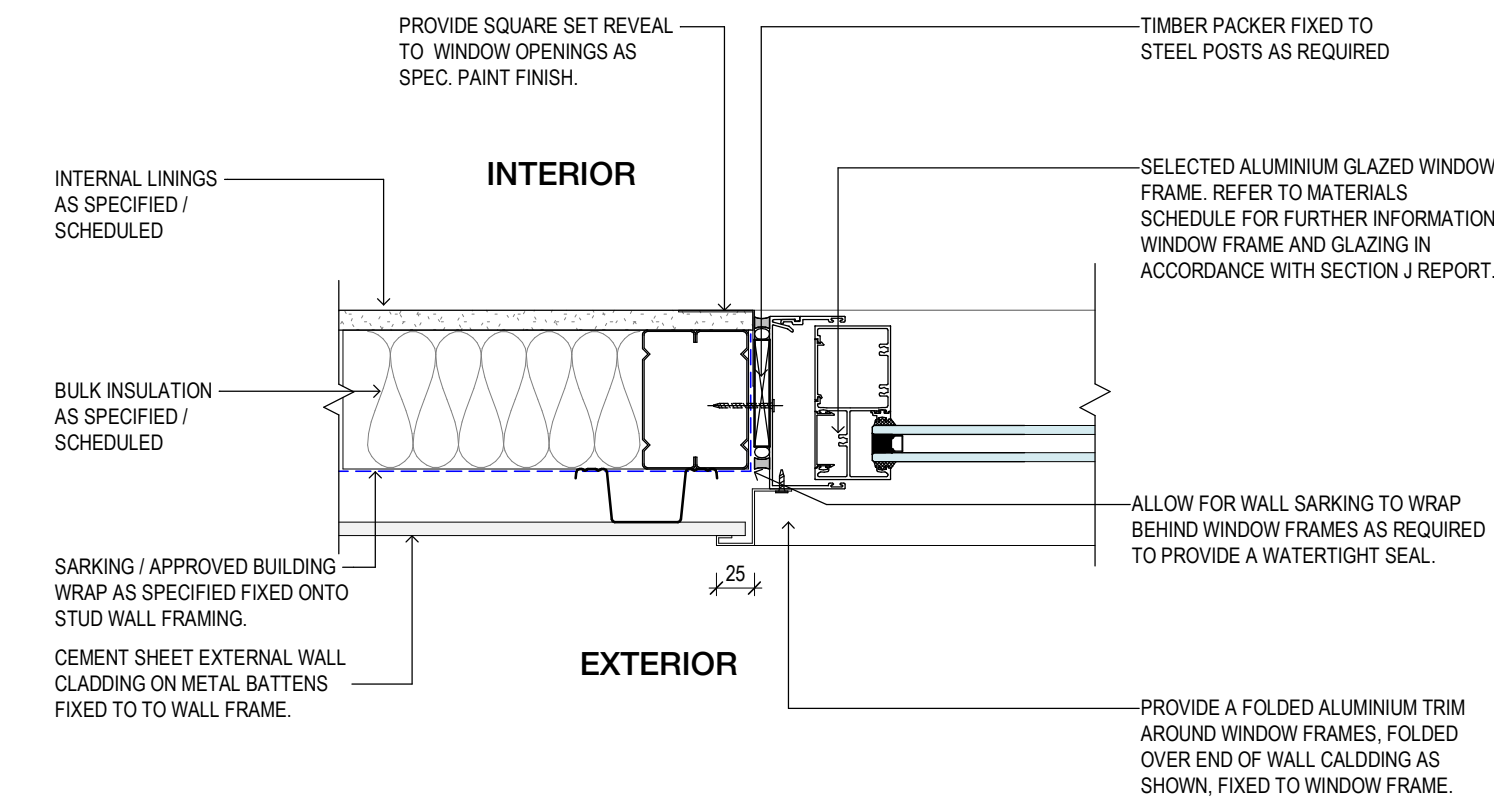


2 TYPICAL - SOU WINDOW JAMB - LIGHTWEIGHT WALL CLADDING
Scale 1:5

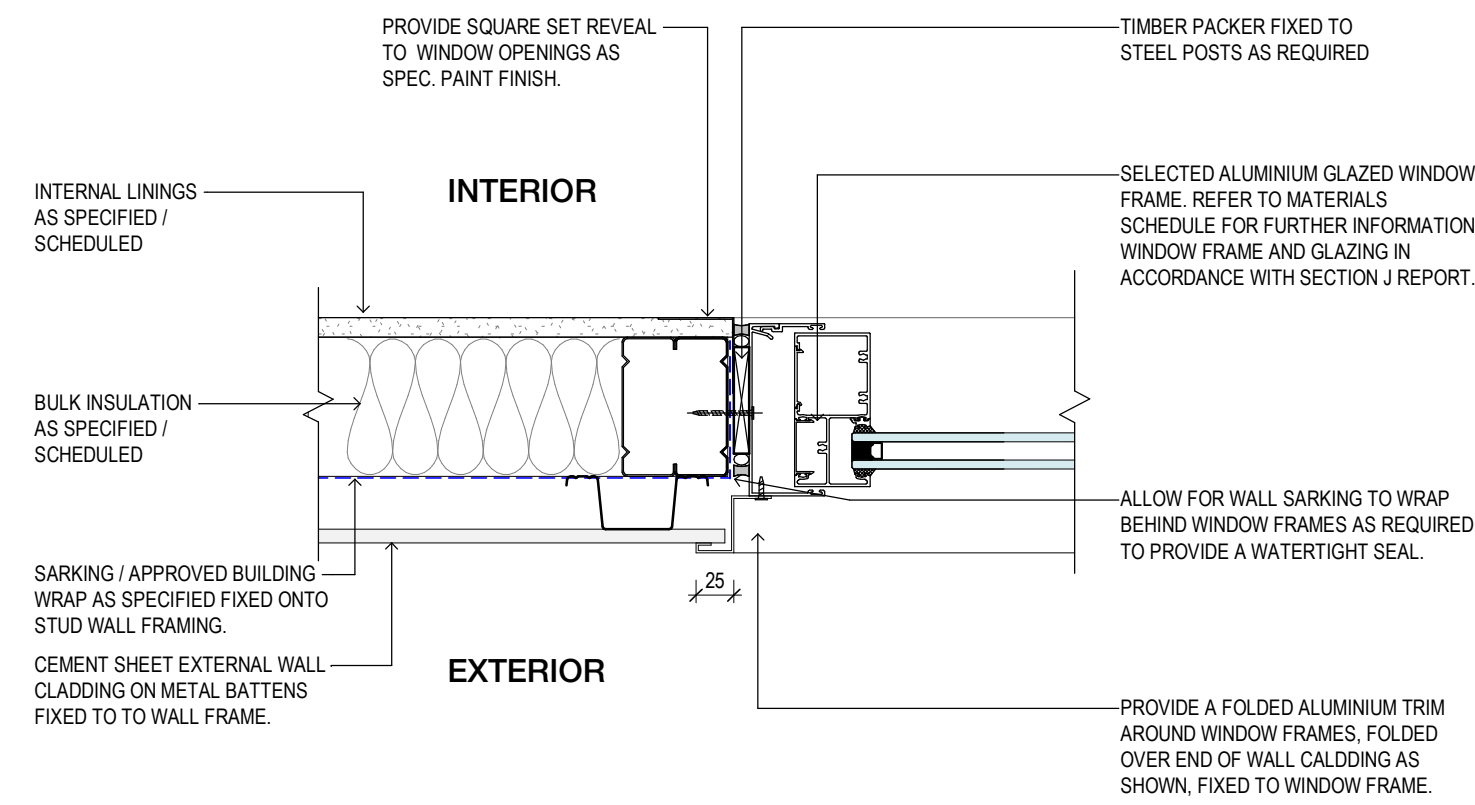


3 TYPICAL - GENERAL WINDOW JAMB - LIGHTWEIGHT WALL CLADDING
Scale 1:5

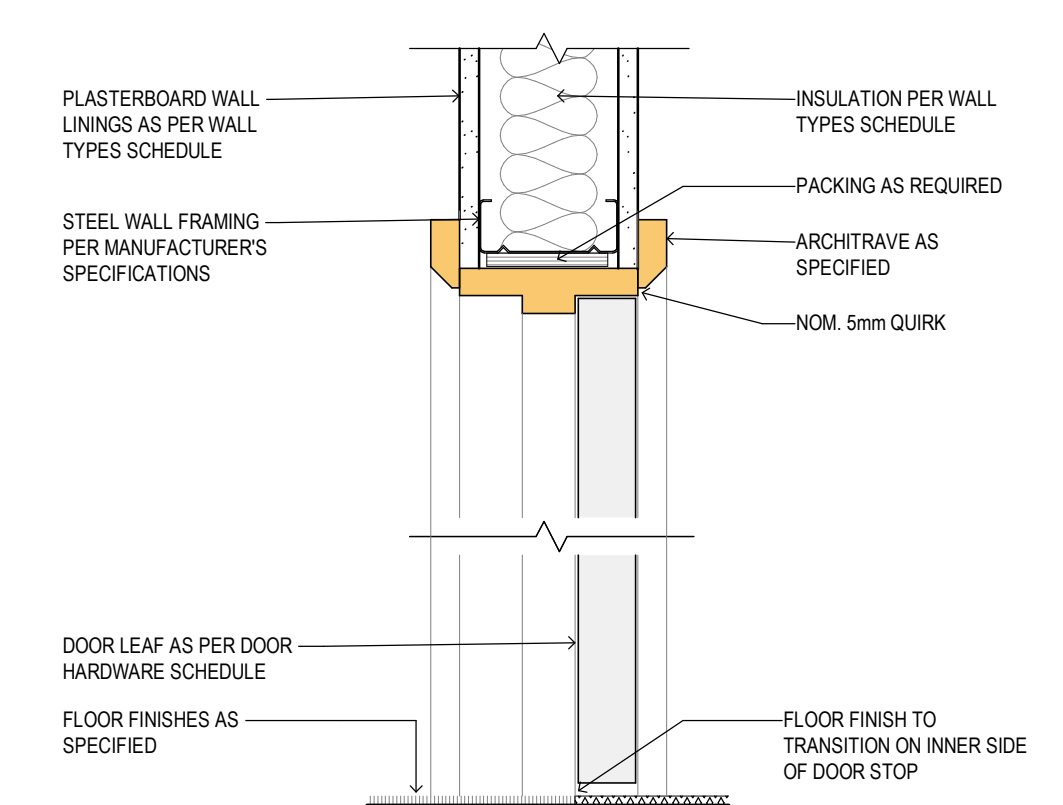


4 TYPICAL SWING DOOR HEAD DETAIL
Scale 1:5

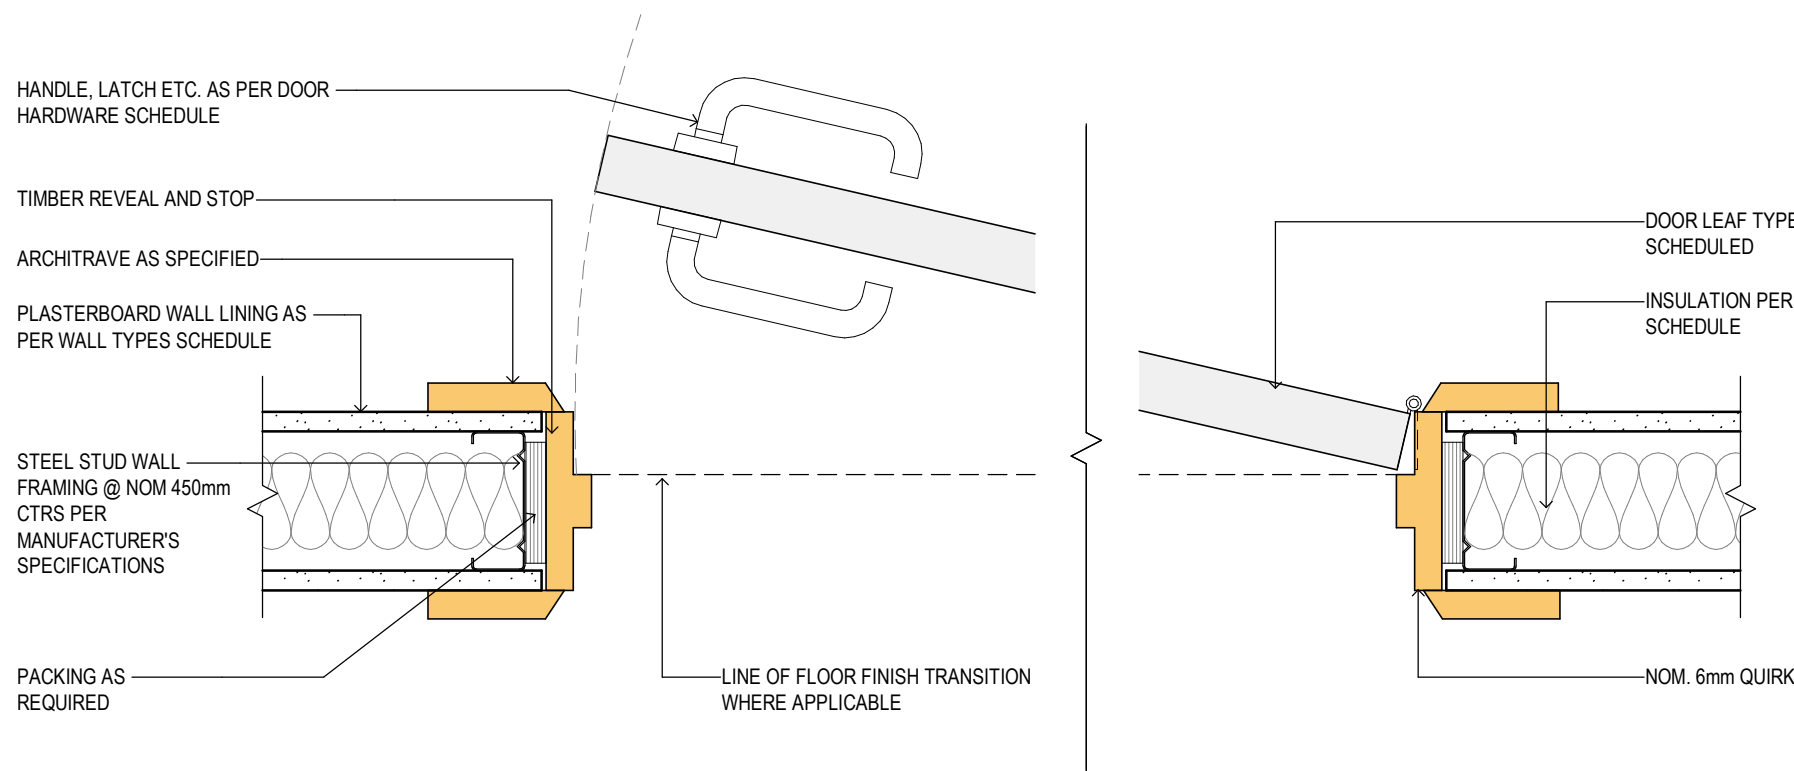


5 TYPICAL SWING DOOR JAMB DETAIL
Scale 1:5

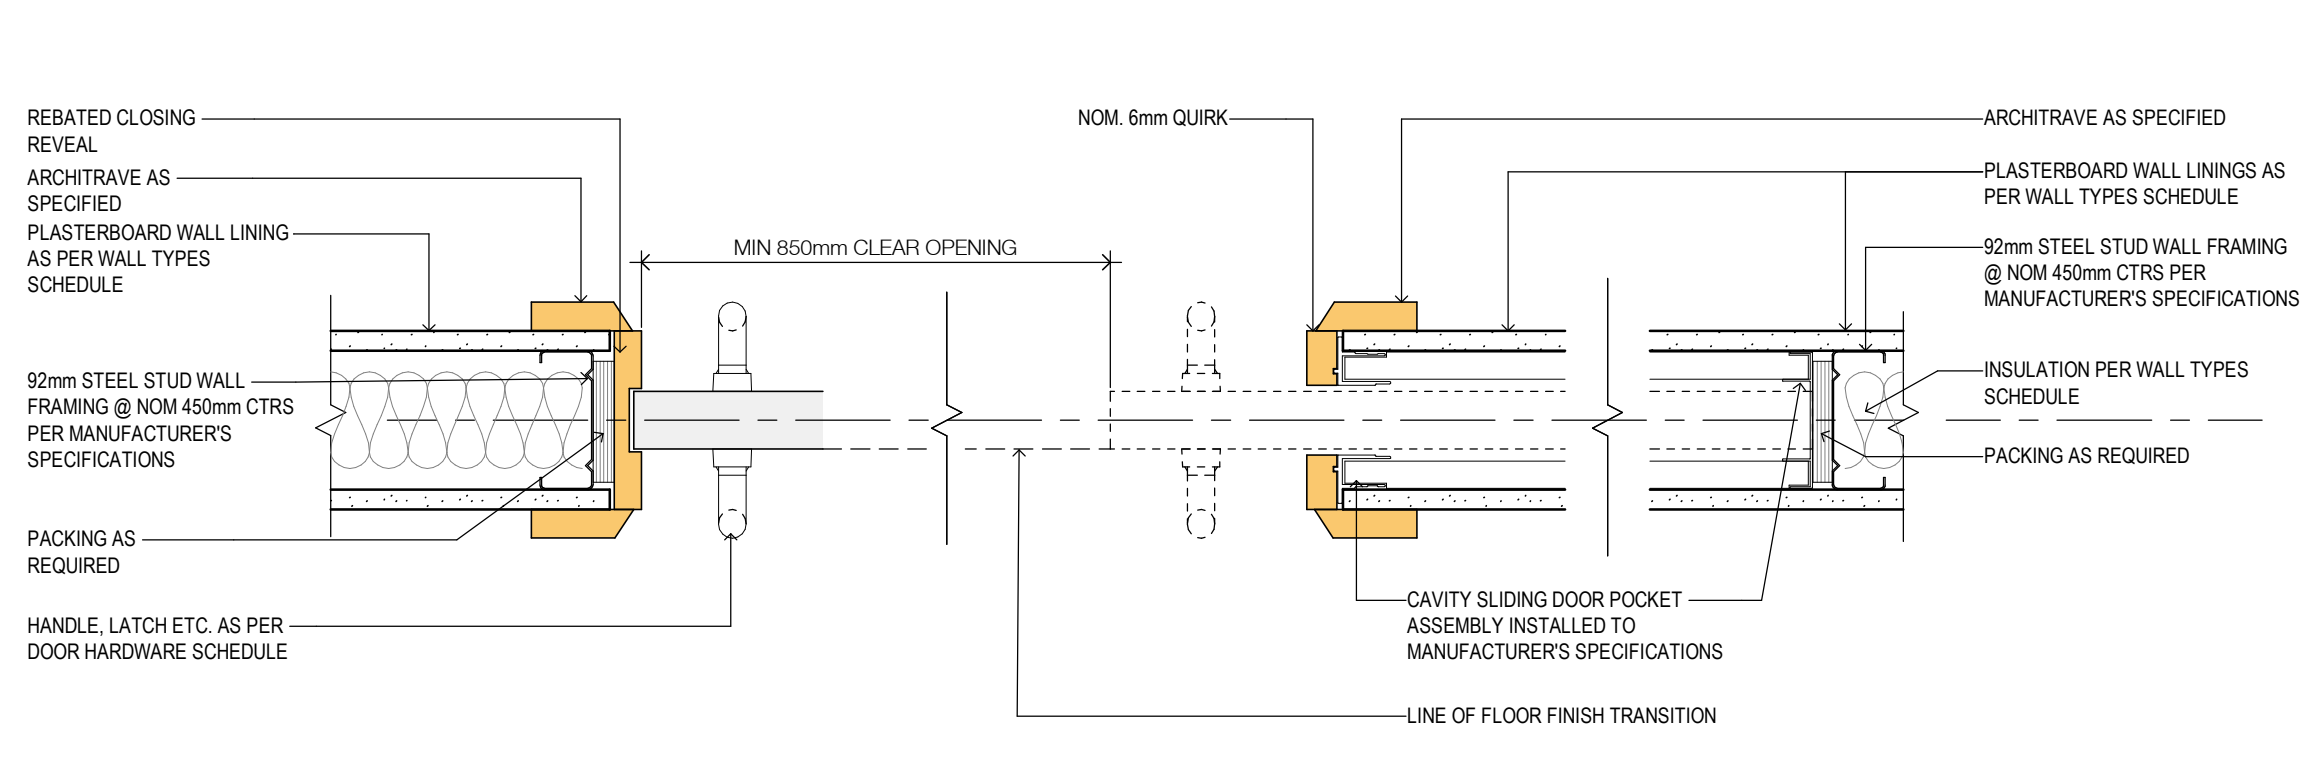


6 TYPICAL INTERNAL SLIDING DOOR PLAN DETAIL
Scale 1:5

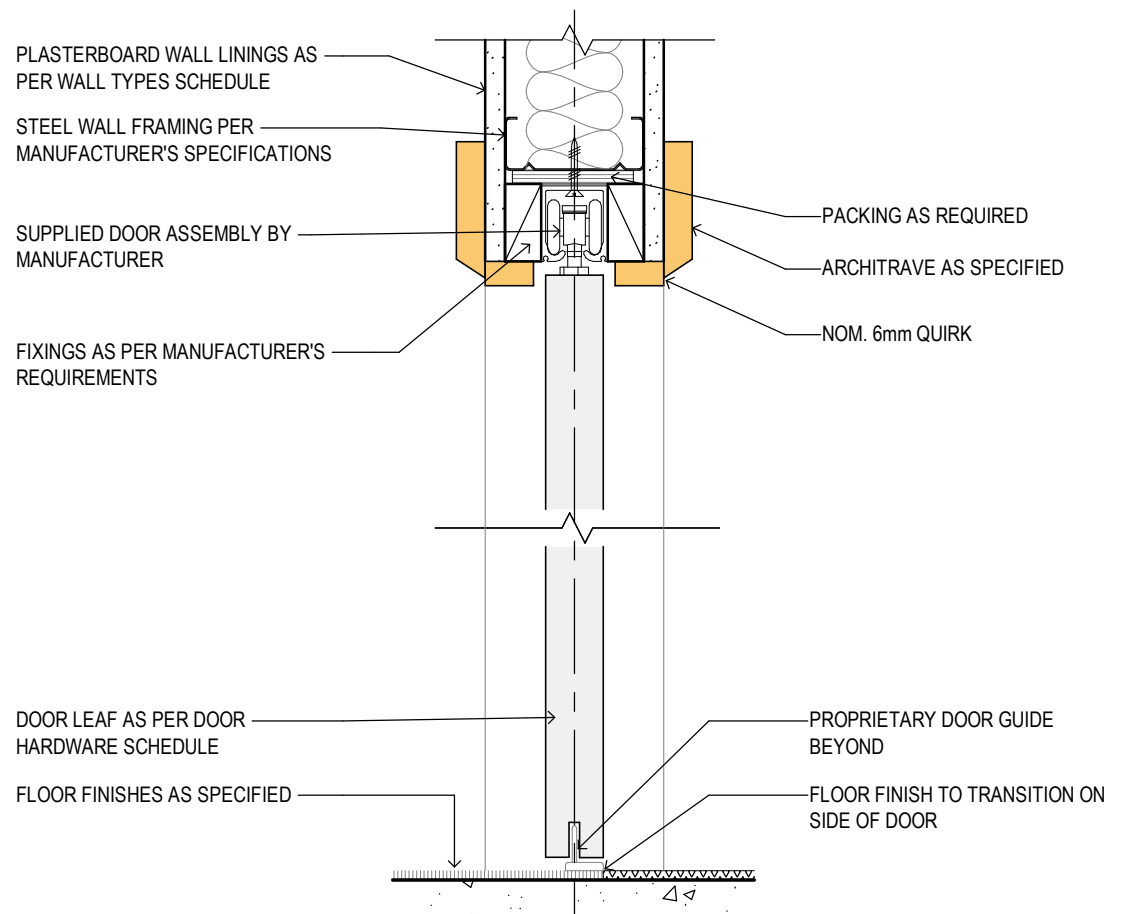


7 INTERNAL CAVITY SLIDING DOOR SILL & HEAD DETAIL
Scale 1:5

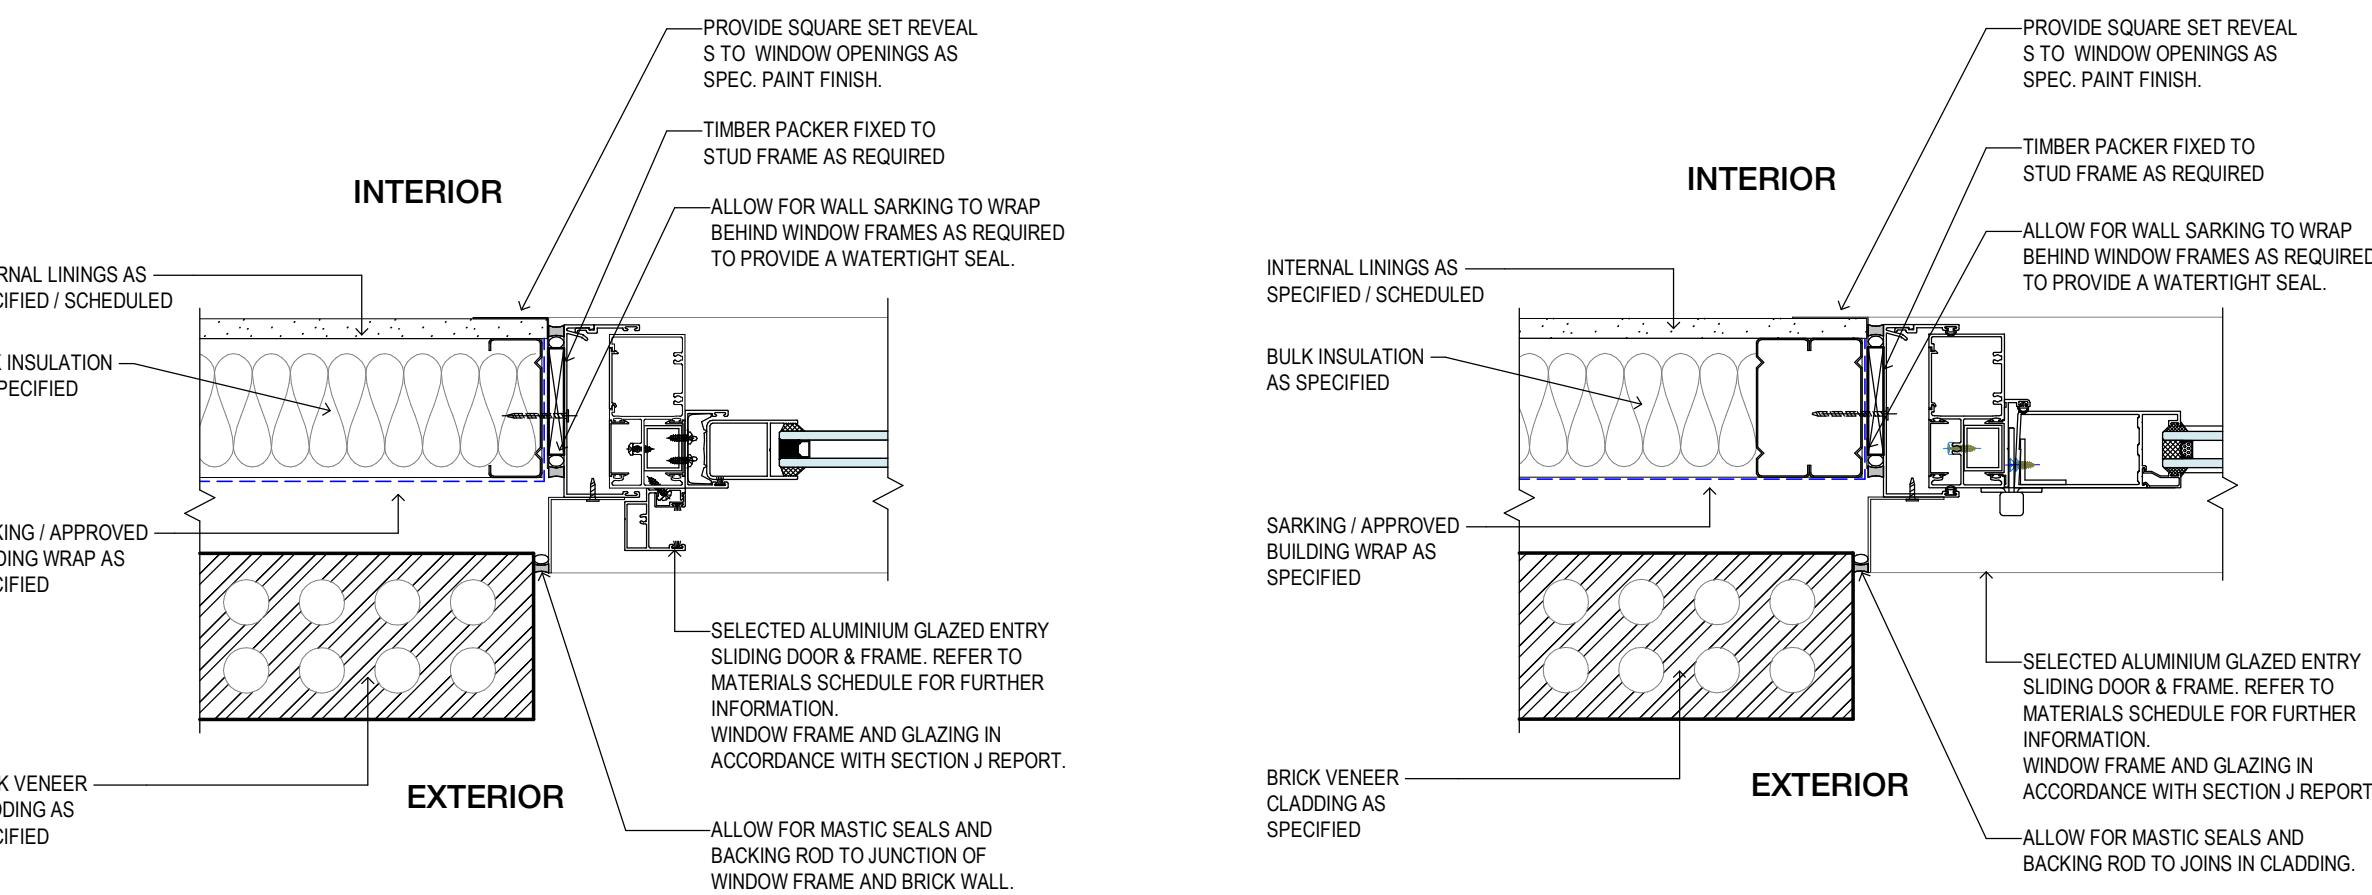

8 EXTERNAL SLIDING DOOR JAMB PLAN DETAIL
Scale 1:5

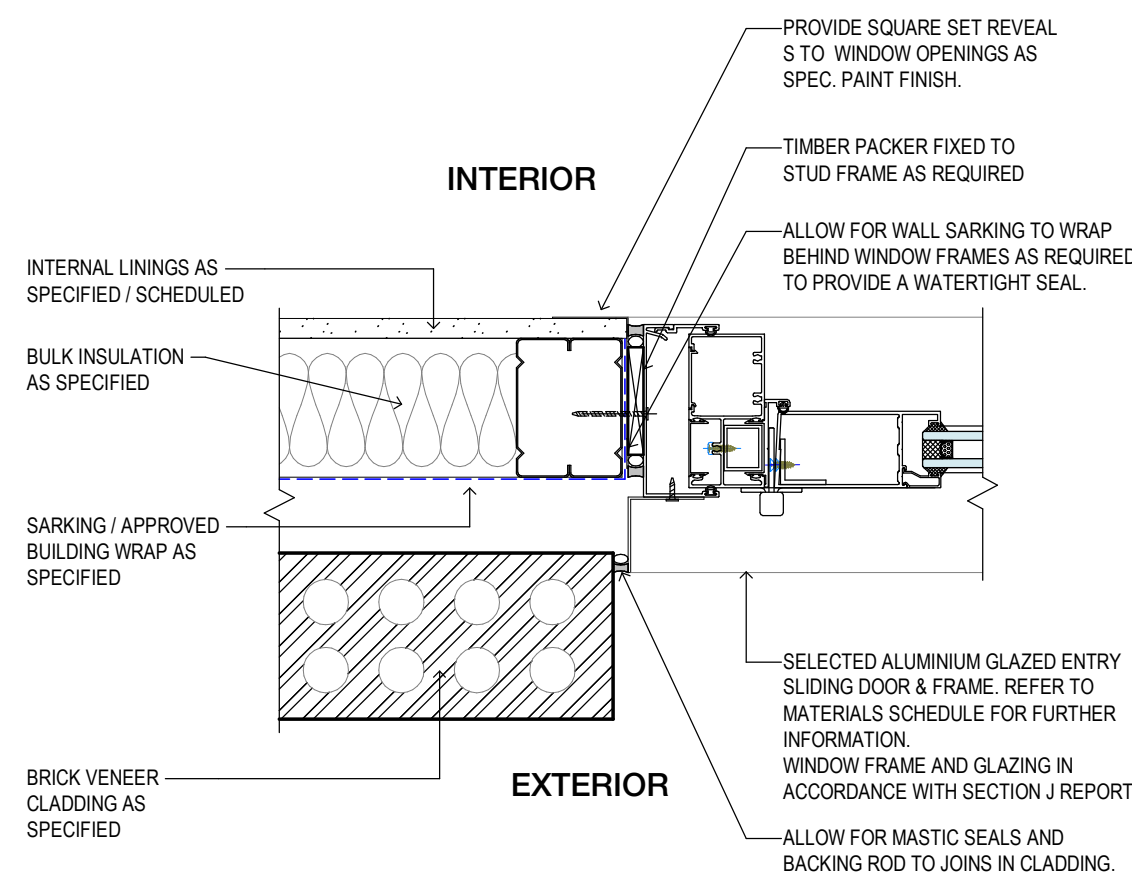

9 HINGED DOOR JAMB PLAN DETAIL
Scale 1:5

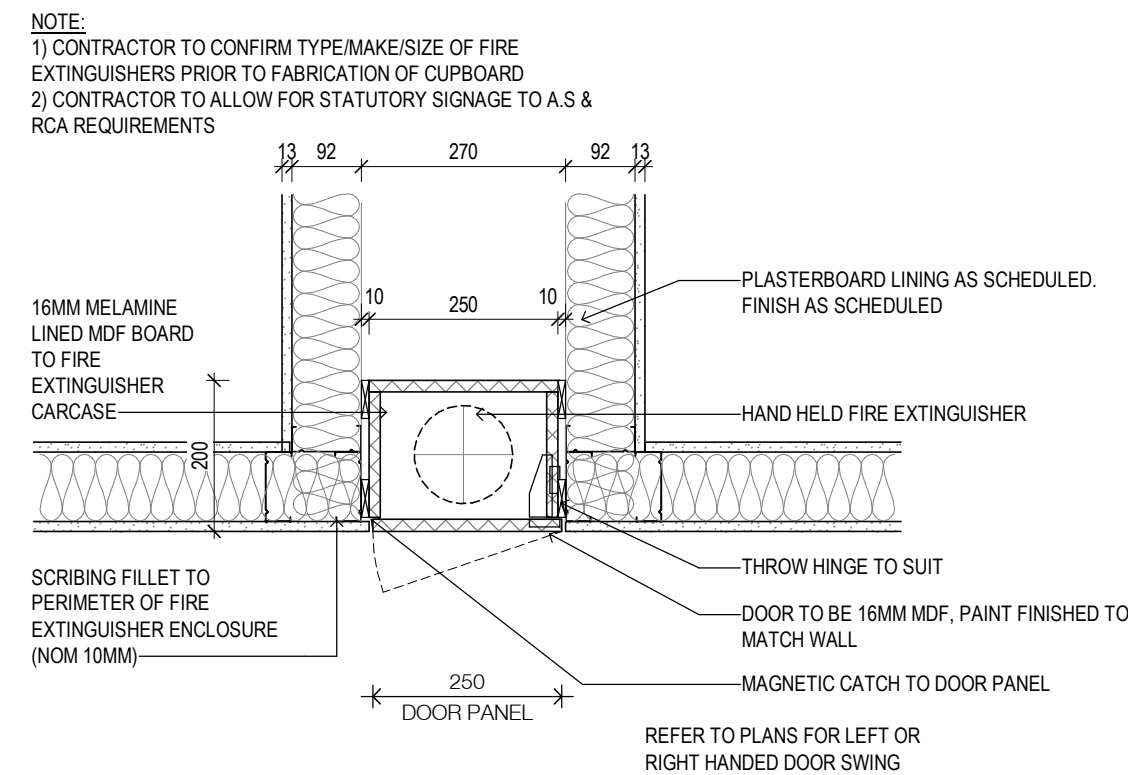

ABOVE DETAILED FIRE EXTINGUISHER CUP'D CAN BE SUBSTITUTED WITH A PROPRETRY CUP'D IF IT FITS OPENING SIZES.

10 RECESSED FIRE EXTINGUISHER - PLAN DETAIL - FE-JC
Scale 1:10

DETAILS ARE TYPICAL TO BOTH RACF & ILA BUILDINGS

FOR CONSTRUCTION

Revision/Issue	Date
P1 ISSUE FOR CONTRACT	2025.10.14
C1 ISSUE FOR CONSTRUCTION	2025.12.19

Clarke Hopkins
architect

ClarkeHopkinsClarke
Melbourne | Wurundjeri
L3, Melbourne Connect
700 Swanston Street
Carlton VIC 3063
Telephone (03) 9419 4340
Email studio@chc.com.au
www.chc.com.au

Sydney | Gadigal Country
Suite 3, Ground Floor
91 Campbell Street
Surry Hills NSW 2010
Telephone (02) 9221 9200
Email studio@chc.com.au
www.chc.com.au

Scale	As indicated @ A1
Date	01/03/2024
Drawn	SG
Architect	EL

Project
Summerset Oakleigh
52 Golf Road, Oakleigh South, VIC

Drawing
Plan Details - Sheet 1

Drawing No.
230185/A1710
C1