




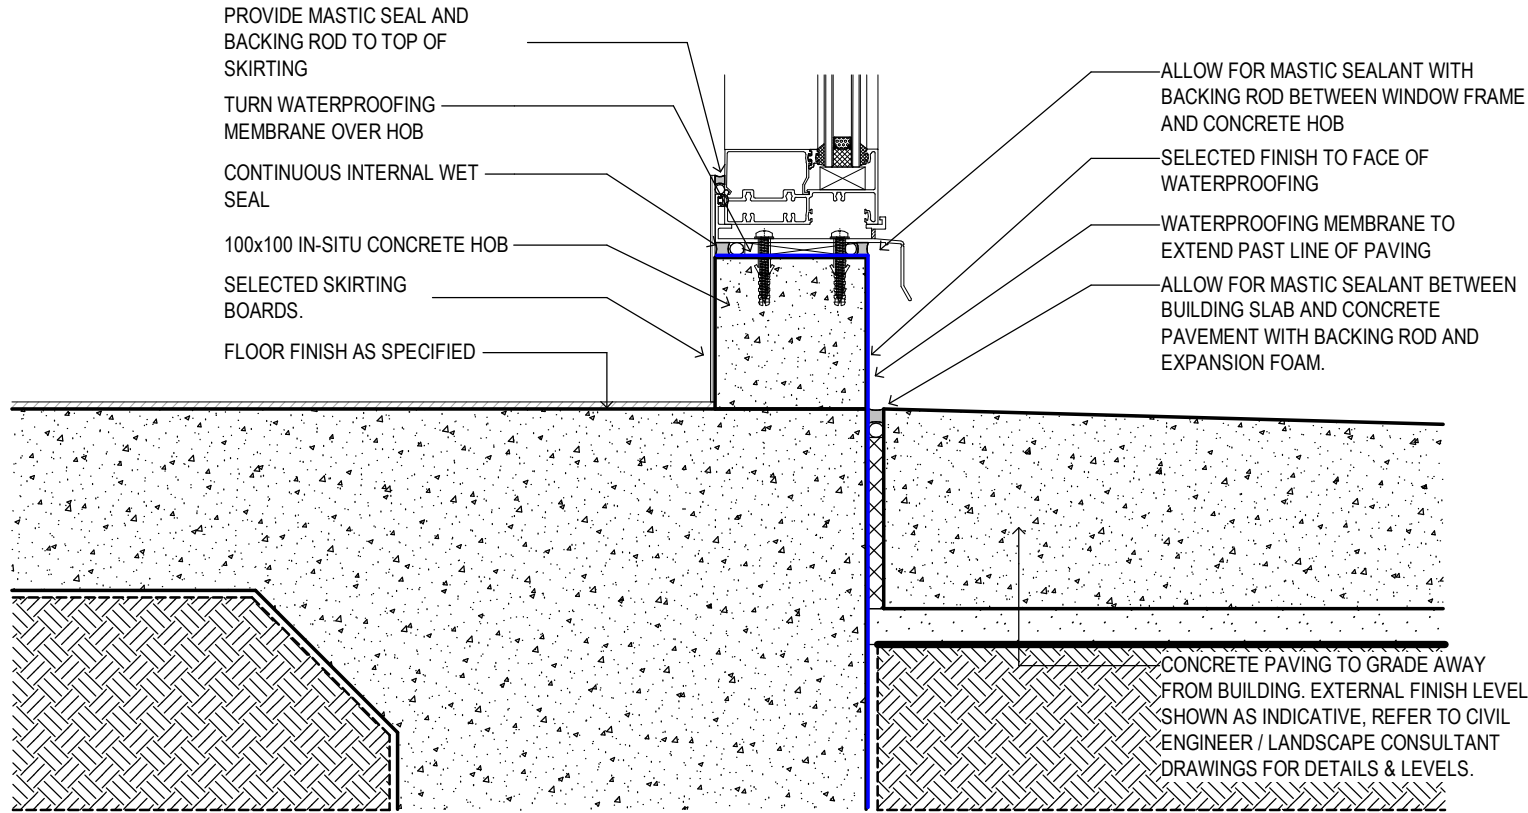


1 WINDOW UNIT ON CONCRETE HOB - SLAB EDGE
Scale 1:5

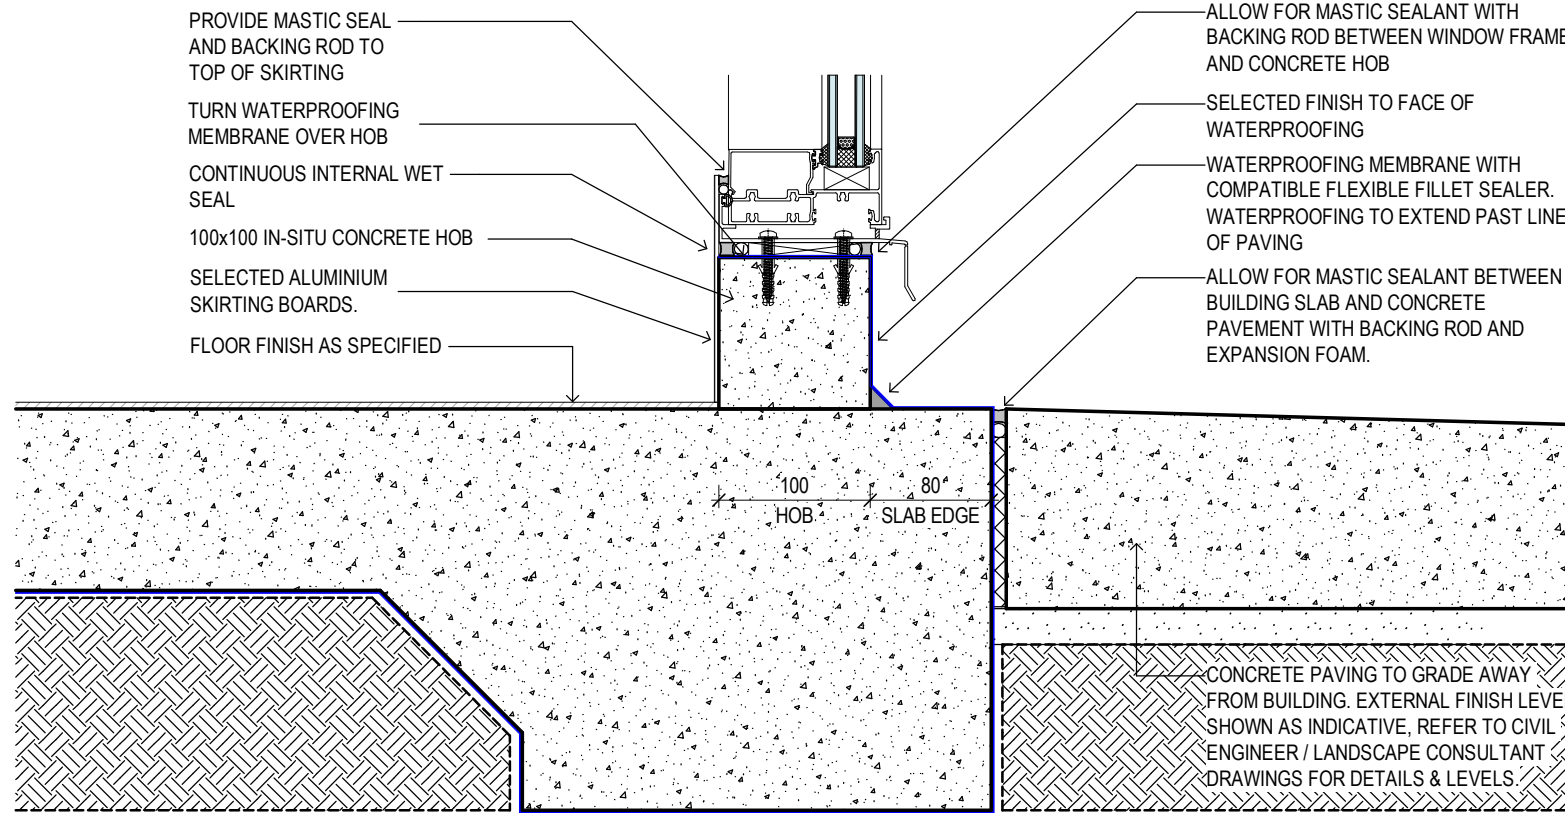


2 WINDOW UNIT ON CONCRETE HOB - BRICK VENEER INSET
Scale 1:5

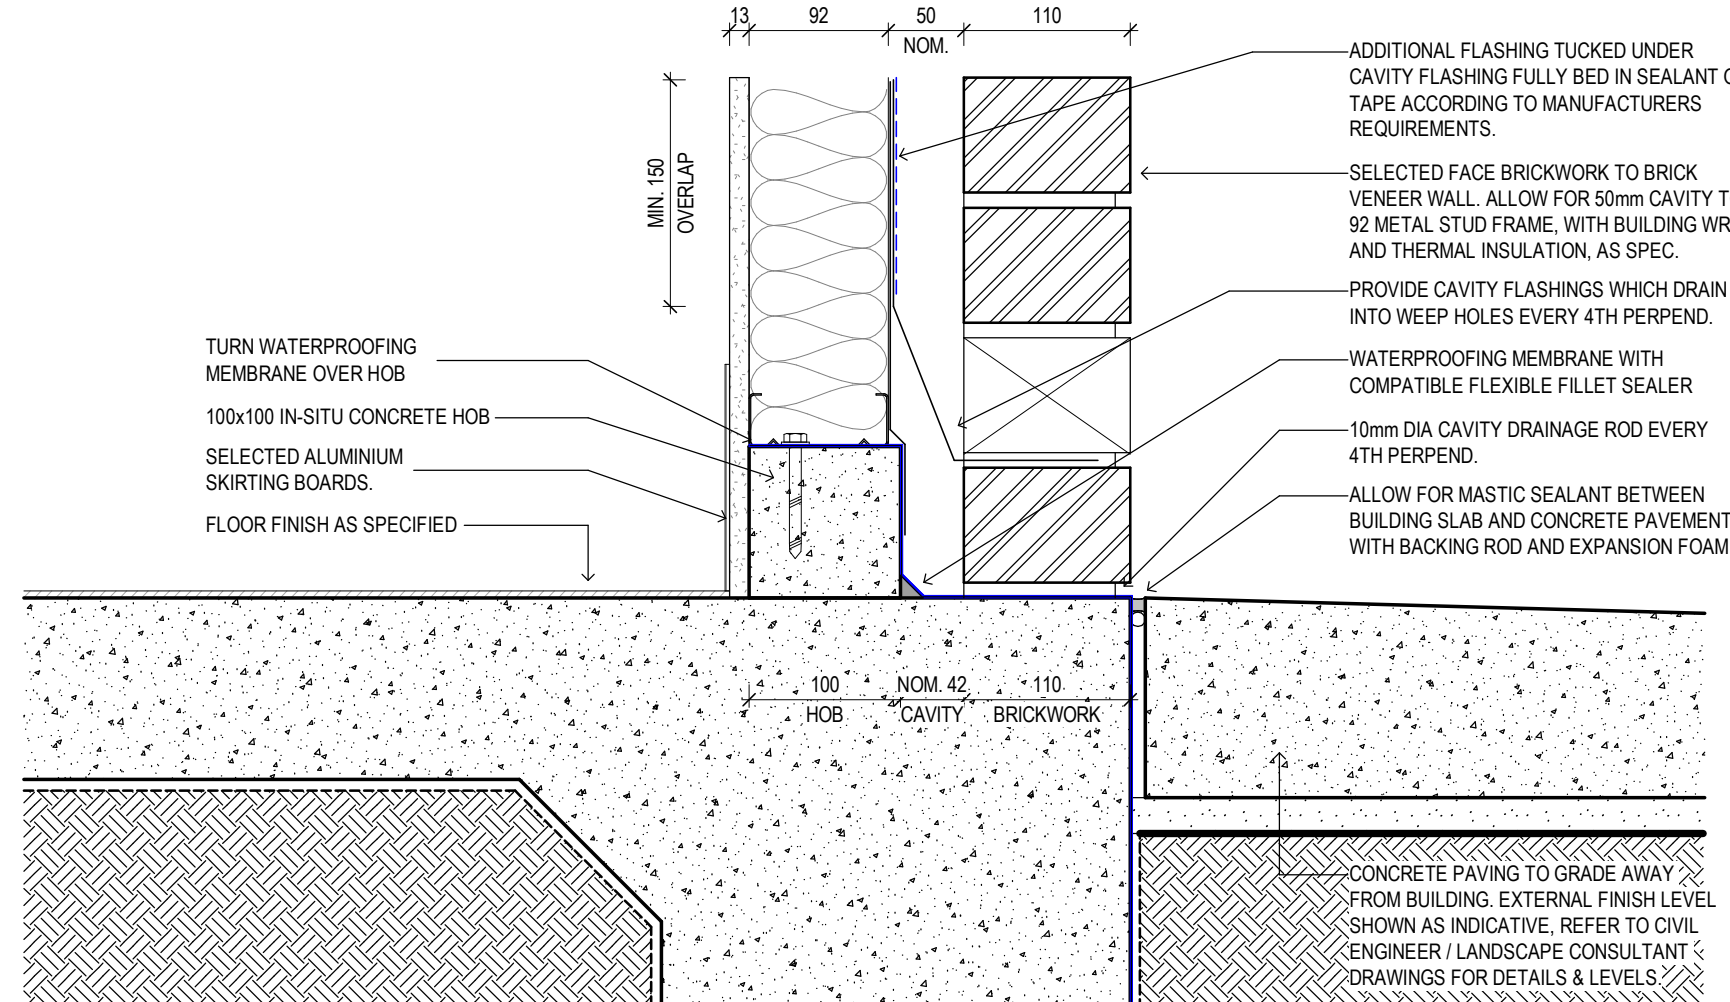


3 CONCRETE HOB TO BRICK VENEER
Scale 1:5

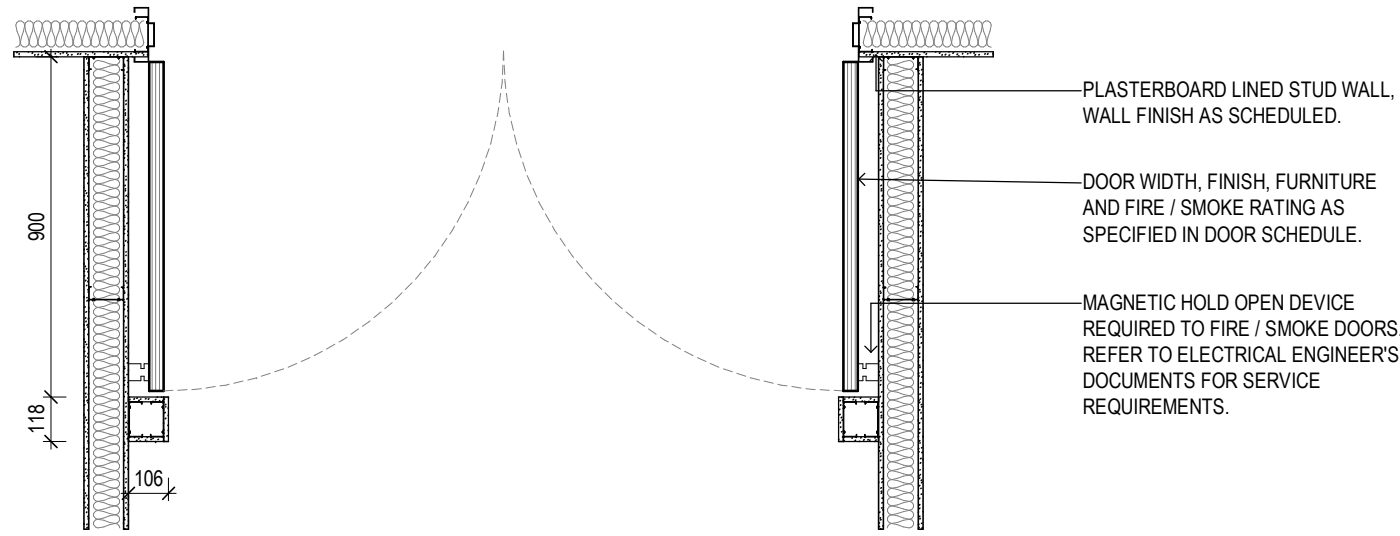


4 TYPICAL - SMOKE DOOR - PLAN
Scale 1:20

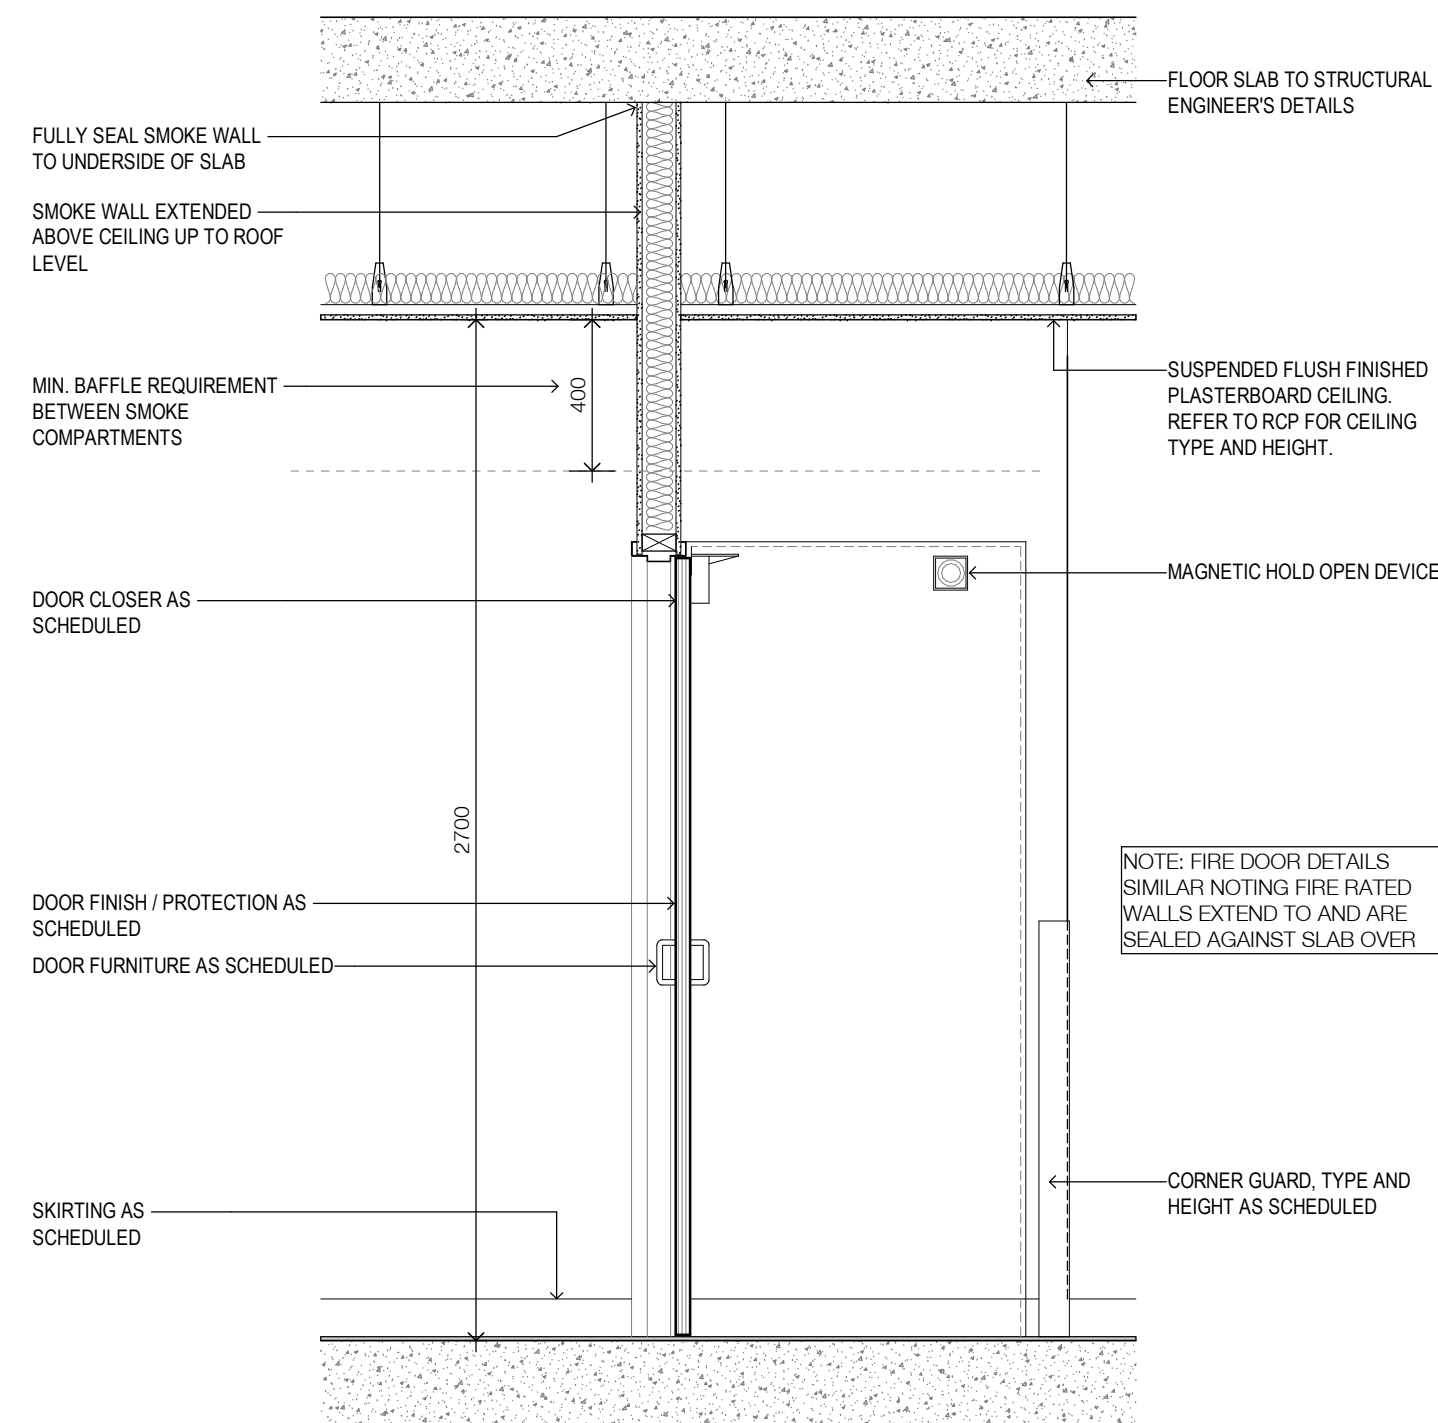


5 TYPICAL SMOKE DOOR SECTION - SLAB OVER
Scale 1:20

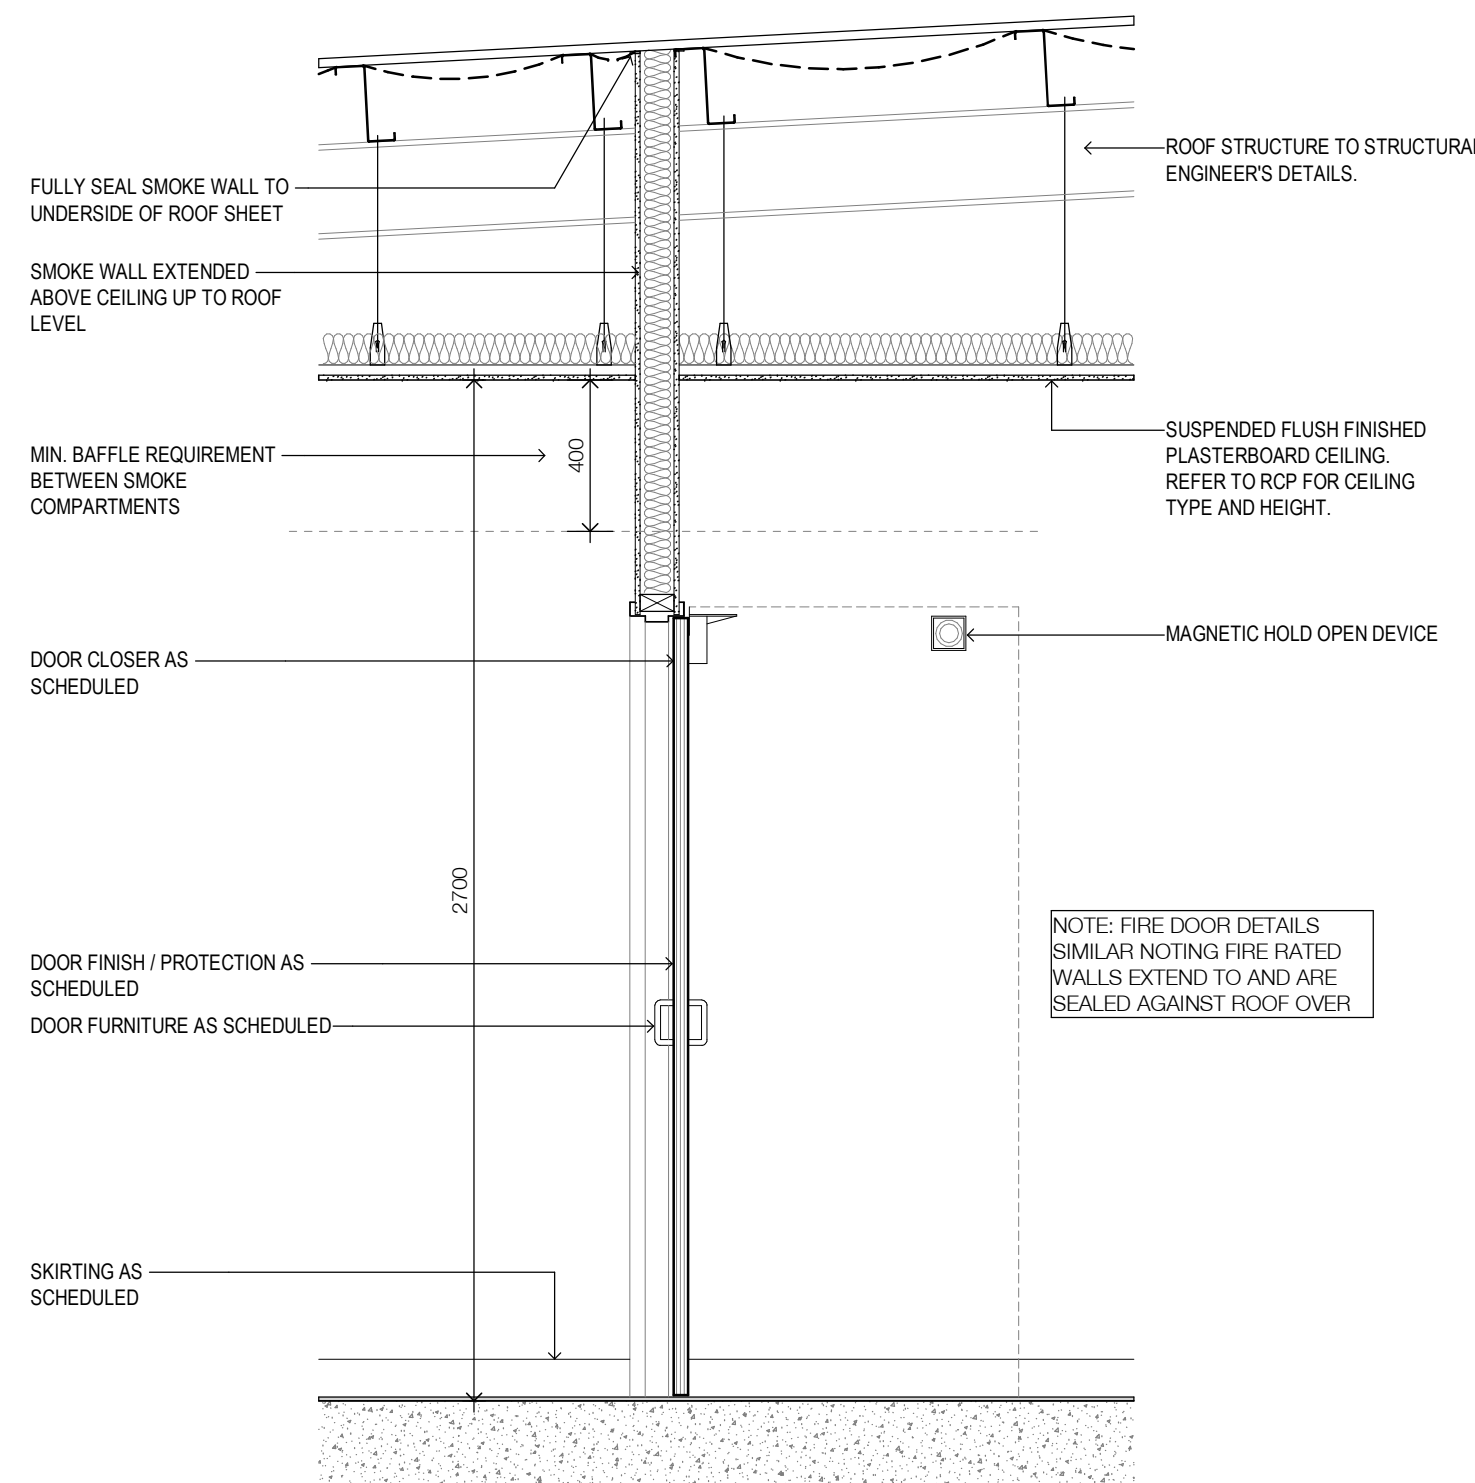


6 TYPICAL SMOKE DOOR SECTION - ROOF OVER
Scale 1:20

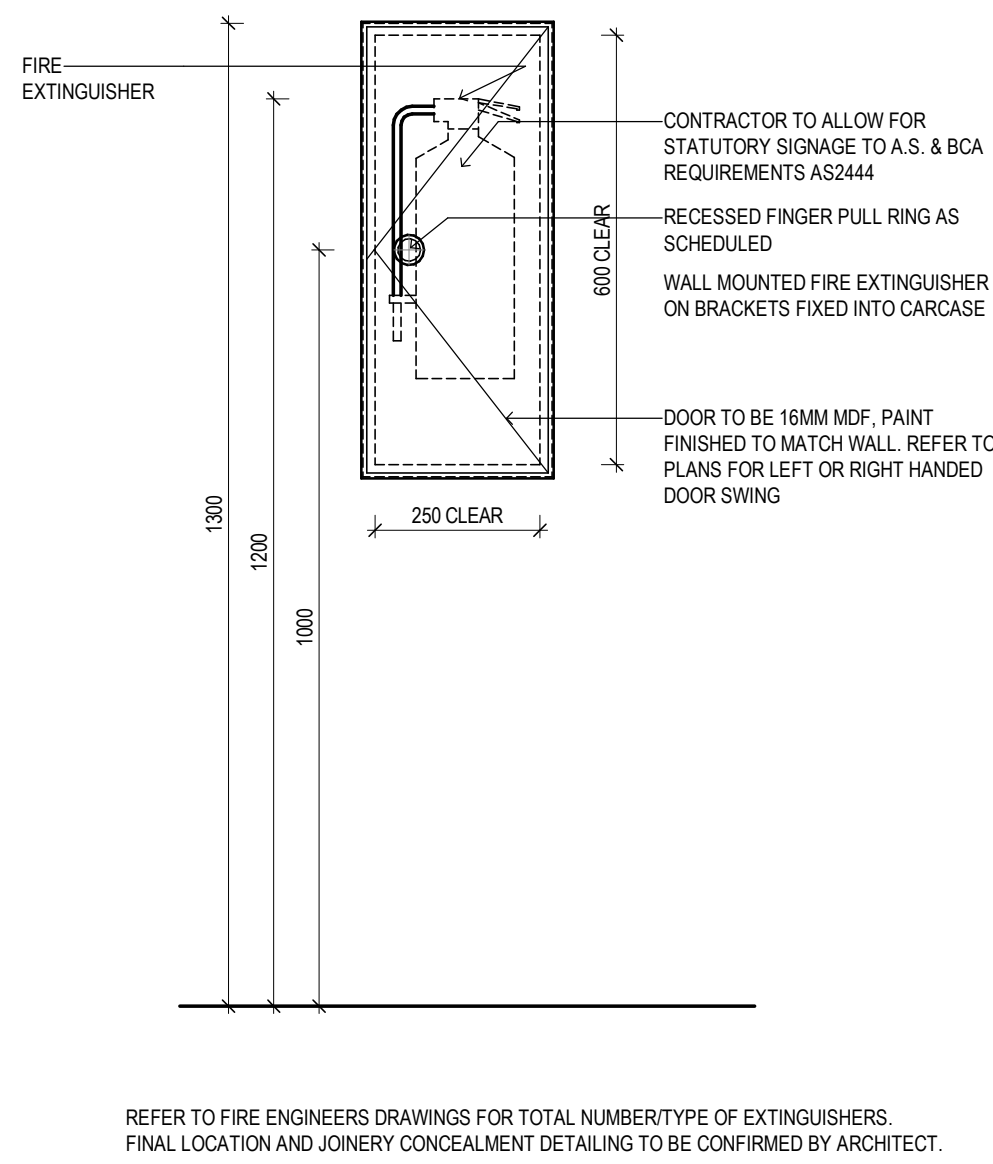


7 RECESSED FIRE EXTINGUISHER DETAIL ELEVATION
Scale 1:10

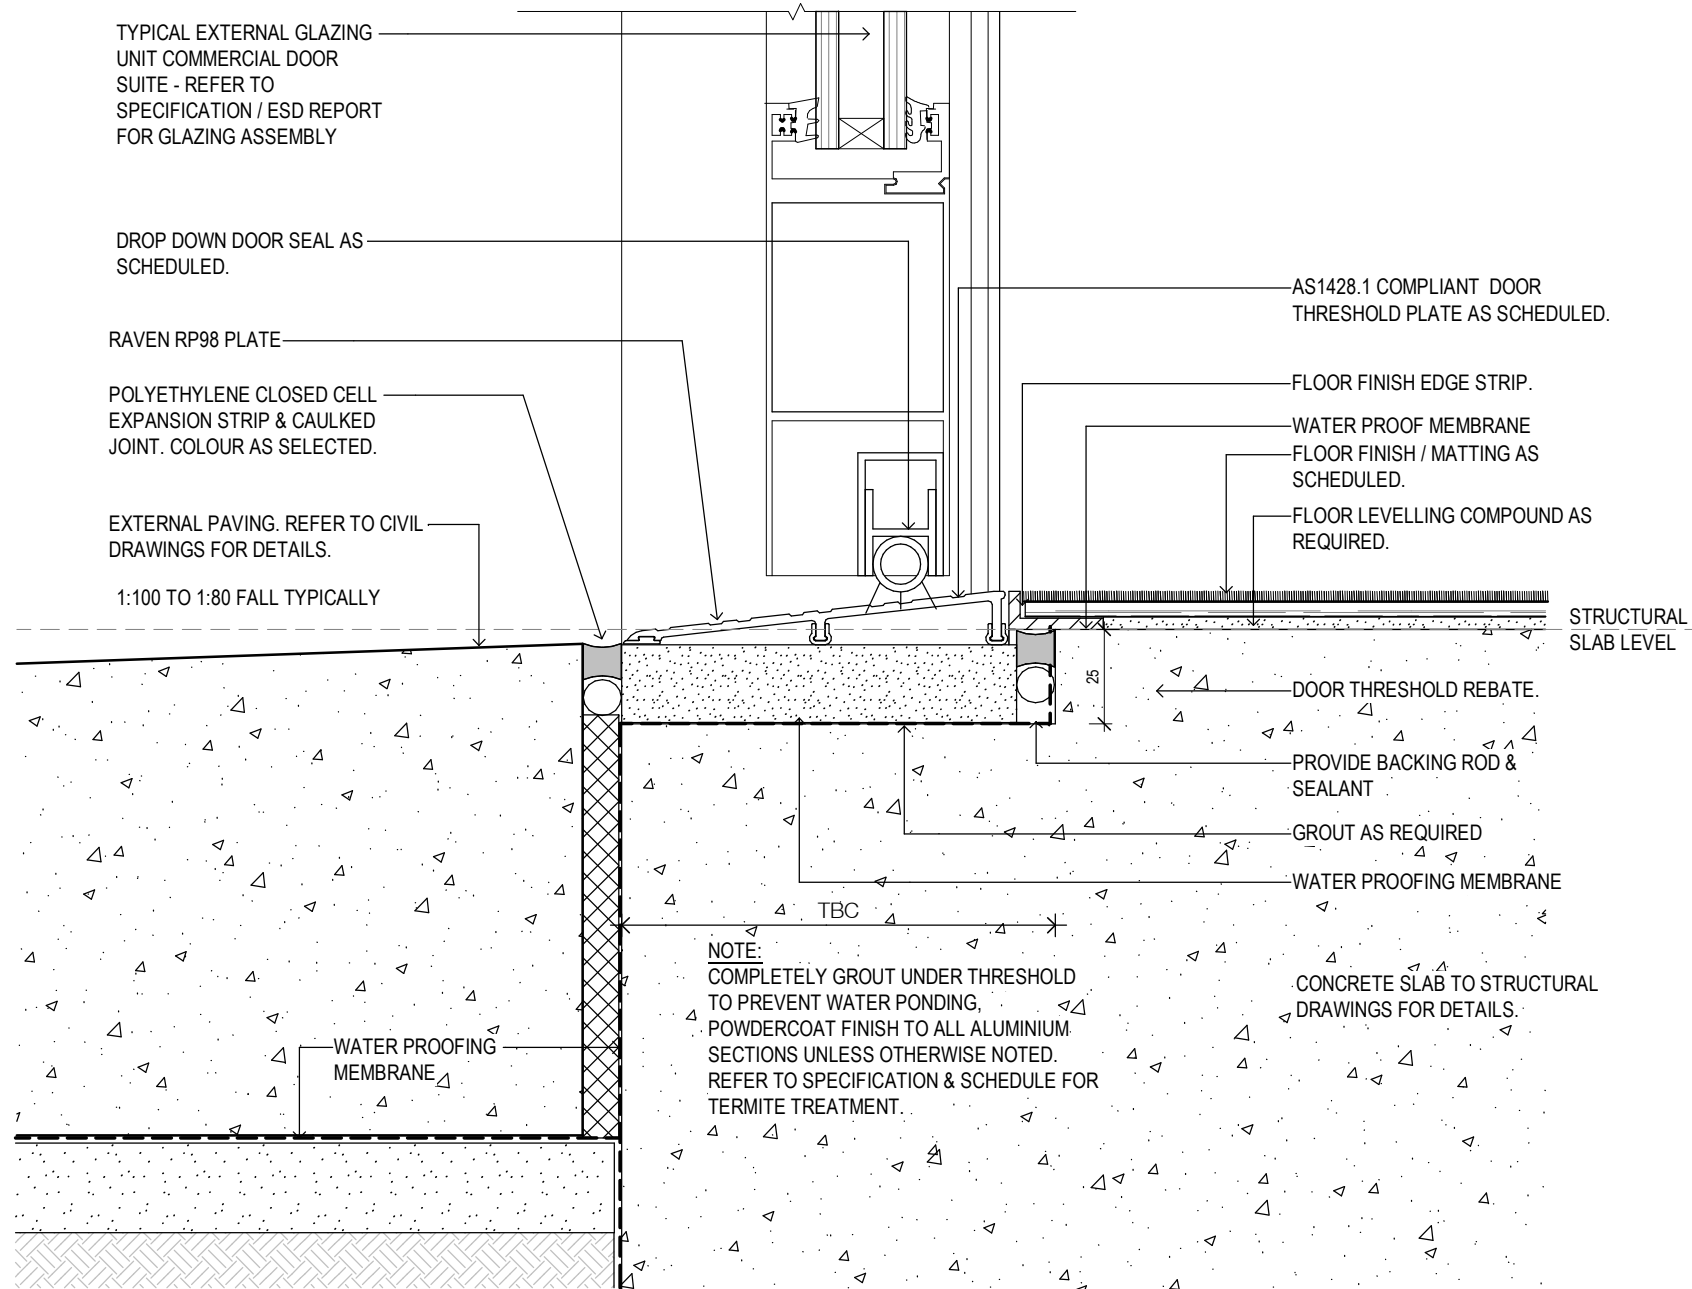


8 TYPICAL - EXTERNAL HINGE DOOR THRESHOLD - WITH THRESHOLD RAMP
Scale 1:2

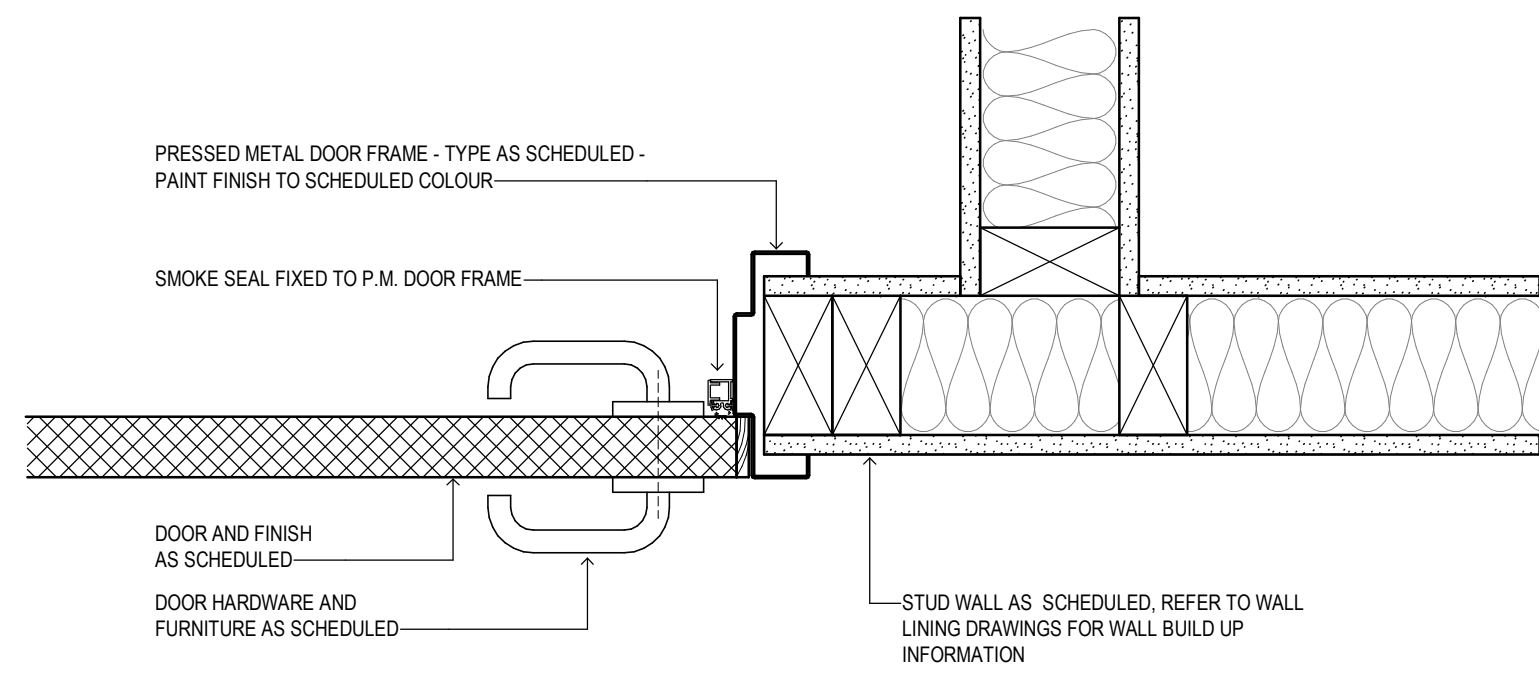

9 TYPICAL - SMOKE DOOR - PLAN DETAIL
Scale 1:5

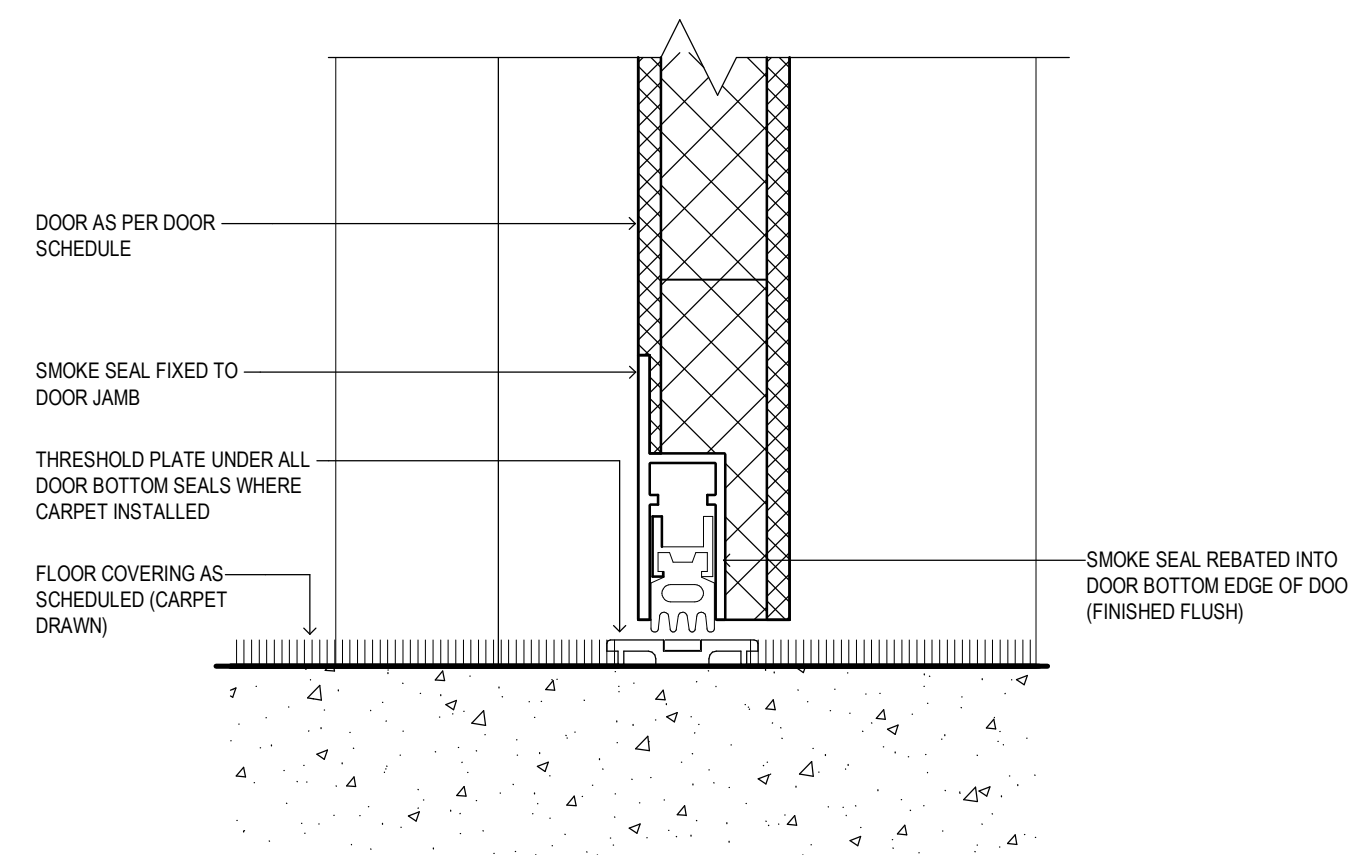

10 TYPICAL - SMOKE DOOR - SECTION DETAIL
Scale 1:2

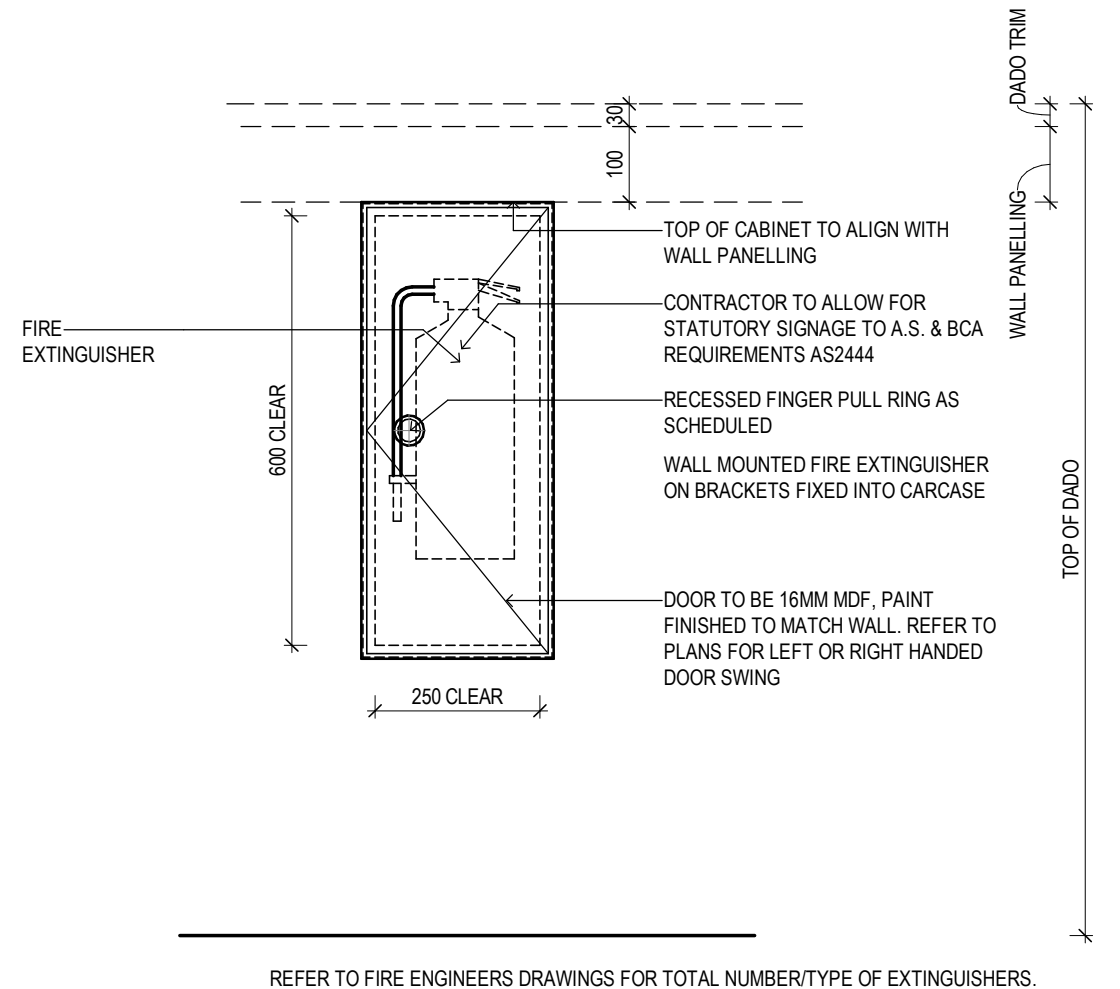

11 RECESSED FIRE EXTINGUISHER DETAIL ELEVATION - FE IN DADO
Scale 1:10

Revision/Issue	Date
P1 ISSUE FOR CONTRACT	2025.10.14
C1 ISSUE FOR CONSTRUCTION	2025.12.19

DETAILS ARE TYPICAL TO
BOTH RACF & ILA BUILDINGS

**Clarke
Hopkins
Clarke**

ClarkeHopkinsClarke
Melbourne | Wurundjeri
L3, Melbourne Connect
700 Swanston Street
Carlton VIC 3063
Telephone (03) 9419 4340
Email studio@chc.com.au
www.chc.com.au

Sydney | Gadigal Country
Suite 3, Ground Floor
91 Campbell Street
Surry Hills NSW 2010
Telephone (02) 9221 9200
Email studio@chc.com.au
www.chc.com.au

Scale	As indicated @ A1
Date	01/03/2024
Drawn	SG
Architect	EL

Project
Summerset Oakleigh
52 Golf Road, Oakleigh South, VIC

Drawing
Typical Details - Sheet 2

Drawing No.
230185/A1731

C1

FOR CONSTRUCTION