


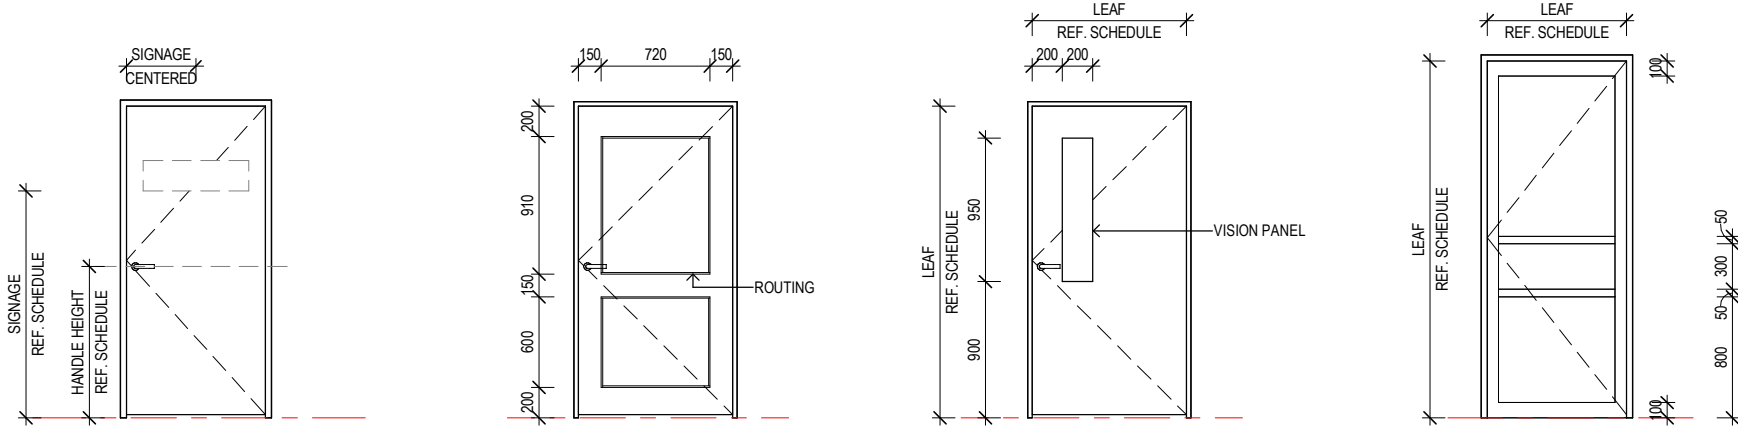

DOOR DIMENSION DIAGRAM
APPLIES TO LEAF TYPES A18, C2,4, P5-11

LEAF TYPE C4
RACF BEDROOM DOOR

LEAF TYPE C2
RACF BEDROOM DOOR

LEAF TYPE D1
RACF BEDROOM DOOR

Door Elevations - RACF

Door Schedule. SSG OKS																															
Revision	Building	Level	Door Number	Type Mark	To Room	To Room: Number	From Room	Leaf Type	Panel 1 Height	Panel 1 Width	Panel 2 Width	Fire Rating	Acoustic Rating	Undercut Height	Frame Type	Architrave	Door Closer	Seals	Elec Striking/Lock	Hold Open	Card Reader/Key Pad	Push to Exit	Locks	Keying Cylinder	Front Door Protection	Front DP Height	Rear Door Protection	Rear DP Height	Auto Door	Comments	
RACF																															
P3	RACF	Basement	R.B01.1	TD01	CARPARK	R.B01	RAMP	P3	-	2600	4000														Protection : NI	0	Protection : NI	0			BASEMENT ENTRY TILT DOOR - REFER ELEVATION AND SCHEDULE
P3	RACF	Basement	R.B02.1	D15	HYDRAULIC PLANT ROOM	R.B02	CARPARK	A2	2040	920	920			20	ST1	-	DC		ML			CR	PEX		Protection : NI	0	Protection : NI	0			
P3	RACF	Basement	R.B03.1	DF02	STAIR 01	R.B03	CARPARK	F5	2040	920	920	1HR		0	ST3	-	DC	FS	ES			CR		Protection : NI	0	Protection : NI	0				
C1	RACF	Basement	R.B04.1	DS04	CARPARK	R.B01	RACF LIFT LOBBY	F10	2040	1200	1200	SM		20	ST3	-	DC		SS	ES	ELEC	KP		Protection : DPR1	900	Protection : DPR1	900			SMOKE DOOR WITH VISION PANEL. REQUIRES SAFETY GLASS	
C1	RACF	Basement	R.B04.2	DS03	CARPARK	R.B01	RACF LIFT LOBBY	S-D2	2040	980	980	SM		20	AL2	-	DC		SS			KP	PEX	Protection : NI	0	Protection : NI	0		AUTO SLIDE	REF. INTERNAL GLAZING SCHEDULE. CONTRAST STRIP TO AS 1288. SMOKE DOOR, SAFETY GLASS.	
P3	RACF	Basement	R.B05.1	D11	STORE	R.B05	CARPARK	C2	2040	920	920	1HR		20	ST1	-	DC		ML			CR	PEX	Protection : NI	0	Protection : NI	0			VISION PANEL	
P3	RACF	Basement	R.B06.1	DF02	STAIR 02	R.B06	CARPARK	F5	2040	920	920	1HR		0	ST3	-	DC	FS	ES			CR		Protection : NI	0	Protection : NI	0				
P3	RACF	Basement	R.B07.1	D11	STORE	R.B07	CARPARK	C2	2040	920	920	1HR		20	ST1	-	DC		ML			CR	PEX	Protection : NI	0	Protection : NI	0			VISION PANEL	
C1	RACF	RACF Ground	LW.G1.1	D38			CIRCULATION LINK	D2	2630	970	970			20	AL1	-	DC		ES			CR		Protection : NI	0	Protection : NI	0			EXTERNAL HINGE DOOR - REFER WINDOW SCHEDULE. CONTRAST STRIP TO AS 1288	
C1	RACF	RACF Ground	LW.G1.2	D38			CIRCULATION LINK	D2	2630	970	970			20	AL1	-	DC		ES			CR		Protection : NI	0	Protection : NI	0			EXTERNAL HINGE DOOR - REFER WINDOW SCHEDULE. CONTRAST STRIP TO AS 1288	
P3	RACF	RACF Ground	R.G01.1	D20	AIRLOCK	R.G01	FIP	A9	2340	860	860			20	ST1	-	DC						KEY		MM						FIRE INDICATOR PANEL - LAMINATE FINISH, JOINERY STYLE DOOR
C1	RACF	RACF Ground	R.G02.1	D31	SALES MANAGER	R.G02	ENTRY	D1	2340	970	970			20	AL1	-	DC		ES			CR		Protection : NI	0	Protection : NI	0			REFER INTERNAL GLAZING SCHEDULE	
C1	RACF	RACF Ground	R.G03.1	D31	VILLAGE MANAGER	R.G03	CORRIDOR	D1	2340	970	970			20	AL1	-	DC		ES			CR		Protection : NI	0	Protection : NI	0			REFER INTERNAL GLAZING SCHEDULE	
C1	RACF	RACF Ground	R.G04.1	D31	CBM OFFICE	R.G04	CORRIDOR	D1	2340	970	970			20	AL1	-	DC		ES			CR		Protection : NI	0	Protection : NI	0			REFER INTERNAL GLAZING SCHEDULE	
C1	RACF	RACF Ground	R.G05.1	D31	MEETING	R.G05	CORRIDOR	D1	2340	970	970			20	AL1	-	DC							KEY		AD					
P3	RACF	RACF Ground	R.G06.1	D09	STORE	R.G06	CORRIDOR	A2	2340	920	920			20	ST1	1 SIDE	DC		ES			CR		Protection : NI	0	Protection : NI	0				
C1	RACF	RACF Ground	R.G07.1	D31	STAFF ADMIN	R.G07	CORRIDOR	D1	2340	970	970			20	AL1	-	DC		ES			CR		Protection : NI	0	Protection : NI	0			PRIVACY FILM - TO BE REVIEWED	
P3	RACF	RACF Ground	R.G07.2	D09	STAFF ADMIN	R.G07	RECEPTION	A2	2340	920	920			20	ST1	2 SIDE	DC		ES			CR		Protection : NI	0	Protection : NI	0			ALLOW DECORATIVE FINISH TO PUBLIC SIDE	
C1	RACF	RACF Ground	R.G08.1	D31	CORRIDOR	R.G08	ENTRY	D1	2340	970	970			20	AL1	-	DC		ES			CR		Protection : NI	0	Protection : NI	0			REFER INTERNAL GLAZING SCHEDULE	
C1	RACF	RACF Ground	R.G14.1	D54	AIRLOCK	R.G01	ENTRY	S-D2	2340	870	870	2HR		20	AL2	-	DC					KP	PEX	Protection : NI	0	Protection : NI	0		AUTO SLIDE	REFER INTERNAL GLAZING SCHEDULE. CONTRAST STRIP TO AS 1288	
C1	RACF	RACF Ground	R.G14.2	DF11			CIRCULATION LINK	F7	2040	920	920	2HR		0	ST3	2 SIDE	DC		FS			HOM		Protection : NI	0	Protection : NI	0			PULL HANDLE TO PULL SIDE ONLY. PUSH PLATE TO PUSH SIDE	
C1	RACF	RACF Ground	R.G14.3	D57			CIRCULATION	S-02	2340	1600	1600			20	AL2	-	DC					KP	PEX	Protection : NI	0	Protection : NI	0		AUTO SLIDE	REFER INTERNAL GLAZING SCHEDULE. CONTRAST STRIP TO AS 1288	
C1	RACF	RACF Ground	R.G14.7	D34			CIRCULATION	D1	2040	920	920			20	AL1	-	DC					KP	PEX	Protection : NI	0	Protection : NI	0		AUTO HINGE	REFER INTERNAL GLAZING SCHEDULE	
C1	RACF	RACF Ground	R.G16.1	D56			CIRCULATION	G14	LOBBY	S-D1	2340	1500			20	AL2	-	DC						Protection : NI	0	Protection : NI	0			AUTO SLIDE	
C1	RACF	RACF Ground	R.G17.1	D31	SALON	R.G17	LOBBY	D1	2340	970	970			20	AL1	-	DC		ES			CR		Protection : NI	0	Protection : NI	0				
C1	RACF	RACF Ground	R.G17.2	D31	SALON	R.G17	CIRCULATION	D1	2340	970	970			20	AL1	-	DC		ES			CR		Protection : NI	0	Protection : NI	0				
C1	RACF	RACF Ground	R.G19.1	D52	LOUNGE	R.G18	PRIVATE DINING/MEETING	S-D1	2340	970	970			20	AL2	-	DC							Protection : NI	0	Protection : NI	0				
C1	RACF	RACF Ground	R.G20.1	D10	FURNITURE STORE	R.G20	LOUNGE	A2	2340	920	920			20	ST1	1 SIDE	DC					ML	CR	PEX	Protection : NI	0	Protection : NI	0			ALLOW DECORATIVE FINISH TO PUBLIC SIDE
C1	RACF	RACF Ground	R.G21.1	D33	LOUNGE	R.G18	LIBRARY	D1	2340	920	920			20	AL1	-	DC							Protection : NI	0	Protection : NI	0				
P3	RACF	RACF Ground	R.G24.1	D09	MALE WC	R.G24	AIRLOCK	A2	2340	920	920			20	ST1	1 SIDE	DC							Protection : NI	0	Protection : NI	0			ALLOW CEILING AIR TRANSFER GRILLE	
P3	RACF	RACF Ground	R.G25.1	D09	ACC. WC	R.G25	AIRLOCK	A2	2340	920	920			20	ST1	1 SIDE	DC							Protection : DPR2	140	Protection : DPR2	140			ALLOW CEILING AIR TRANSFER GRILLE	
C1	RACF	RACF Ground	R.G26.1	D09	FEMALE WC	R.G26	AIRLOCK	A2	2340	920	920			20	ST1	1 SIDE	DC							Protection : NI	0	Protection : NI	0			ALLOW CEILING AIR TRANSFER GRILLE	
C1	RACF	RACF Ground	R.G29.1	D13	THEATRE/CHAPEL	R.G29	CIRCULATION	A4	2340	970	970			20	ST3	2 SIDE	DC		AS					Protection : NI	0	Protection : NI	0				
C1	RACF	RACF Ground	R.G30.1	D31	FLEX / GROUP EXERCISE	R.G30	CIRCULATION	D1	2340	970	970			20	AL1	-	DC	AS	ES			CR		Protection : NI	0	Protection : NI	0			REFER INTERNAL GLAZING SCHEDULE	
P3	RACF	RACF Ground	R.G30.2	OP01	FLEX / GROUP EXERCISE	R.G30	GYM	L	2340	1044	1044			0	ST3	2 SIDE	DC		AS					Protection : NI	0	Protection : NI	0			2400H SOLID OPERABLE WALL - 5 EQUAL PANELS - REFER ELEVATION	
C1	RACF	RACF Ground	R.G31.1	D31	GYM	R.G31	CIRCULATION	D1	2340	970	970			20	AL1	-	DC	AS	ES			CR		Protection : NI	0	Protection : NI	0			REFER INTERNAL GLAZING SCHEDULE	
C1	RACF	RACF Ground	R.G32.1	D31	CONS	R.G32	CIRCULATION	D1	2340	970	970			20	AL1	-	DC	AS					KEY		AD				ALLOW FULL HEIGHT PRIVACY FILM		
C1	RACF	RACF Ground	R.G33.1	D31	CONS	R.G33	CIRCULATION	D1	2340	970	970			20	AL1	-	DC	AS					KEY		AD				ALLOW FULL HEIGHT PRIVACY FILM		
C1	RACF	RACF Ground	R.G35.1	D20	LOADING	R.G35																KP	PEX	Protection : NI	0	Protection : NI	0			AUTOMATIC ROLLER DOOR - REFER ELEVATION	
P3	RACF	RACF Ground	R.G35.2	D16	LOADING	R.G35	BULK STORAGE	A2	2040	820	820			20	ST1	-	DC						KEY	SS	Protection : NI	0	Protection : DPR1	900			
P3	RACF	RACF Ground	R.G35.3	D16	LOADING	R.G35	BULK STORAGE	A2	2040	820	820			20	ST1	-	DC						KEY	SS	Protection : NI	0	Protection : DPR1	900			
P3	RACF	RACF Ground	R.G35.4	D16	LOADING	R.G35	HARD WASTE	A2	2040	820	820			20	ST1	-	DC						KEY	MM	Protection : NI	0	Protection : DPR1	900			
C1	RACF	RACF Ground	R.G36.1	D11	WASTE	R.G36	LOADING	C2	2040	920	920			20	ST1	-	DC		ML			CR	PEX	Protection : DPR1	900	Protection : DPR1	900			VISION PANEL	
C1	RACF	RACF Ground	R.G36.2	D11	WASTE	R.G36	BOH CORRIDOR	C2	2040	920	920			20	ST1	-	DC		ML			CR	PEX	Protection : DPR1	900	Protection : DPR1	900			VISION PANEL	
P3	RACF	RACF Ground	R.G36.3	D15	WASTE	R.G36	WASTE	A2	2040	920	920			20	ST1	-	DC</														