

Legend - Internal Elevations

DRAWINGS TO BE READ IN CONJUNCTION WITH ARCHITECTURAL SPECIFICATION & MATERIALS, PRODUCTS & FINISHES SCHEDULE.

PT# PAINT FINISH TO ALL WALLS WITHIN NEW & AFFECTED ROOMS/ AREAS UNLESS OTHERWISE SHOWN

- CSE CONCRETE SEALER
- DPR DOOR PROTECTION
- GD GRAPHIC FILM
- LM LAMINATE
- MI MIRROR
- PBD PINBOARD
- PT PAINT FINISH
- REN RENDER FINISH
- SB SPLASHBACK
- ST STONE
- WB WHITEBOARD
- WP WALL PROTECTION
- WT WALL TILE
- WV WALL VINYL
- UPH UPHOLSTERY

NOTES:
1. LAMINATE CARCASS FOR ALL VISIBLE OPEN SHELVING, UNLESS OTHERWISE NOTED
2. MELAMINE TO ALL INTERNAL CARCASS OF JOINERY, UNLESS OTHERWISE NOTED.


--- PROVIDE NOGGINGS FOR FUTURE USE

Legend - Floor Finishes


- C CARPET
- CO CONCRETE
- E EPOXY FINISH
- L LINOLEUM
- M MATTING
- PU PAVING UNIT - TBC WITH LANDSCAPE
- R RUBBER FLOORING
- T TILING
- TF TIMBER FLOORING
- V VINYL
- LVT LUXURY VINYL TILE PLANK

Keynote Legend


- 2DSOG DISPENSER - DISPOSABLE GLOVE - GROUP 2
- 2DSPBS BEDSHEET DISPENSER - GROUP 2
- 3ART ARTWORK - GROUP 3
- 3CTP CURTAINS - GROUP 3
- 3DSPPT DISPENSER - PAPER TOWEL - GROUP 3
- 3DSS SOAP DISPENSER - GROUP 3
- 3SHB BIN SHARPS - GROUP 3
- 3TBCO COFFEE TABLE - GROUP 3
- B6 BASIN - TYPE 6
- BH-J BULKHEAD - JOINERY TYPE
- CAM CCTV CAMERA
- CBU CUPBOARD
- CDR CARD READER
- DATA DATA OUTLET
- DRB DOOR RELEASE BUTTON
- EM EMERGENCY LIGHT
- FE-JC FIRE EXTINGUISHER IN JOINERY CUPBOARD
- GPO2 POWER OUTLET - DOUBLE
- GPOCL POWER OUTLET - CLEANERS
- LF1 LIGHT FITTING - REFER TO ELECTRICAL ENGINEER SPECIFICATION
- LF5 LIGHT FITTING - TYPE 5
- LF9 LIGHT FITTING - TYPE 9
- LS LIGHT SWITCH
- MD MOTION DETECTOR
- NC NURSE CALL
- SH SHELF
- SK2 SKIRTING - TYPE 2
- SMD SMOKE DETECTOR
- SPK ANNUNCIATOR SPEAKER
- SPR SPRINKLER
- TAP4 TAP - TYPE 4
- WAP WIRELESS ACCESS POINT

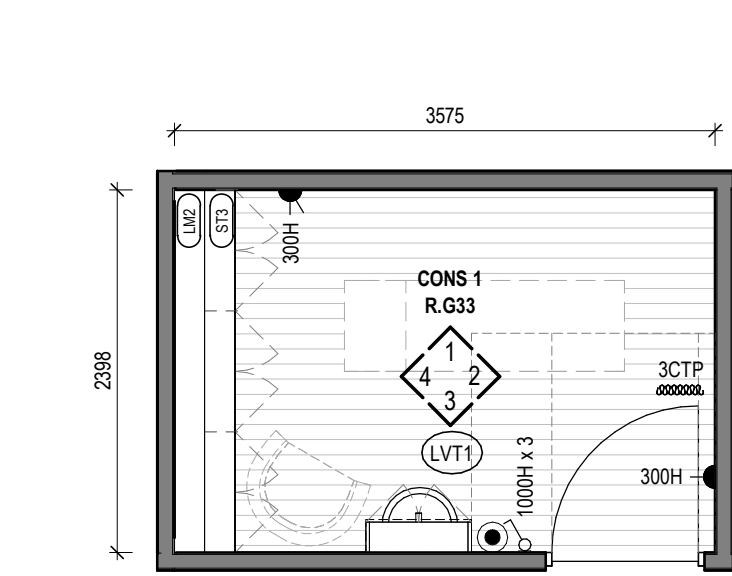


1 VILLAGE HEALTH & WELLNESS - CONSULT 1
Scale 1: 50

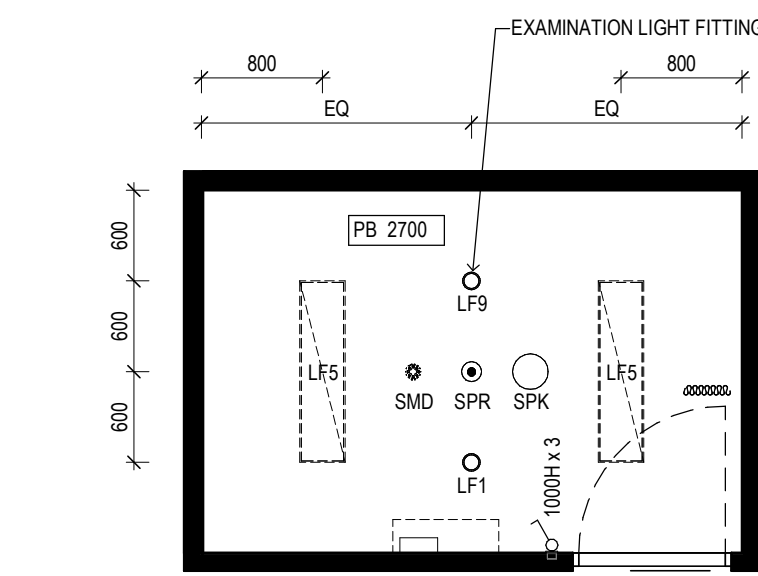


2 RCP - VILLAGE HEALTH & WELLNESS - CONSULT 1
Scale 1: 50

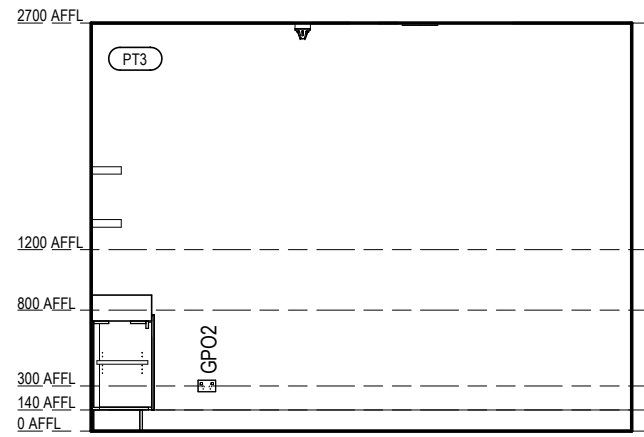


VILLAGE HEALTH & WELLNESS - CONSULT 1
ELEVATION 1
Scale 1: 50

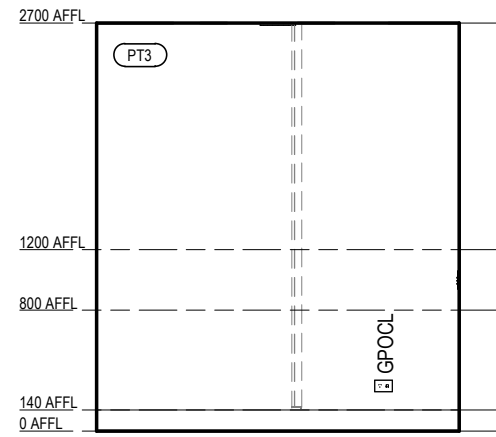


VILLAGE HEALTH & WELLNESS - CONSULT 1
ELEVATION 2
Scale 1: 50

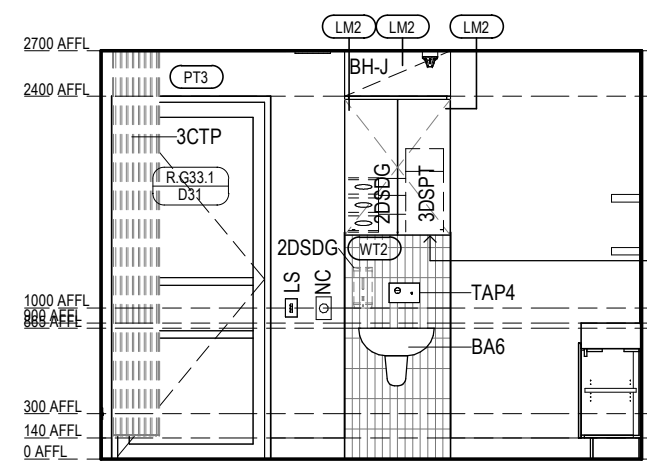


VILLAGE HEALTH & WELLNESS - CONSULT 1
ELEVATION 3
Scale 1: 50

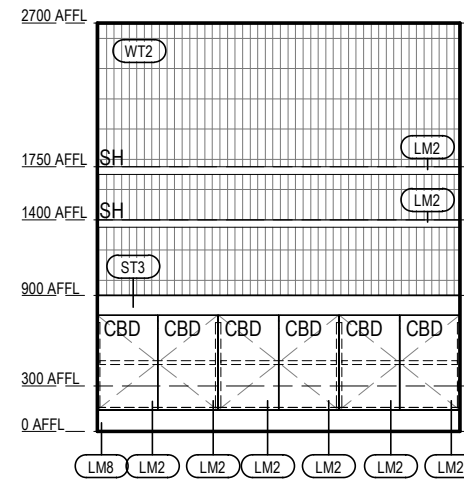


VILLAGE HEALTH & WELLNESS - CONSULT 1
ELEVATION 4
Scale 1: 50

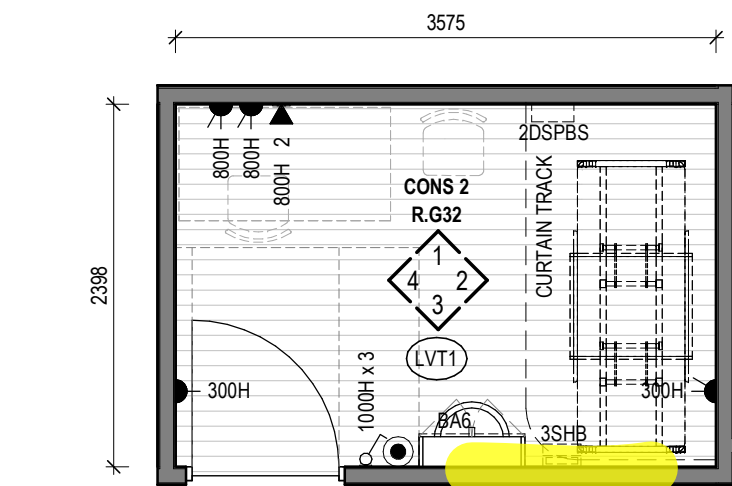


3 VILLAGE HEALTH & WELLNESS - CONSULT 2
Scale 1: 50

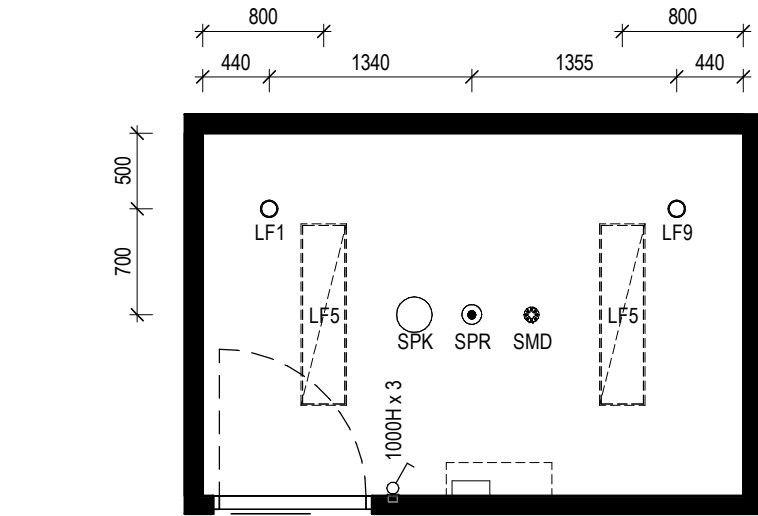


4 RCP - VILLAGE HEALTH & WELLNESS - CONSULT 2
Scale 1: 50

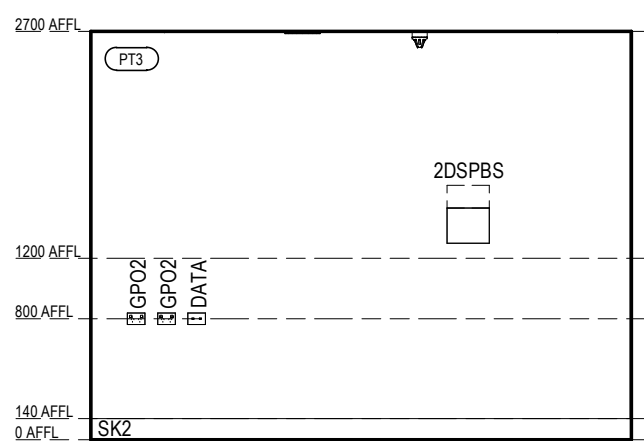


VILLAGE HEALTH & WELLNESS - CONSULT 2
ELEVATION 1
Scale 1: 50

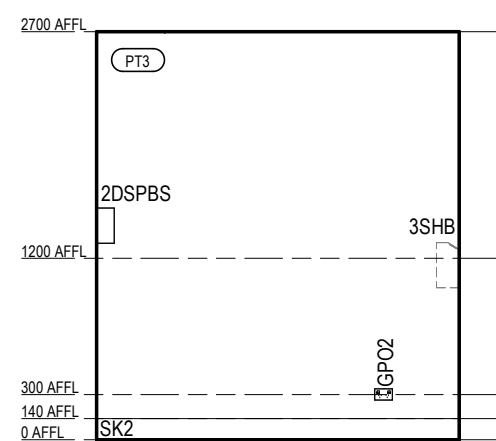


VILLAGE HEALTH & WELLNESS - CONSULT 2
ELEVATION 2
Scale 1: 50

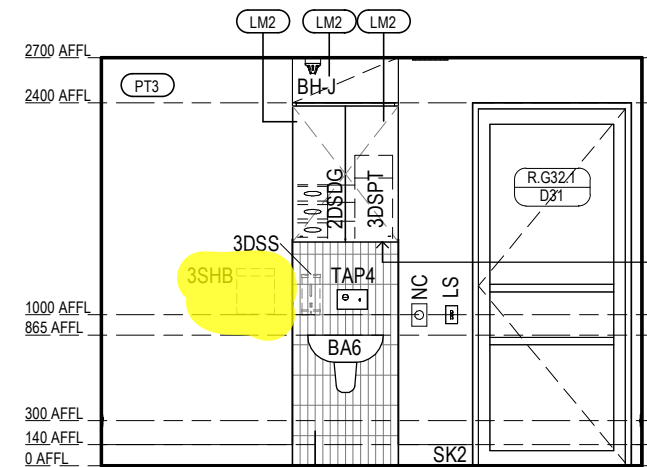


VILLAGE HEALTH & WELLNESS - CONSULT 2
ELEVATION 3
Scale 1: 50

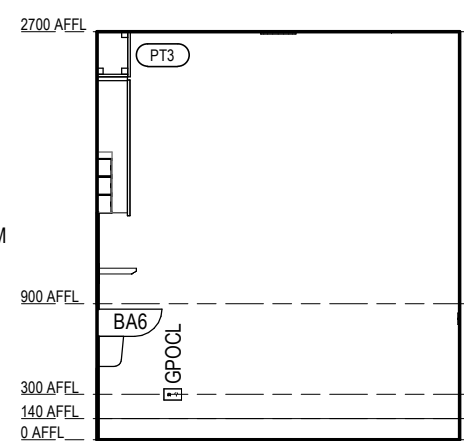


VILLAGE HEALTH & WELLNESS - CONSULT 2
ELEVATION 4
Scale 1: 50

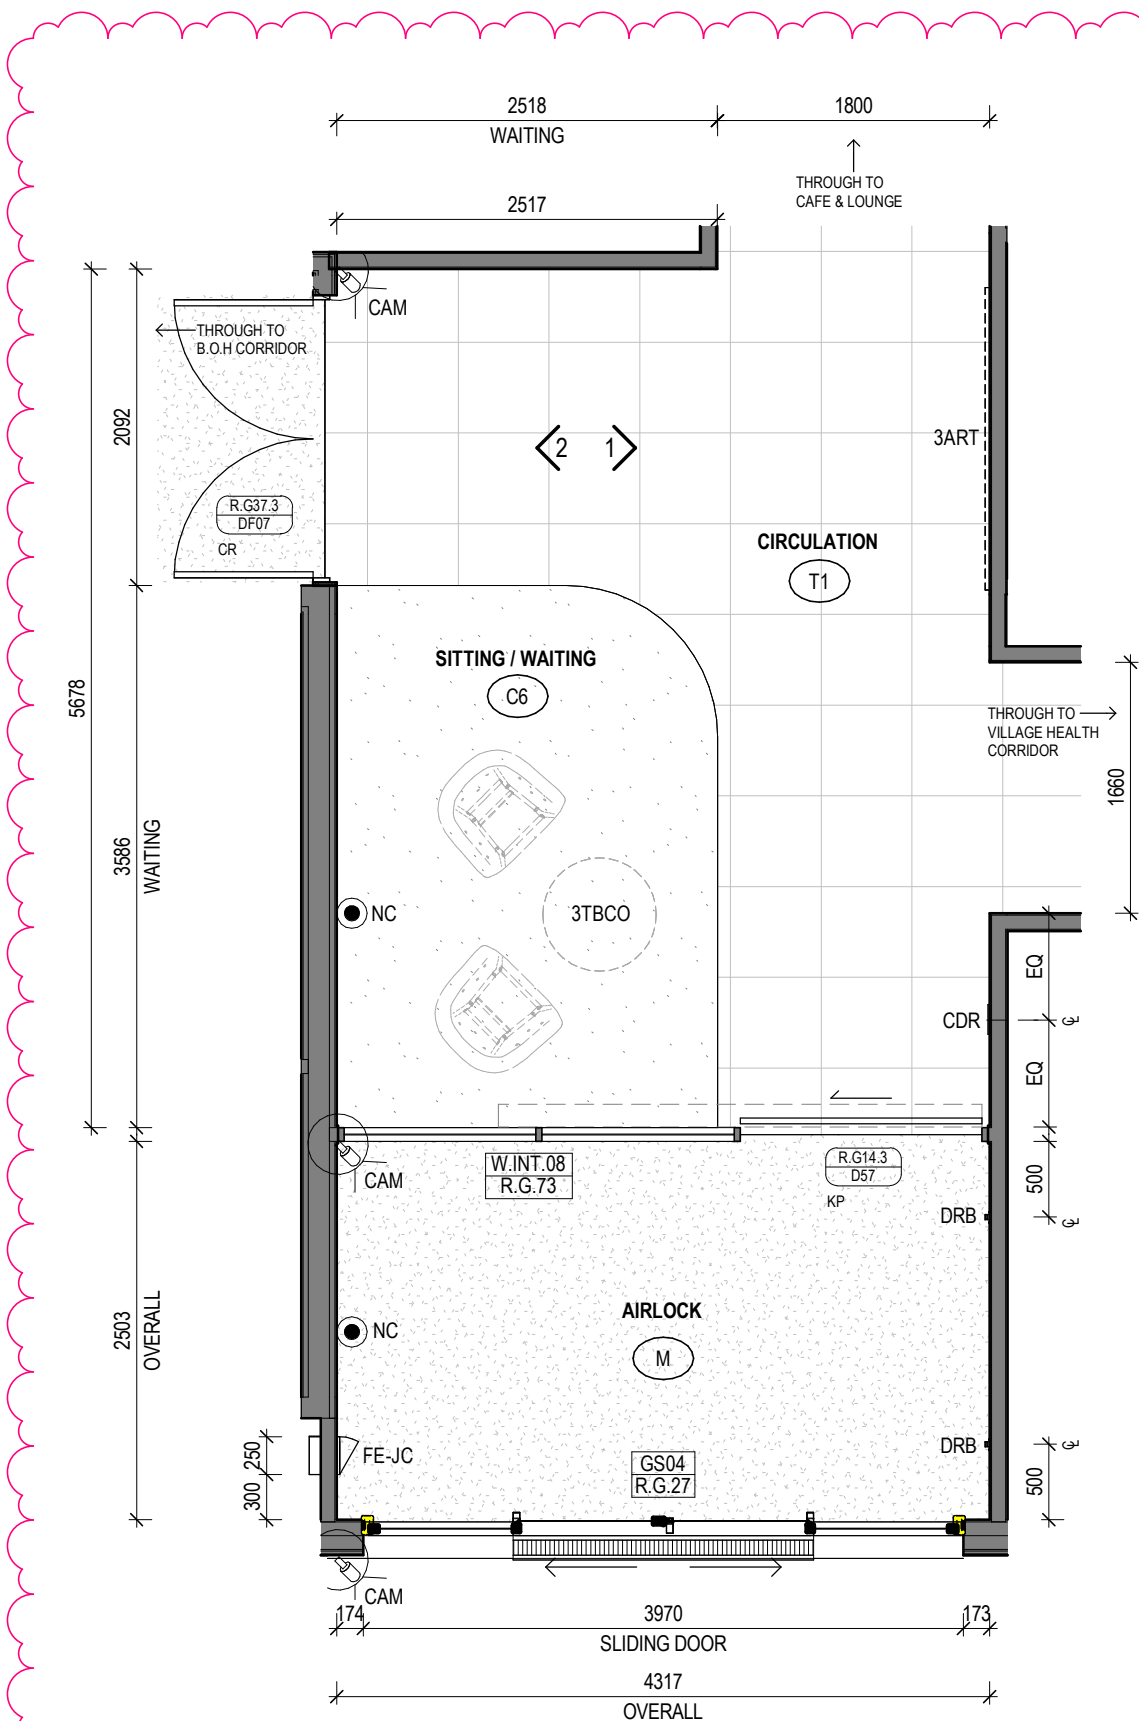


5 VILLAGE HEALTH & WELLNESS - AIRLOCK & WAITING
Scale 1: 50

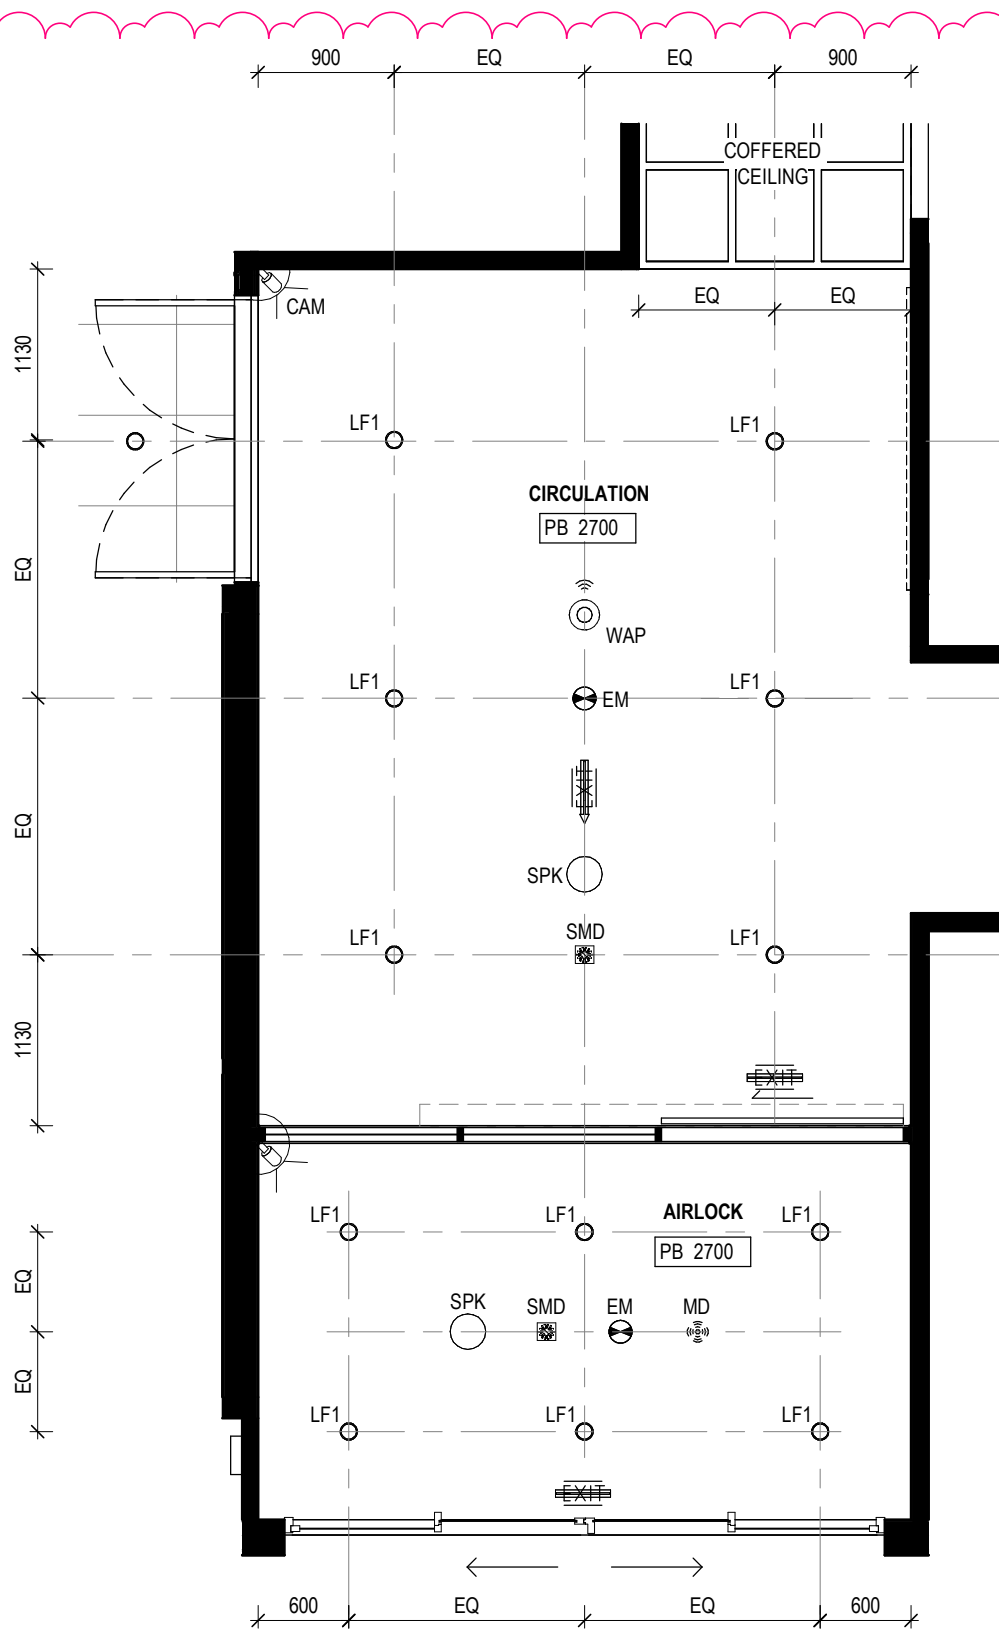

6 RCP - VILLAGE HEALTH & WELLNESS - AIRLOCK & WAITING
Scale 1: 50

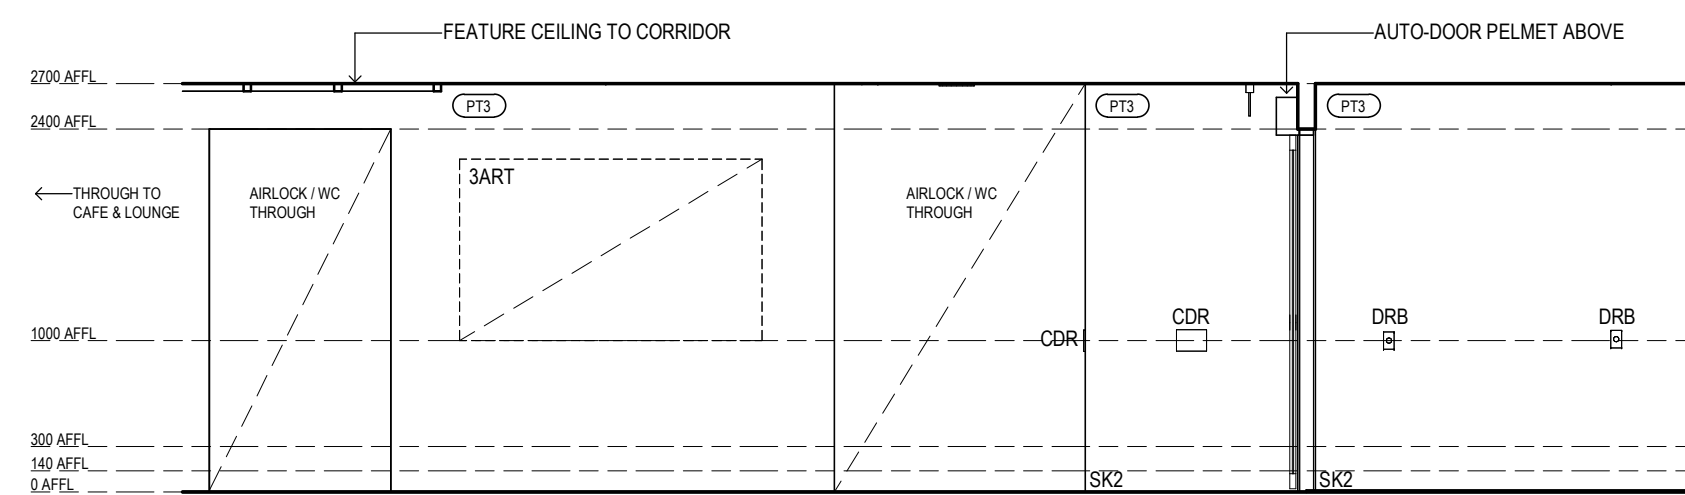

VILLAGE HEALTH & WELLNESS - AIRLOCK & CIRCULATION
ELEVATION 1
Scale 1: 50

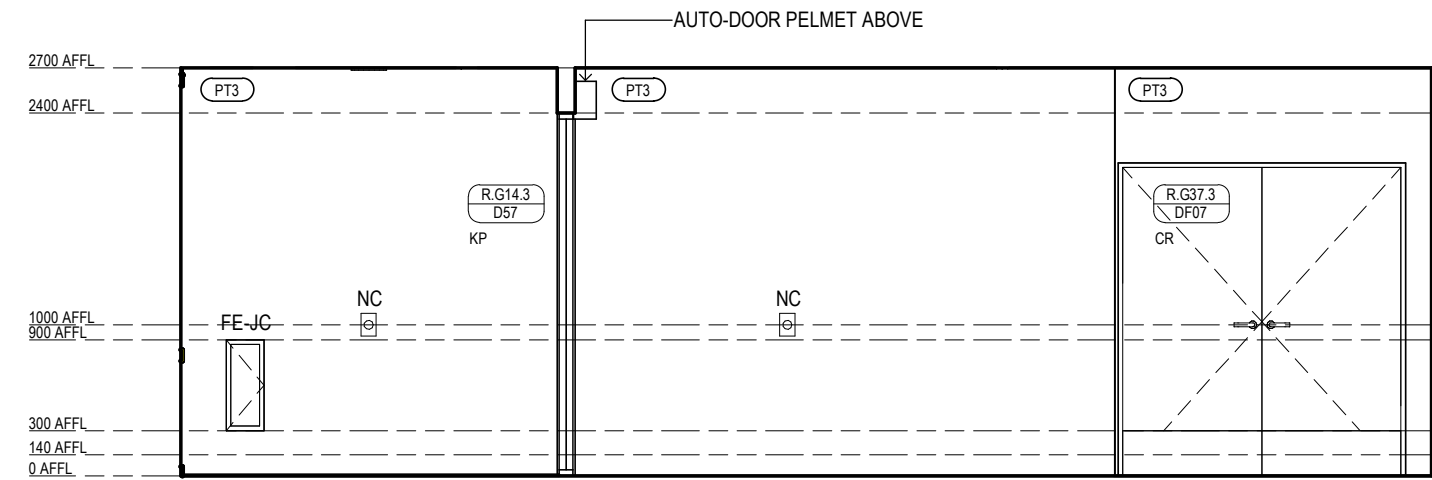

VILLAGE HEALTH & WELLNESS - AIRLOCK & WAITING
ELEVATION 2
Scale 1: 50

Revision/Issue	Date
C1 ISSUE FOR CONSTRUCTION - INTERIORS	2026.03.26
C2 ISSUE FOR CONSTRUCTION	2026.05.08

Clarke
Hopkins
Clarke

Melbourne | Wurundjeri
L3, Melbourne Connect
700 Swanston Street
Carlton VIC 3063
Telephone (03) 9419 4340
Email studio@chc.com.au
www.chc.com.au

Sydney | Gadigal Country
Suite 3, Ground Floor
91 Campbell Street
Surry Hills NSW 2010
Telephone (02) 9221 9200
Email studio@chc.com.au
www.chc.com.au

Scale	1: 50 @ A1
Date	01/03/2024
Drawn	TM / DP
Architect	EL

Project	Summerset Oakleigh 52 Golf Road, Oakleigh South, VIC
---------	---

Drawing	Internal Elevations - Village Health & Wellness - Consult, Airlock & Waiting
---------	--

Drawing No.	230185/A1809	C2
-------------	--------------	----

FOR CONSTRUCTION