



JOINERY - NOTES

- JOINER TO MEASURE ON SITE BEFORE MANUFACTURING JOINERY UNITS.
- DIMENSIONS ARE NOMINAL. ALWAYS CHECK ON SITE AND COORDINATE WITH ARCHITECT/PROJECT MANAGER.
- ALL BRACING & SUPPORT FOR STABILITY WITHIN JOINERY TO BE CONCEALED AS REQUIRED.
- MAXIMUM REACHABLE HEIGHT TO BE 1800MM TO TOP OF SHELF, ANYTHING HIGHER TO BE APPROVED BY CHC.
- PROVIDE INFILLS FOR TIGHT CORNERS - NOM. 25/40MM MAX.
- ALL SHARKNOSE DOOR PULLS TO BE 25MM CLEAR FROM OBSTRUCTION.
- ALL SUBSTITUTIONS OF ITEMS IN SCHEDULE ARE TO BE APPROVED BY ARCHITECT OR INTERIOR DESIGNER.
- JOINER TO PROVIDE SHOP DRAWINGS TO BE APPROVED BY ARCHITECT/INTERIOR DESIGNER.
- ALL FIXED & WALL MOUNTED JOINERY TO BE FIXED ON STRUCTURAL MEMBER. PROVIDE ADDITIONAL SUPPORT AS REQUIRED. CONCEAL ALL FIXINGS UNLESS NOTED OTHERWISE.
- REFER TO ALL EQUIPMENT SPECIFICATIONS FOR ANY CLEARANCES AND VENTILATION REQUIREMENTS TO BE INTEGRATED.
- CONTRACTOR TO CONFIRM DIMENSIONS OF SELECTED APPLIANCES AND CHECK SUPPLIER SPECIFICATIONS TO ENSURE NEAT FIT INTO THE RECESS PROVIDED, INCLUDING ALLOWANCE FOR SERVICE CONNECTION.
- SERVICES TO JOINERY TO BE COORDINATED ON SITE.
- ALL FIXINGS TO FIXED OPEN SHELVES TO BE FULLY CONCEALED. ENSURE HEAVY DUTY CONCEALED BRACKETS AND FIXINGS TO HOLD THE SHELVES RIGHT ANGLE STRAIGHT ALIGNED AND SECURED TO THE WALL SUPPORT STRUCTURE.
- ALL INTERNAL JOINERY SURFACES FINISHED IN MELAMINE FINISH WITH SOLID COLOUR MATCH ABS EDGING UNLESS OTHERWISE NOTED ON DOCUMENTATION. NO INTERNAL SURFACES TO BE LEFT BARE.
- WHERE JOINERY UNITS ARE TO BE CONSTRUCTED IN MULTIPLE SECTIONS, CHECK INDIVIDUAL SECTION AND OVERALL UNIT DIMENSIONS COLLATE. LOCATE JOINT LINES AS INDICATED ON DRAWINGS, AND CONCEAL FIXINGS AT JOINT LINES.
- LAMINATE BENCHTOPS TO BE POST FORMED 40MM THICK WITH 5MM RADIUS TO TOP AND BOTTOM EDGE.
- STONE AND SOLID SURFACE (CORIAN) BENCHTOPS TO BE 40MM (UNLESS NOTED OTHERWISE) WITH 3MM ARRIS TOP AND BOTTOM EDGE.
- ALL INTERNAL SHELVING WITH OVERALL WIDTH DIMENSION 900MM OR LESS SHALL GENERALLY BE CONSTRUCTED FROM 18MM THICK MDF. INTERNAL SHELVING WITH OVERALL WIDTH DIMENSION GREATER THAN 900MM TO BE CONSTRUCTED FROM 25MM THICK MDF, UNLESS OTHERWISE NOTED.
- ADJUSTABLE SHELVING TO BE INSTALLED TO ALLOW ADJUSTMENT AT 50MM INCREMENTS.
- ENSURE ALL DOORS/ DRAWERS OPEN WITHOUT IMPEDIMENT FROM HINGES, ADJACENT JOINERY/WALL ETC.
- ALIGN FLOOR/FLOOR AND FLOOR/WALL TILE JOINTS. CHECK ON SITE ANY DESIGN DETAIL MATERIAL DATUM LINES TO BE COORDINATED PRIOR TO CONSTRUCTION OF JOINERY UNIT AS REQUIRED.
- ALL FINISHES JOINS GENERALLY TO BE APPROVED BY CHC PRIOR TO CONSTRUCTION.
- FLOOR FINISH MATERIAL TO BE SET OUT AS INDICATED ON PLANS. ALL FLOOR FINISH MATERIAL TO EXTEND BELOW AND BEYOND JOINERY KICKER. NO EXPOSED UNFINISHED FLOOR. GENERALLY ENSURE SKIRTING ALIGNMENT THROUGHOUT UNLESS NOTED OTHERWISE.
- ALL LAMINATED INTERNAL SURFACES AND EDGES SHALL ALL BE FINISHED IN MATCHING ABS EDGING STRIP UNLESS NOTED OTHERWISE.
- ALL JOINTS IN BENCHTOPS AND SPLASHBACK TO BE CONFIRMED WITH ARCHITECT PRIOR TO MANUFACTURE.
- PROVIDE MINIMUM OF 10MM RECESSED SHADOWLINE BETWEEN JOINERY TO JOINERY AND 20MM RECESSED SHADOWLINE AT JOINERY AND CEILING JUNCTION OR JOINERY AND WALL JUNCTION, UNLESS OTHERWISE NOTED.
- SHADOW GAPS TO WALL JUNCTION BE PAINTED TO MATCH ADJACENT WALL UNLESS OTHERWISE NOTED.
- ALL JOINERY DOORS/ DRAWERS FACE TO SIT FRONT OF JOINERY CARCASS. NOMINATED JOINERY FINISH TO BOTH SIDES FF DOOR/ DRAWER FACES.
- 25MM FINGER PULL TO ALL DRAWERS AND CUPBOARDS U N O.
- PROVIDE CAM LOCK TO ALL STORAGE AND DESK DRAWERS AND CUPBOARDS.
- ALL JOINERY TO BE RIGID SELF-SUPPORTING WITH SEAMLESS CONSISTENT FINISH THROUGHOUT. ENSURE ADEQUATE STRUCTURE TO SEATING JOINERY SELF-SUPPORTED TO BE ABLE TO WITHSTAND HIGH LOAD BEARING CAPACITY.
- ENSURE ALL DETAILING, SERVICES TO BE SHOWN ON SHOP DRAWINGS.
- ARCHITECT TO REVIEW WALL PROTECTION RAIL INSTALLATION HEIGHT ON SITE TO CONFIRM WALL DAMAGE ZONE FROM WALKERS.
- WHERE OVERHEAD CUPBOARDS ARE SHOWN WITHOUT JOINERY PULLS, ALLOW FOR DOOR FRONTS TO EXTEND FOR A FINGER PULL.

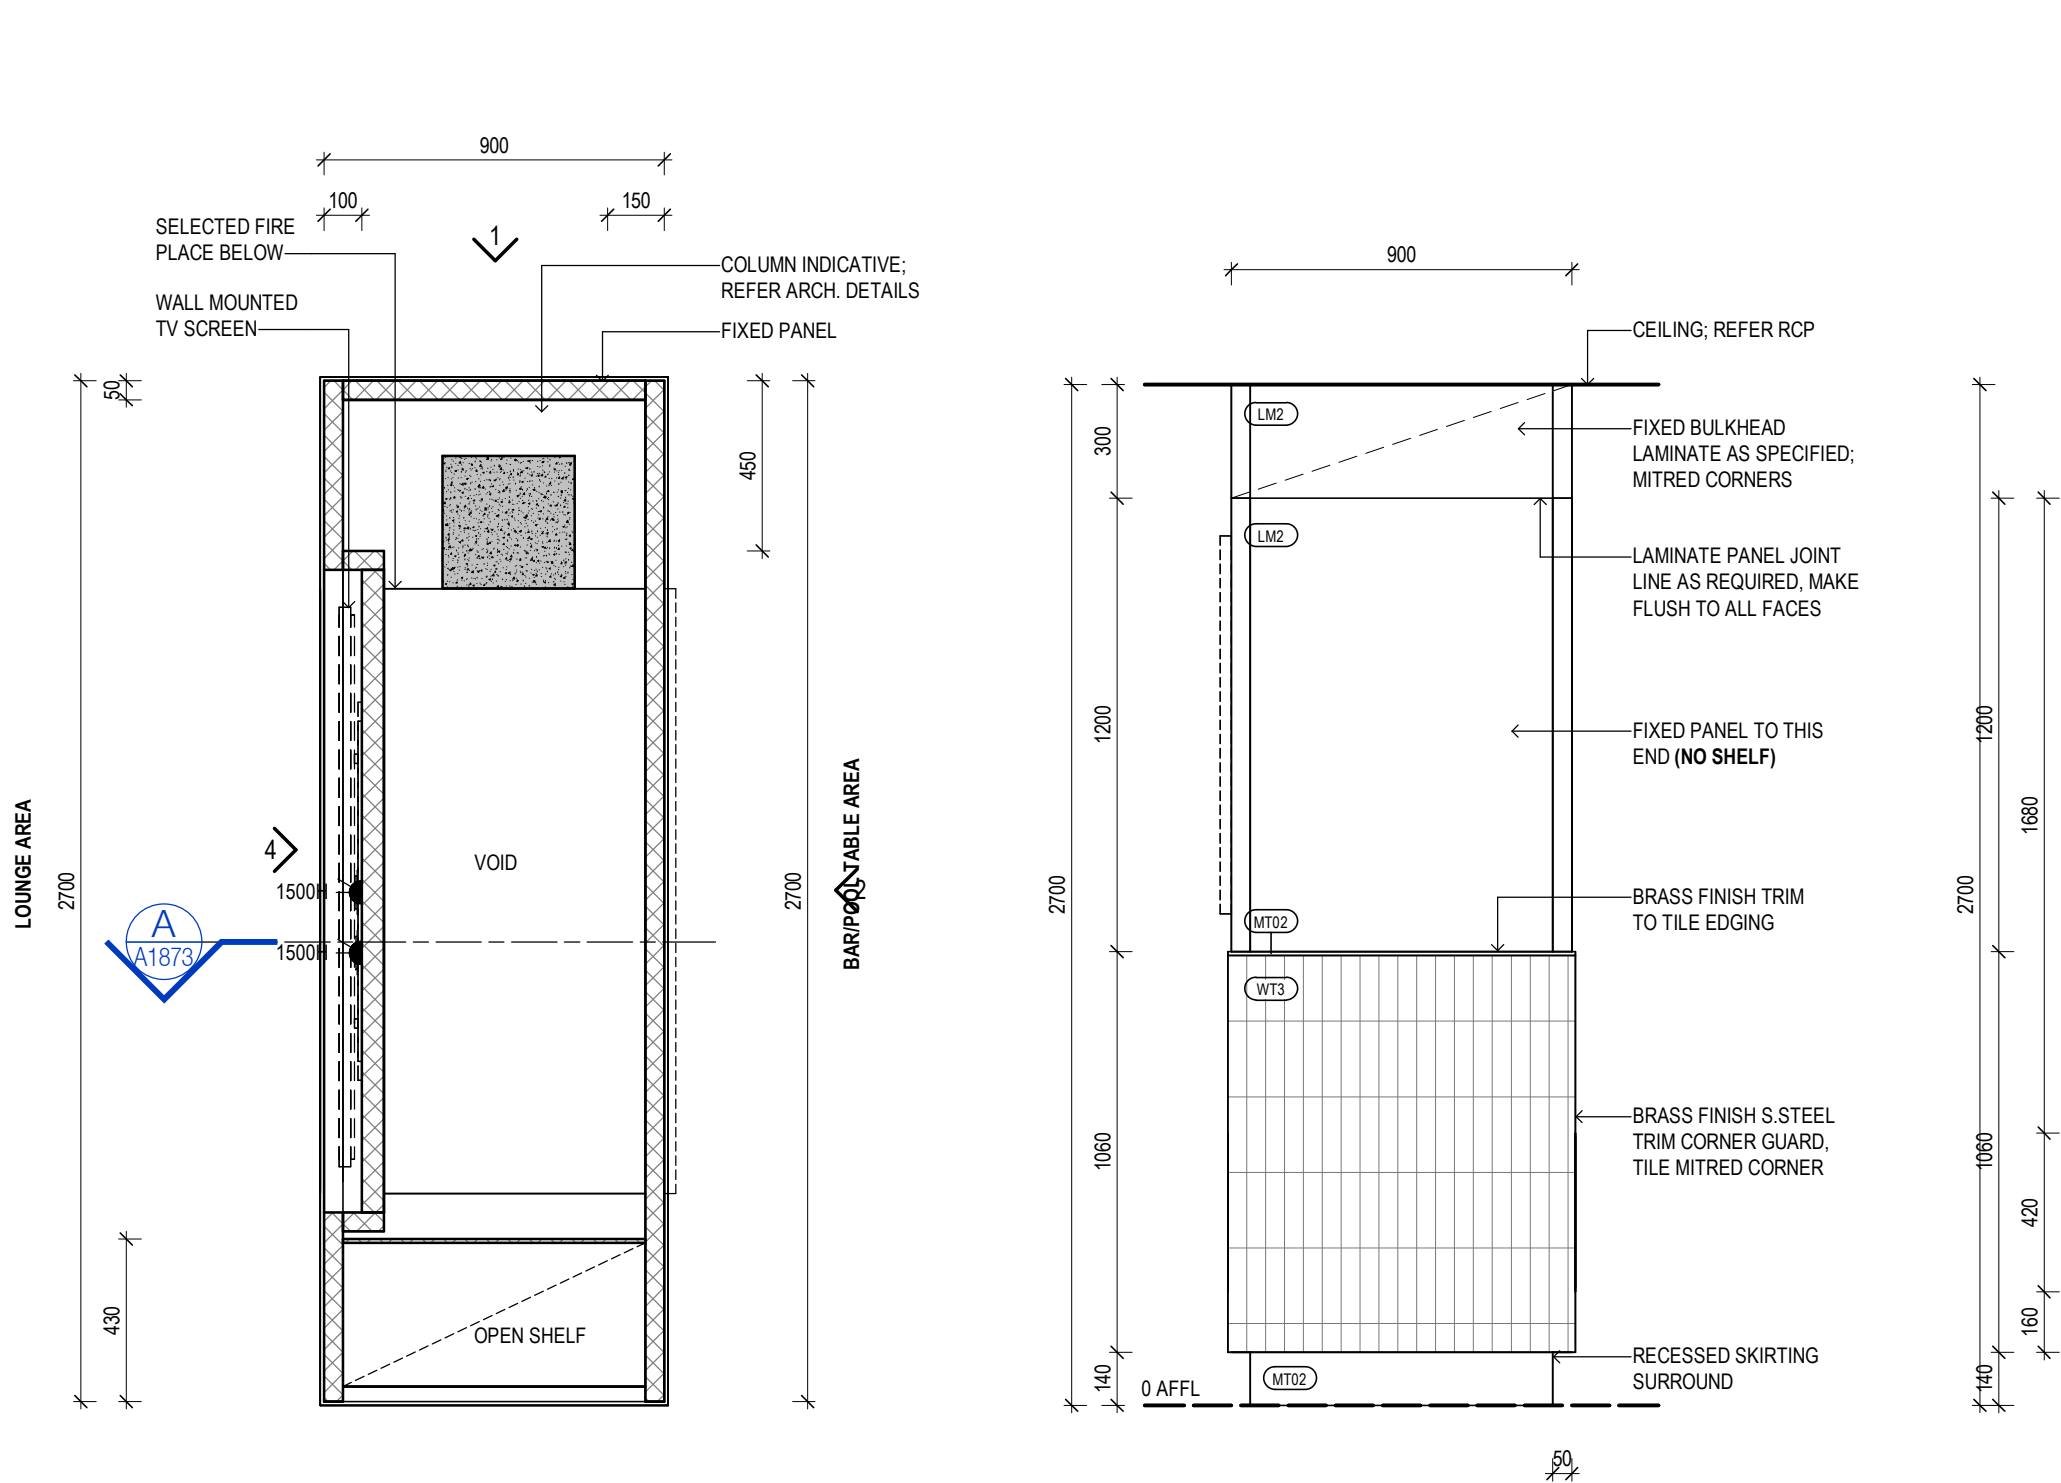

1 J-04 - SPORTS BAR JOINERY
Scale 1 : 20


J-04 - Sports Bar Joinery
ELEVATION 1
Scale 1 : 20

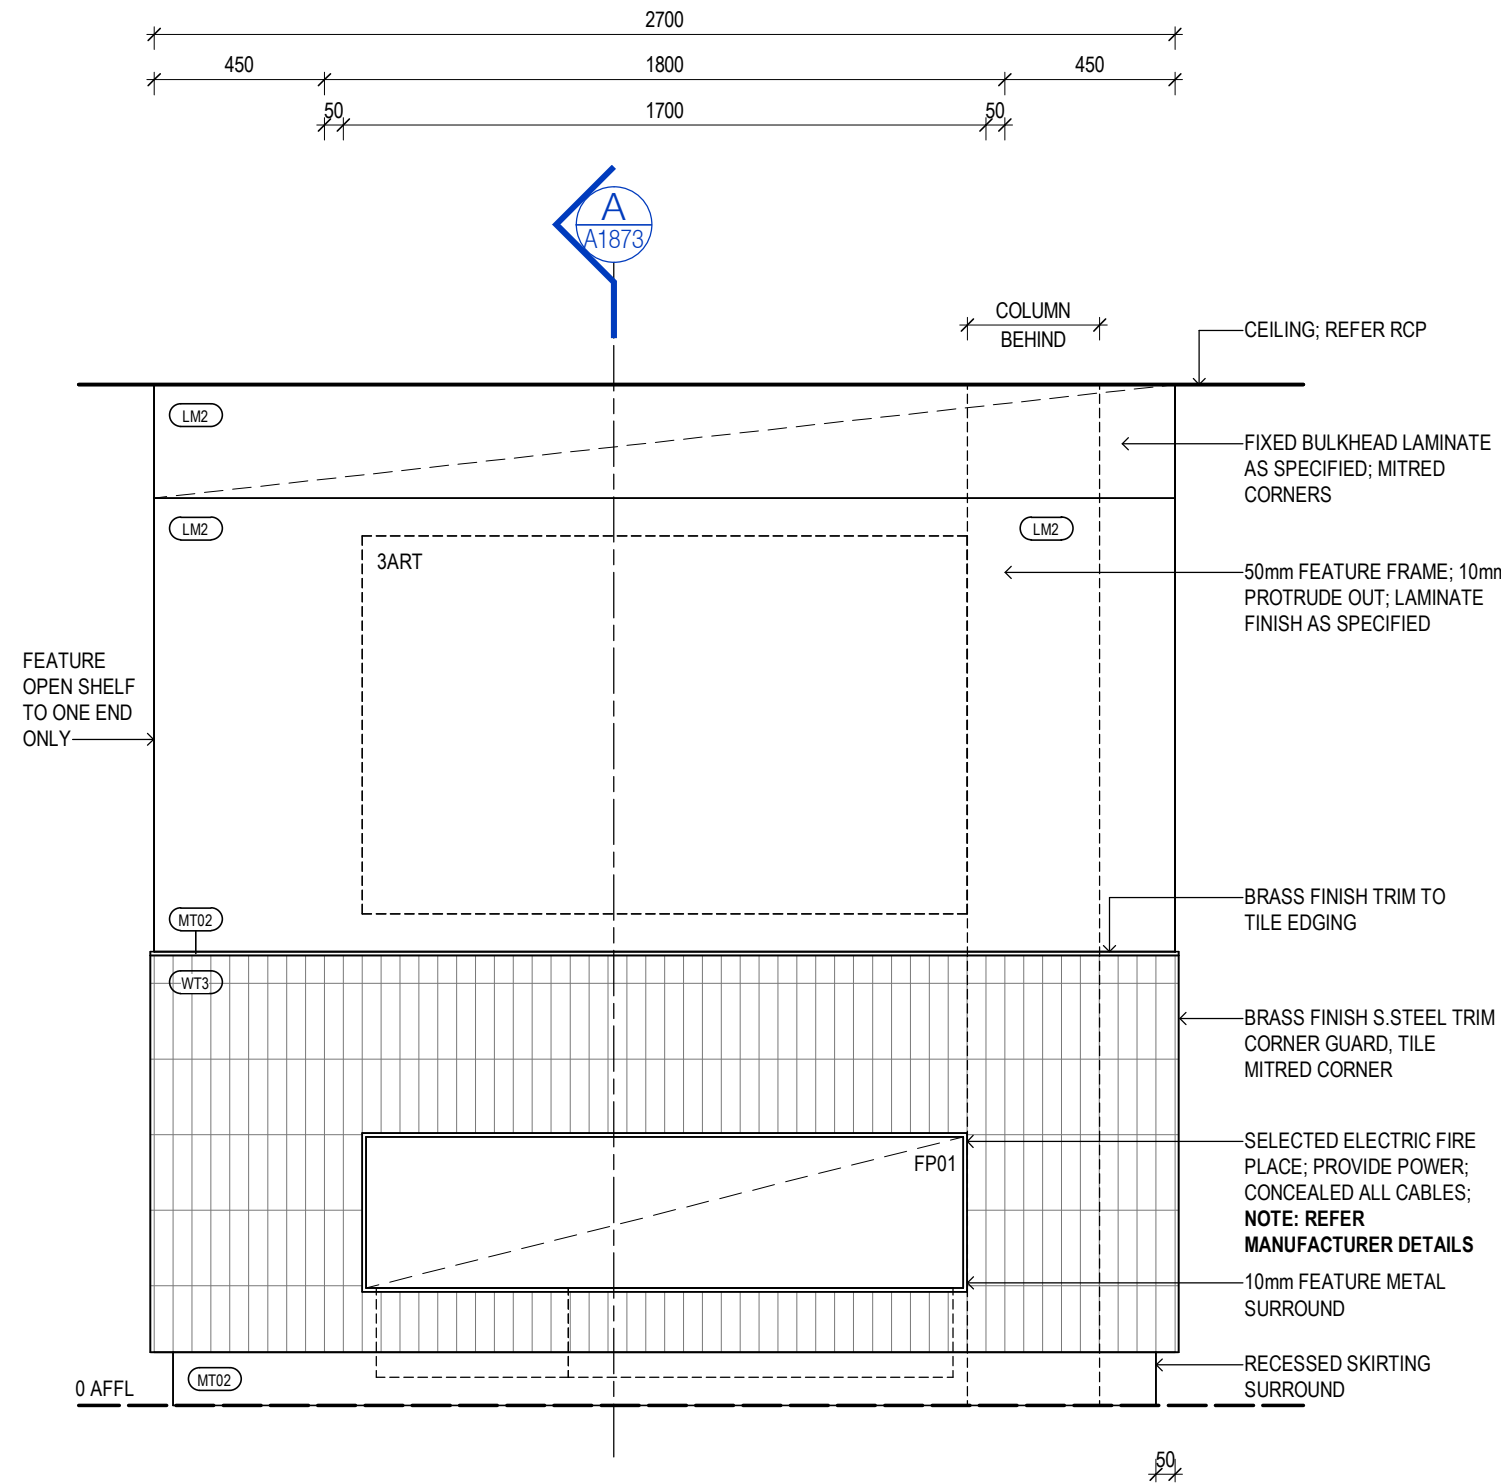


J-04 - Sports Bar Joinery - Bar/Pool Table Side
ELEVATION 2
Scale 1 : 20

3D SPORT UNIT - BAR/POOL TABLE SIDE


3D SPORT UNIT - LOUNGE SIDE

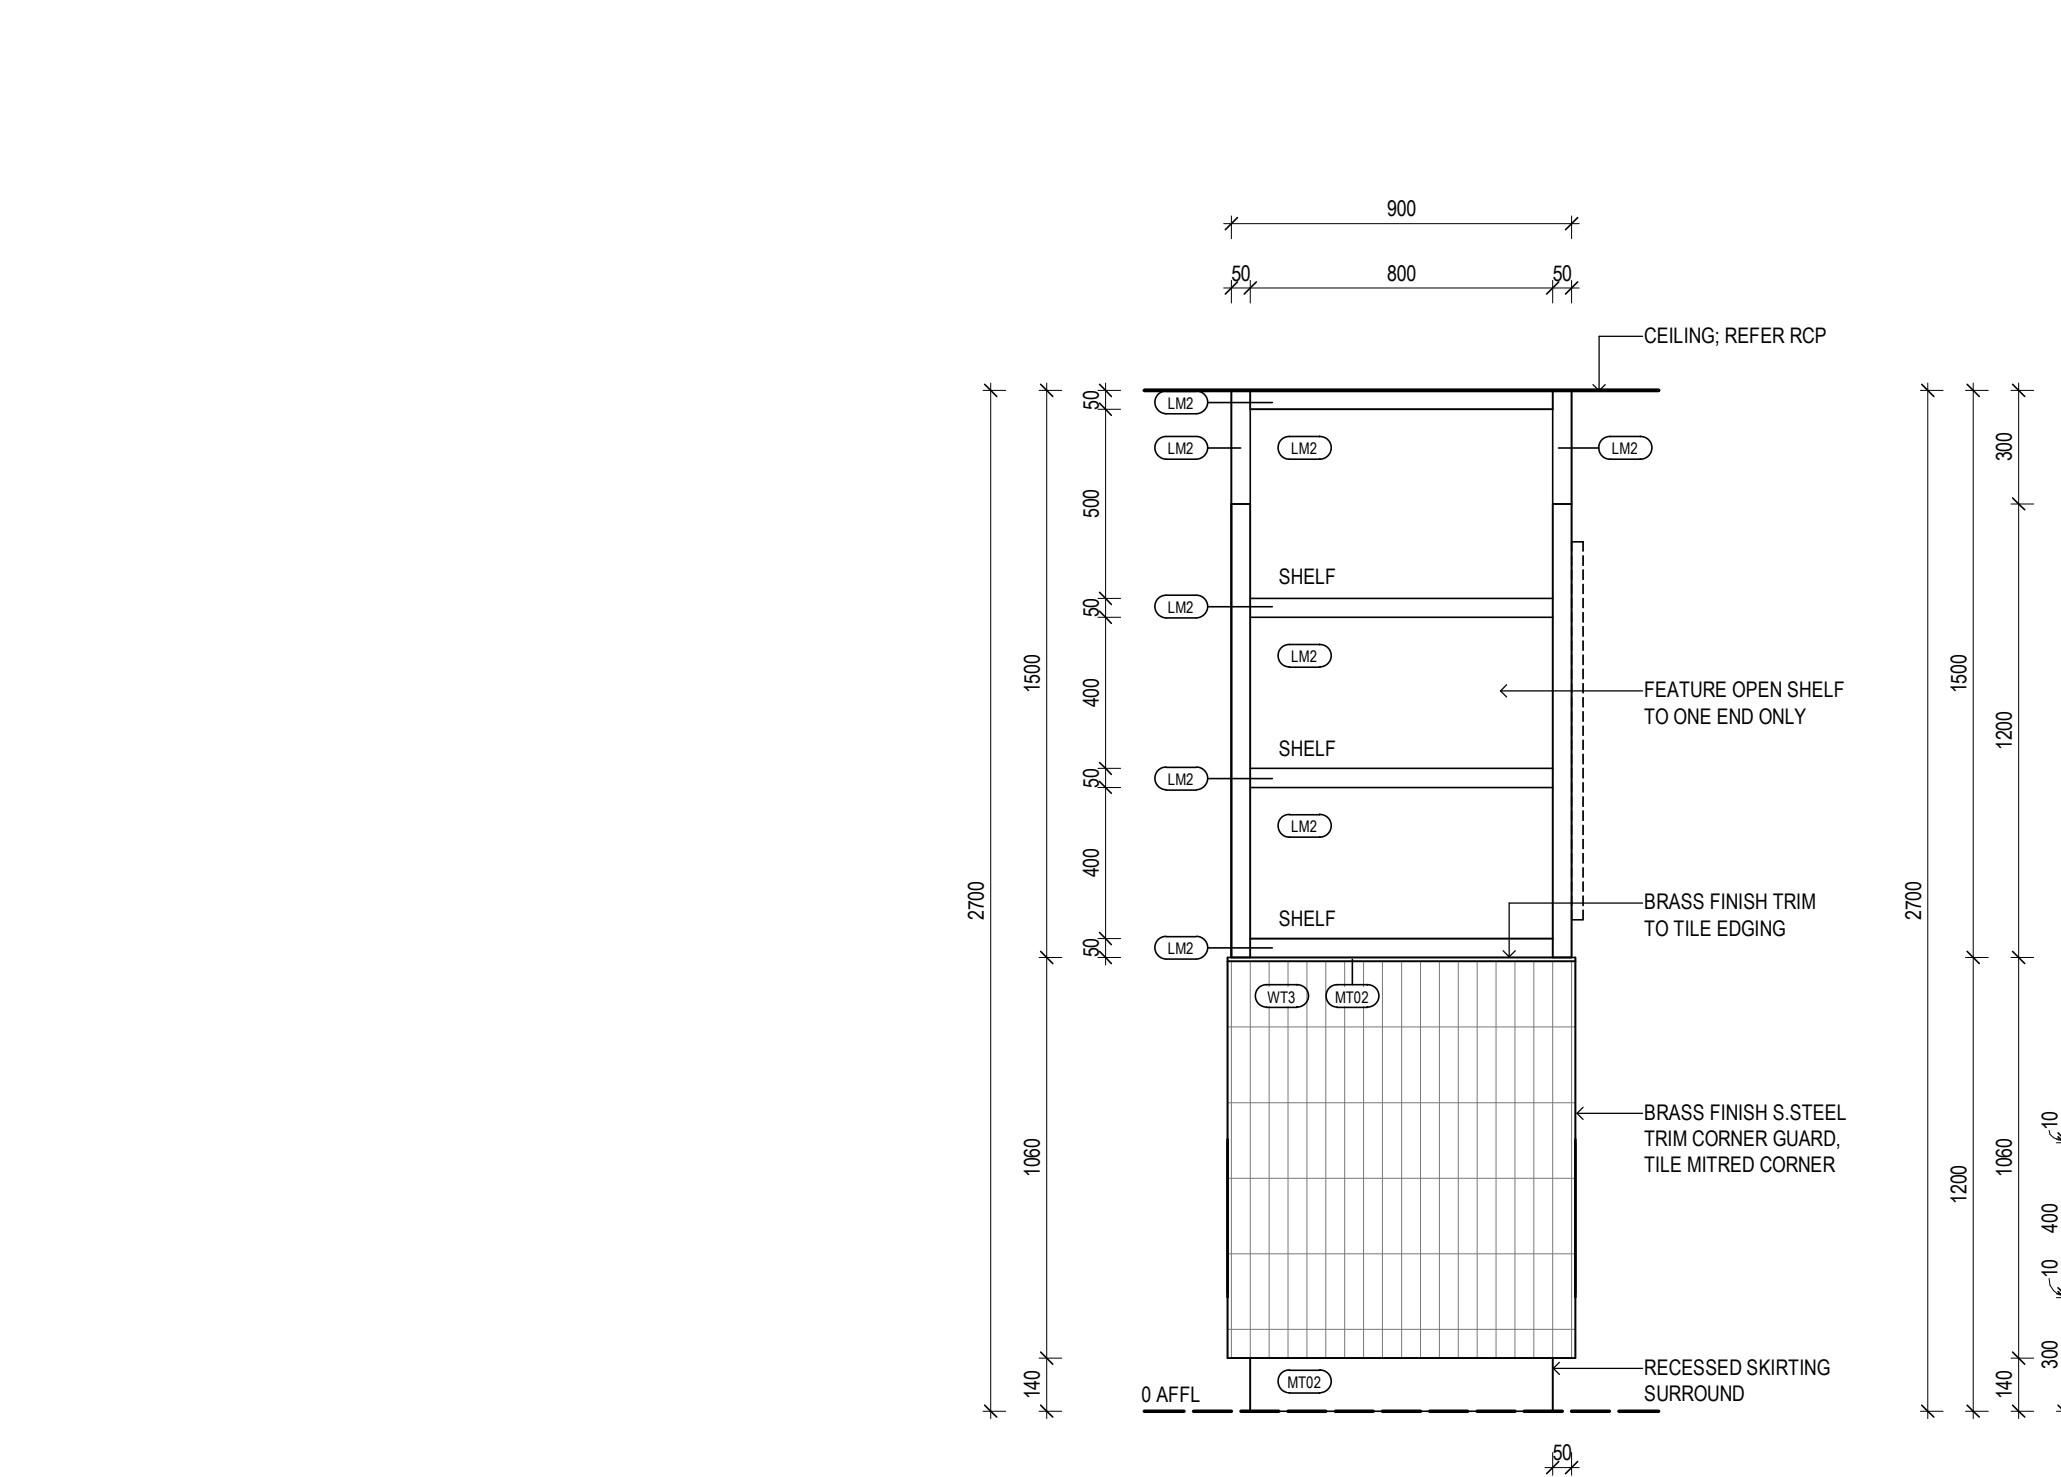

J-04 - Sports Bar Joinery
ELEVATION 3
Scale 1 : 20

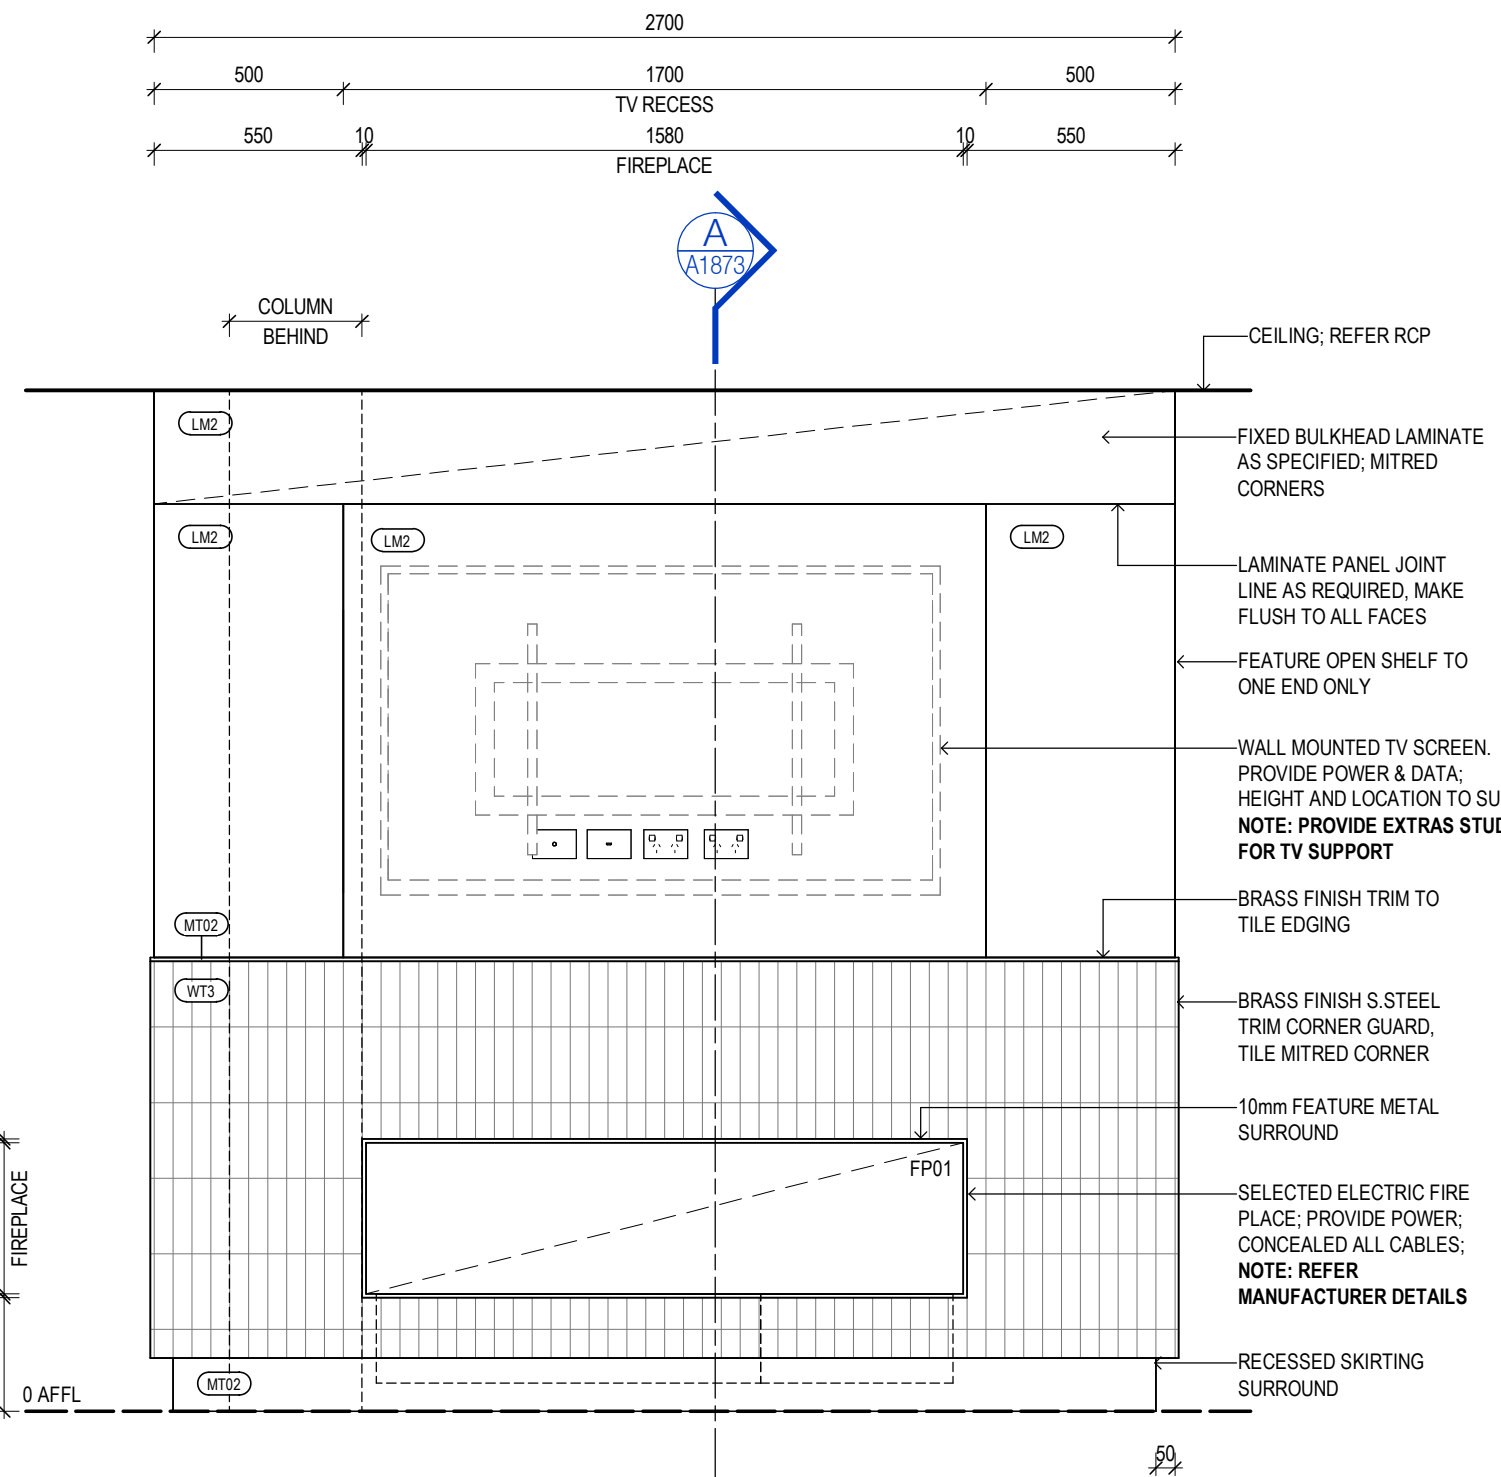

J-04 - Sports Bar Joinery - Lounge Side
ELEVATION 4
Scale 1 : 20

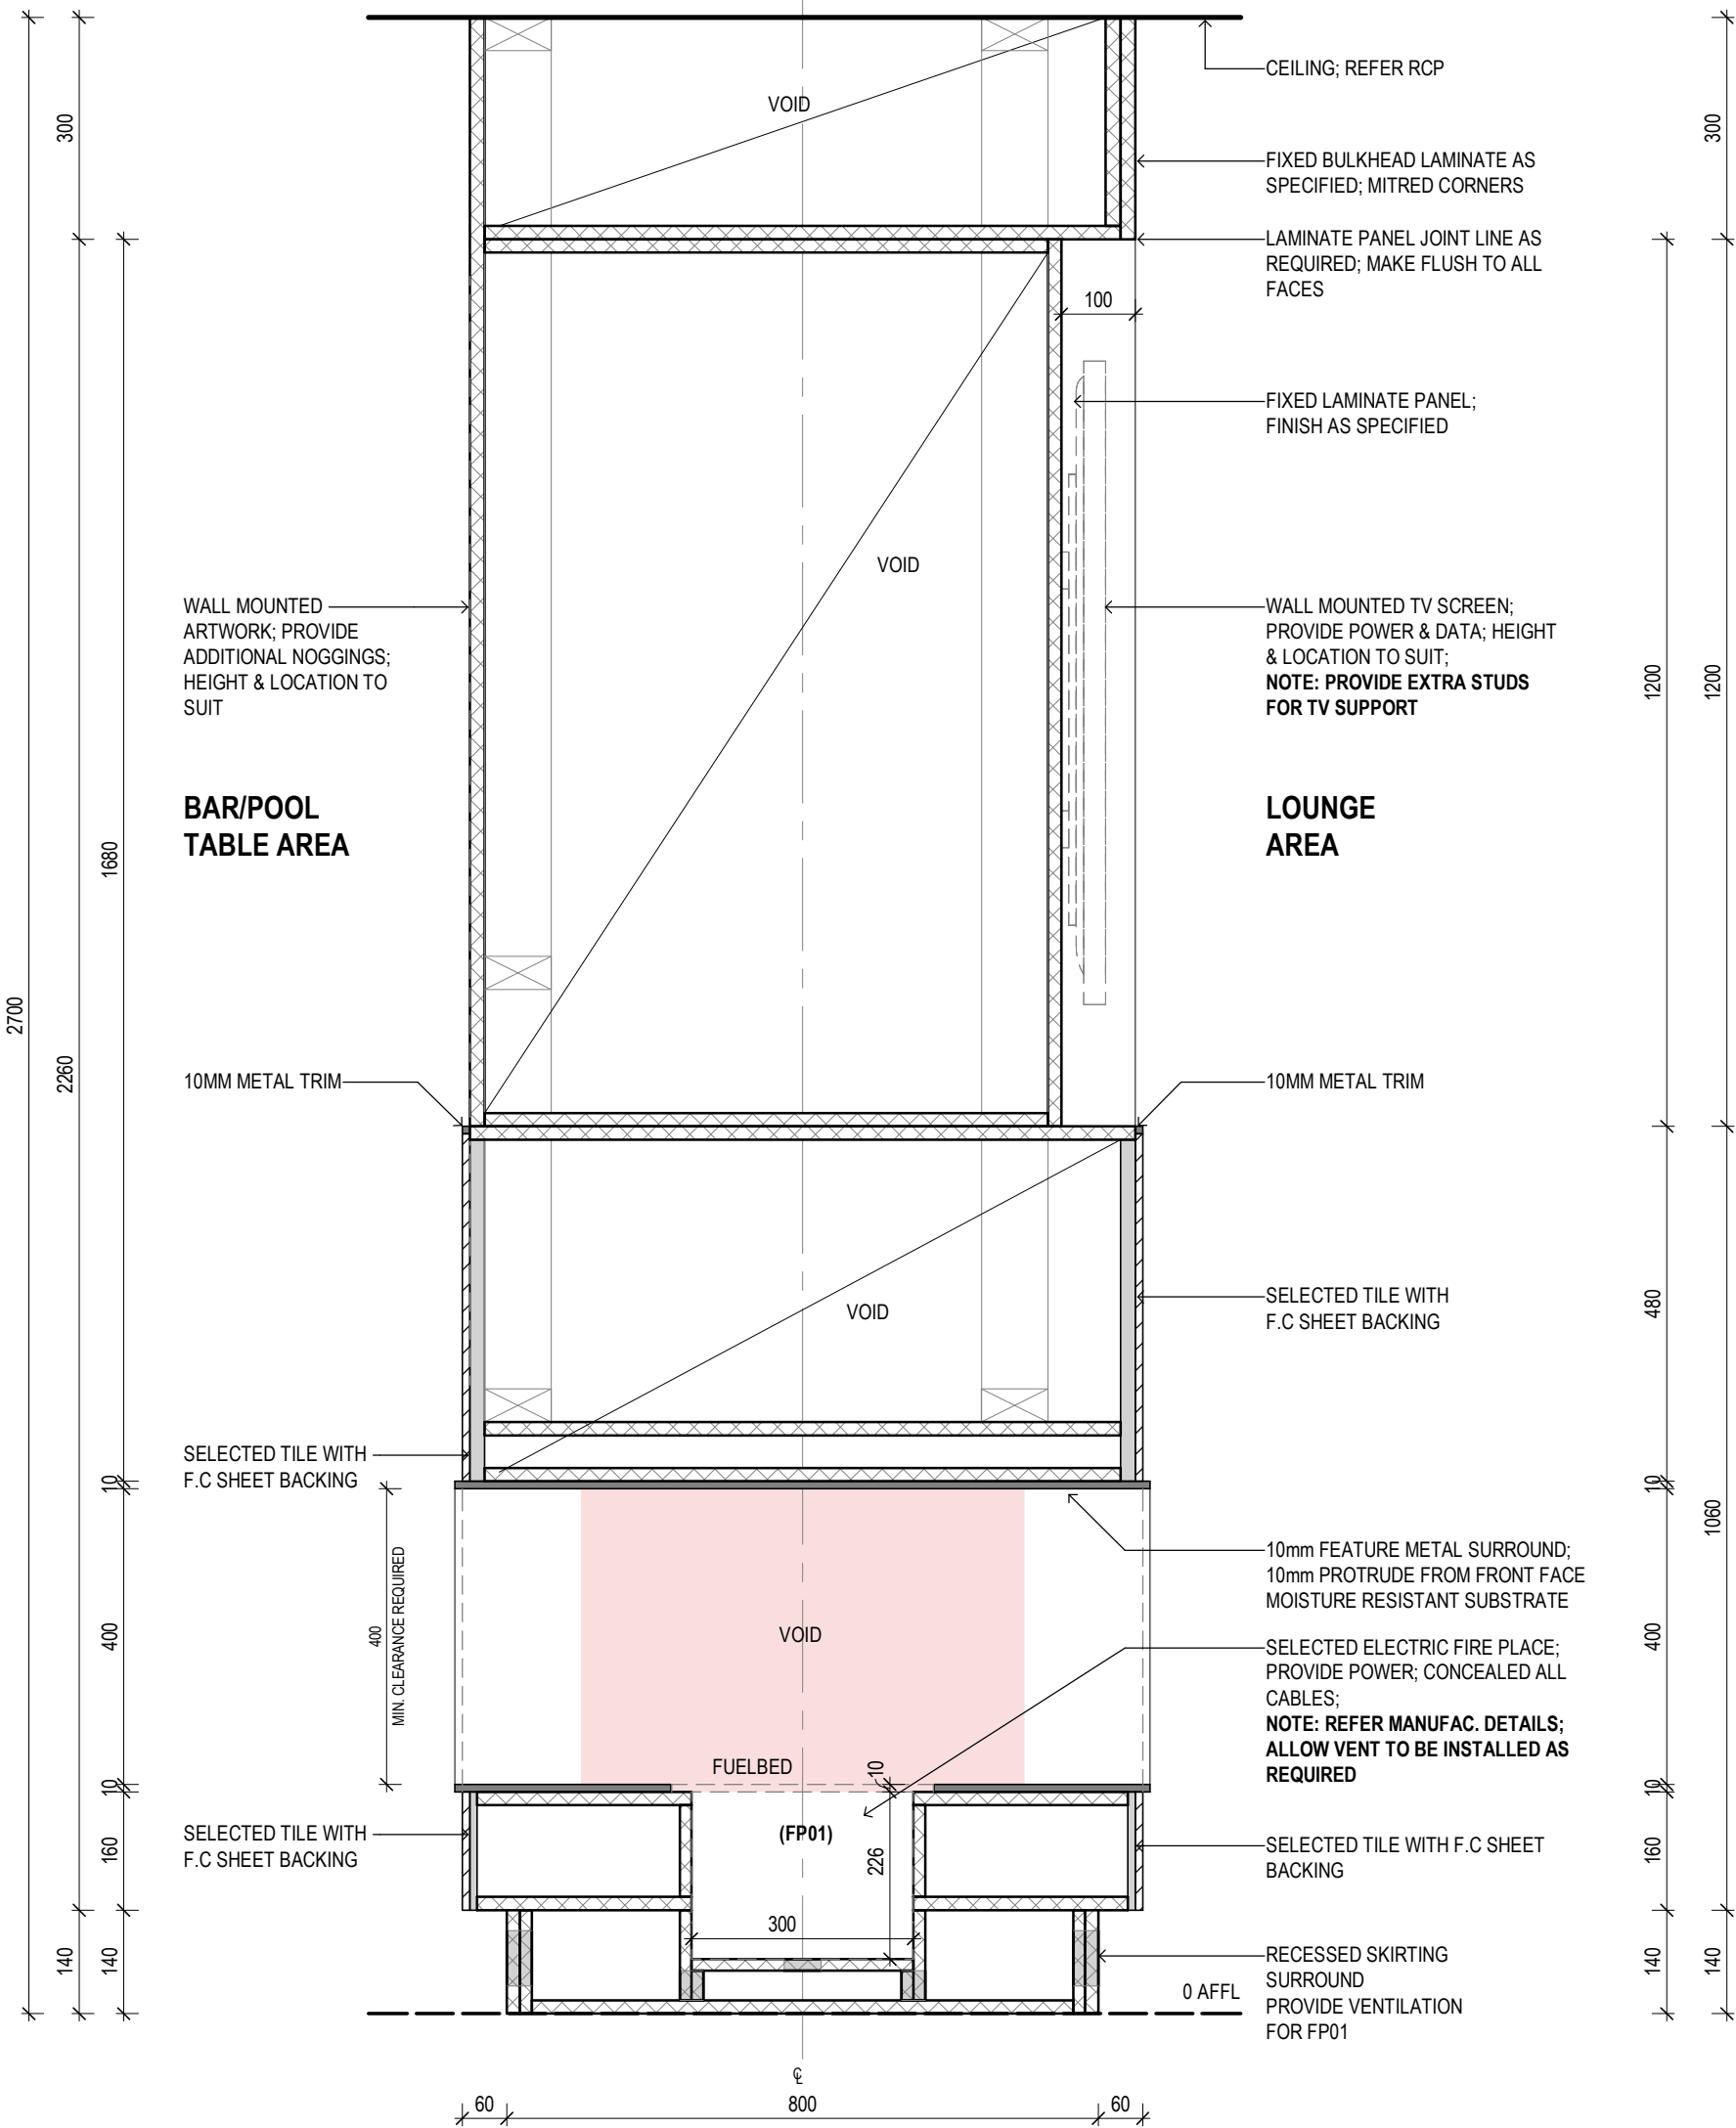

A J-04 - SPORTS BAR JOINERY SECTION A
Scale 1 : 10

Revision/Issue	Date
P1 Preliminary Issue	2025.09.01
P2 ISSUE FOR CONTRACT	2025.10.10
C1 ISSUE FOR CONSTRUCTION - INTERIORS	2026.03.26
C2 ISSUE FOR CONSTRUCTION - INTERIORS	2026.03.30

Clarke
Hopkins
Clarke

Melbourne | Wurundjeri
L3, Melbourne Connect
700 Swanston Street
Carlton VIC 3063
Telephone (03) 9419 4340
Email studio@chc.com.au
www.chc.com.au

Sydney | Gadigal Country
Suite 3, Ground Floor
91 Campbell Street
Surry Hills NSW 2010
Telephone (02) 9221 9200
Email studio@chc.com.au
www.chc.com.au

Scale	As indicated @ A1
Date	01/03/2024
Drawn	TM
Architect	EL

Project
Summerset Oakleigh
52 Golf Road, Oakleigh South, VIC

Drawing
Special Joinery Details - Sheet 4 - Sports
Bar Joinery

Drawing No.

230185/A1873

C2

FOR CONSTRUCTION