




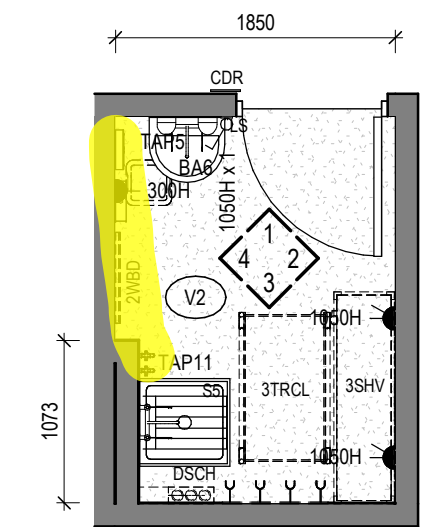


1 RACF-CLEANER - TYPE 1
Scale 1: 50

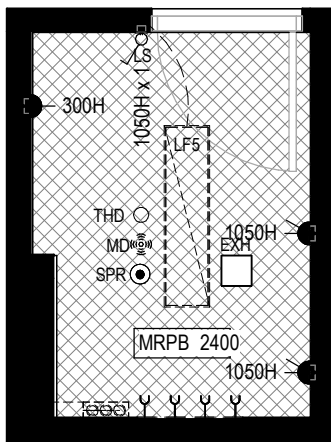


2 RCP-CLEANER - TYPE 1
Scale 1: 50

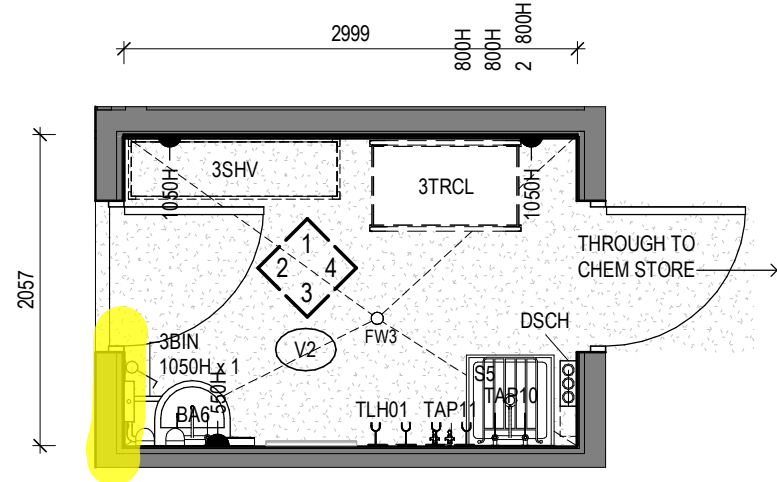


3 RACF-CLEANER - TYPE 2
Scale 1: 50

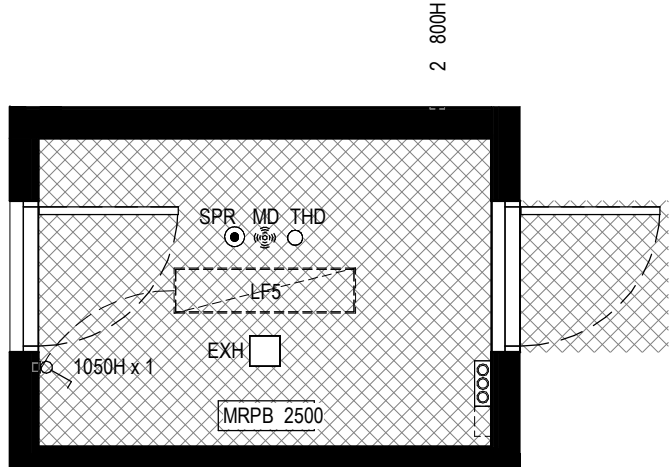


4 RCP-CLEANER - TYPE 2
Scale 1: 50

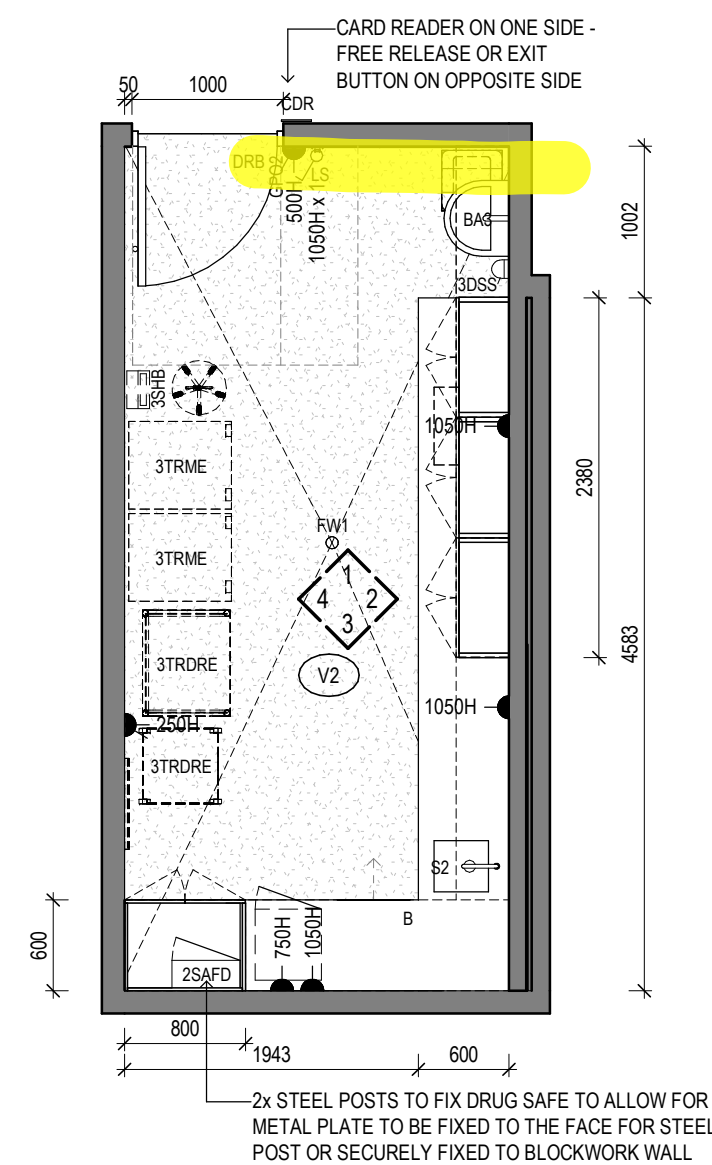


5 RACF-TREATMENT
Scale 1: 50

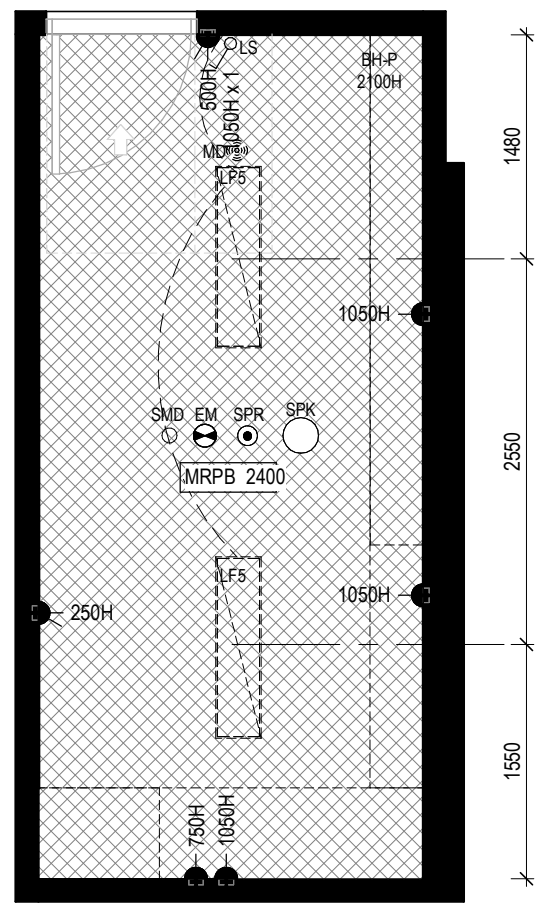


6 RCP-TREATMENT
Scale 1: 50

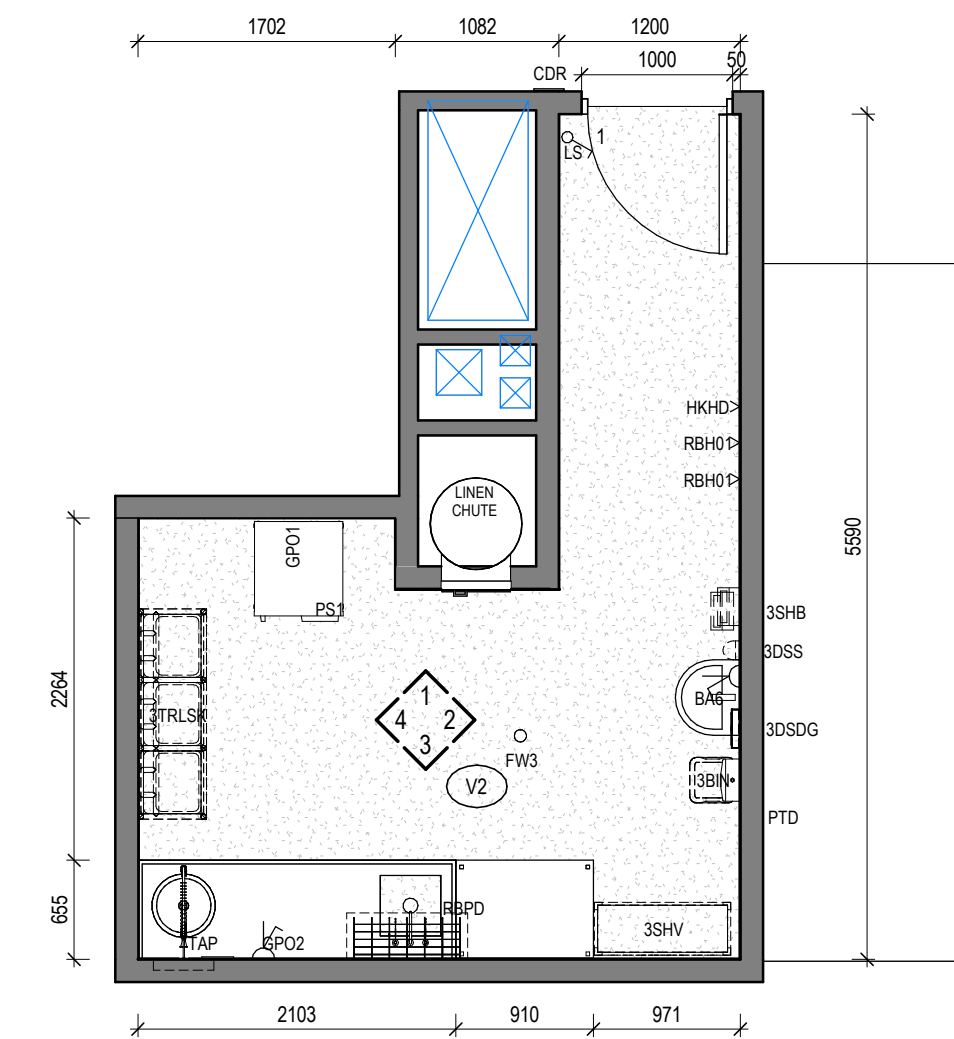


7 RACF-SLUICE
Scale 1: 50

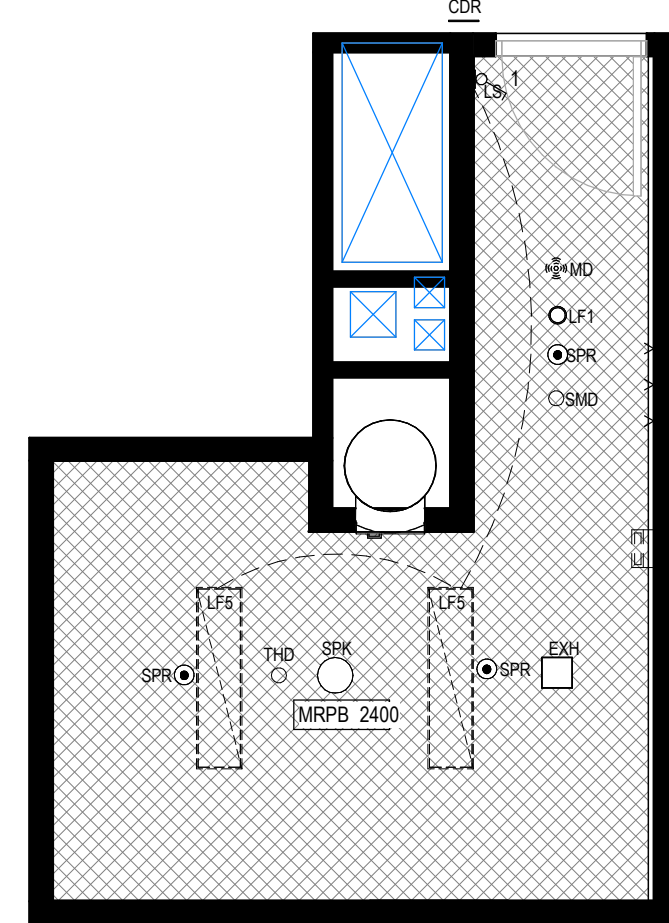


8 RCP-SLUICE
Scale 1: 50

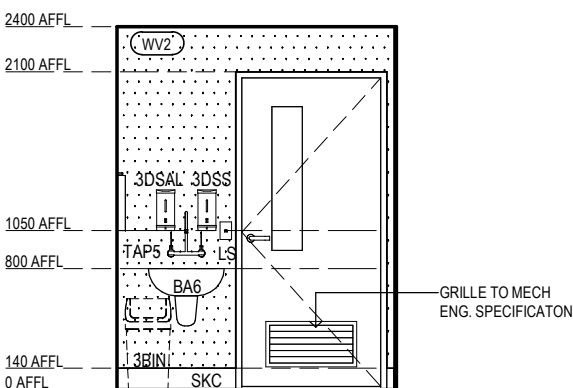


RACF BOH - CLEANER - TYPE 1
ELEVATION 1
Scale 1: 50

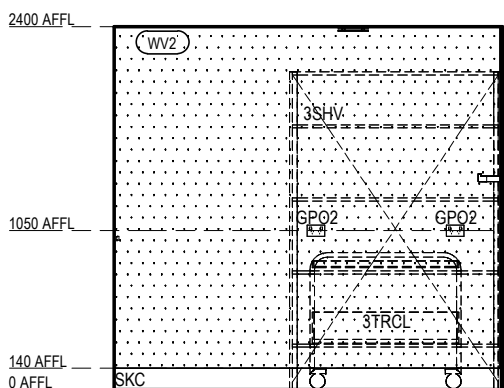


RACF BOH - CLEANER - TYPE 1
ELEVATION 2
Scale 1: 50

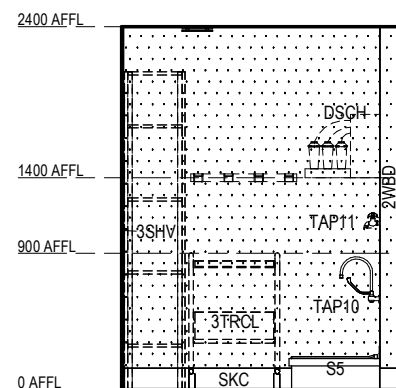


RACF BOH - CLEANER - TYPE 1
ELEVATION 3
Scale 1: 50

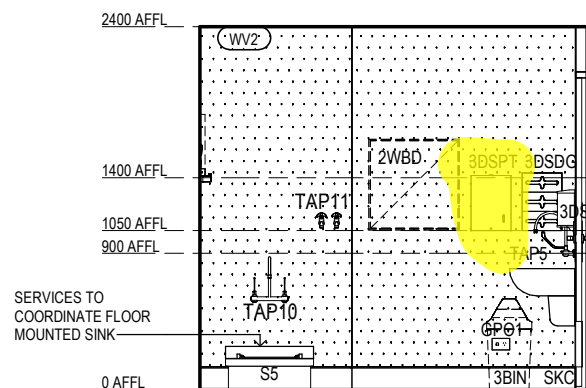


RACF BOH - CLEANER - TYPE 1
ELEVATION 4
Scale 1: 50

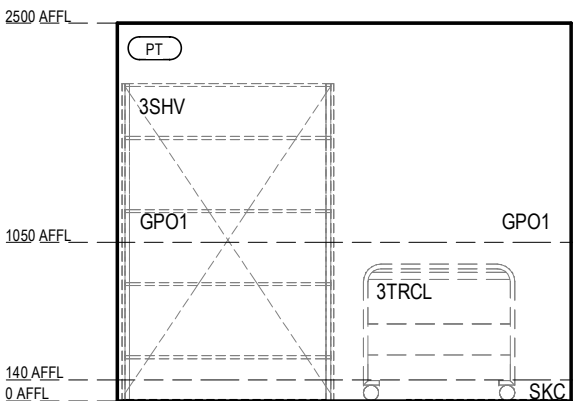


RACF BOH - CLEANER - TYPE 2
ELEVATION 1
Scale 1: 50

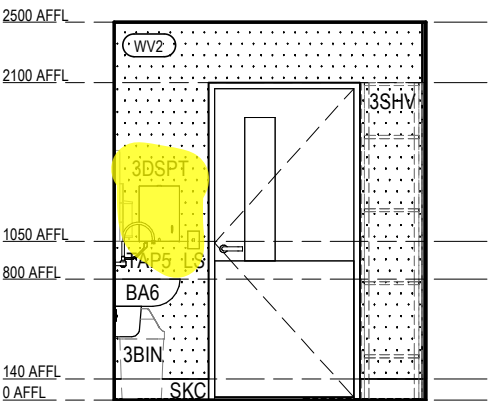


RACF BOH - CLEANER - TYPE 2
ELEVATION 2
Scale 1: 50

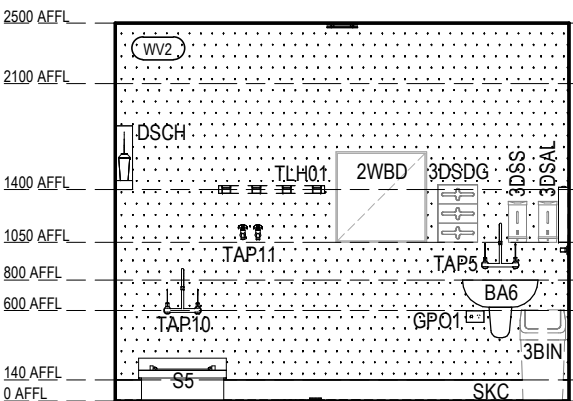


RACF BOH - CLEANER - TYPE 2
ELEVATION 3
Scale 1: 50

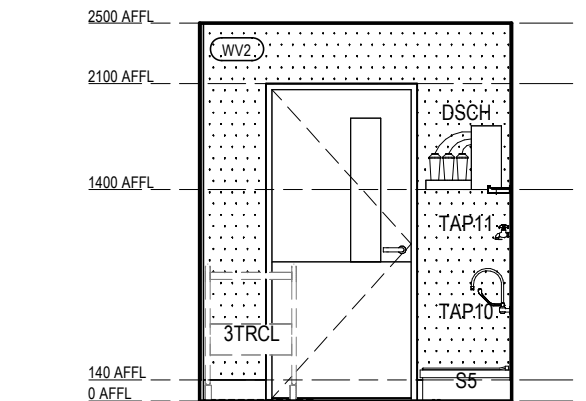


RACF BOH - CLEANER - TYPE 2
ELEVATION 4
Scale 1: 50

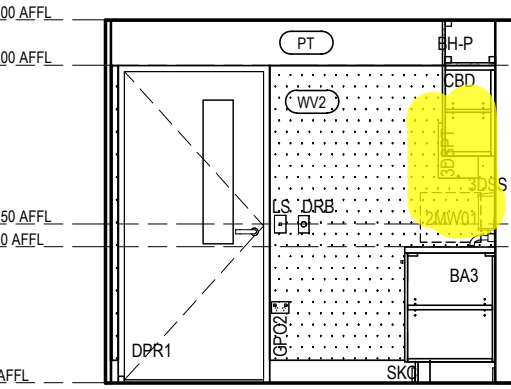


RACF BOH - TREATMENT
ELEVATION 1
Scale 1: 50

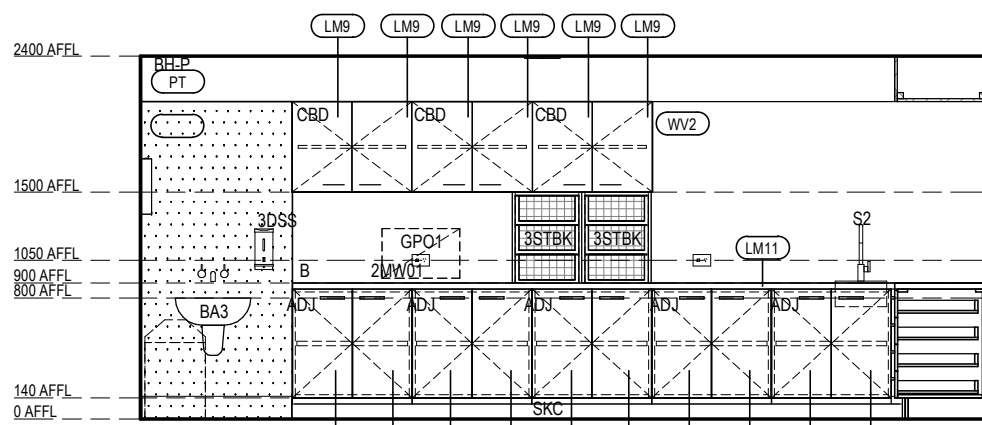


RACF BOH - TREATMENT
ELEVATION 2
Scale 1: 50

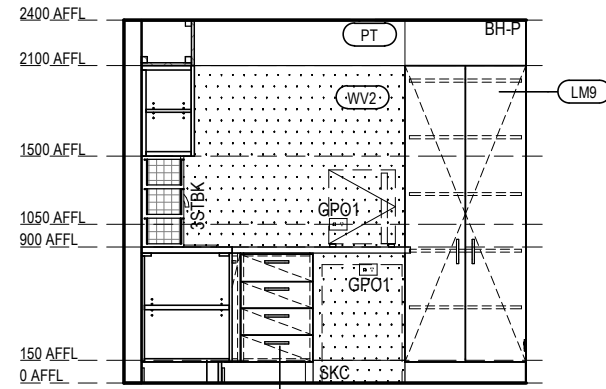


RACF BOH - TREATMENT
ELEVATION 3
Scale 1: 50

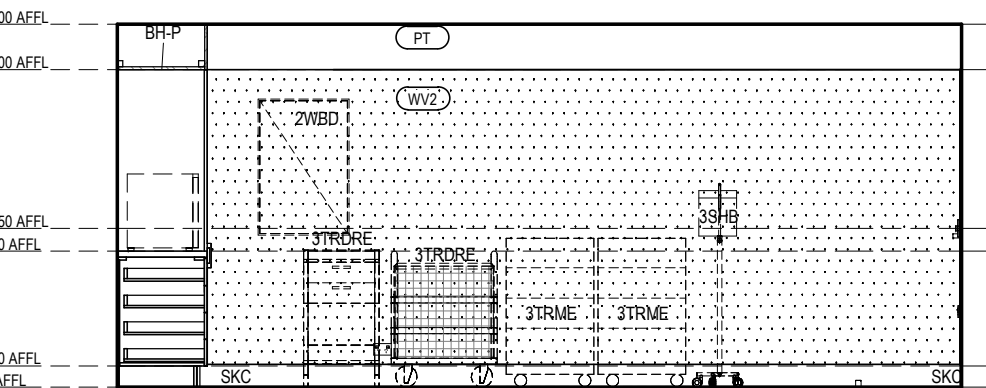


RACF BOH - TREATMENT
ELEVATION 4
Scale 1: 50

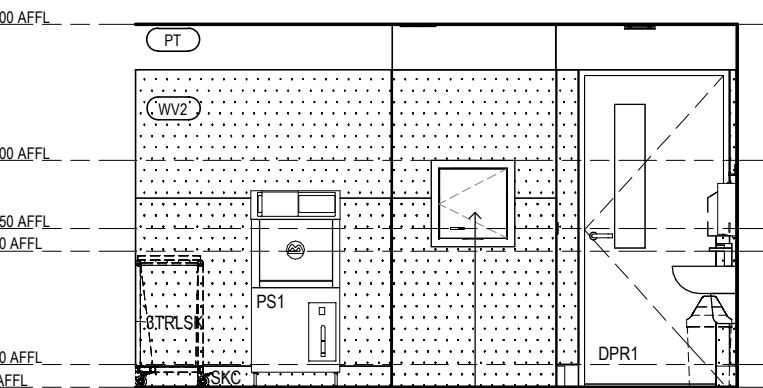


RACF BOH - SLUICE
ELEVATION 1
Scale 1: 50

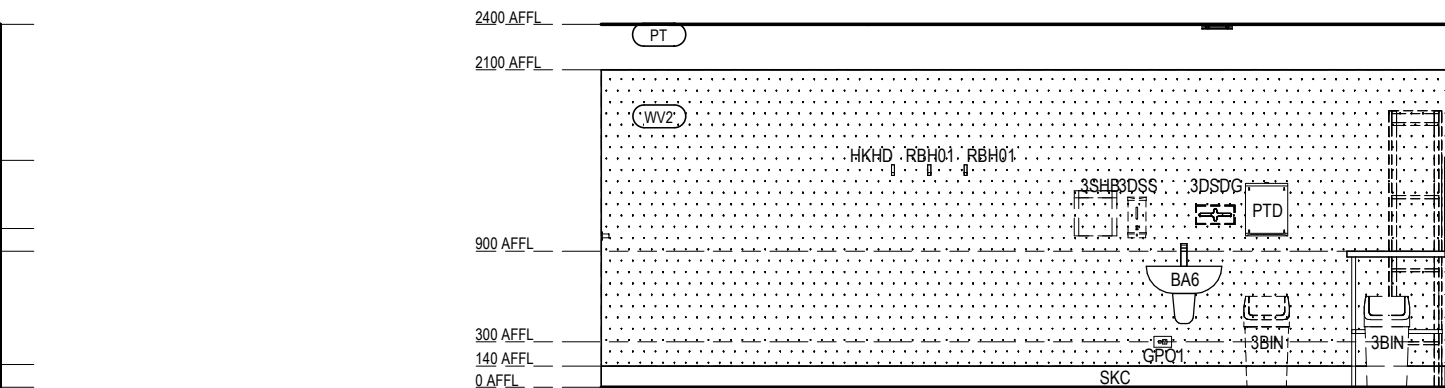

RACF BOH - SLUICE
ELEVATION 2
Scale 1: 50

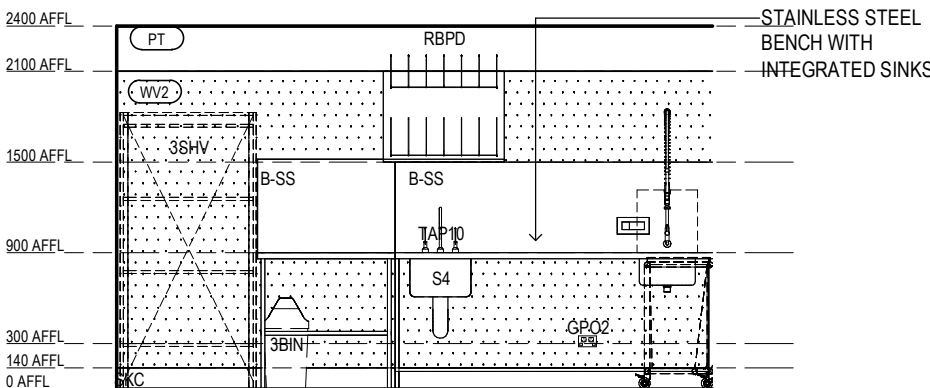

RACF BOH - SLUICE
ELEVATION 3
Scale 1: 50

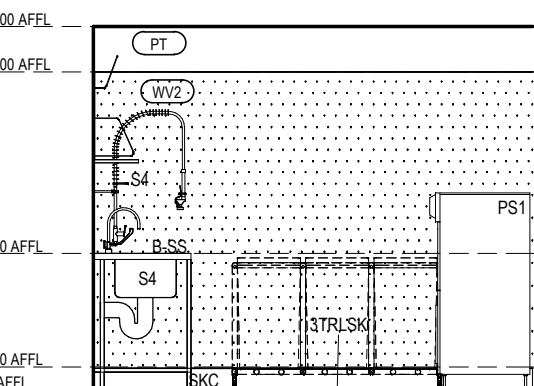

RACF BOH - SLUICE
ELEVATION 4
Scale 1: 50

Legend - Internal Elevations

DRAWINGS TO BE READ IN CONJUNCTION WITH ARCHITECTURAL SPECIFICATION & MATERIALS, PRODUCTS & FINISHES SCHEDULE.

PT# PAINT FINISH TO ALL WALLS WITHIN NEW & AFFECTED ROOMS/ AREAS UNLESS OTHERWISE SHOWN

- CSE CONCRETE SEALER
- DPR DOOR PROTECTION
- GD GRAPHIC FILM
- LM LAMINATE
- MI MIRROR
- PBD PINBOARD
- PT PAINT FINISH
- REN RENDER FINISH
- SB SPLASHBACK
- ST STONE
- WB WHITEBOARD
- WP WALL PROTECTION
- WT WALL TILE
- VV WALL VINYL
- UPH UPHOLSTERY

NOTES:
1. LAMINATE CARCASS FOR ALL VISIBLE OPEN SHELVING, UNLESS OTHERWISE NOTED
2. MELAMINE TO ALL INTERNAL CARCASS OF JOINERY, UNLESS OTHERWISE NOTED.

--- PROVIDE NOGGINGS FOR FUTURE USE

Legend - Floor Finishes

- C CARPET
- CO CONCRETE
- E EPOXY FINISH
- L LINOLEUM
- M MATTING
- PU PAVING UNIT - TBC WITH LANDSCAPE
- R RUBBER FLOORING
- T TILING
- TF TIMBER FLOORING
- V VINYL
- LVT LUXURY VINYL TILE PLANK

Keynote Legend

- 2MW01 MICROWAVE - TYPE 1 - GROUP 2
- 2SAFD DRUG SAFE - TYPE 1 - GROUP 2
- 2WBD WHITEBOARD - GROUP 2
- 3BIN WASTE BIN - GROUP 3
- 3DSAL ALCOHOL HAND RUB DISPENSER - GROUP 3
- 3DSDG GLYCE DISPENSER - GROUP 3
- 3DSPT DISPENSER - PAPER TOWEL - GROUP 3
- 3JSS SOAP DISPENSER - GROUP 3
- 3SHB BIN SHARPS - GROUP 3
- 3SHV SHELVING - GROUP 3
- 3STBK STORAGE BASKET - GROUP 3
- 3TRCL TROLLEY CLEANERS - GROUP 3
- 3TRDRE TROLLEY DRESSING - GROUP 3
- 3TRLSK TROLLEY LINEN SKIP - GROUP 3
- 3TRME TROLLEY MEDICATION - GROUP 3
- ADJ ADJUSTABLE SHELF
- B BENCH - STANDARD
- B-SS BENCH - STAINLESS STEEL
- BA3 BASIN - TYPE 3
- BA6 BASIN - TYPE 6
- BH-P BULKHEAD - PLASTERBOARD TYPE
- CBP CURBBOARD
- CDR CARD READER
- DPR1 DOOR PROTECTION - TYPE 1
- DRB DOOR RELEASE BUTTON
- DSCH DISPENSER - CHEMICAL MIXER
- EM EMERGENCY LIGHT
- EXH EXHAUST
- FW1 FLOOR WASTE - TYPE 1
- FW3 FLOOR WASTE - TYPE 3
- GPO1 POWER OUTLET - SINGLE
- GPO2 POWER OUTLET - DOUBLE
- HKHD HOOK - HEAVY DUTY
- LF1 LIGHT FITTING - REFER TO ELECTRICAL
- ENGINEER SPECIFICATION
- LF5 LIGHT FITTING - TYPE 5
- LS LIGHT SWITCH
- MD MOTION DETECTOR
- PS1 PAN SANITISER
- PTD PAPER TOWEL DISPENSER
- RBH01 ROBE HOOK - TYPE 1
- RPD RACK BEDPAN WITH DRIP TRAY
- S2 SINK - TYPE 2
- S4 SINK - TYPE 4
- S5 SINK - TYPE 5
- SKC SKIRTING - COVED
- SMD SMOKE DETECTOR
- SPK ANNUNCIATOR SPEAKER
- SPR SPRINKLER
- TAP TAP
- TAP5 TAP - TYPE 5
- TAP10 TAP - TYPE 10
- TAP11 TAP - TYPE 11
- THD THERMAL DETECTOR
- TLH01 TOOL HOLDER - WALL MOUNTED

FOR CONSTRUCTION

Drawing No.

230185/A1820

C1

Revision/Issue	Date
P1 Preliminary Internal Elevations - RACF	2025.08.08
P2 Consolidated Set-to-date / SMG Comments	2025.08.15
P3 ISSUE FOR CONTRACT	2025.10.10
C1 ISSUE FOR CONSTRUCTION - INTERIORS	2026.03.30

Clarke Hopkins
architects

ClarkeHopkinsClarke
Melbourne | Wurundjeri
L3, Melbourne Connect
700 Swanston Street
Carlton VIC 3063
Telephone (03) 9419 4340
Email studio@chc.com.au
www.chc.com.au

Sydney | Gadigal Country
Suite 3, Ground Floor
91 Campbell Street
Surry Hills NSW 2010
Telephone (02) 9221 9200
Email studio@chc.com.au
www.chc.com.au

Scale	As indicated @ A1
Date	01/03/2024
Drawn	RM
Architect	EL

Project
Summerset Oakleigh
52 Golf Road, Oakleigh South, VIC

Drawing
Internal Elevations - RACF BOH - Clean,
Treatment & Sluice