

Legend - Internal Elevations

DRAWINGS TO BE READ IN CONJUNCTION WITH ARCHITECTURAL SPECIFICATION & MATERIALS, PRODUCTS & FINISHES SCHEDULE.

PT# PAINT FINISH TO ALL WALLS WITHIN NEW & AFFECTED ROOMS/ AREAS UNLESS OTHERWISE SHOWN

- CSE CONCRETE SEALER
- DPR DOOR PROTECTION
- GD GRAPHIC FILM
- LM LAMINATE
- MI MIRROR
- PBD PINBOARD
- PT PAINT FINISH
- REN RENDER FINISH
- SB SPLASHBACK
- ST STONE
- WB WHITEBOARD
- WP WALL PROTECTION
- WT WALL TILE
- WV WALL VINYL

NOTES:
1. LAMINATE CARCASS FOR ALL VISIBLE OPEN SHELVING, UNLESS OTHERWISE NOTED
2. MELAMINETO ALL INTERNAL CARCASS OF JOINERY, UNLESS OTHERWISE NOTED.

Legend - Floor Finishes

- C CARPET
- CO CONCRETE
- E EPOXY FINISH
- L LINOLEUM
- M MATTING
- FU PAVING UNIT - TBC WITH LANDSCAPE
- R RUBBER FLOORING
- T TILING
- TF TIMBER FLOORING
- V VINYL
- LVT LUXURY VINYL TILE PLANK

PROTECTION RAILS OR CRASH RAILS - REFER TO MATERIAL SCHEDULE FOR DETAILS








WL1- REFER TO MATERIAL SCHEDULE FOR DETAILS

WL2 - REFER TO MATERIAL SCHEDULE FOR DETAILS

NOTE:
FALLS TO ALL FLOOR WASTES IN ACCORDANCE WITH AS 3740.

Keynote Legend

- 2DSDG DISPENSER - DISPOSABLE GLOVE - GROUP 2
- 3DSST DISPENSER - PAPER TOWELS - GROUP 3
- 3DSS SOAP DISPENSER - GROUP 3
- 3TRLN TROLLEY LINEN - GROUP 3
- ADJ ADJUSTABLE SHELF
- BAS BASIN - TYPE 5
- BH-P BULKHEAD - PLASTERBOARD TYPE
- EM EMERGENCY LIGHT
- GPO1 POWER OUTLET - SINGLE
- GPO2 POWER OUTLET - DOUBLE
- LFS LIGHT FITTING - TYPE 5
- MD MOTION DETECTOR
- SKC SKIRTING - COVED
- SMD SMOKE DETECTOR
- SPK ANUNCIATOR
- SPR SPRINKLER
- TAP4 TAP - TYPE 4

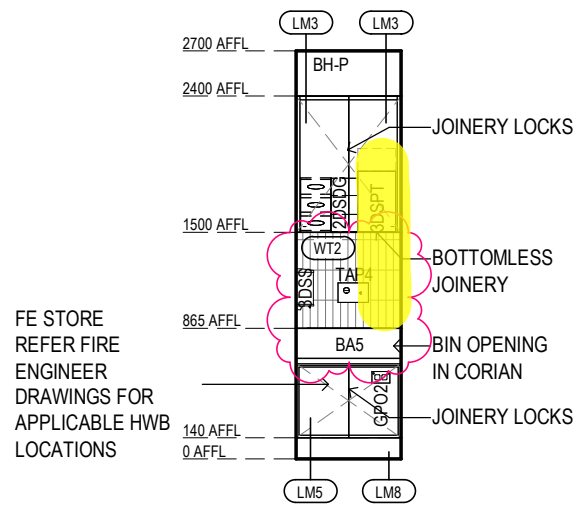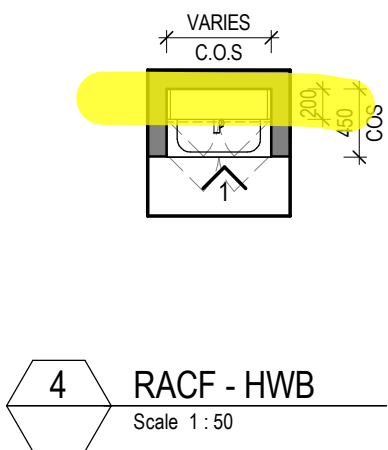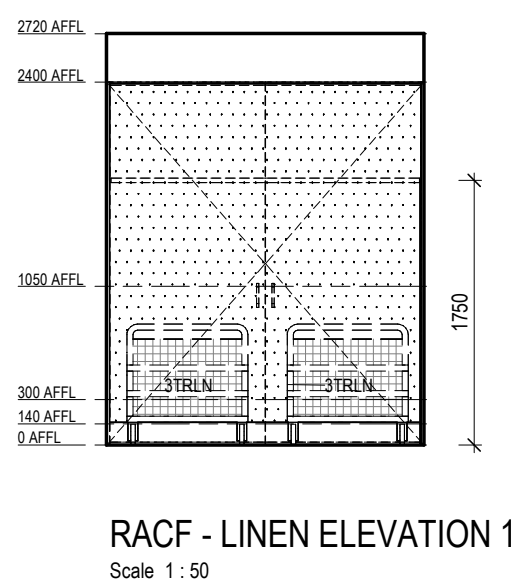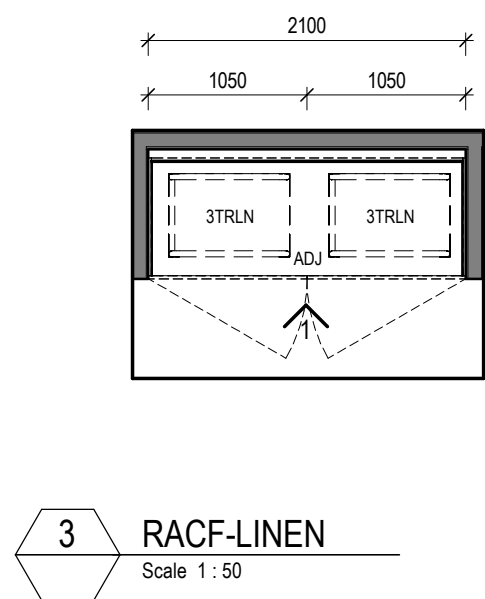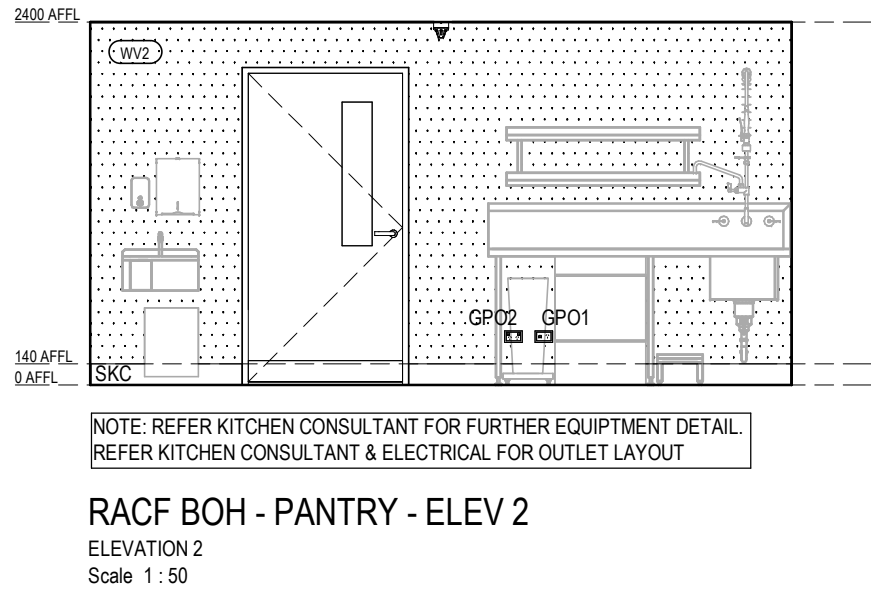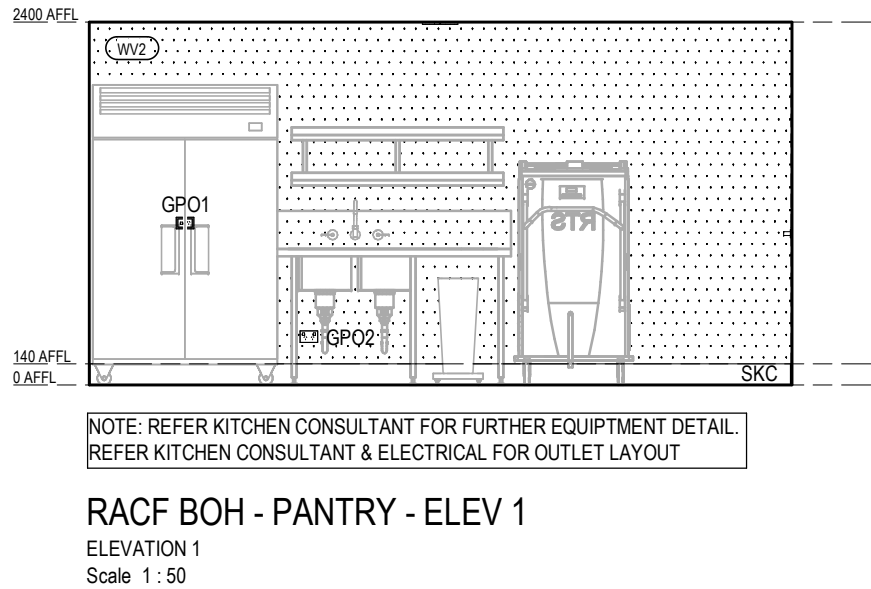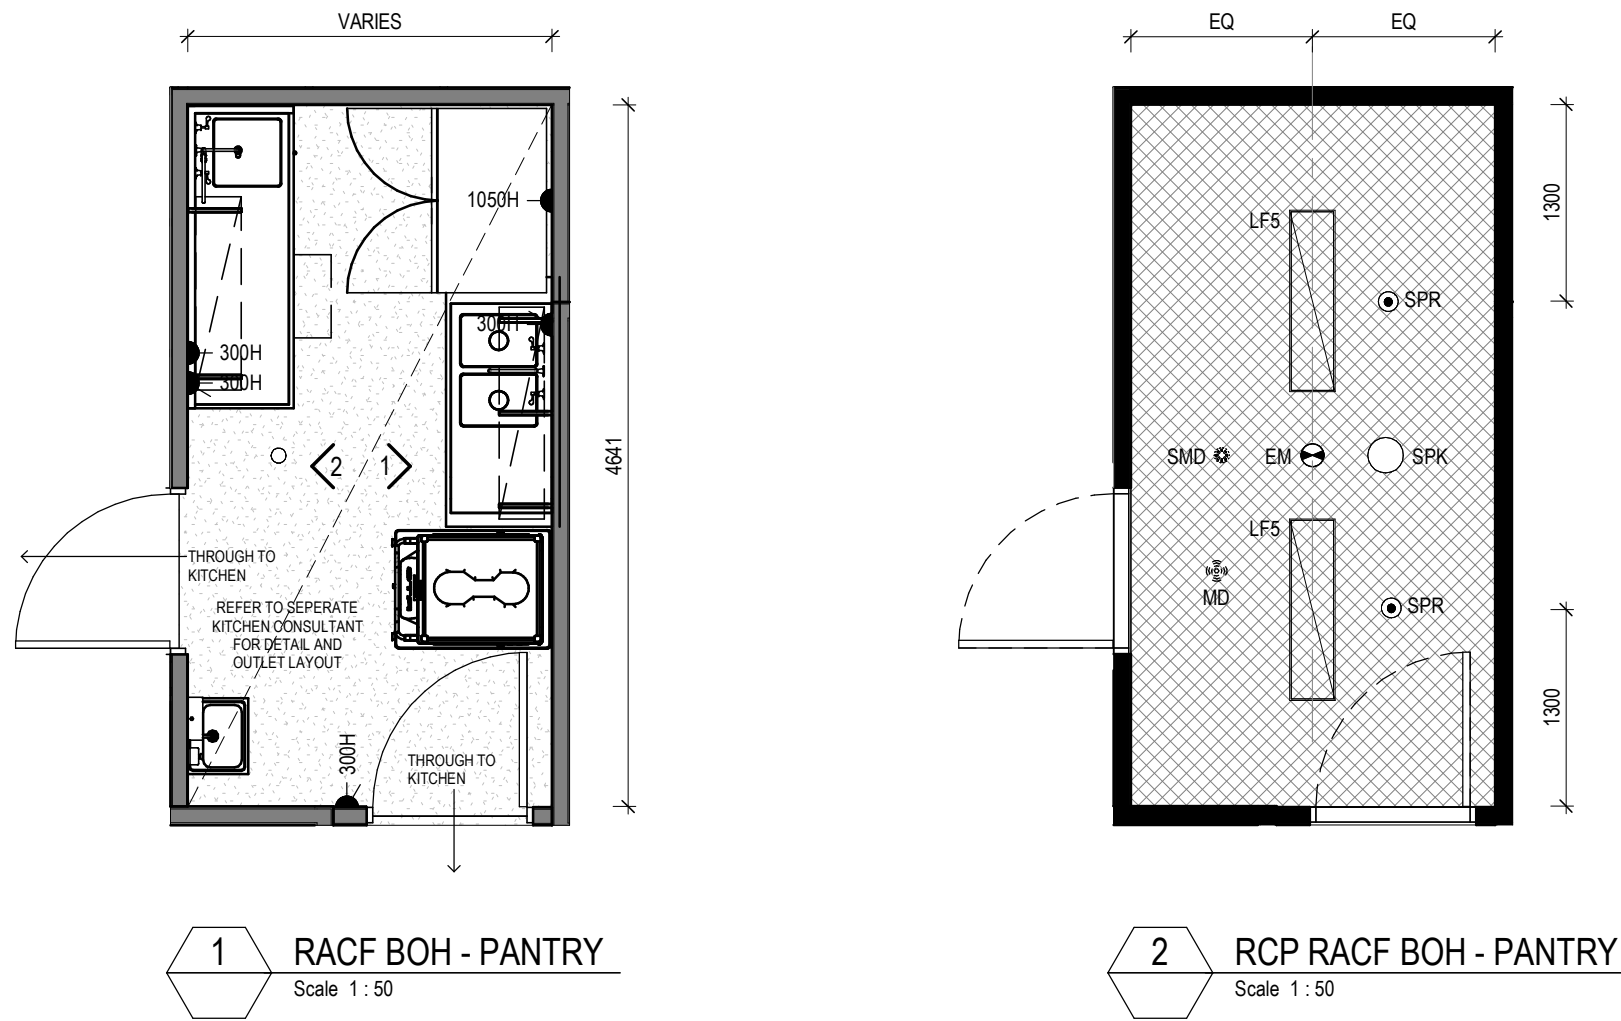

STORE

2100 WALL PROTECTION TO BE PROVIDED TO ALL STORE ROOMS

FOR CONSTRUCTION

Revision/Issue	Date
P1 Preliminary Internal Elevations - RACF	2025.08.08
P2 Consolidated Set-to-date / SMG Comments	2025.08.15
P3 ISSUE FOR CONTRACT	2025.10.10
C1 ISSUE FOR CONSTRUCTION - INTERIORS	2026.03.30

ClarkeHopkinsClarke

Melbourne | Wurundjeri
L3, Melbourne Connect
700 Swanston Street
Carlton VIC 3063
Telephone (03) 9419 4340
Email studio@chc.com.au
www.chc.com.au

Sydney | Gadigal Country
Suite 3, Ground Floor
91 Campbell Street
Surry Hills NSW 2010
Telephone (02) 9221 9200
Email studio@chc.com.au
www.chc.com.au

Scale	As indicated @ A1
Date	01/03/2024
Drawn	TM
Architect	EL

Project
Summerset Oakleigh
52 Golf Road, Oakleigh South, VIC

Drawing
Internal Elevations - RACF BOH - Pantry,
ACC W/C, Linen & HWB

Drawing No.
230185/A1821
C1