

Legend - Internal Elevations

DRAWINGS TO BE READ IN CONJUNCTION WITH ARCHITECTURAL SPECIFICATION & MATERIALS, PRODUCTS & FINISHES SCHEDULE.

PT# PAINT FINISH TO ALL WALLS WITHIN NEW & AFFECTED ROOMS/ AREAS UNLESS OTHERWISE SHOWN

- CSE CONCRETE SEALER
- DPR DOOR PROTECTION
- GD GRAPHIC FILM
- LM LAMINATE
- MI MIRROR
- PBD PINBOARD
- PT PAINT FINISH
- REN RENDER FINISH
- SB SPLASHBACK
- ST STONE
- WB WHITEBOARD
- WP WALL PROTECTION
- WT WALL TILE
- WV WALL VINYL
- UPH UPHOLSTERY

NOTES:
1. LAMINATE CARCASS FOR ALL VISIBLE OPEN SHELVING, UNLESS OTHERWISE NOTED
2. MELAMINE TO ALL INTERNAL CARCASS OF JOINERY, UNLESS OTHERWISE NOTED.

--- PROVIDE NOGGINGS FOR FUTURE USE

Legend - Floor Finishes

- C CARPET
- CO CONCRETE
- E EPOXY FINISH
- L LINOLEUM
- M MATTING
- PU PAVING UNIT - TBC WITH LANDSCAPE
- R RUBBER FLOORING
- T TILING
- TF TIMBER FLOORING
- V VINYL
- LVT LUXURY VINYL TILE PLANK

--- PROTECTION RAILS OR CRASH RAILS - REFER TO MATERIAL SCHEDULE FOR DETAILS

--- WL1- REFER TO MATERIAL SCHEDULE FOR DETAILS

--- WL2- REFER TO MATERIAL SCHEDULE FOR DETAILS

NOTE:

FALLS TO ALL FLOOR WASTES IN ACCORDANCE WITH AS 3740.

Keynote Legend

- ZDSOG DISPENSER - DISPOSABLE GLOVE - GROUP 2
- ZBN WASTE BIN - GROUP 3
- 3DSPT DISPENSER - PAPER TOWEL - GROUP 3
- 3DSS SOAP DISPENSER - GROUP 3
- AP ACCESS PANEL
- BA2 BASIN - TYPE 2
- DST DOOR STOP
- EXH EXHAUST
- FW1 FLOOR WASTE - TYPE 1
- GP02L POWER OUTLET - DOUBLE - LARGE PLATE
- GR1 GRAB RAIL - TYPE 1
- GR2 GRAB RAIL - TYPE 2
- GR3 GRAB RAIL - TYPE 3
- GR4 GRAB RAIL - TYPE 4
- GR6 GRAB RAIL - TYPE 6
- LF1 LIGHT FITTING - REFER TO ELECTRICAL ENGINEER SPECIFICATION
- LS-L LIGHT SWITCH - LARGE PLATE
- M1 MIRROR - TYPE 1
- MIX MIXER
- NC NURSE CALL
- P2 TOILET PAN TYPE 02
- P3 TOILET PAN TYPE 03
- RBH01 ROBE HOOK - TYPE 1
- SH SHELF
- SHW1 SHOWER - TYPE 1
- SMD SMOKE DETECTOR
- SPR SPRINKLER
- SR SHOWER ROSE
- TAP1 TAP - TYPE 1
- TAP2 TAP - TYPE 2
- TAP7 TAP - TYPE 7
- TRH1 TOILET ROLL HOLDER - TYPE 1


FOR CONSTRUCTION

Drawing No.


230185/A1840

C3


© ClarkeHopkinsClarke

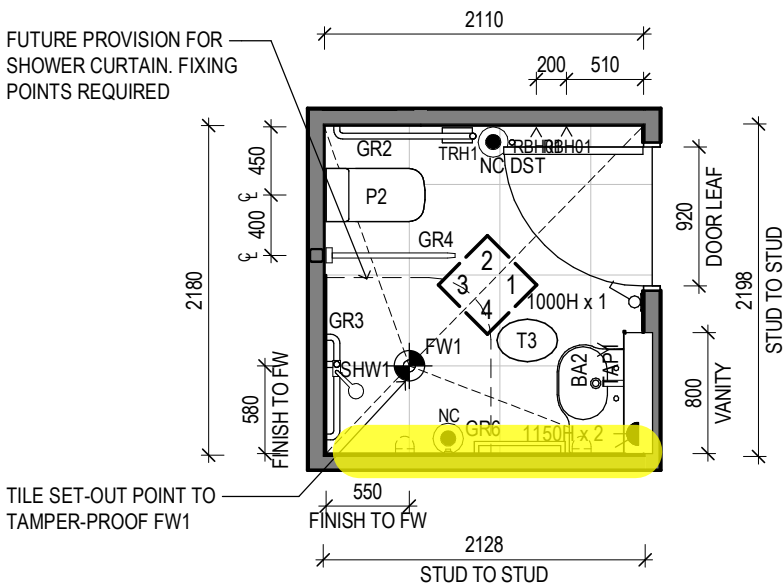


1 RACF STANDARD ENSUITE
Scale 1 : 50

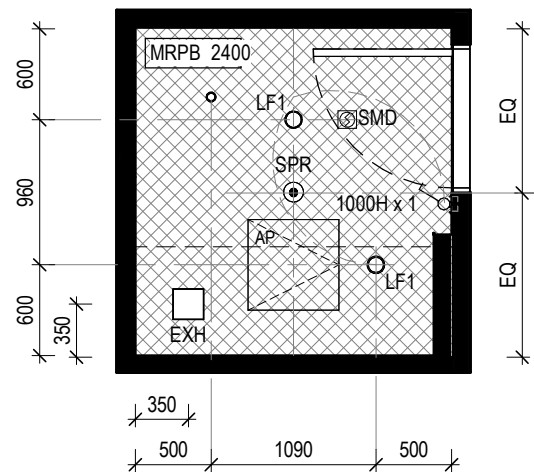


2 RCP-STANDARD ENSUITE
Scale 1 : 50

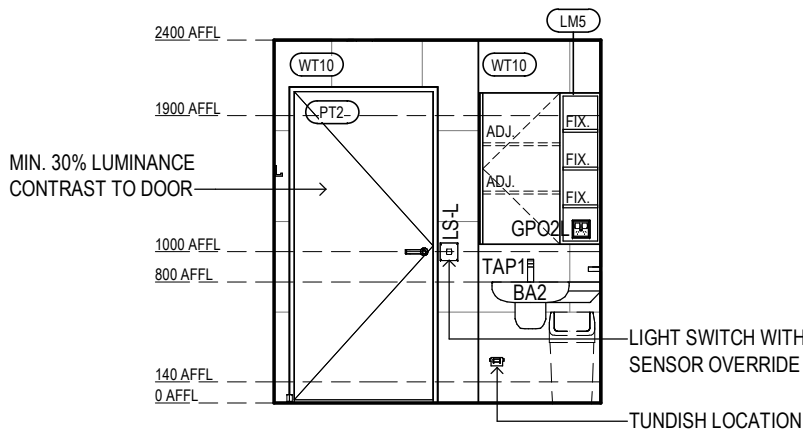


RACF STANDARD ROOM ENSUITE
ELEVATION 1
Scale 1 : 50

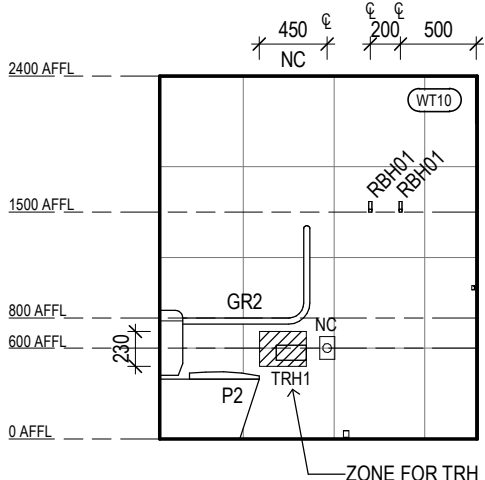


RACF STANDARD ROOM ENSUITE
ELEVATION 2
Scale 1 : 50

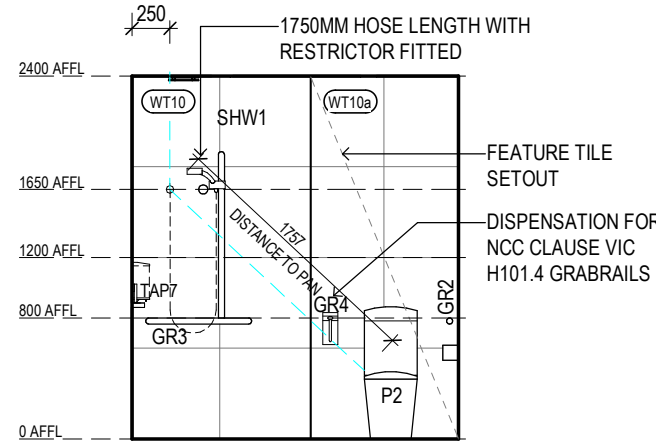


RACF STANDARD ROOM ENSUITE - ELEVATION 3
ELEVATION 3
Scale 1 : 50

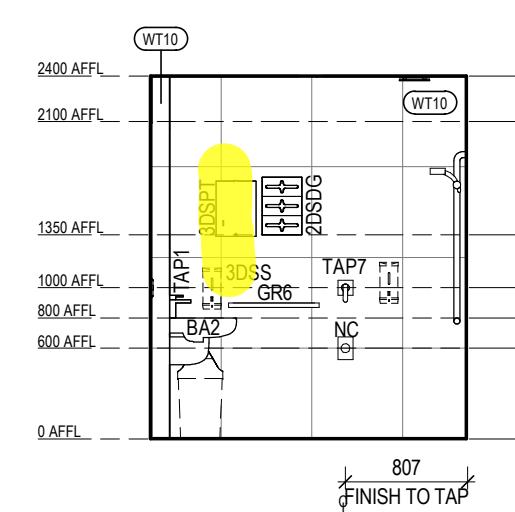


RACF STANDARD ROOM ENSUITE - ELEVATION 4
ELEVATION 4
Scale 1 : 50

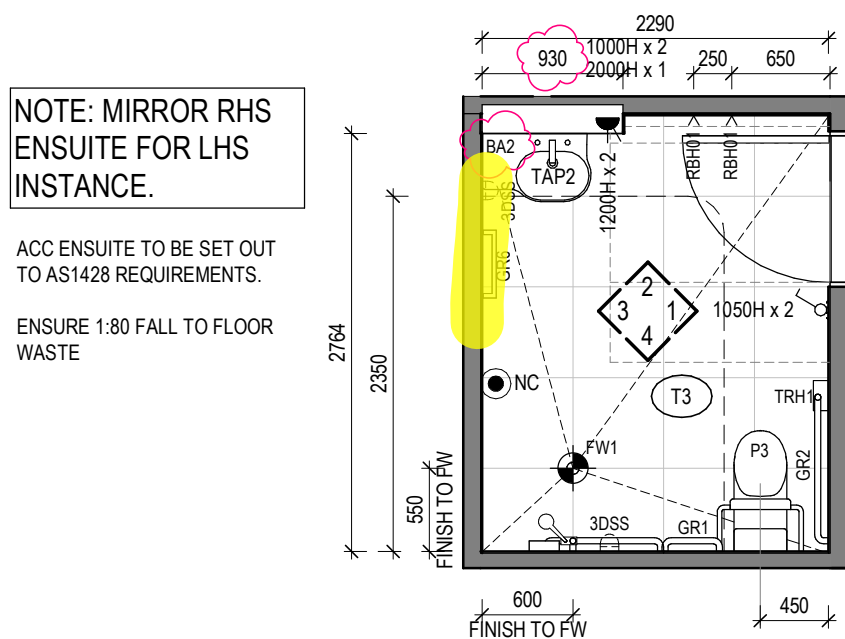


3 RACF ACCESSIBLE ENSUITE RHS
Scale 1 : 50

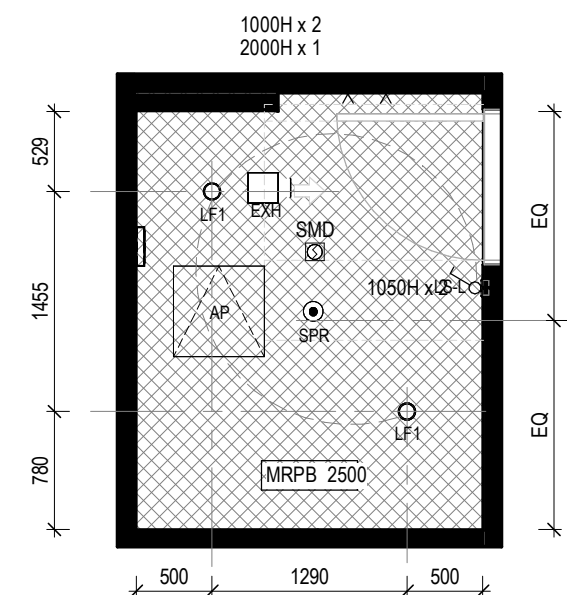


4 RCP - ACCESSIBLE BEDROOM
Scale 1 : 50

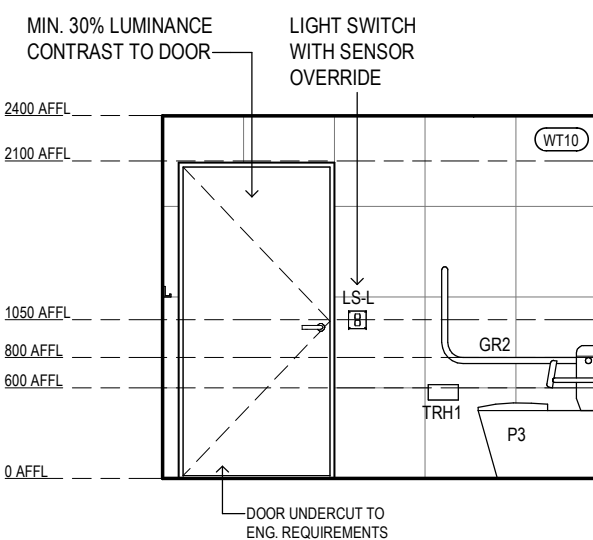


RACF - ACCESSIBLE ENSUITE
ELEVATION 1
Scale 1 : 50

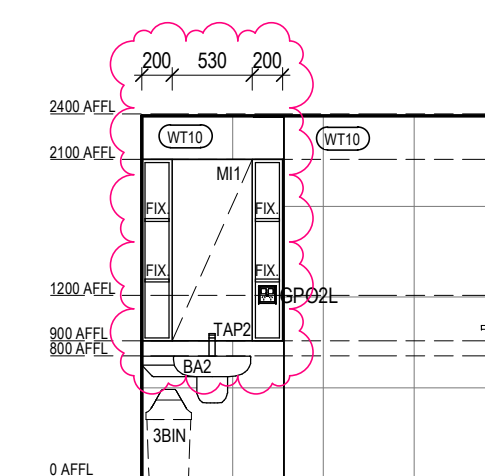

RACF - ACCESSIBLE ENSUITE
ELEVATION 2
Scale 1 : 50

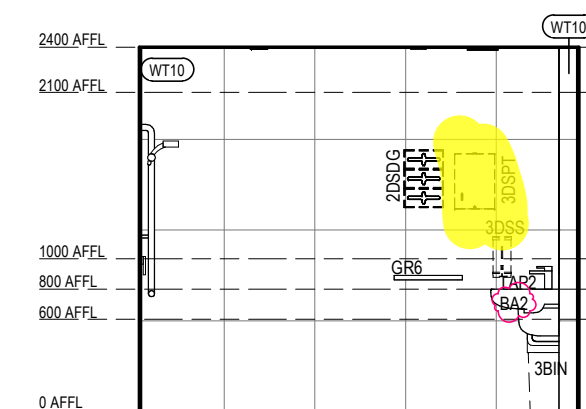

RACF - ACCESSIBLE ENSUITE
ELEVATION 3
Scale 1 : 50

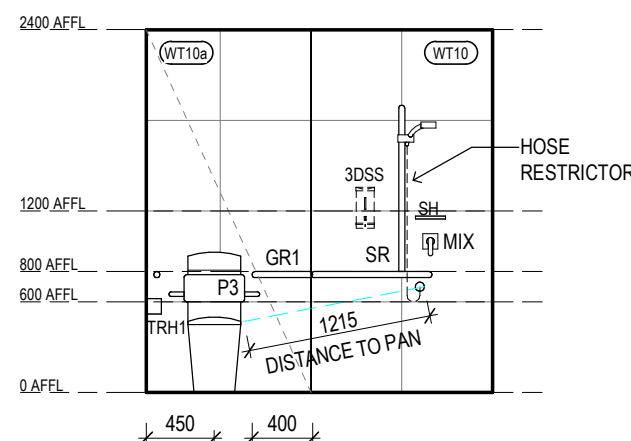

RACF - ACCESSIBLE ENSUITE
ELEVATION 4
Scale 1 : 50

Revision/Issue	Date
P2 Consolidated Set-to-date / SMG Comments	2025.08.15
P3 ISSUE FOR CONTRACT	2025.10.10
C1 ISSUE FOR CONSTRUCTION - INTERIORS	2026.03.30
C2 ISSUE FOR CONSTRUCTION	2026.06.08
C3 ISSUE FOR CONSTRUCTION	2026.06.02

ClarkeHopkinsClarke

Melbourne | Wurundjeri
L3, Melbourne Connect
700 Swanston Street
Carlton VIC 3063
Telephone (03) 9419 4340
Email studio@chc.com.au
www.chc.com.au

Sydney | Gadigal Country
Suite 3, Ground Floor
91 Campbell Street
Surry Hills NSW 2010
Telephone (02) 9221 9200
Email studio@chc.com.au
www.chc.com.au

Scale	As indicated @ A1
Date	01/03/2024
Drawn	RM
Architect	AC

Project
Summerset Oakleigh
52 Golf Road, Oakleigh South, VIC

Drawing
Internal Elevations - RACF Standard & Accessible Ensuites