




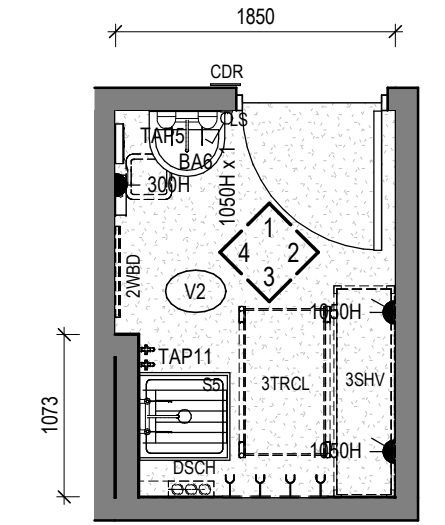


1 RACF-CLEANER - TYPE 1
Scale 1 : 50

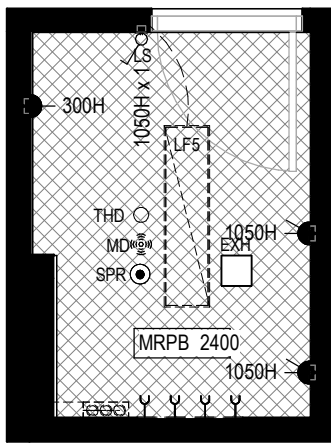


2 RCP-CLEANER - TYPE 1
Scale 1 : 50

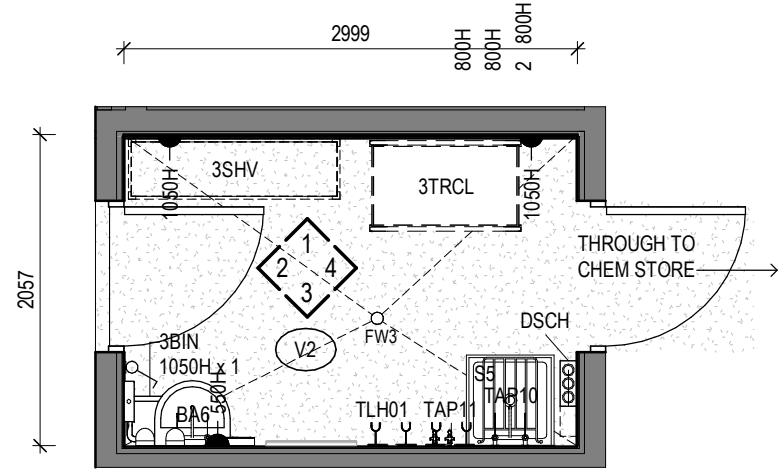


3 RACF-CLEANER - TYPE 2
Scale 1 : 50

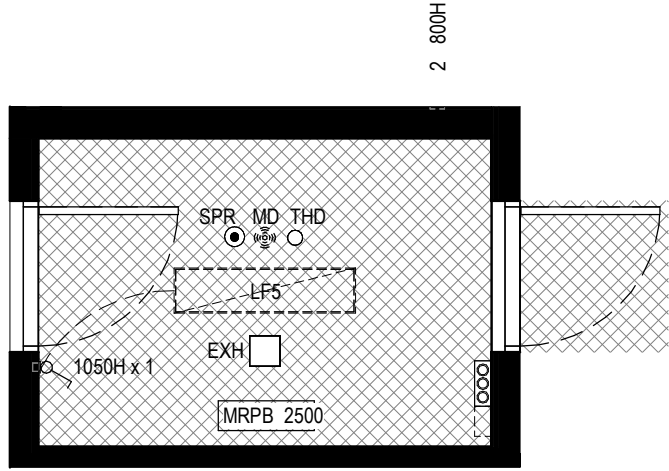


4 RCP-CLEANER - TYPE 2
Scale 1 : 50

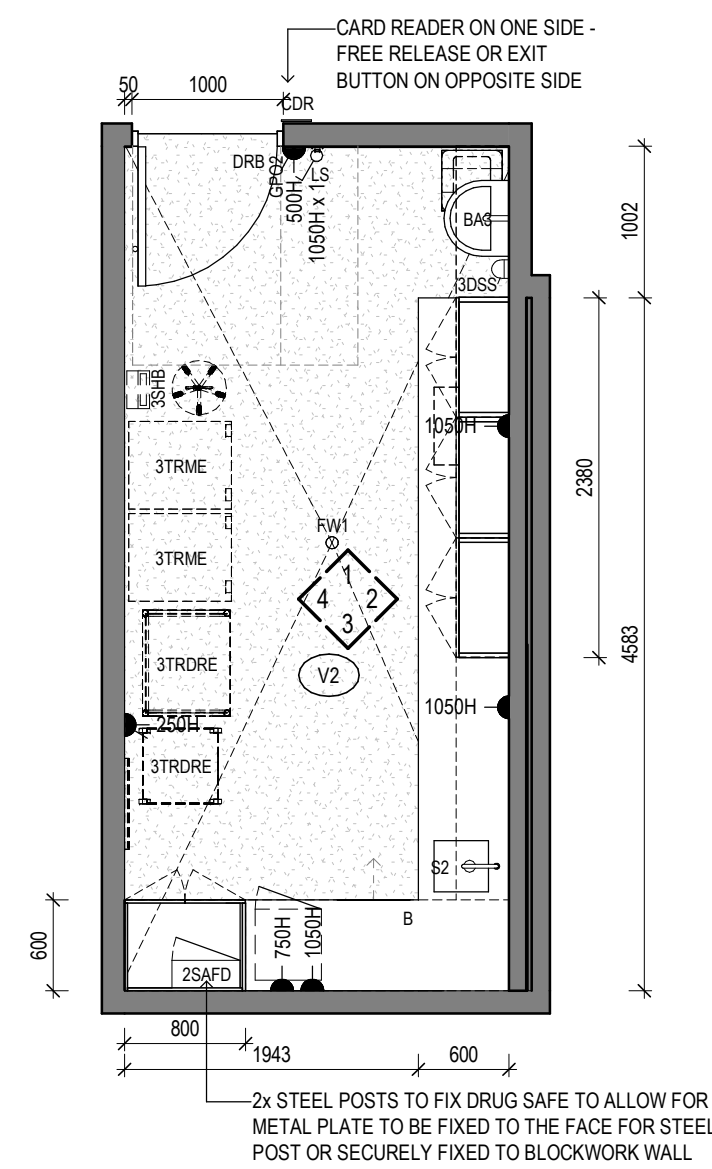


5 RACF-TREATMENT
Scale 1 : 50

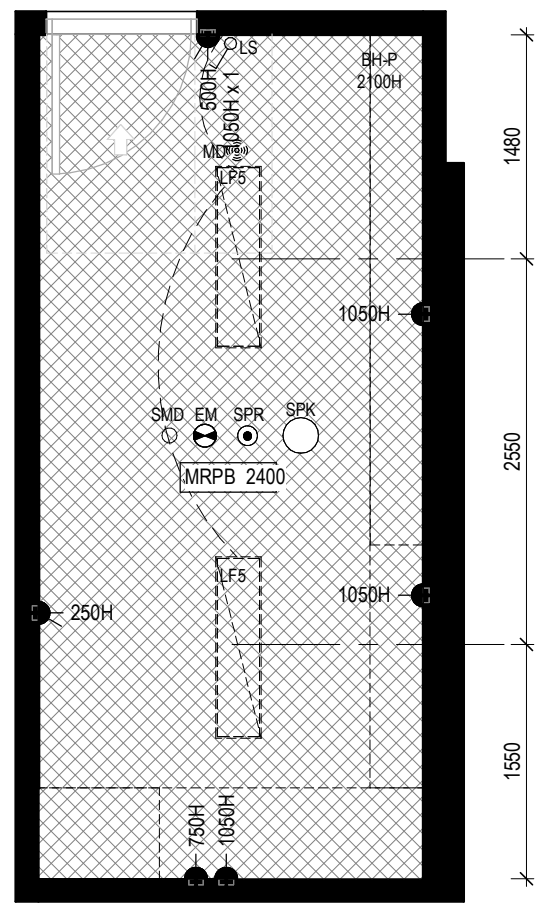


6 RCP-TREATMENT
Scale 1 : 50

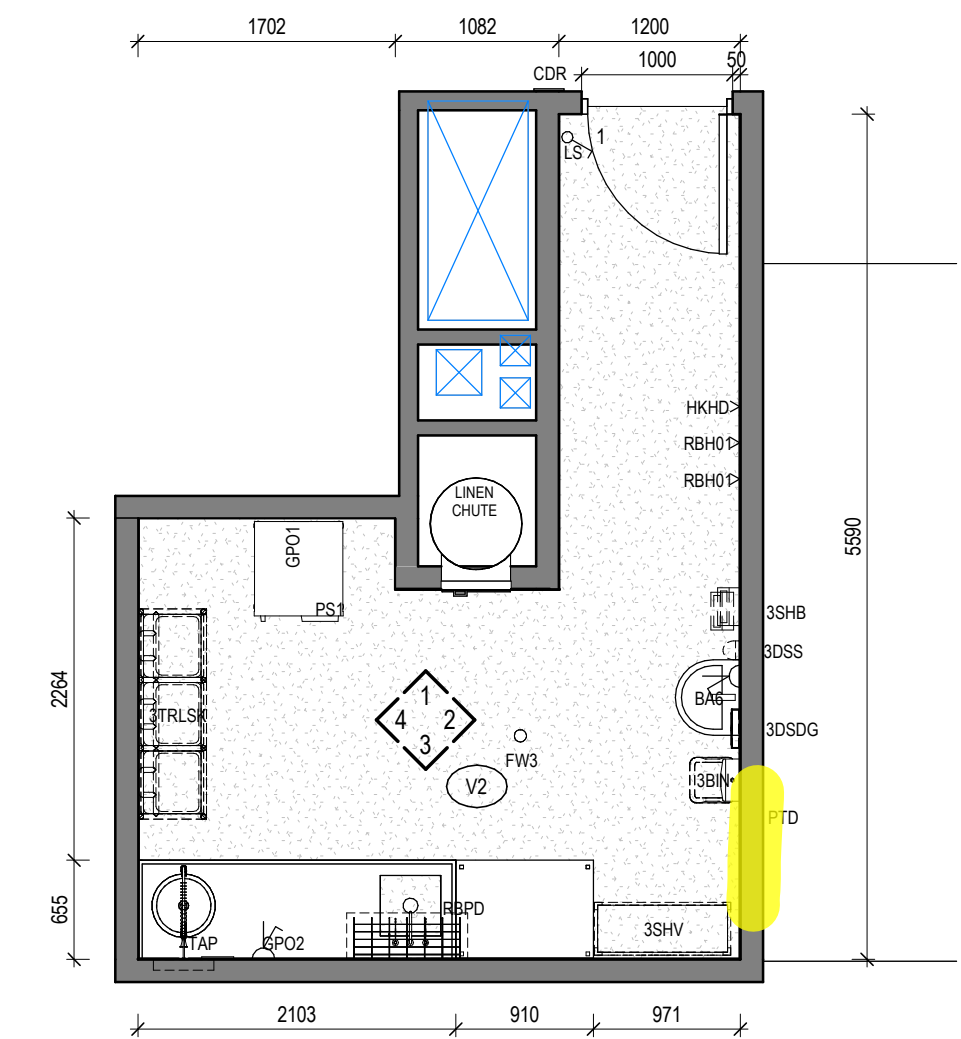


7 RACF-SLUICE
Scale 1 : 50

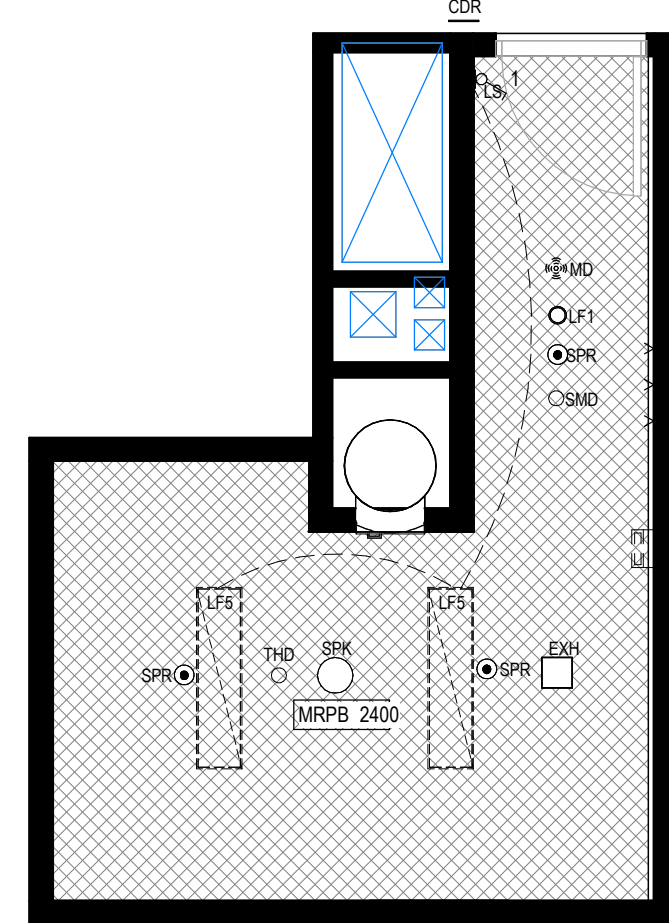


8 RCP-SLUICE
Scale 1 : 50

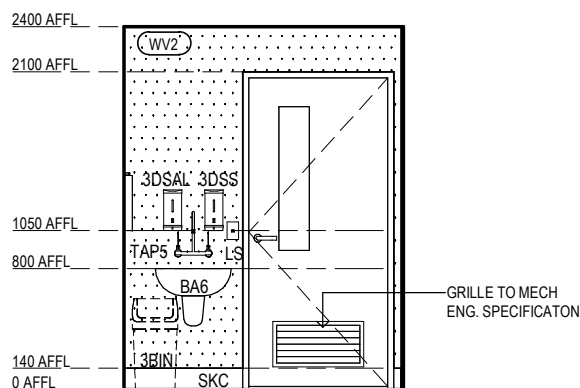


RACF BOH - CLEANER - TYPE 1
ELEVATION 1
Scale 1 : 50

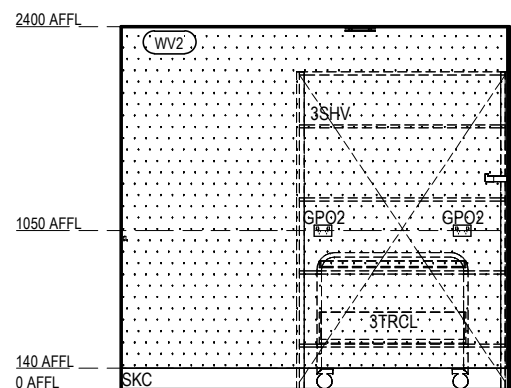


RACF BOH - CLEANER - TYPE 1
ELEVATION 2
Scale 1 : 50

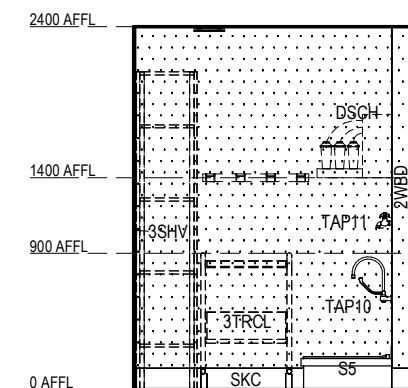


RACF BOH - CLEANER - TYPE 1
ELEVATION 3
Scale 1 : 50

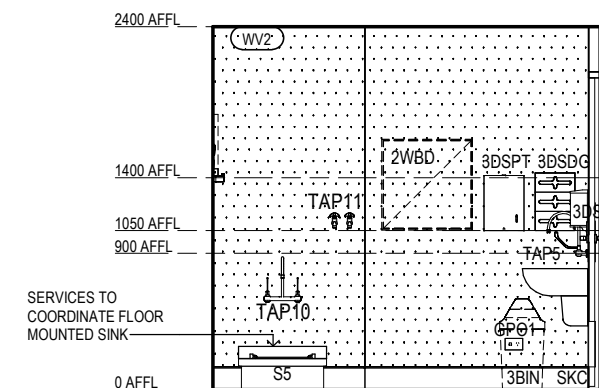


RACF BOH - CLEANER - TYPE 1
ELEVATION 4
Scale 1 : 50

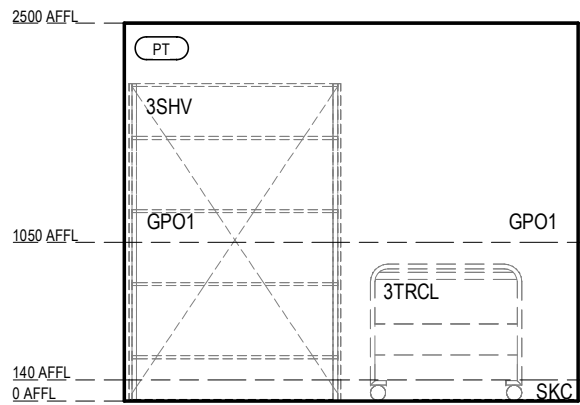


RACF BOH - CLEANER - TYPE 2
ELEVATION 1
Scale 1 : 50

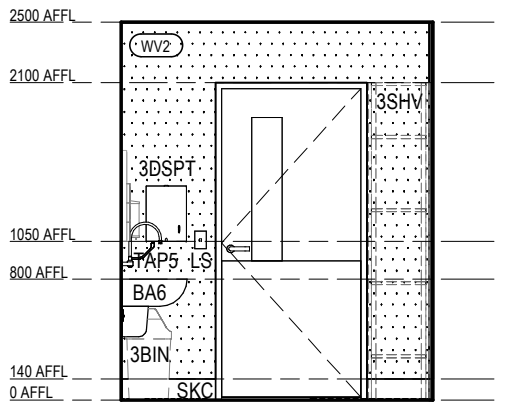


RACF BOH - CLEANER - TYPE 2
ELEVATION 2
Scale 1 : 50

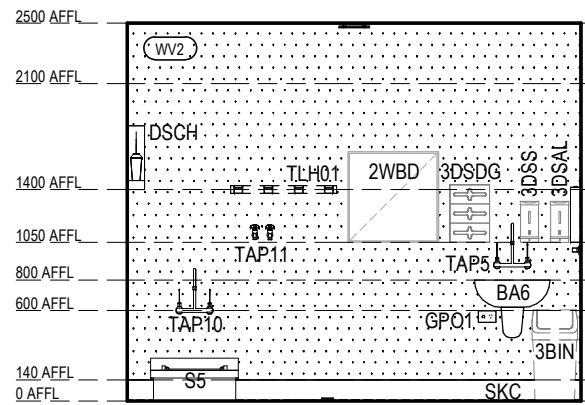


RACF BOH - CLEANER - TYPE 2
ELEVATION 3
Scale 1 : 50

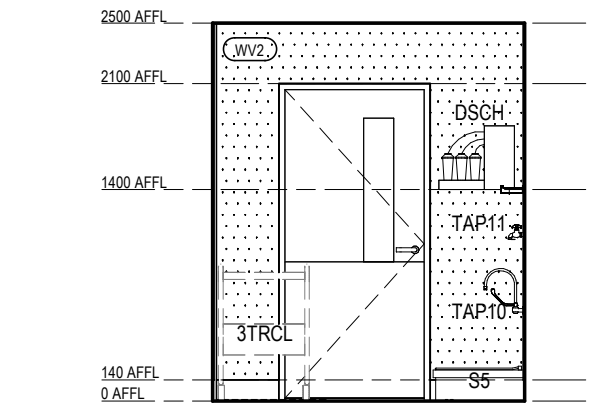


RACF BOH - CLEANER - TYPE 2
ELEVATION 4
Scale 1 : 50

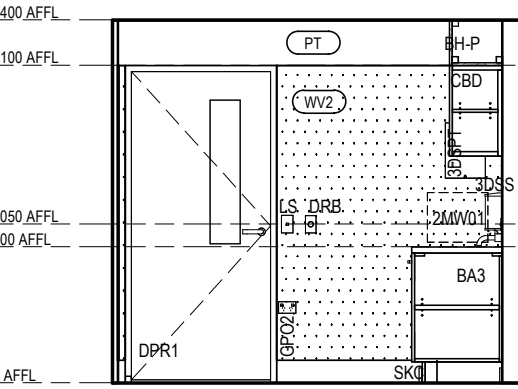


RACF BOH - TREATMENT
ELEVATION 1
Scale 1 : 50

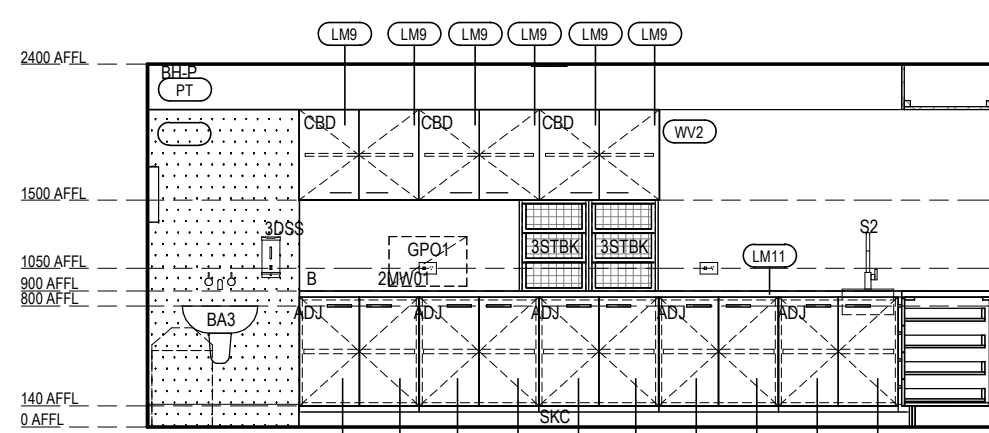


RACF BOH - TREATMENT
ELEVATION 2
Scale 1 : 50

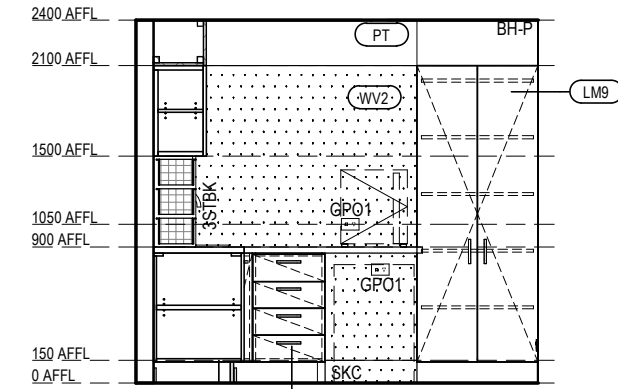


RACF BOH - TREATMENT
ELEVATION 3
Scale 1 : 50

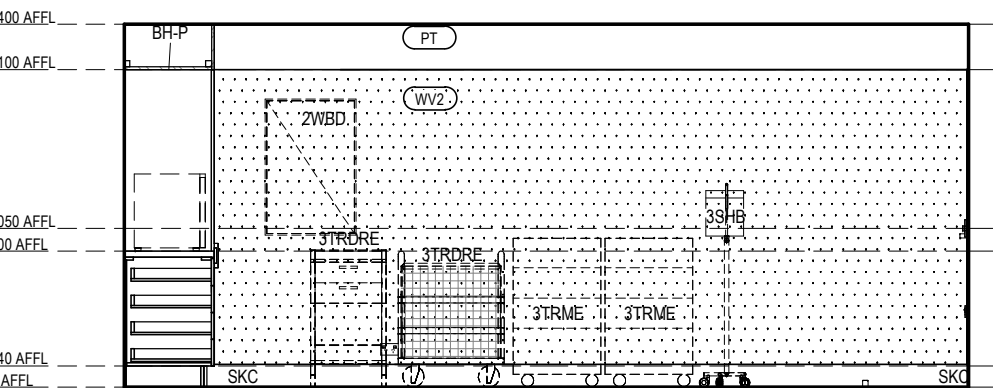

RACF BOH - TREATMENT
ELEVATION 4
Scale 1 : 50

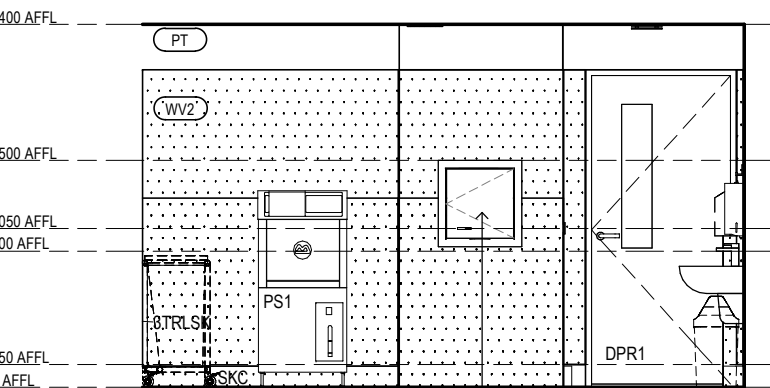

RACF BOH - SLUICE
ELEVATION 1
Scale 1 : 50

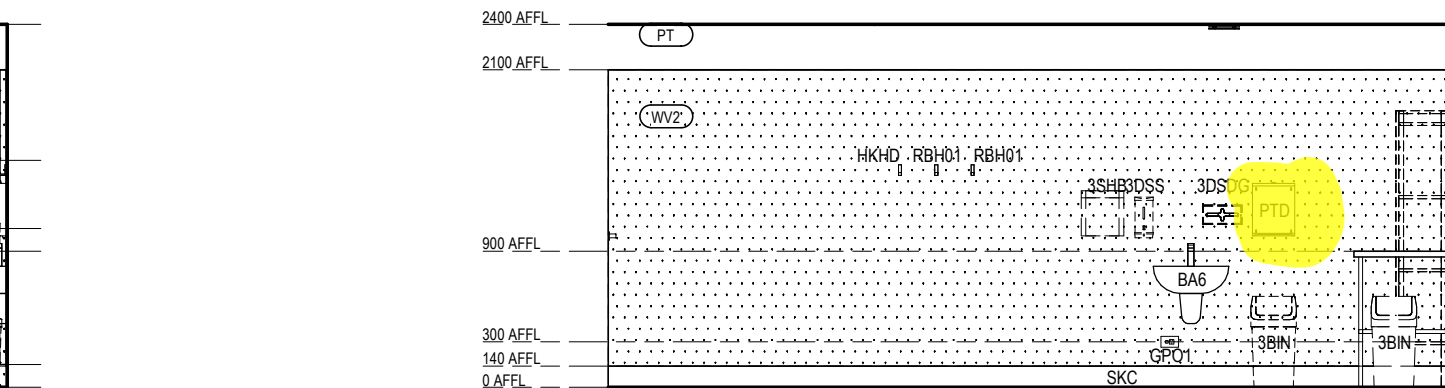

RACF BOH - SLUICE
ELEVATION 2
Scale 1 : 50

