




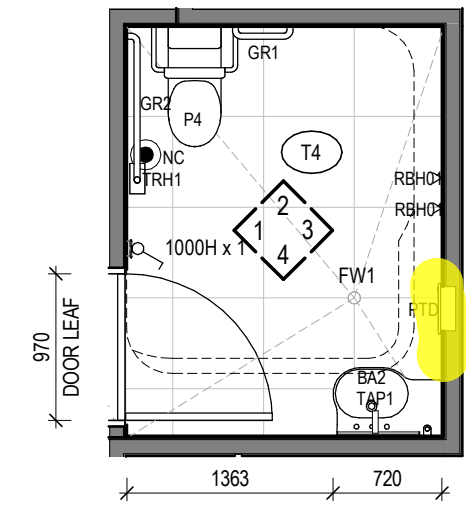


3 RACF AMENITIES - ACCESSIBLE WC 01
Scale 1: 50

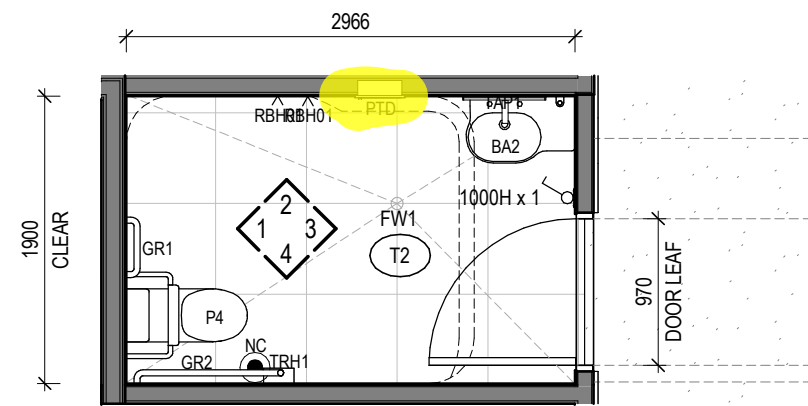


4 RACF AMENITIES - ACCESSIBLE WC 02
Scale 1: 50

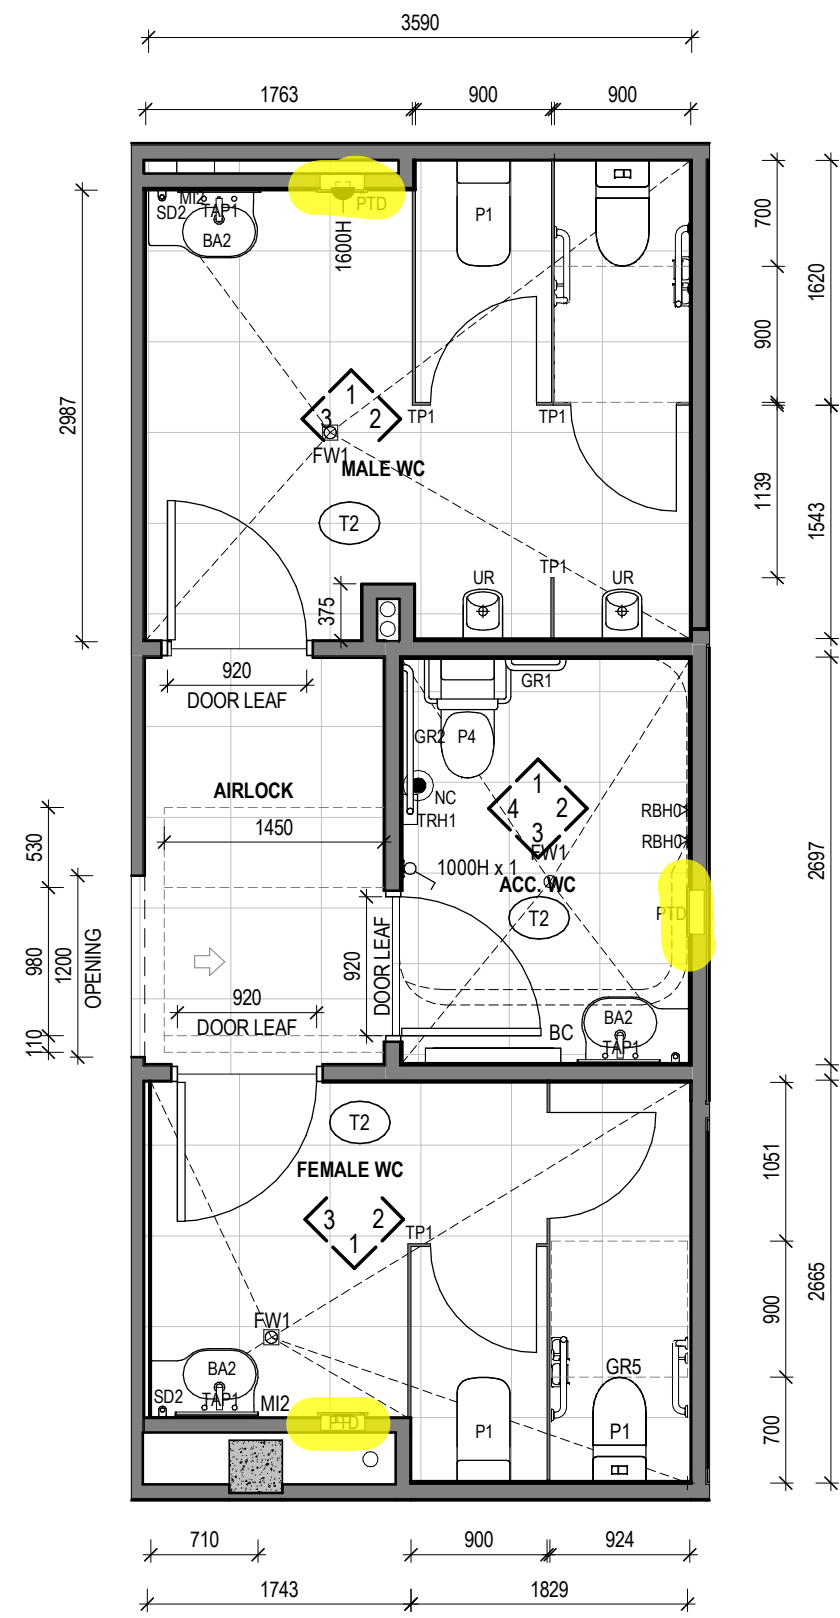


1 VILLAGE LIFESTYLE - AMENITIES
Scale 1: 50

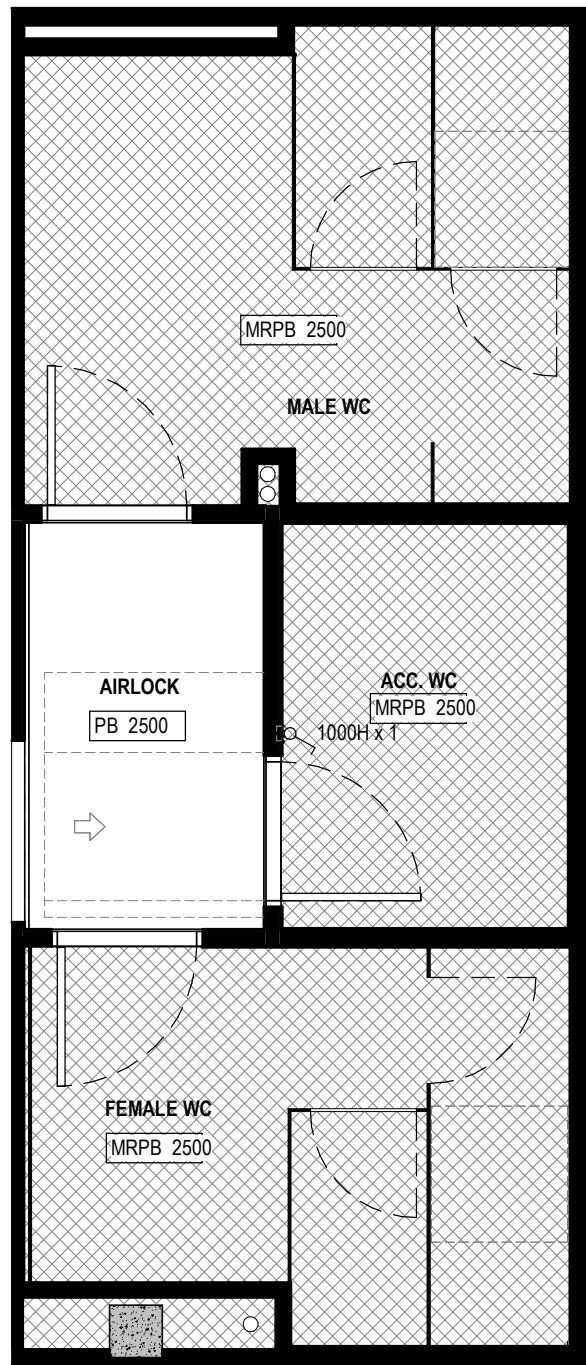


2 RCP - VILLAGE LIFESTYLE - AMENITIES
A1400 Scale 1: 50

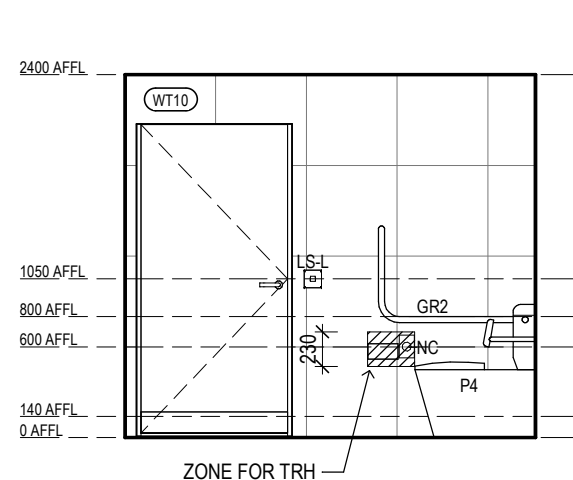


ACCESSIBLE WC 01 - 1

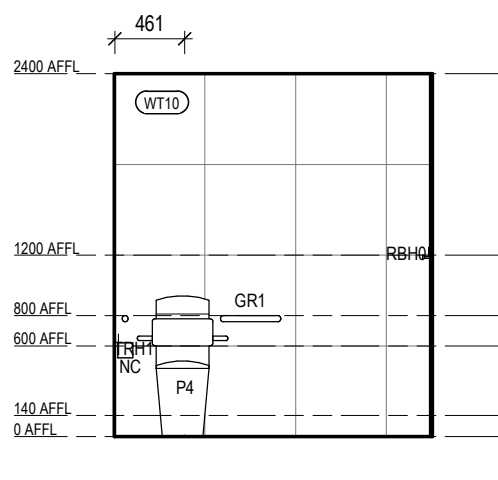


ACCESSIBLE WC 01 - 2

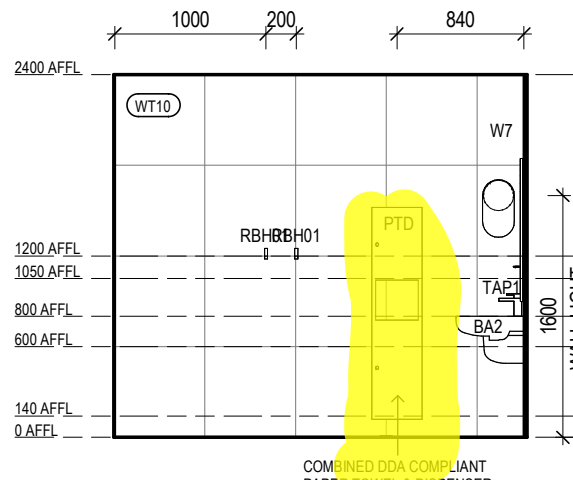


ACCESSIBLE WC 01 - 3

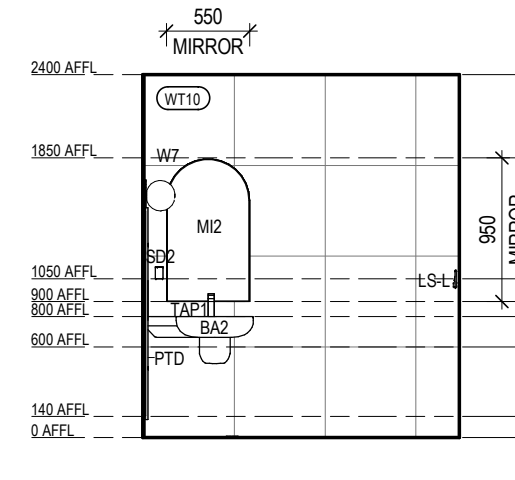


ACCESSIBLE WC 01 - 4

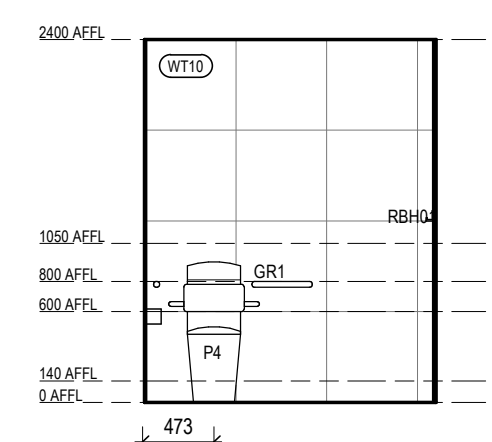


ACCESSIBLE WC 02 - 1

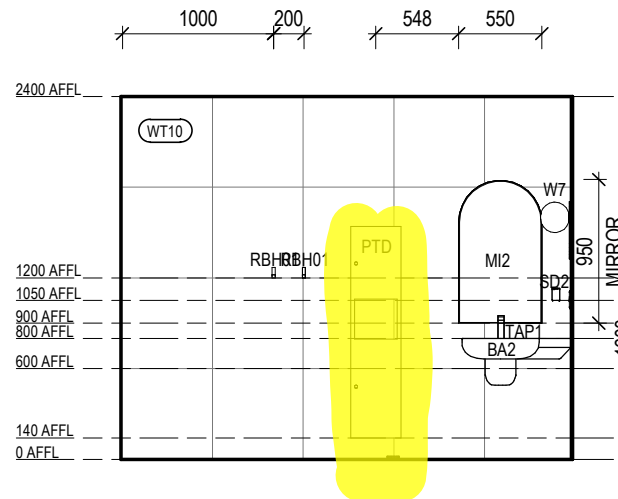


ACCESSIBLE WC 02 - 2

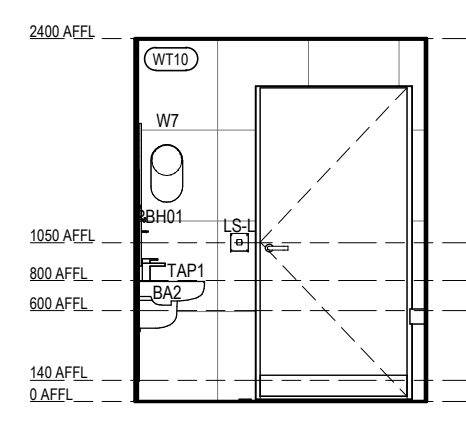


ACCESSIBLE WC 02 - 3

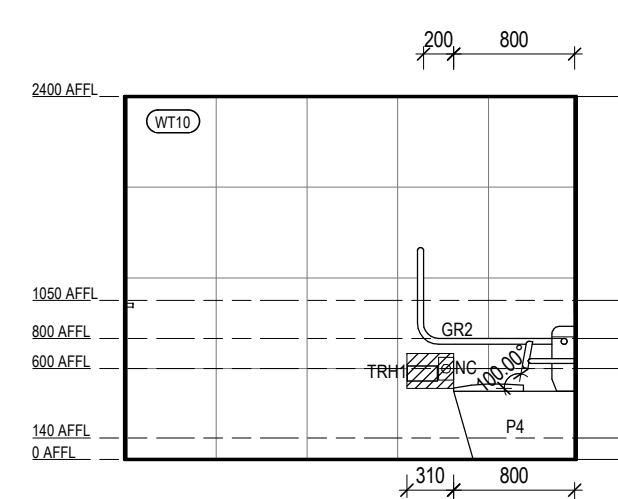


ACCESSIBLE WC 02 - 4

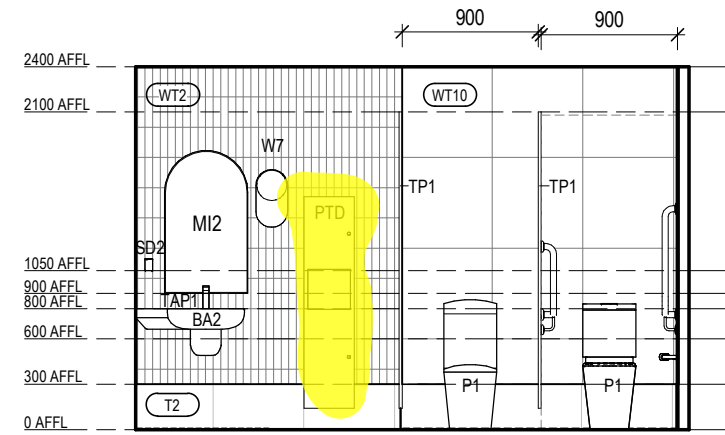


VILLAGE AMENITIES - MALE WC - 1

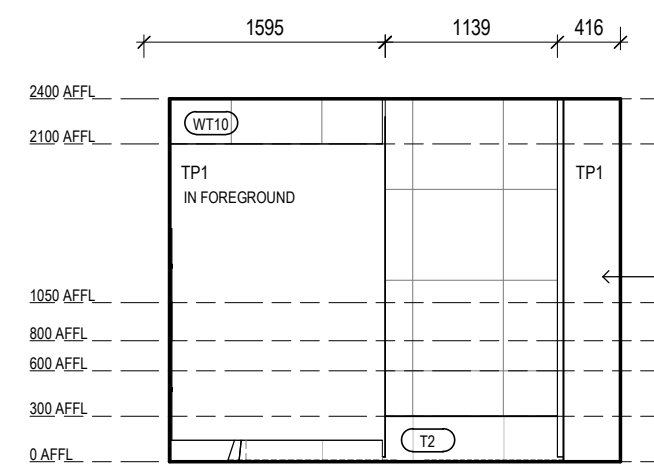


VILLAGE AMENITIES - MALE WC - 2

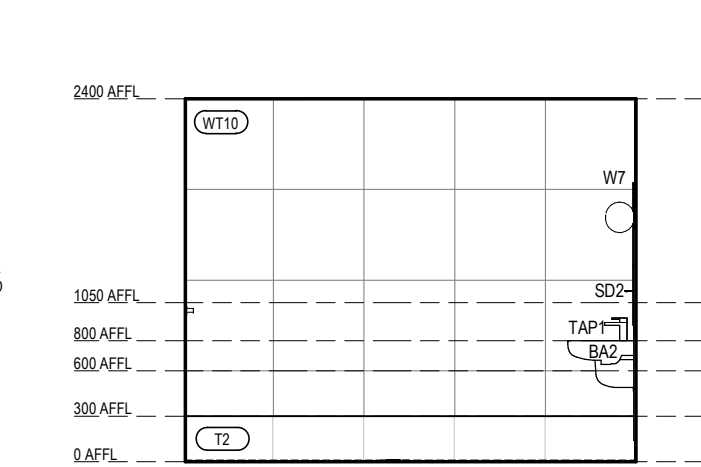


VILLAGE AMENITIES - MALE WC - 3

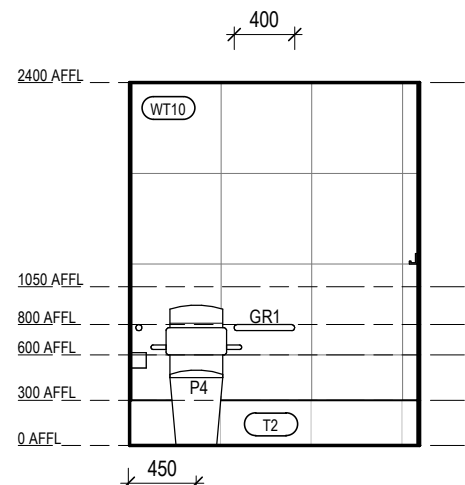


VILLAGE AMENITIES - ACC WC - 1

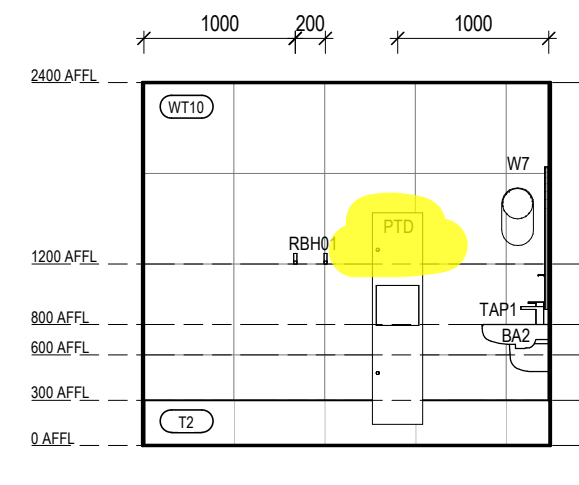


VILLAGE AMENITIES - ACC WC - 2

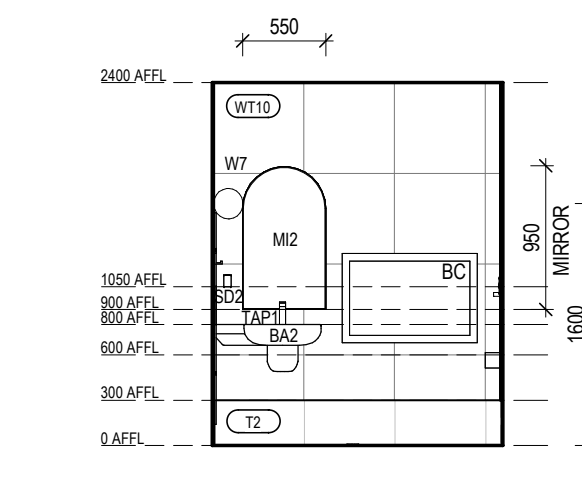


VILLAGE AMENITIES - ACC WC - 3

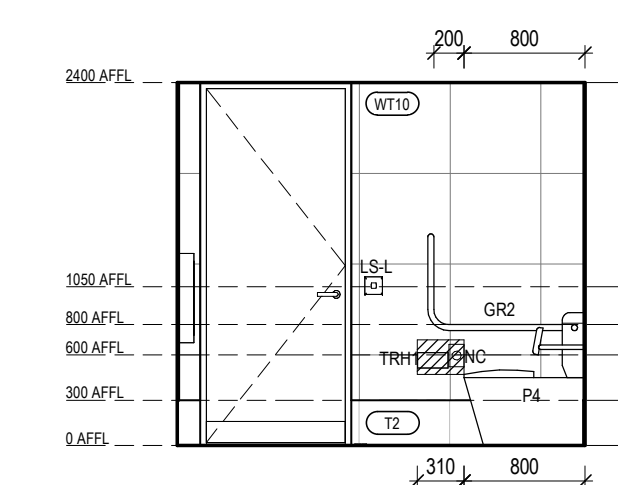


VILLAGE AMENITIES - ACC WC - 4

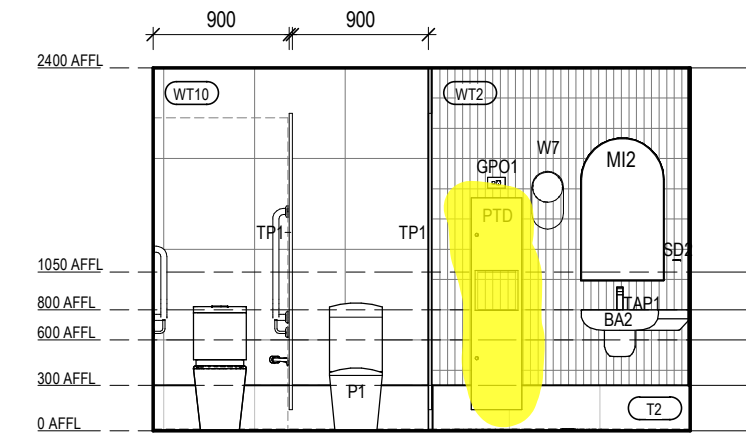

VILLAGE AMENITIES - FEMALE WC - 1

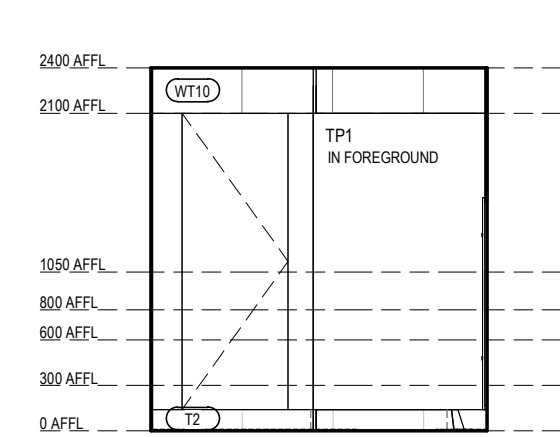

VILLAGE AMENITIES - FEMALE WC - 2

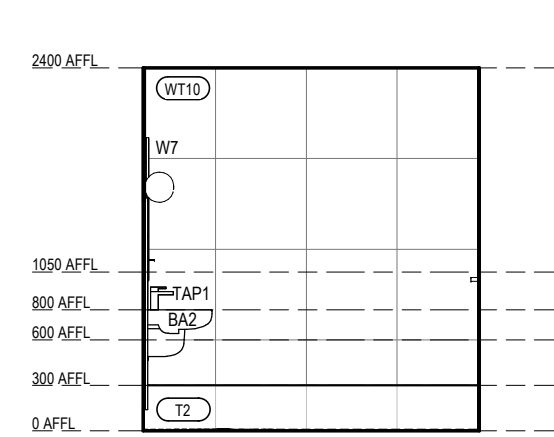

VILLAGE AMENITIES - FEMALE WC - 3

Legend - Internal Elevations

DRAWINGS TO BE READ IN CONJUNCTION WITH ARCHITECTURAL SPECIFICATION & MATERIALS, PRODUCTS & FINISHES SCHEDULE.

PT# PAINT FINISH TO ALL WALLS WITHIN NEW & AFFECTED ROOMS/ AREAS UNLESS OTHERWISE SHOWN

- CSE CONCRETE SEALER
- DPR DOOR PROTECTION
- GD GRAPHIC FILM
- LM LAMINATE
- MI MIRROR
- PBD PINBOARD
- PT PAINT FINISH
- REN RENDER FINISH
- SB SPLASHBACK
- ST STONE
- WB WHITEBOARD
- WP WALL PROTECTION
- WT WALL TILE
- WV WALL VINYL
- UPH UPHOLSTERY

NOTES:
1. LAMINATE CARCASS FOR ALL VISIBLE OPEN SHELVING, UNLESS OTHERWISE NOTED
2. MELAMINE TO ALL INTERNAL CARCASS OF JOINERY, UNLESS OTHERWISE NOTED.

--- PROVIDE NOGGINGS FOR FUTURE USE

Legend - Floor Finishes

- C CARPET
- CO CONCRETE
- E EPOXY FINISH
- L LINOLEUM
- M MATTING
- FU PAVING UNIT - TBC WITH LANDSCAPE
- R RUBBER FLOORING
- T TILING
- TF TIMBER FLOORING
- V VINYL
- LVT LUXURY VINYL TILE PLANK

--- PROTECTION RAILS OR CRASH RAILS - REFER TO MATERIAL SCHEDULE FOR DETAILS

--- WL1- REFER TO MATERIAL SCHEDULE FOR DETAILS

--- WL2- REFER TO MATERIAL SCHEDULE FOR DETAILS

NOTE:
FALLS TO ALL FLOOR WASTES IN ACCORDANCE WITH AS 3740.

Keynote Legend

- BA2 BASIN - TYPE 2
- BC BABY CHANGE TABLE
- FW1 FLOOR WASTE - TYPE 1
- GP01 POWER OUTLET - SINGLE
- GR1 GRAB RAIL - TYPE 1
- GR2 GRAB RAIL - TYPE 2
- GR5 GRAB RAIL - TYPE 5
- LS-L LIGHT SWITCH - LARGE PLATE
- MI2 MIRROR - TYPE 2
- NC NURSE CALL
- P1 TOILET PAN TYPE 01
- P4 TOILET PAN TYPE 04
- PTD PAPER TOWEL DISPENSER
- RBH01 ROBE HOOK - TYPE 1
- SD2 SOAP DISPENSER - TYPE 2
- TAP1 TAP - TYPE 1
- TP1 TOILET PARTITION - TYPE 1
- TRH1 TOILET ROLL HOLDER - TYPE 1
- UR URINAL
- W7 WALL LIGHT - TYPE 7

FOR CONSTRUCTION

Revision/Issue	Date
P1 RACF & ILA WIP Consultant Coordination & Review	2025.06.24
P2 Consolidated Set-to-date / SMG Comments	2025.08.15
P3 ISSUE FOR CONTRACT	2025.10.10
C1 ISSUE FOR CONSTRUCTION - INTERIORS	2026.03.30

Clarke Hopkins
architects

ClarkeHopkinsClarke
Melbourne | Wurundjeri
L3, Melbourne Connect
700 Swanston Street
Carlton VIC 3063
Telephone (03) 9419 4340
Email studio@chc.com.au
www.chc.com.au

Sydney | Gadigal Country
Suite 3, Ground Floor
91 Campbell Street
Surry Hills NSW 2010
Telephone (02) 9221 9200
Email studio@chc.com.au
www.chc.com.au

Scale	As indicated @ A1
Date	01/03/2024
Drawn	TT / TM
Architect	EL

Project
Summerset Oakleigh
52 Golf Road, Oakleigh South, VIC

Drawing
Internal Elevations - Amenities

Drawing No.
230185/A1845
C1