
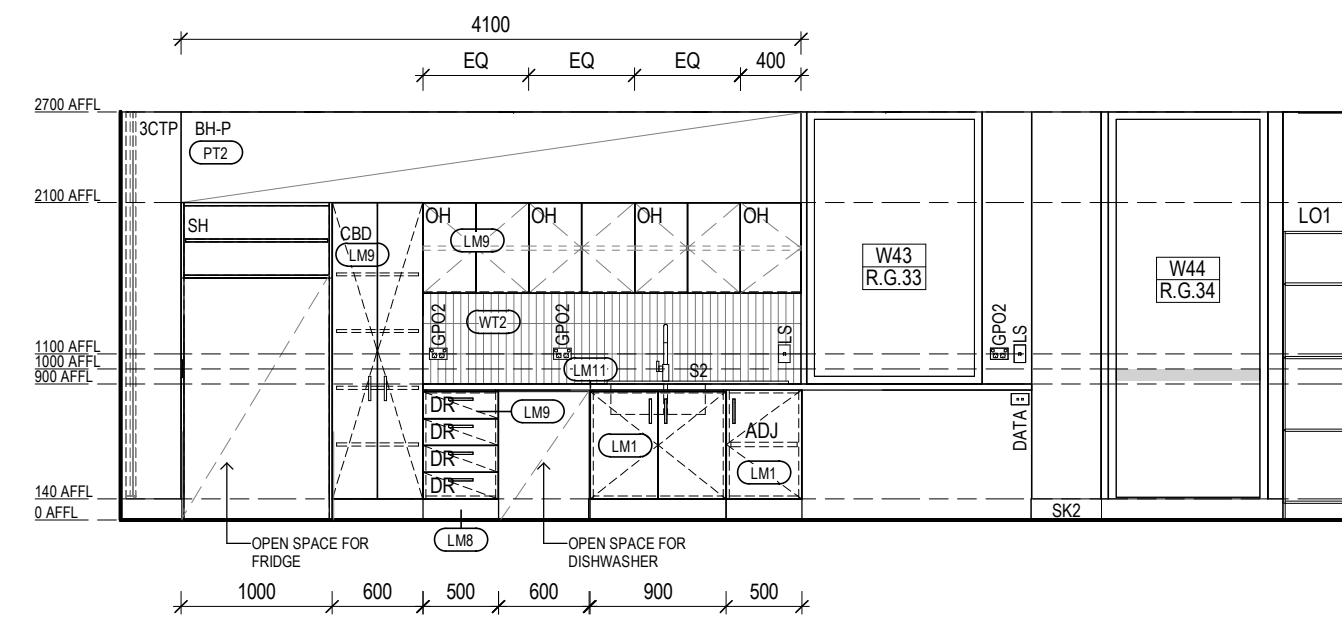
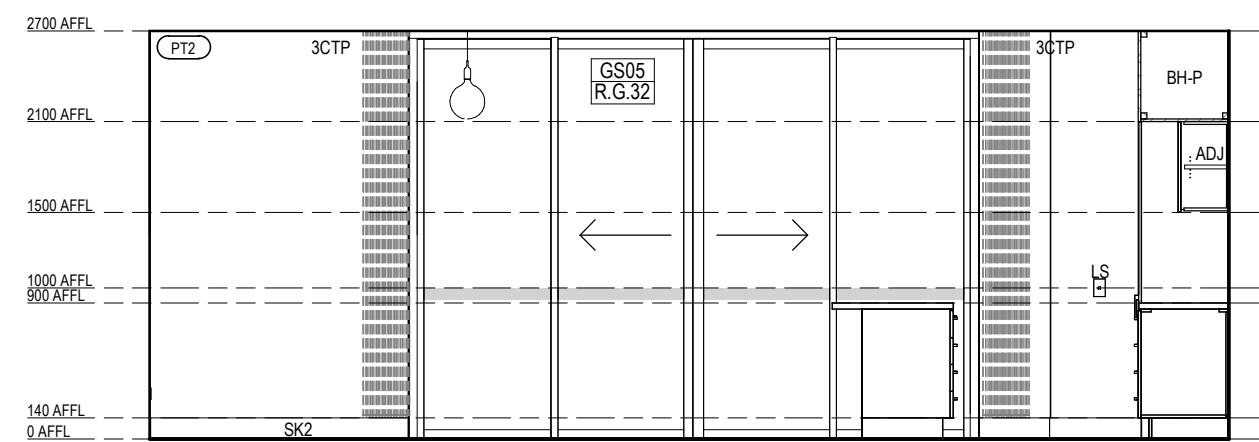
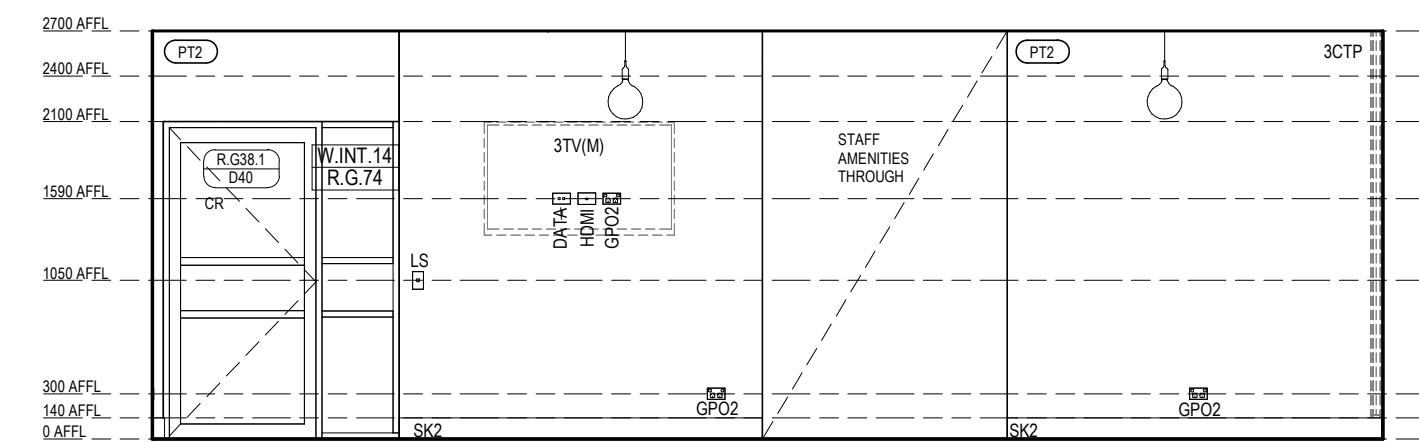
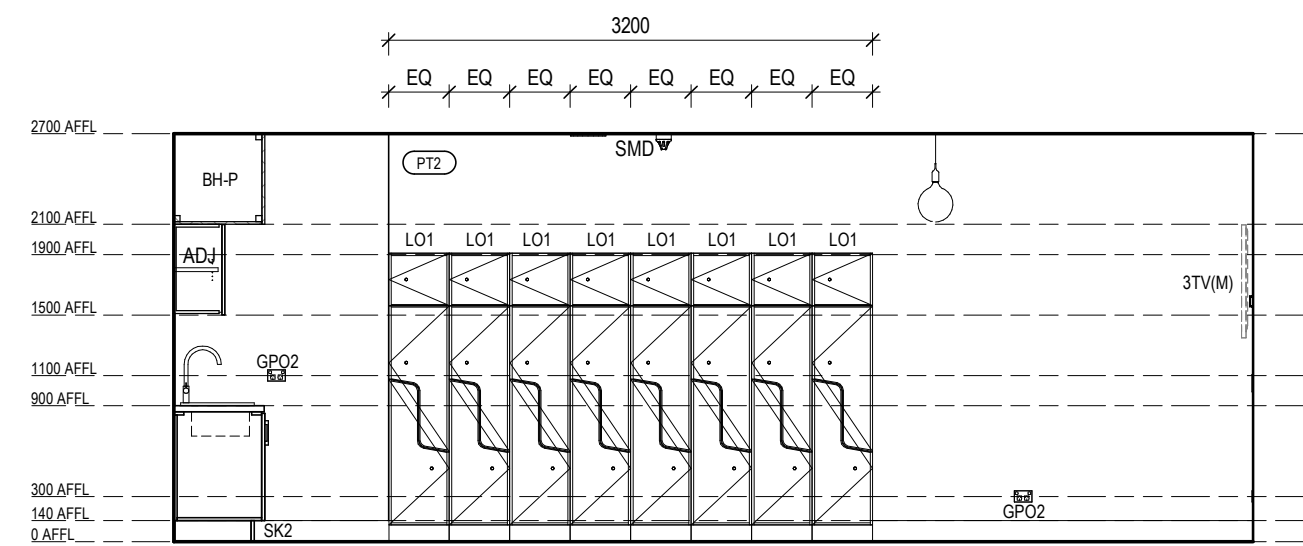
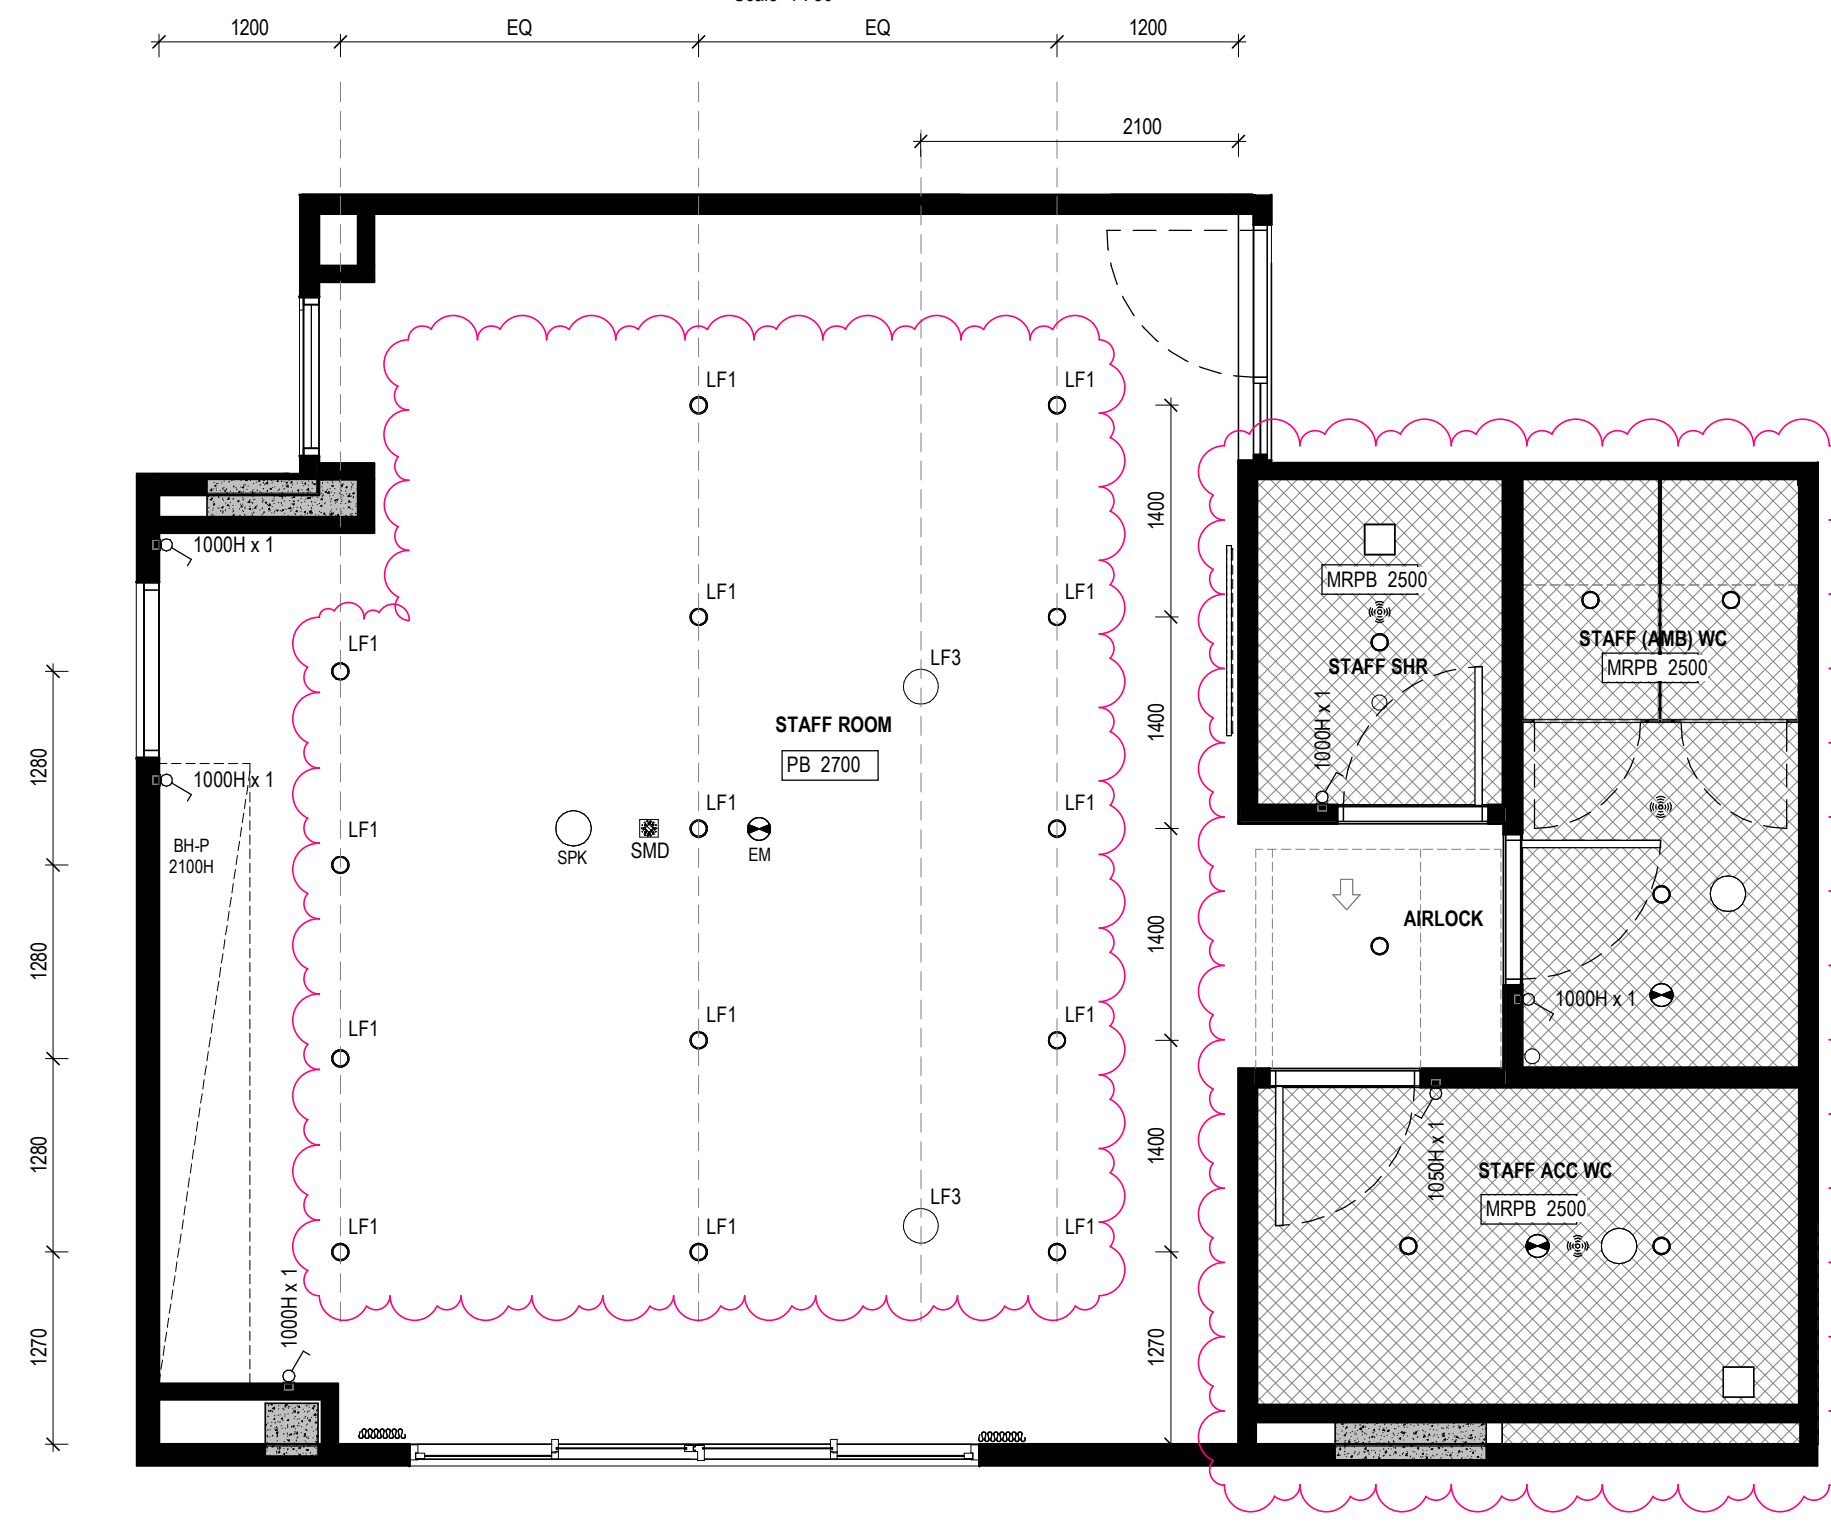
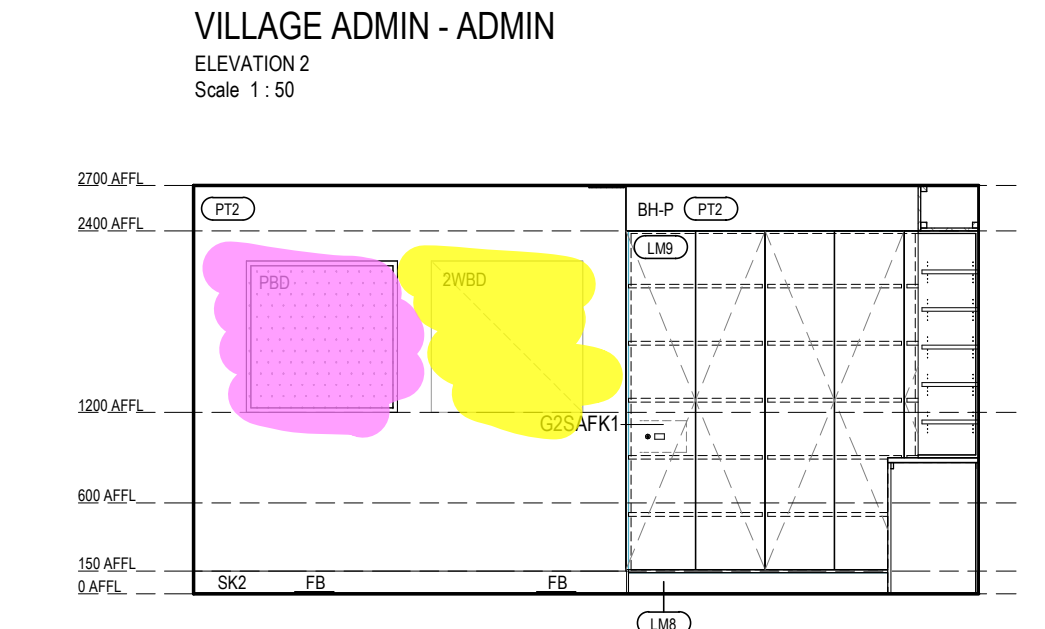
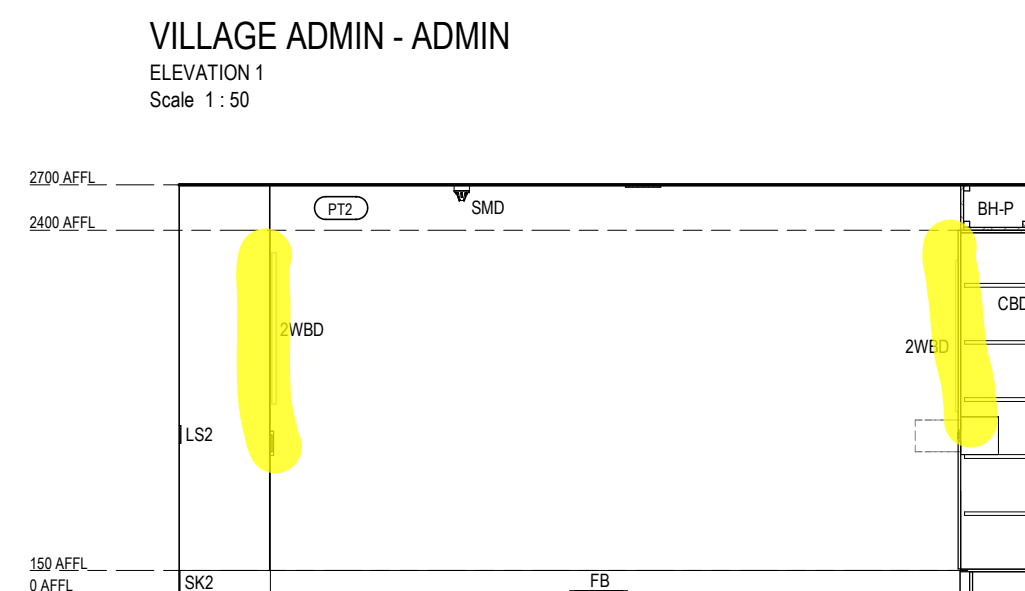
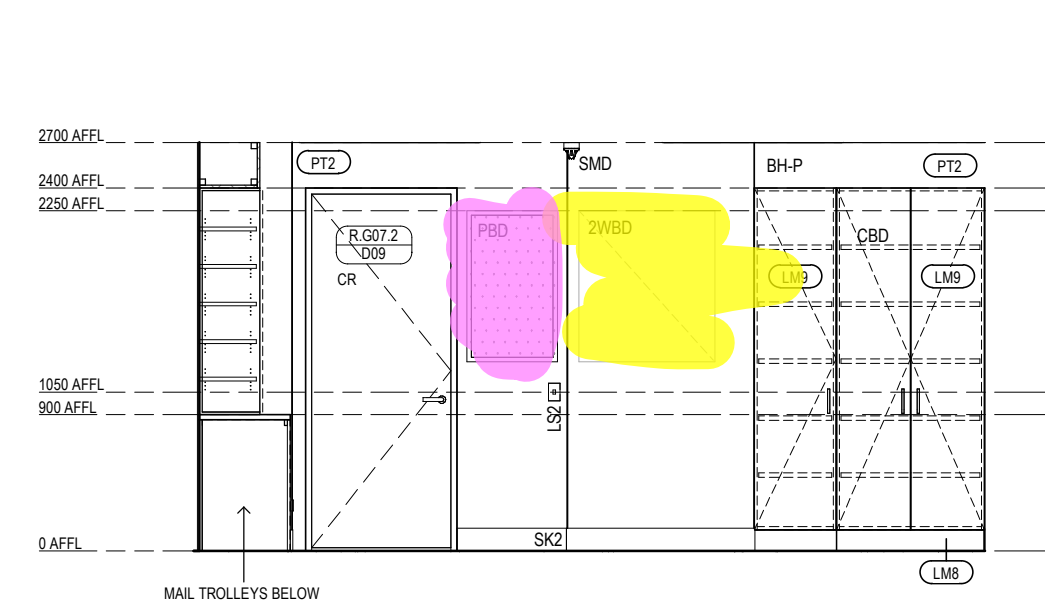
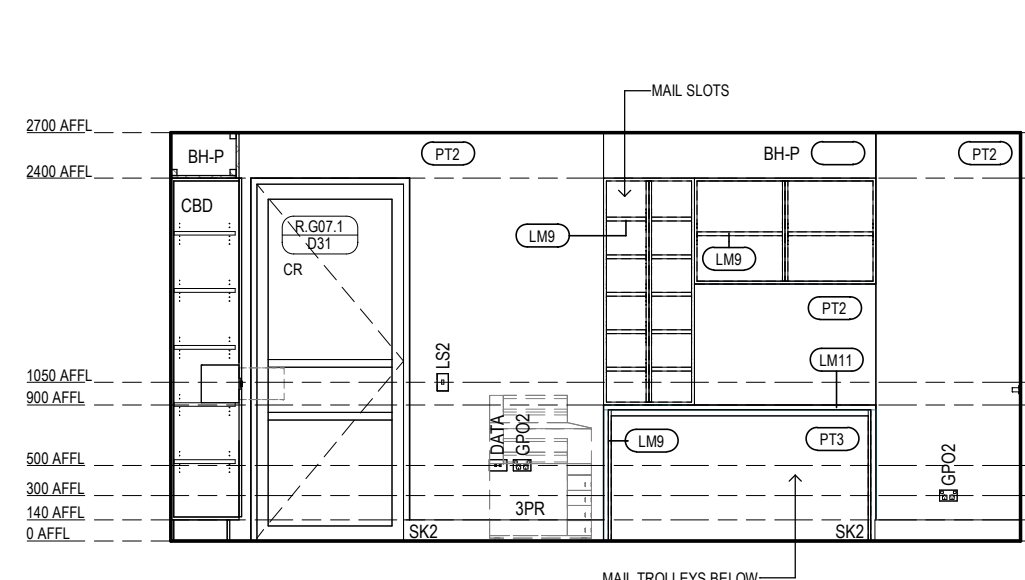
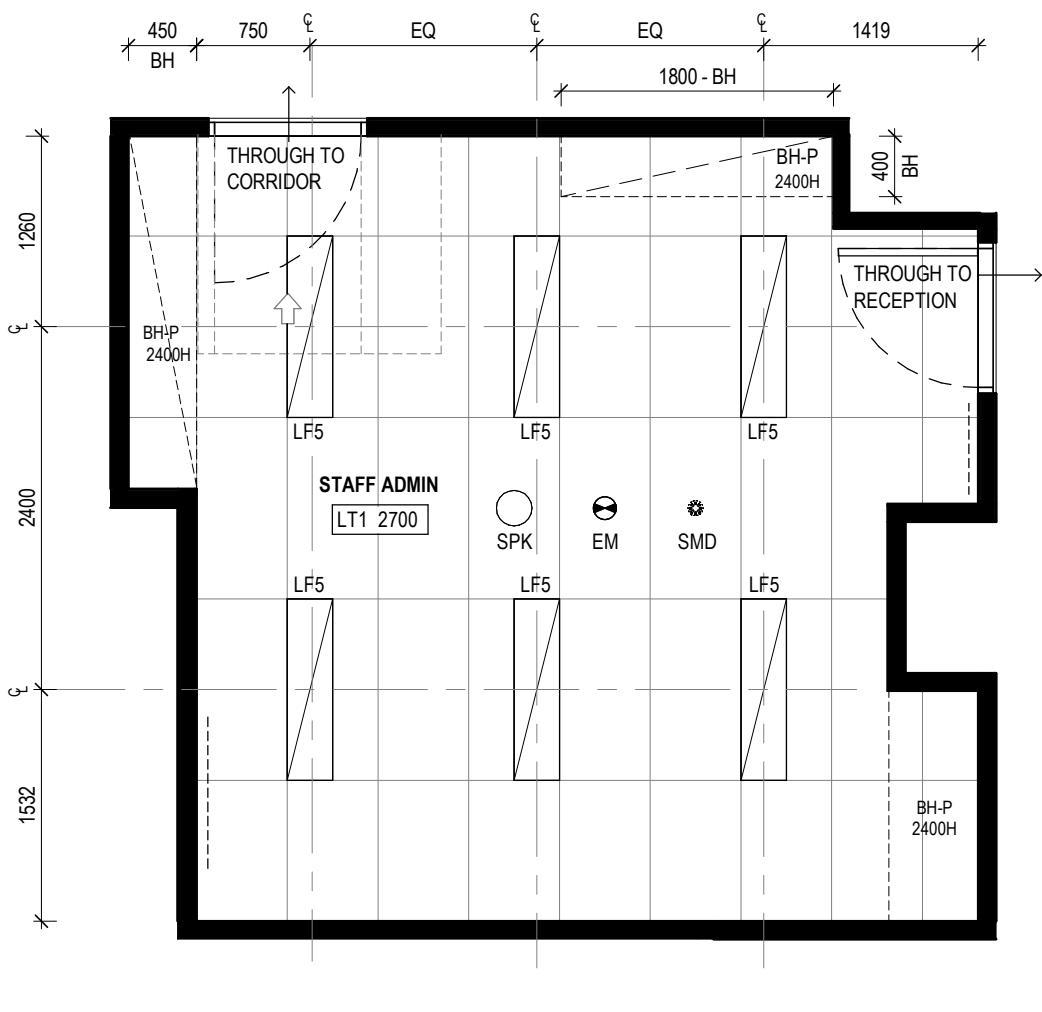


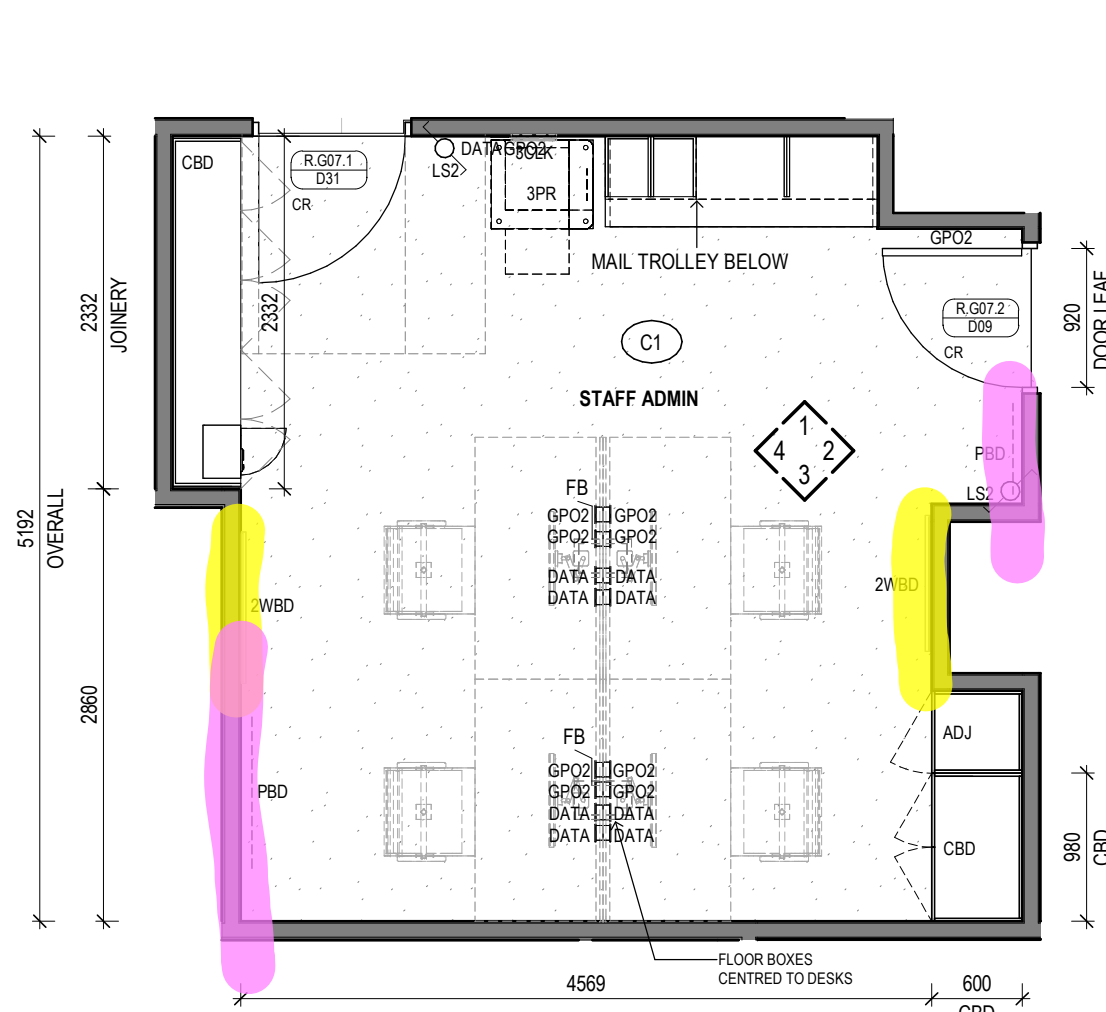

Legend - Internal Elevations

DRAWINGS TO BE READ IN CONJUNCTION WITH ARCHITECTURAL SPECIFICATION & MATERIALS, PRODUCTS & FINISHES SCHEDULE.

PT# PAINT FINISH TO ALL WALLS WITHIN NEW & AFFECTED ROOMS/
AREAS UNLESS OTHERWISE SHOWN

- | | |
|-----|-----------------|
| CSE | CONCRETE SEALER |
| DPR | DOOR PROTECTION |
| GD | GRAPHIC FILM |
| LM | LAMINATE |
| MI | MIRROR |
| PBD | PINBOARD |
| PT | PAINT FINISH |
| REN | RENDER FINISH |
| SB | SPLASHBACK |
| ST | STONE |
| WB | WHITEBOARD |
| WP | WALL PROTECTION |
| WT | WALL TILE |
| WV | WALL VINYL |

NOTES:

1. LAMINATE CARCASS FOR ALL VISIBLE OPEN SHELVING, UNLESS OTHERWISE NOTED
2. MELAMINETO ALL INTERNAL CARCASS OF JOINERY, UNLESS OTHERWISE NOTED.

Legend - Floor Finishes

- | | |
|-----|----------------------------------|
| C | CARPET |
| CO | CONCRETE |
| E | EPOXY FINISH |
| L | LINOLEUM |
| M | MATTING |
| PU | PAVING UNIT - TBC WITH LANDSCAPE |
| R | RUBBER FLOORING |
| T | TILING |
| TF | TIMBER FLOORING |
| V | VINYL |
| LVT | LUXURY VINYL TILE PLANK |

- PROTECTION RAILS OR CRASH RAILS - REFER TO MATERIAL SCHEDULE FOR DETAILS
- WL1- REFER TO MATERIAL SCHEDULE FOR DETAILS
- WL2- REFER TO MATERIAL SCHEDULE FOR DETAILS

NOTE:
FALLS TO ALL FLOOR WASTES IN ACCORDANCE WITH AS 3740.

Keynote Legend

- | | |
|---------|--|
| ZWB0 | WHITEBOARD - GROUP 2 |
| 3CLK | CLOCK - GROUP 3 |
| 3CTR | CURTAINS - GROUP 3 |
| 3PCR | PRINTER - GROUP 3 |
| 3TBC0 | COFFEE TABLE - GROUP 3 |
| 3TVM0 | TELEVISION SCREEN 55 INCH - GROUP 3 |
| ADJ1 | ADJUSTABLE SHELF |
| BHP+P | BULKHEAD - PLASTERBOARD TYPE |
| CHM4 | CCTV CAMERA |
| CBD | CUPBOARD |
| DATA | DATA OUTLET |
| DR | DRAINER |
| EM | EMERGENCY LIGHT |
| FB | FLOOR BOX |
| FE-JC | FIRE EXTINGUISHER IN JOINERY CUPBOARD |
| GZSAFK1 | |
| GP02 | POWER OUTLET - DOUBLE |
| HDM1 | HDMI OUTLET |
| LF1 | LIGHT FITTING - REFER TO ELECTRICAL ENGINEER SPECIFICATION |
| LF3 | LIGHT FITTING - TYPE 3 |
| LF5 | LIGHT FITTING - TYPE 5 |
| LO1 | LOCKER - TYPE 1 |
| LS | LIGHT SWITCH |
| LS2 | LIGHT SWITCH - TWO WAY |
| OH | OVERHEAD CUPBOARD/SHELVING |
| P1 | TOILET PAN - TYPE 01 |
| PBD | PINGBOARD - FRAMED |
| SC2 | SHIRK - TYPE 2 |
| SH | SHELF |
| SQ | SKIRTING - TYPE 2 |
| SPD | SMOKE DETECTOR |
| SPK | ANUNCIATOR |