




UPDATES PER
APR-REV-000133

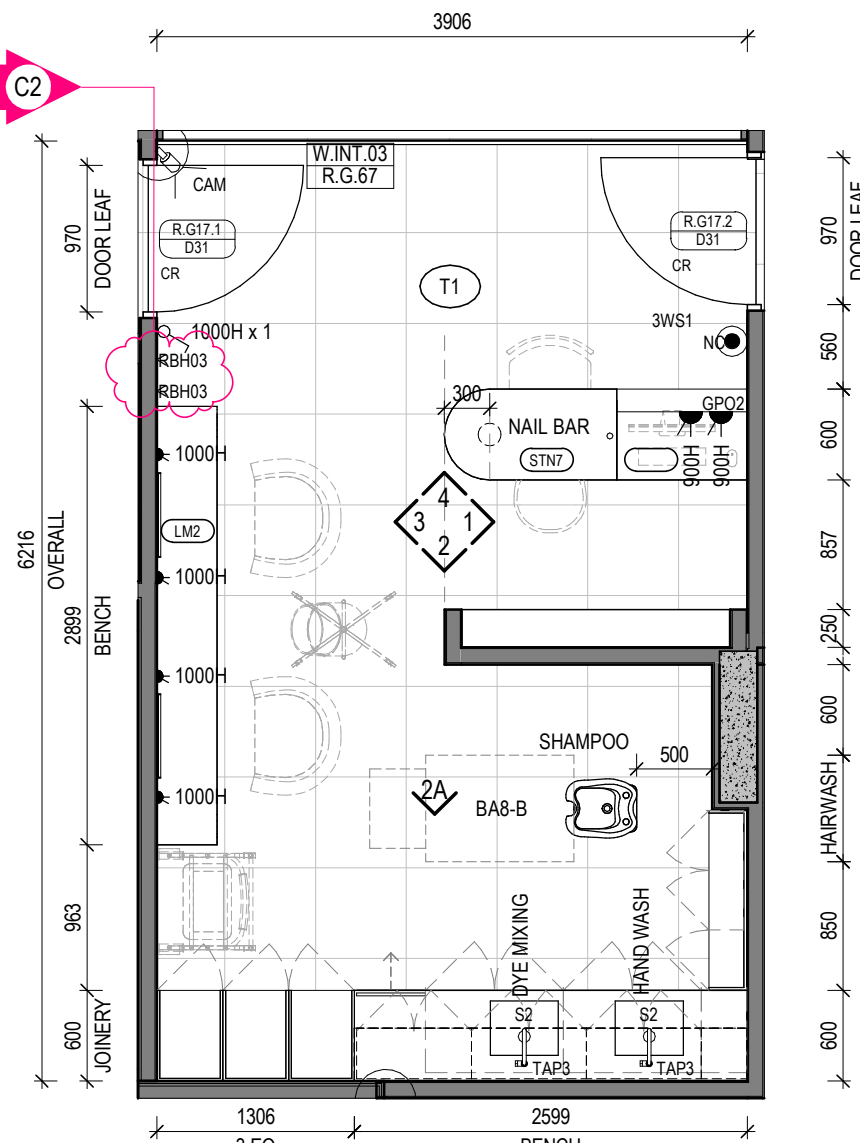

1 VILLAGE HEALTH & WELLNESS - SALON
Scale 1: 50

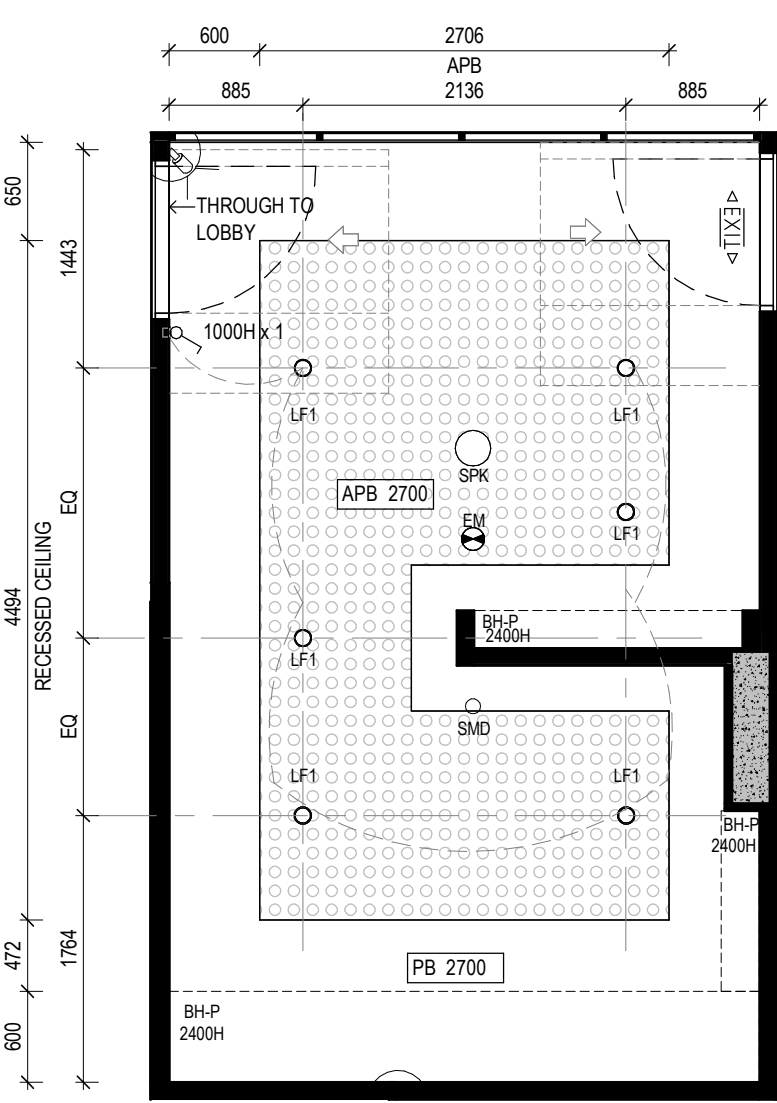


2 RCP - VILLAGE HEALTH & WELLNESS - SALON
Scale 1: 50

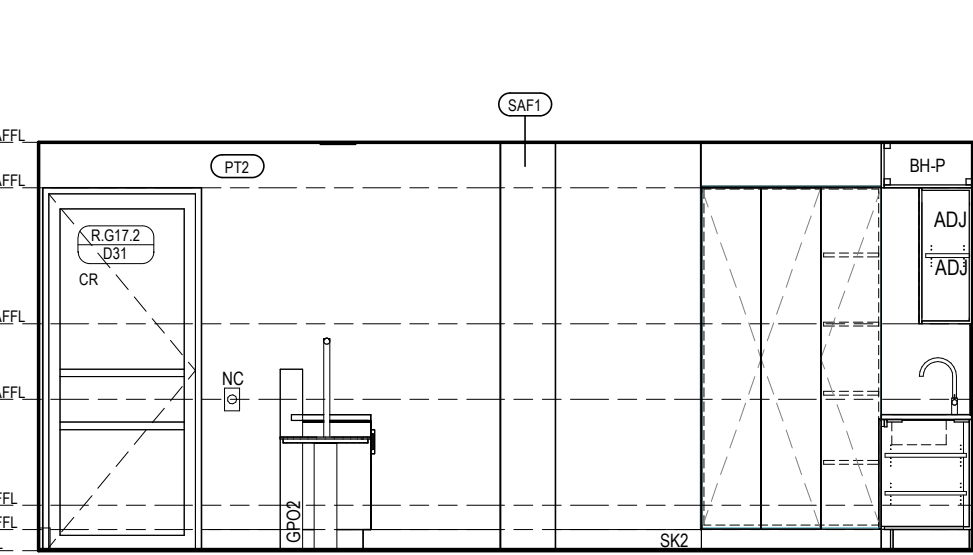


VILLAGE HEALTH & WELLNESS - SALON
ELEVATION 1
Scale 1: 50


UPDATES PER
APR-REV-000133

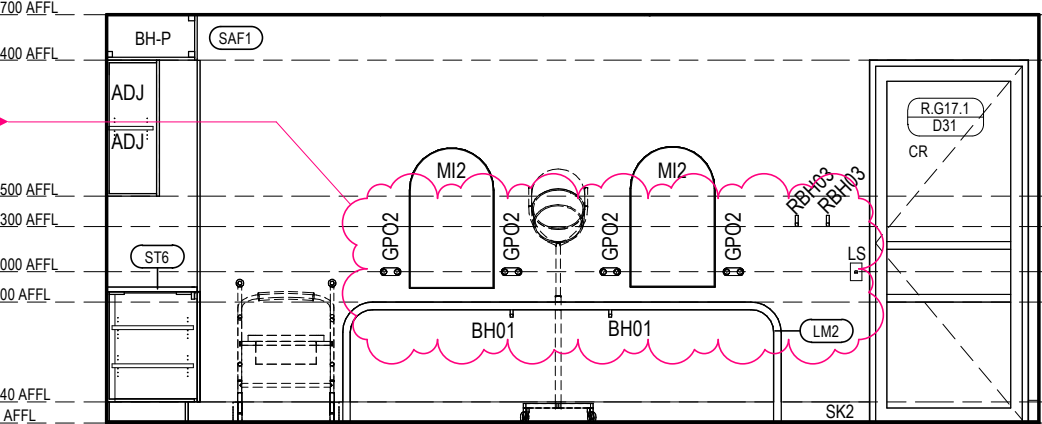


VILLAGE HEALTH & WELLNESS - SALON
ELEVATION 2
Scale 1: 50

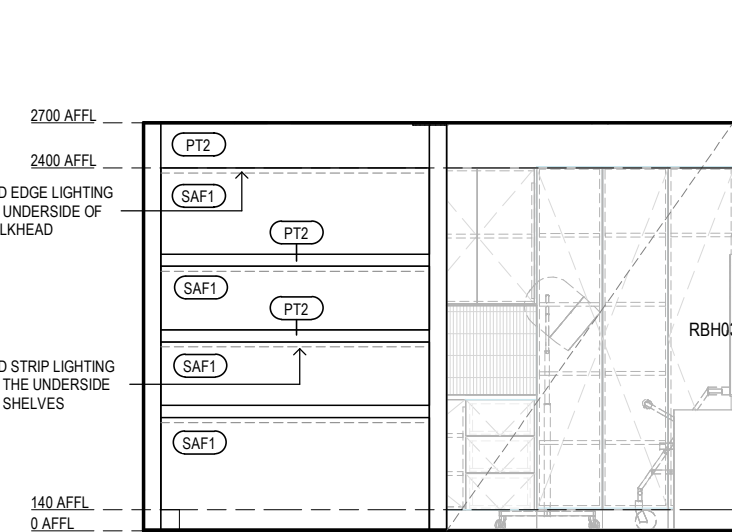

VILLAGE HEALTH & WELLNESS - SALON
ELEVATION 3
Scale 1: 50

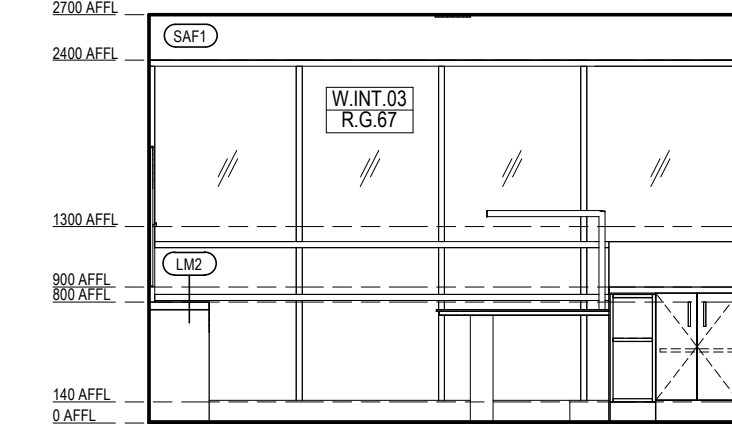

VILLAGE HEALTH & WELLNESS - SALON
ELEVATION 4
Scale 1: 50

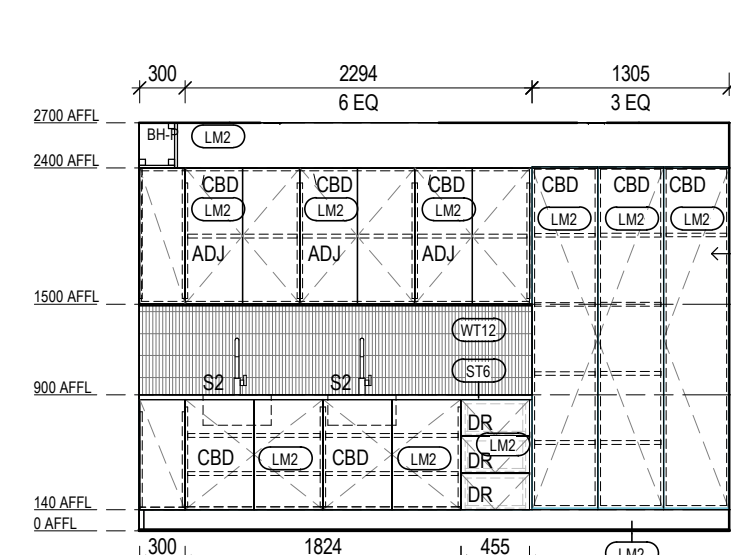

VILLAGE HEALTH & WELLNESS - SALON
ELEVATION 2A
Scale 1: 50

Legend - Internal Elevations

DRAWINGS TO BE READ IN CONJUNCTION WITH ARCHITECTURAL SPECIFICATION & MATERIALS, PRODUCTS & FINISHES SCHEDULE.


PTB PAINT FINISH TO ALL WALLS WITHIN NEW & AFFECTED ROOMS/ AREAS UNLESS OTHERWISE SHOWN

- CSE CONCRETE SEALER
- DPR DOOR PROTECTION
- GD GRAPHIC FILM
- LM LAMINATE
- MI MIRROR
- PBD PINBOARD
- PT PAINT FINISH
- REN RENDER FINISH
- SB SPLASHBACK
- ST STONE
- WB WHITEBOARD
- WP WALL PROTECTION
- WT WALL TILE
- WV WALL VINYL
- UPH UPHOLSTERY


NOTES:
1. LAMINATE CARCASS FOR ALL VISIBLE OPEN SHELVING, UNLESS OTHERWISE NOTED
2. MELAMINE TO ALL INTERNAL CARCASS OF JOINERY, UNLESS OTHERWISE NOTED.

Legend - Floor Finishes


- C CARPET
- CO CONCRETE
- E EPOXY FINISH
- L LINOLEUM
- M MATTING
- PU PAVING UNIT - TBC WITH LANDSCAPE
- R RUBBER FLOORING
- T TILING
- TF TIMBER FLOORING
- V VINYL
- LVT LUXURY VINYL TILE PLANK

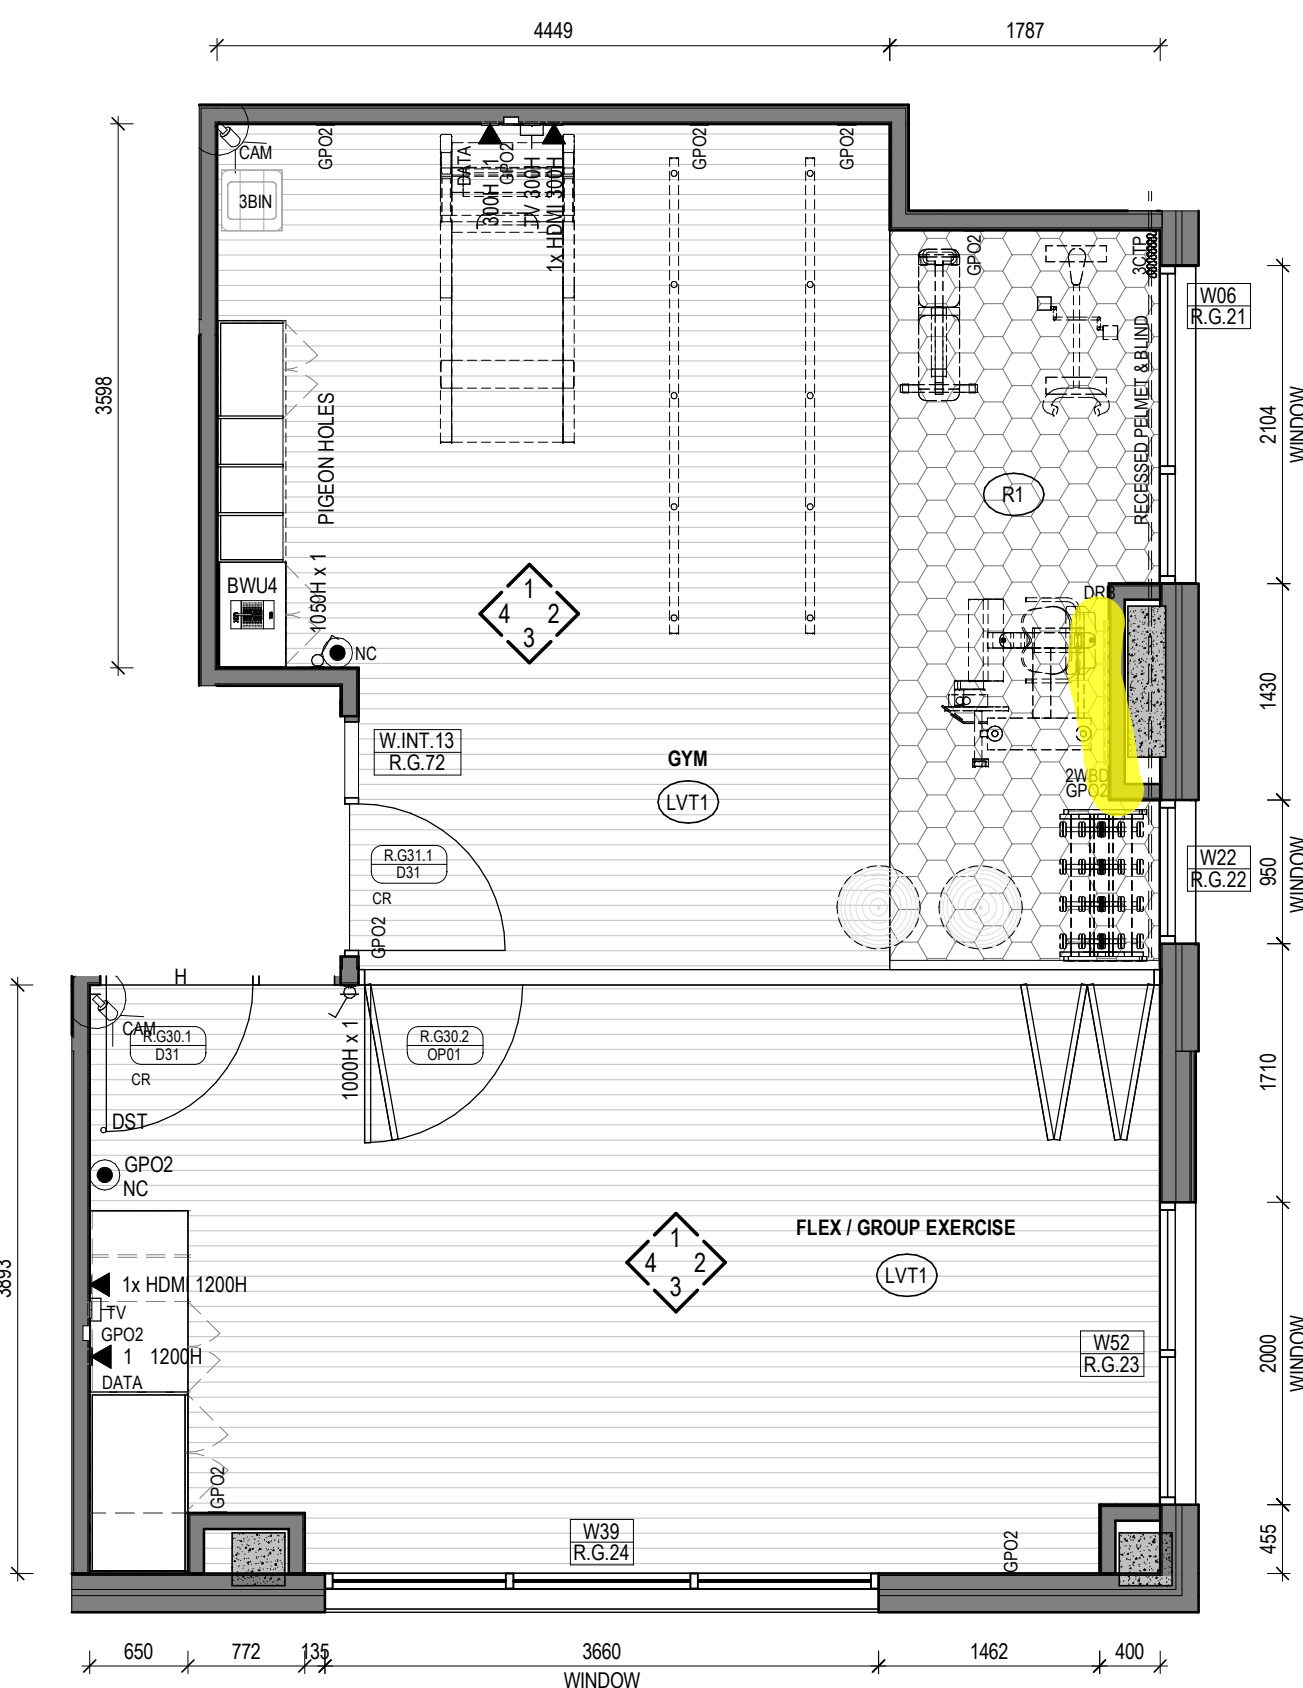


5 VILLAGE HEALTH & WELLNESS - GYM
Scale 1: 50

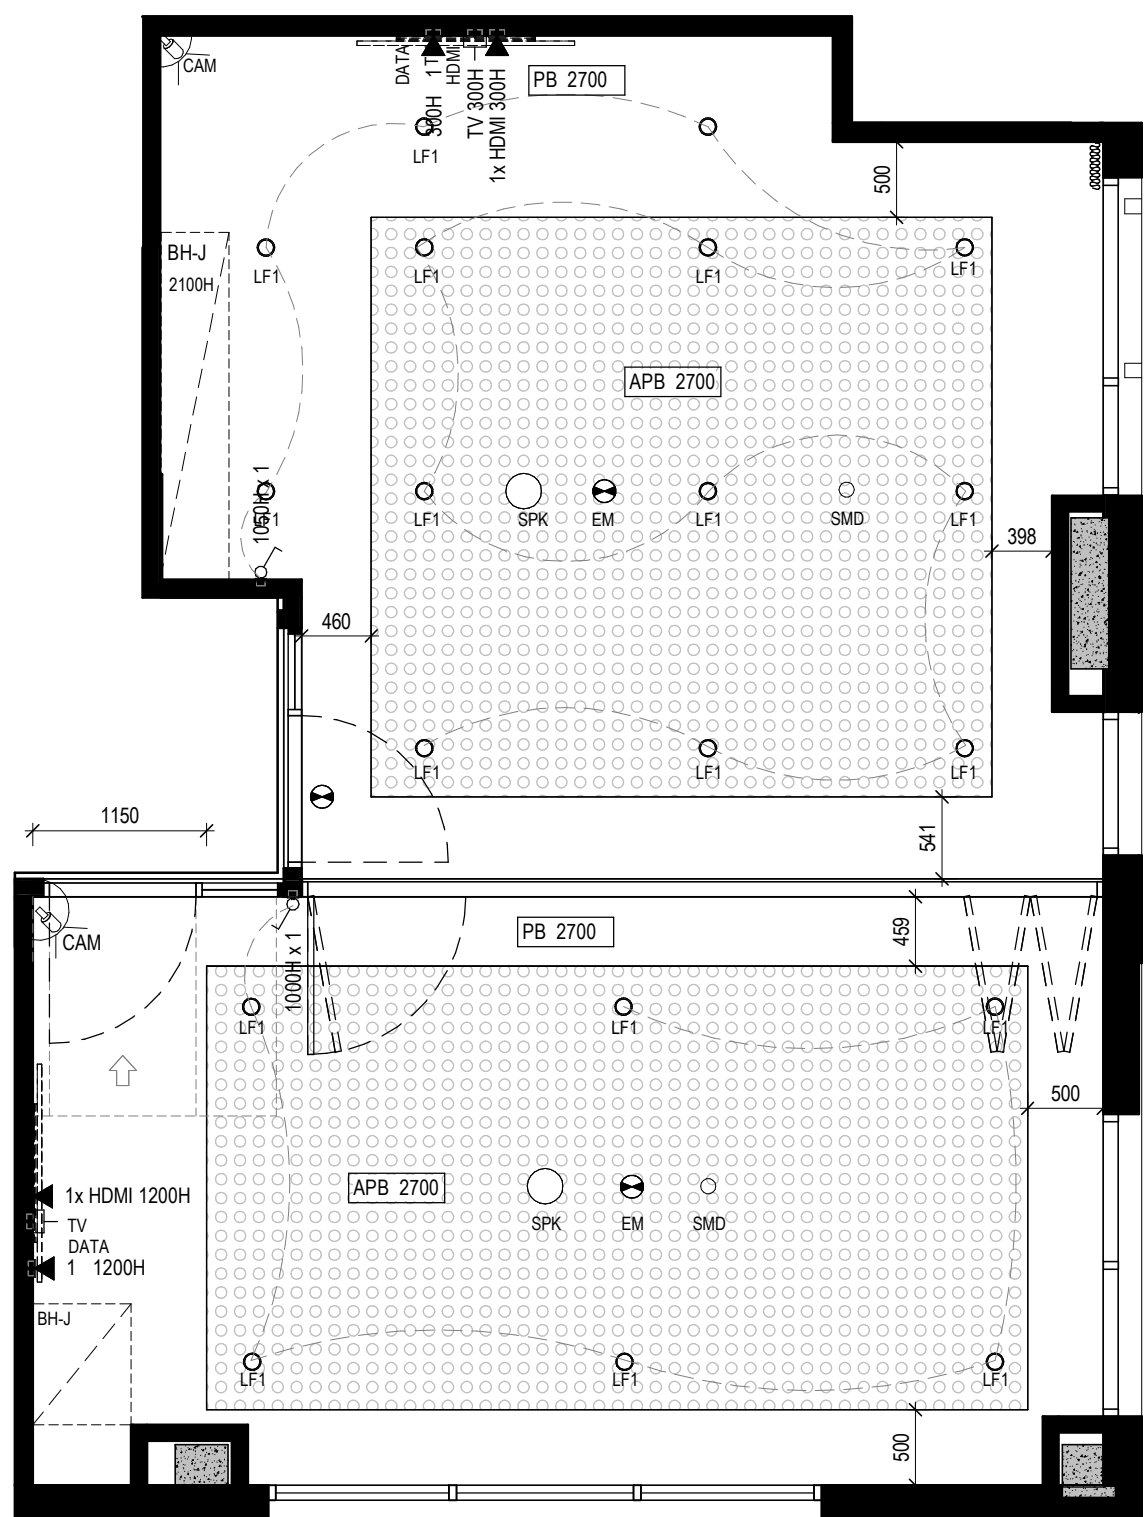


6 RCP - VILLAGE HEALTH & WELLNESS - GYM
Scale 1: 50

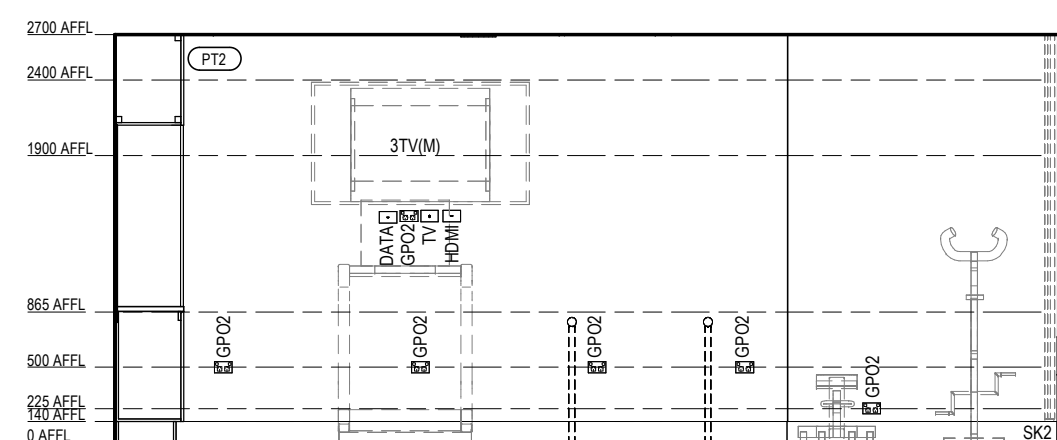


VILLAGE HEALTH & WELLNESS - GYM
ELEVATION 1
Scale 1: 50

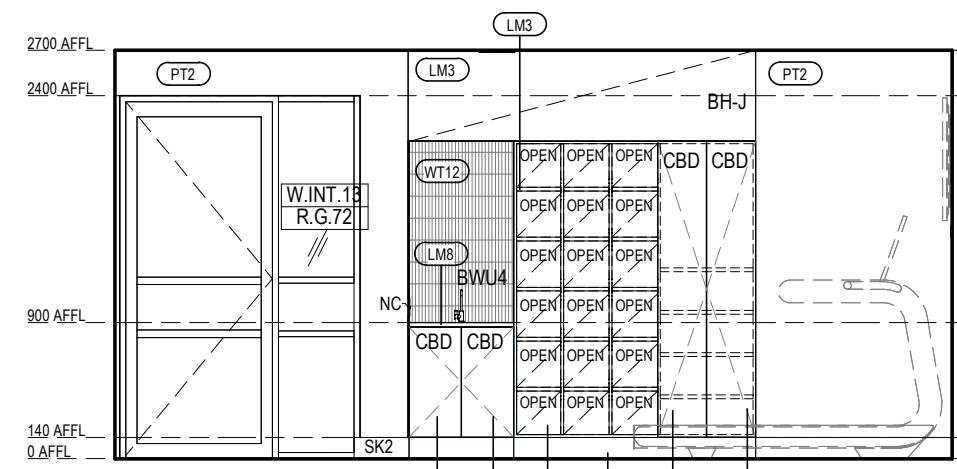


VILLAGE HEALTH & WELLNESS - GYM
ELEVATION 4
Scale 1: 50

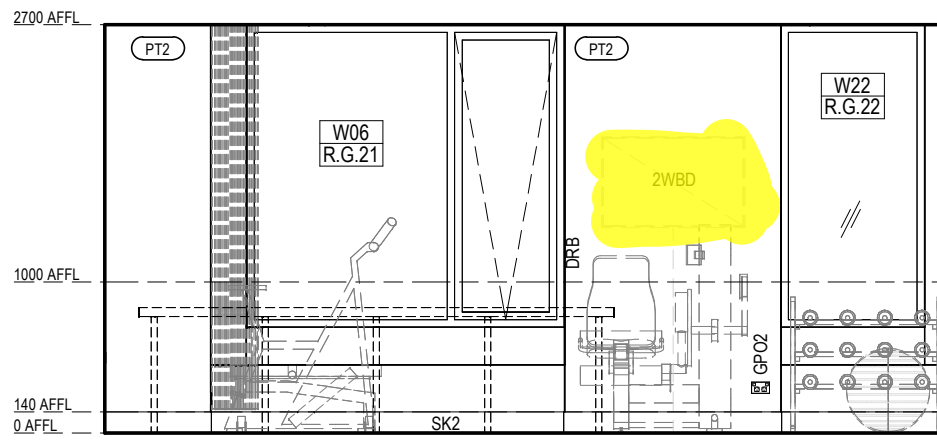


VILLAGE HEALTH & WELLNESS - GYM
ELEVATION 2
Scale 1: 50

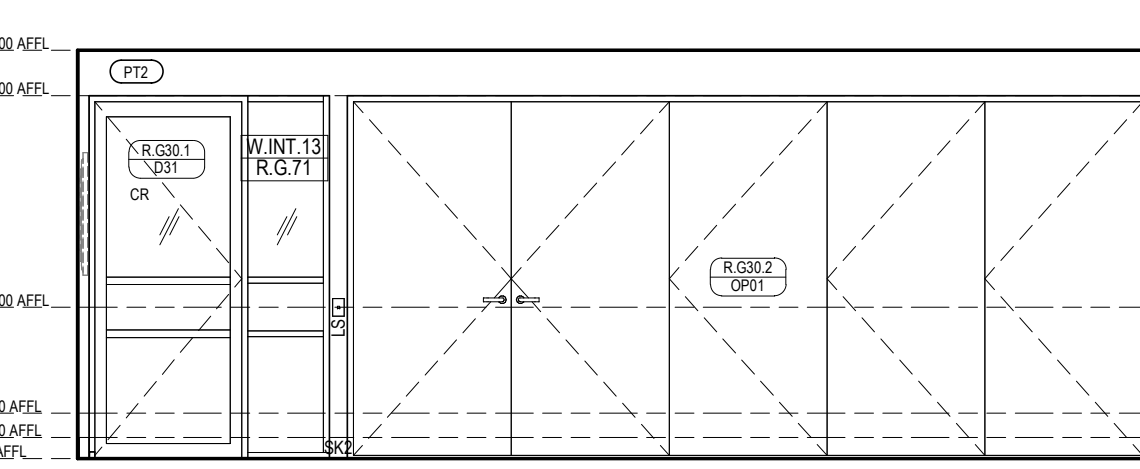


VILLAGE HEALTH & WELLNESS - FLEX
ELEVATION 1
Scale 1: 50

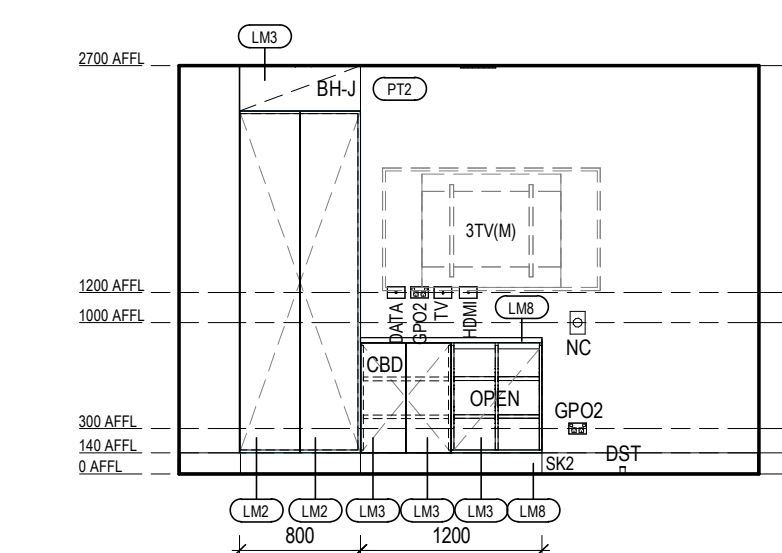

VILLAGE HEALTH & WELLNESS - FLEX
ELEVATION 4
Scale 1: 50

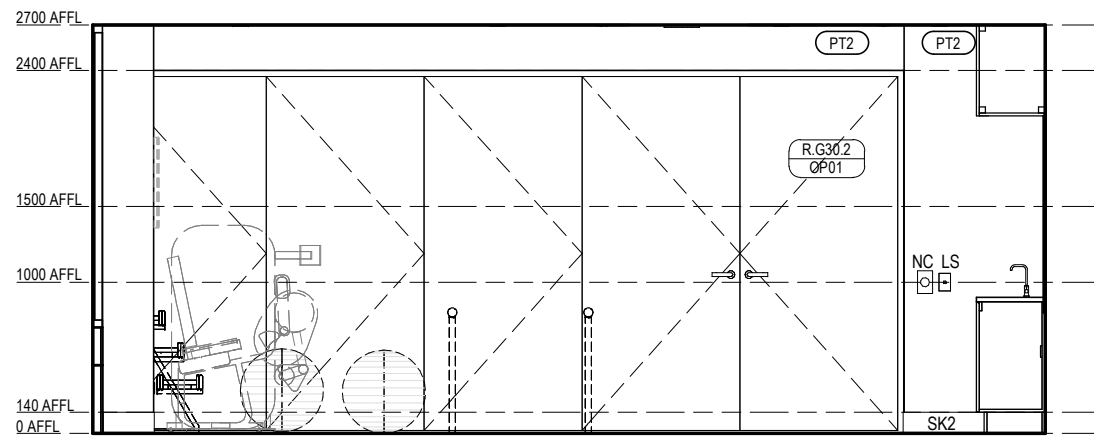

VILLAGE HEALTH & WELLNESS - GYM
ELEVATION 3
Scale 1: 50

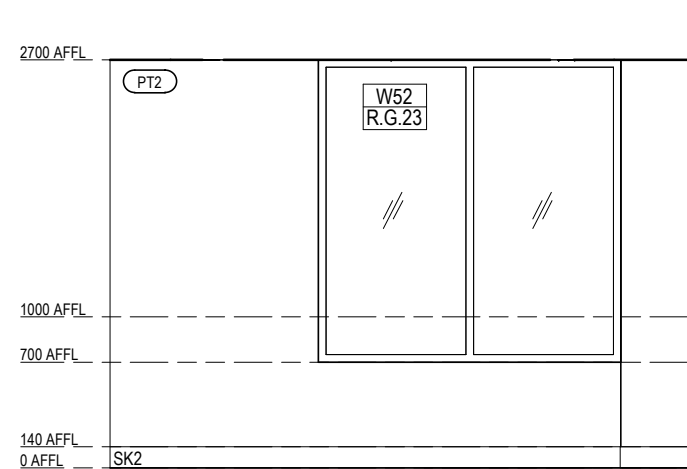

VILLAGE HEALTH & WELLNESS - FLEX
ELEVATION 2
Scale 1: 50

Keynote Legend

- 2WB0 WHITEBOARD - GROUP 2
- 3B01 WASTE BIN - GROUP 3
- 3CTP CURTAINS - GROUP 3
- 3TV(M) TELEVISION SCREEN 55 INCH - GROUP 3
- 3WS1 WORK STATION - GROUP 3
- ADJ ADJUSTABLE SHELF
- BAB-B BAG HOOK - TYPE 1
- BH01 BULKHEAD - JOINERY TYPE
- BH-P BULKHEAD - PLASTERBOARD TYPE
- BWL4 BOILING WATER UNIT - TYPE 4
- CAM CCTV CAMERA
- CBD CUPBOARD
- DATA DATA OUTLET
- DR DRAWER
- DRB DOOR RELEASE BUTTON
- DST DOOR STOP
- EM EMERGENCY LIGHT
- GPO2 POWER OUTLET - DOUBLE

Keynote Legend

- H HINGED
- HDMI HDMI OUTLET
- LF1 LIGHT FITTING - REFER TO ELECTRICAL ENGINEER SPECIFICATION
- LS LIGHT SWITCH
- M2 MIRROR - TYPE 2
- NC NURSE CALL
- RBH03 ROSE HOOK - TYPE 3
- S2 SINK - TYPE 2
- SK2 SKIRTING - TYPE 2
- SMD SMOKE DETECTOR
- SPK ANNUNCIATOR SPEAKER
- TAP3 TAP - TYPE 3
- TV TELEVISION COAXIAL OUTLET

Revision/Issue	Date
P1 Consolidated Set-to-date / SMG Comments	2025.08.15
P2 ISSUE FOR CONTRACT	2025.10.10
C1 ISSUE FOR CONSTRUCTION - INTERIORS	2026.03.26
C2 ISSUE FOR CONSTRUCTION - RFI RESPONSE	2026.06.17

Clarke Hopkins Clarke

Melbourne | Wurundjeri

700 Swanston Street
Carlton VIC 3063
Telephone (03) 9419 4340
Email studio@chc.com.au
www.chc.com.au

Sydney | Gadigal Country

Suite 3, Ground Floor
91 Campbell Street
Surry Hills NSW 2010
Telephone (02) 9221 9200
Email studio@chc.com.au
www.chc.com.au

Scale	1: 50 @ A1
Date	01/03/2024
Drawn	EL / DP
Architect	EL

Project
Summerset Oakleigh
52 Golf Road, Oakleigh South, VIC

Drawing
Internal Elevations - Village Health & Wellness - Salon & Gym

Drawing No.
230185/A1810
C2

FOR CONSTRUCTION