



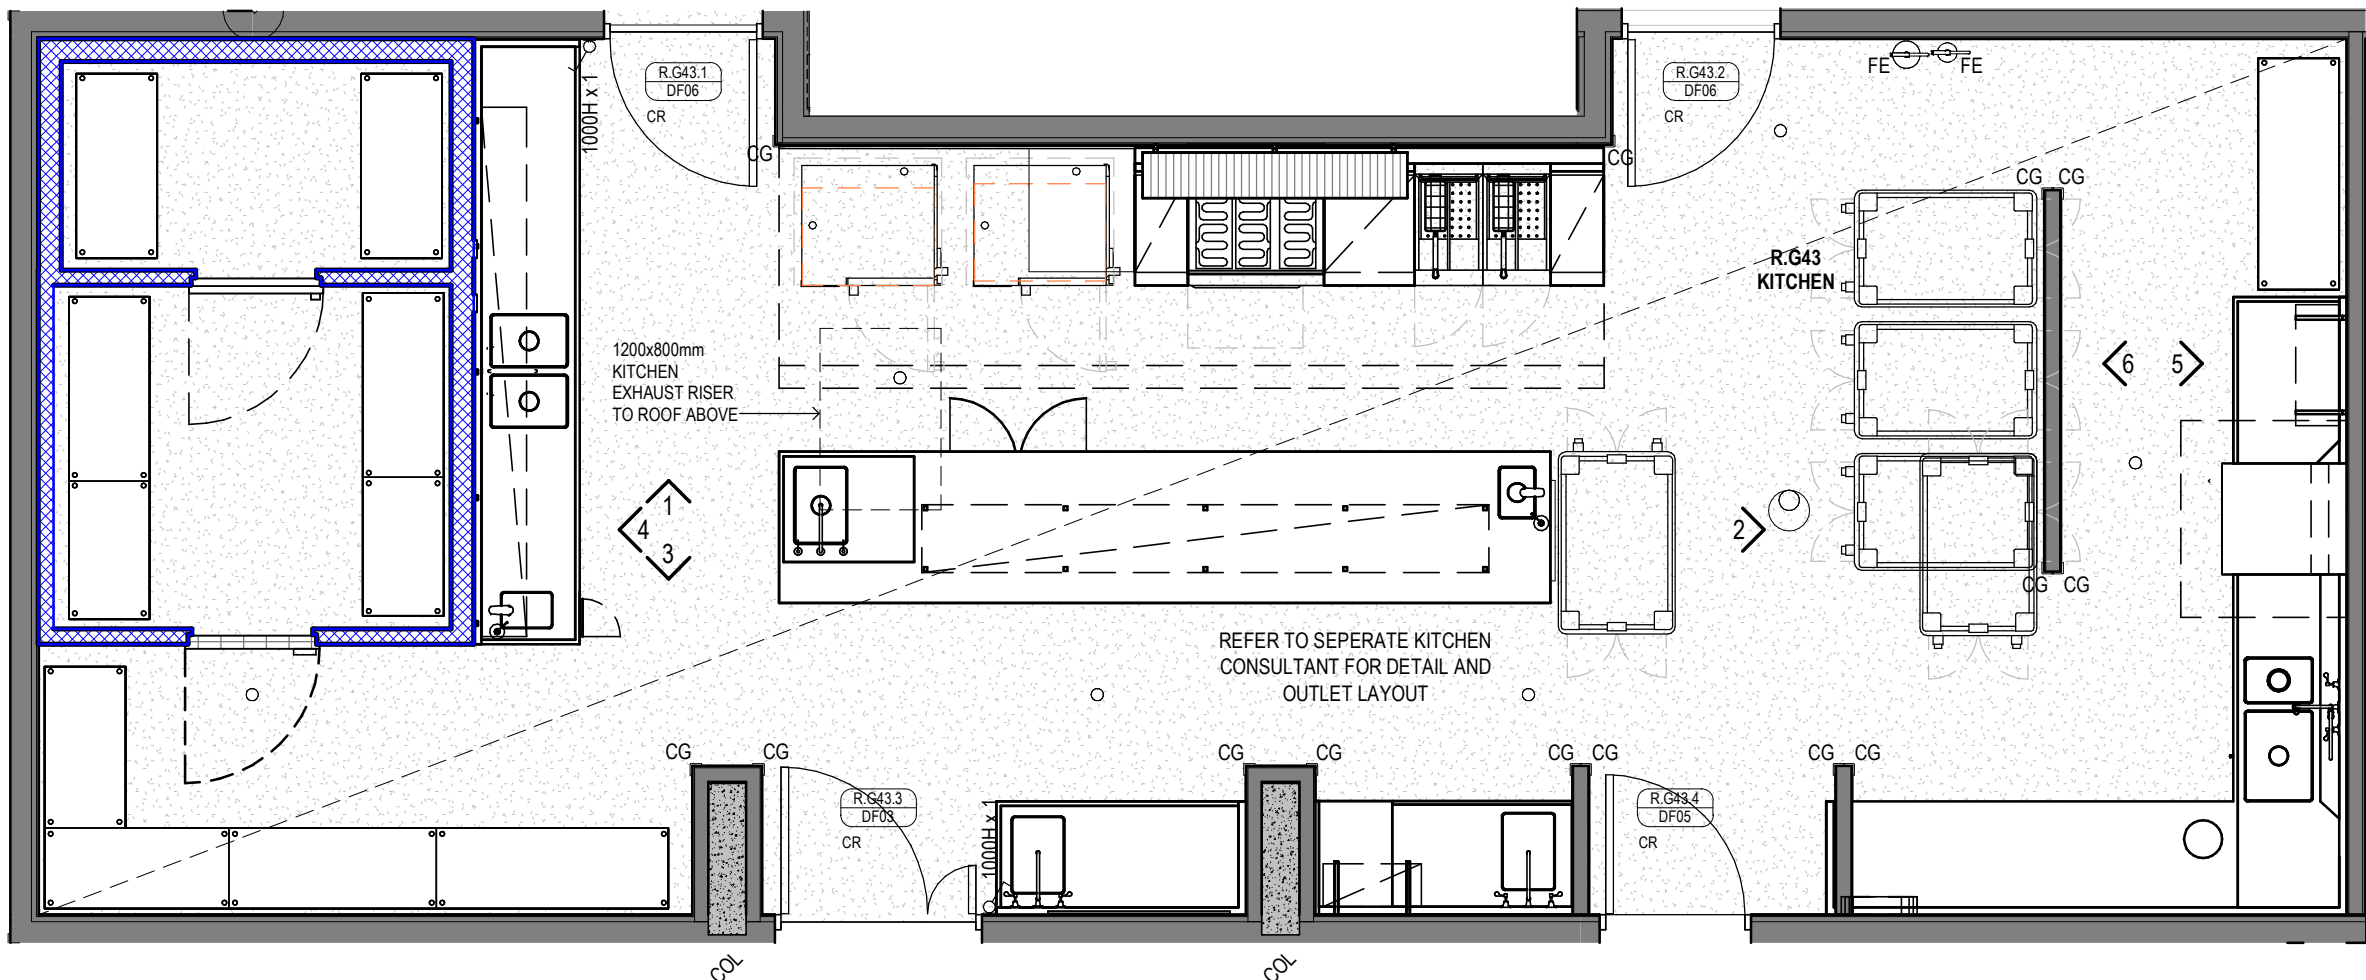


Note
Any refrigerated or cooling chambers which are of sufficient size for a person to enter shall be provided with:
(a) A door which is capable of being opened by hand from the inside without a key; and
(b) Internal lighting controlled only by a switch which is located adjacent to the entrance doorway inside the chamber; and
(c) An indicator lamp positioned outside the chamber, which is illuminated when the interior lights required by (b) are switched on; and
(d) An alarm that is:
i. located outside but controlled only from within the chamber, and
ii. able to achieve a sound pressure level outside the chamber of 90 dB(A) when measured 3m from the sounding device.
Doors to refrigerated rooms and cool rooms shall have a clear width of not less than 600mm and a clear height of not less than 1.5m

1 MAIN KITCHEN
Scale 1: 50

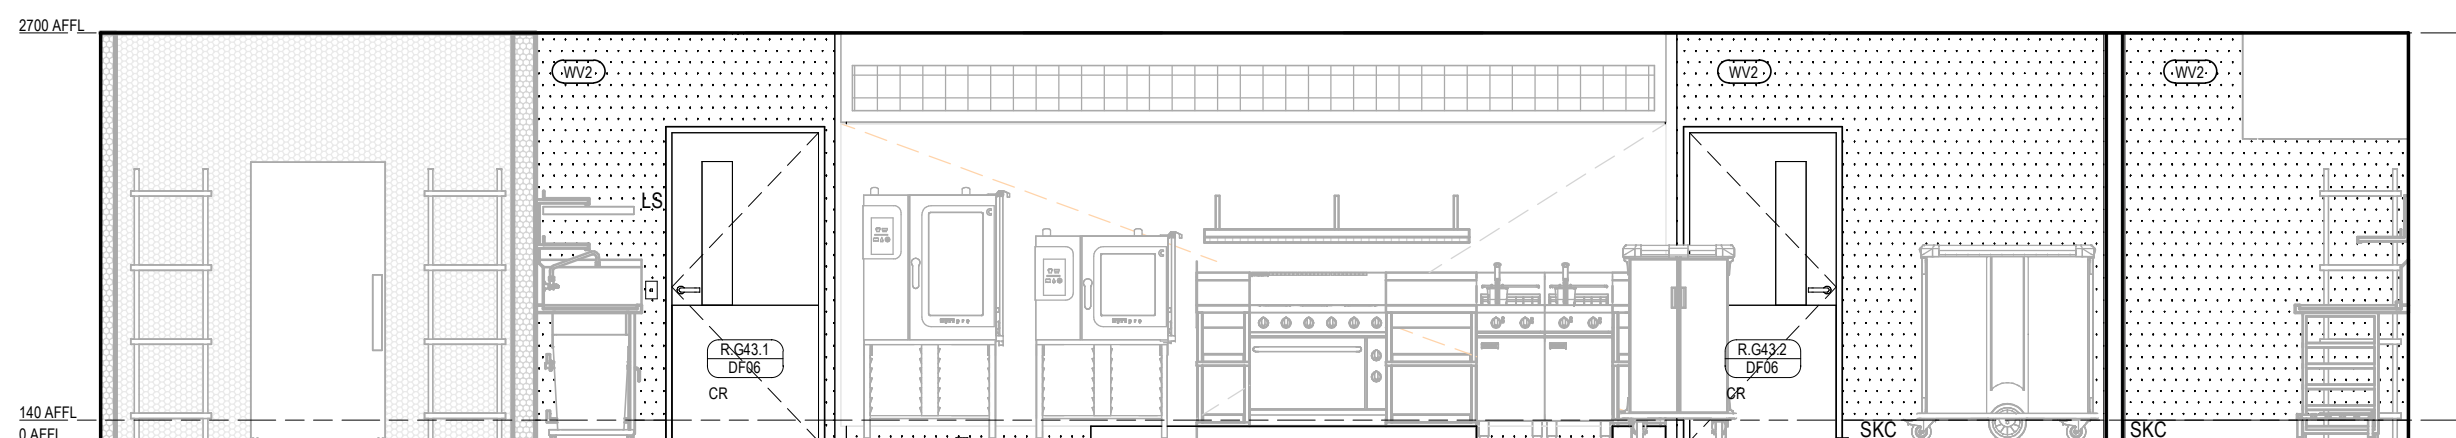


MAIN KITCHEN
ELEVATION 1
Scale 1: 50

NOTE: REFER KITCHEN CONSULTANT FOR FURTHER EQUIPMENT DETAIL.
REFER KITCHEN CONSULTANT & ELECTRICAL FOR OUTLET LAYOUT

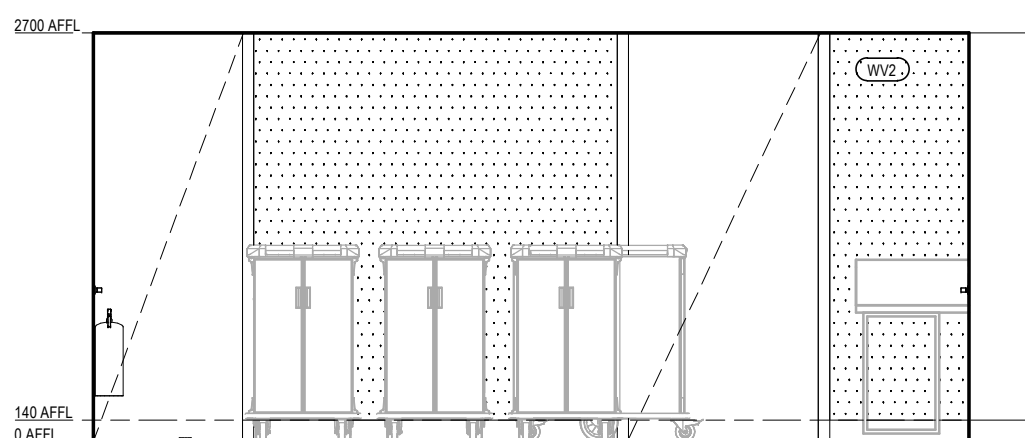


MAIN KITCHEN
ELEVATION 2
Scale 1: 50

NOTE: REFER KITCHEN CONSULTANT FOR FURTHER EQUIPMENT DETAIL.
REFER KITCHEN CONSULTANT & ELECTRICAL FOR OUTLET LAYOUT

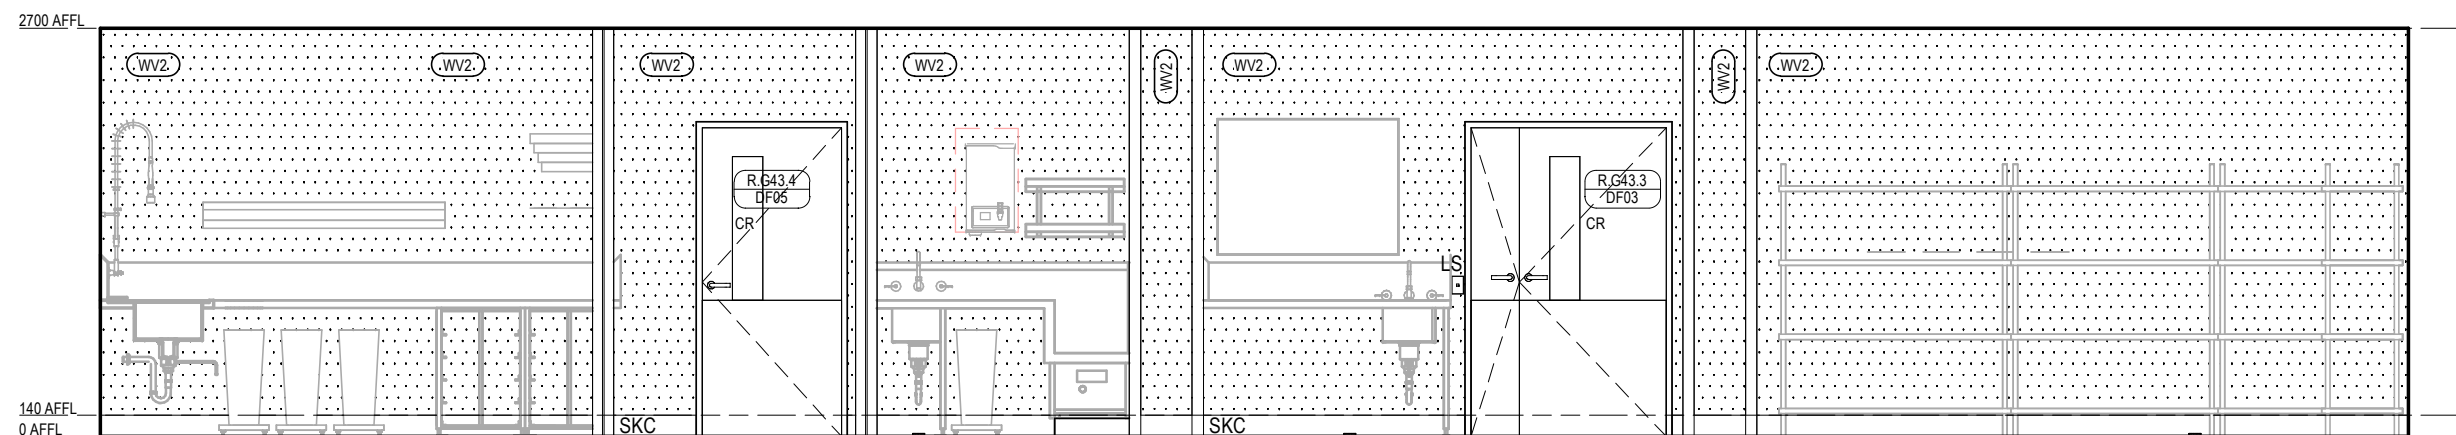


MAIN KITCHEN
ELEVATION 3
Scale 1: 50

NOTE: REFER KITCHEN CONSULTANT FOR FURTHER EQUIPMENT DETAIL.
REFER KITCHEN CONSULTANT & ELECTRICAL FOR OUTLET LAYOUT

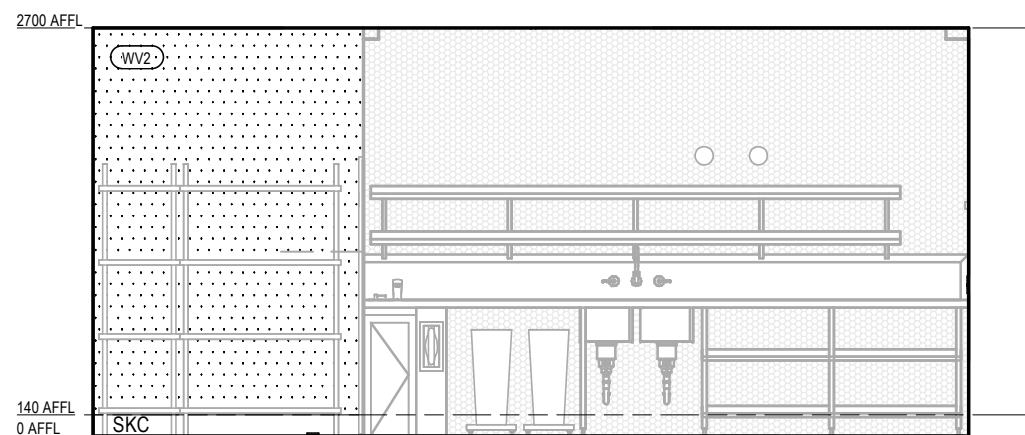


MAIN KITCHEN
ELEVATION 4
Scale 1: 50

NOTE: REFER KITCHEN CONSULTANT FOR FURTHER EQUIPMENT DETAIL.
REFER KITCHEN CONSULTANT & ELECTRICAL FOR OUTLET LAYOUT

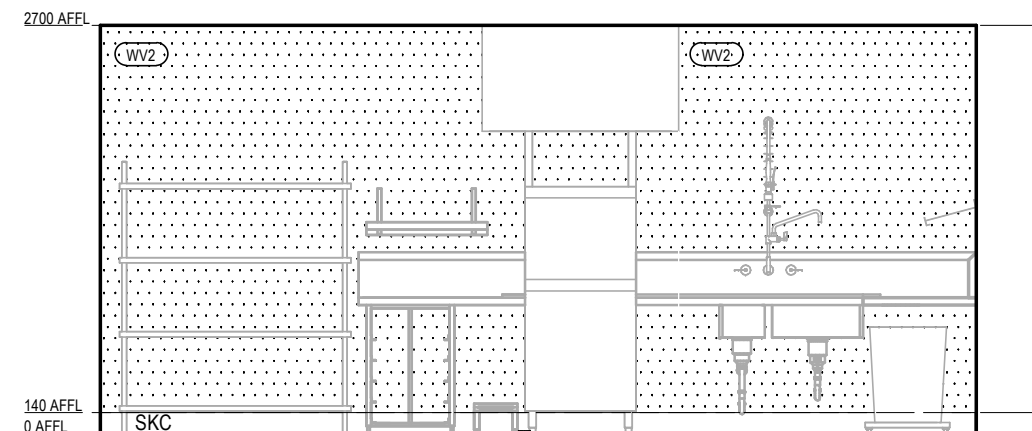


MAIN KITCHEN
ELEVATION 5
Scale 1: 50

NOTE: REFER KITCHEN CONSULTANT FOR FURTHER EQUIPMENT DETAIL.
REFER KITCHEN CONSULTANT & ELECTRICAL FOR OUTLET LAYOUT

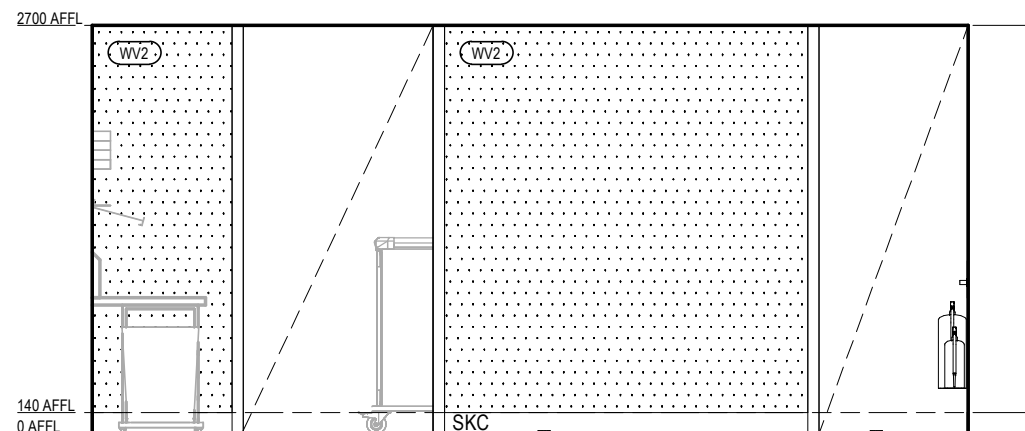


MAIN KITCHEN
ELEVATION 6
Scale 1: 50


NOTE: REFER KITCHEN CONSULTANT FOR FURTHER EQUIPMENT DETAIL.
REFER KITCHEN CONSULTANT & ELECTRICAL FOR OUTLET LAYOUT

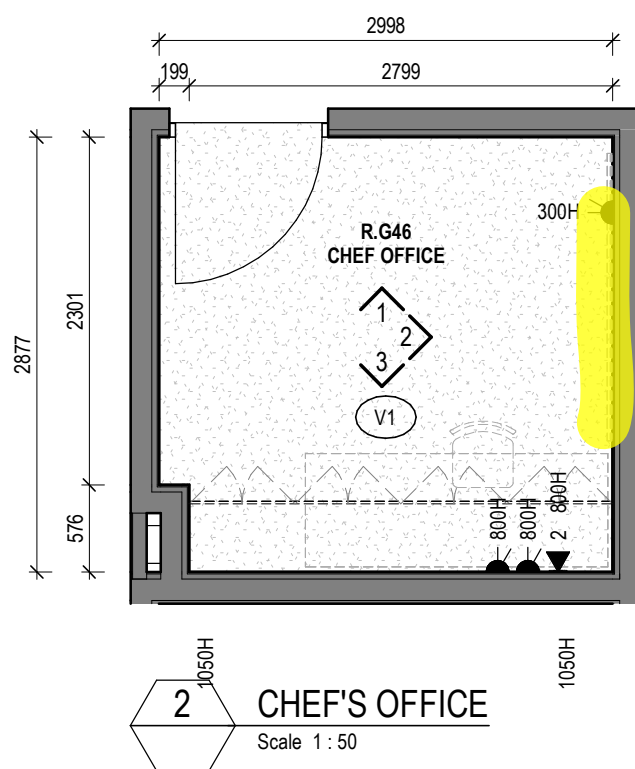


2 CHEF'S OFFICE
Scale 1: 50

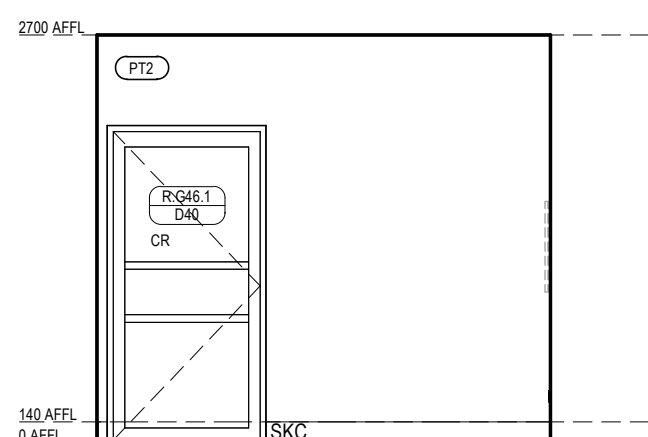

CHEF'S OFFICE
ELEVATION 1
Scale 1: 50

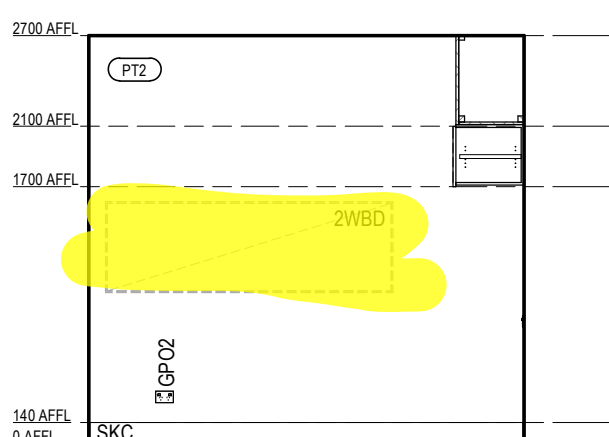

CHEF'S OFFICE
ELEVATION 2
Scale 1: 50

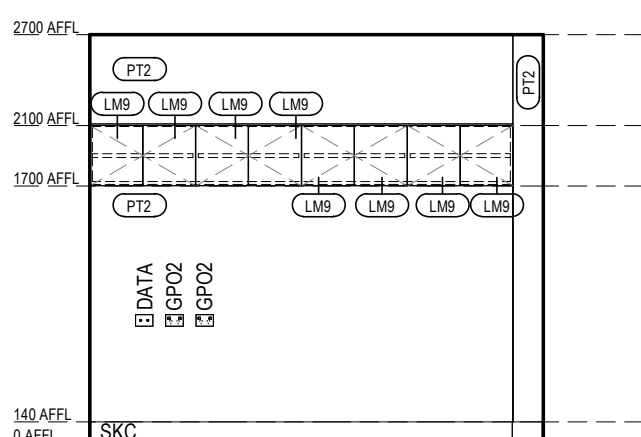

CHEF'S OFFICE
ELEVATION 3
Scale 1: 50

Legend - Internal Elevations

DRAWINGS TO BE READ IN CONJUNCTION WITH ARCHITECTURAL SPECIFICATION & MATERIALS, PRODUCTS & FINISHES SCHEDULE.

PT# PAINT FINISH TO ALL WALLS WITHIN NEW & AFFECTED ROOMS/ AREAS UNLESS OTHERWISE SHOWN

- CSE CONCRETE SEALER
- DPR DOOR PROTECTION
- GD GRAPHIC FILM
- LM LAMINATE
- MI MIRROR
- PBD PINBOARD
- PT PAINT FINISH
- REN RENDER FINISH
- SB SPLASHBACK
- ST STONE
- WB WHITEBOARD
- WP WALL PROTECTION
- WT WALL TILE
- WV WALL VINYL

NOTES:
1. LAMINATE CARCASS FOR ALL VISIBLE OPEN SHELVING, UNLESS OTHERWISE NOTED.
2. MELAMINETO ALL INTERNAL CARCASS OF JOINERY, UNLESS OTHERWISE NOTED.

Legend - Floor Finishes

- C CARPET
- CO CONCRETE
- E EPOXY FINISH
- L LINOLEUM
- M MATTING
- PU PAVING UNIT - TBC WITH LANDSCAPE
- R RUBBER FLOORING
- T TILING
- TF TIMBER FLOORING
- V VINYL
- LVT LUXURY VINYL TILE PLANK

Keynote Legend

- ZWB1 WHITEBOARD - GROUP 1
- ZWB2 WHITEBOARD - GROUP 2
- CG CORNER GAUGE
- COL COLUMN
- DATA DATA
- FE FIRE EXTINGUISHER
- GP02 POWER OUTLET - DOUBLE
- LS LIGHT SWITCH
- SK SKIRTING - COVED

FOR CONSTRUCTION

Revision/Issue
C1 ISSUE FOR CONSTRUCTION - INTERIORS
Date
2026.03.26

Clarke
Hopkins
Clarke

ClarkeHopkinsClarke

Melbourne | Wurundjeri
L3, Melbourne Connect
700 Swanston Street
Carlton VIC 3063
Telephone (03) 9419 4340
Email studio@chc.com.au
www.chc.com.au

Sydney | Gadigal Country
Suite 3, Ground Floor
91 Campbell Street
Sunny Hills NSW 2010
Telephone (02) 9221 9200
Email studio@chc.com.au
www.chc.com.au

Scale
Date
Drawn
Architect
As indicated @ A1
01/03/2024
TM
EL

Project
Summerset Oakleigh
52 Golf Road, Oakleigh South, VIC

Drawing
Internal Elevations - RACF BOH - MAIN
KITCHEN

Drawing No.
230185/A1822
C1