

General Notes

BUILDER TO VIEW THE SITE DURING THE TENDER PERIOD TO SATISFY THEMSELVES OF THE LATENT SITE CONDITIONS AND FULL EXTENT OF WORK AS REQUIRED TO ALLOW FOR THE COMPLETION OF ALL WORKS AS DETAILED IN ALL DOCUMENTATION.

ALL DOCUMENTS ARE TO BE REVIEWED IN CONJUNCTION WITH RELEVANT CONSULTANTS DRAWINGS AND SPECIFICATIONS.

CONTRACTOR TO USE 92MM METAL STUD FRAMING UNLESS NOTED OTHERWISE. REFER TO ACOUSTIC REPORT AND FIRE/SMOKE COMPARTMENT PLANS FOR WALLS THAT EXTEND TO UNDERSIDE OF SLAB AND ROOF SHEETING.

ALLOW FOR WALL STRENGTHENING BEHIND WALL MOUNTED FIXTURES AND FITTINGS INCLUDING BUT NOT LIMITED TO GRABRAILS, HANDRAILS, EQUIPMENT HOOKS, DRUG SAFES.

ALL FIRE, SMOKE, ACOUSTIC WALLS, CORRIDOR WALLS TO BEDROOMS AND APARTMENTS ARE FULL HEIGHT TO UNDERSIDE OF SLAB OR SHEET METAL ROOF.

IMPACT RESISTANT PLASTERBOARD TO BE INSTALED FROM 0 AFFL TO 1200 AFFL (TYPICALLY TO ALL STORES AND CORRIDORS)
ONLY CORRIDORS WITHOUT DADO PANELS REQUIRE IMPACT RESISTANT PLASTERBOARD

ALLOW FOR FURRING CHANNELS AND LINING TO ALL CONCRETE COLUMNS. LINING TO MATCH WITH LINING OF ASSOCIATED ROOM.

Legend - General

	WALL TYPE - REFER TO WALL SET-OUT PLANS & WALL TYPES SHEET FOR DETAILS
	RELATIVE LEVEL
	PROPOSED FINISH LEVEL


ABBREVIATIONS

BAL1	BALUSTRADE - TYPE 1
BAL2	BALUSTRADE - TYPE 2
BAL3	BALUSTRADE - TYPE 3
COL	COLUMN
COL-S	STEEL COLUMN
DPI	DOWNPIPE - TYPE 1
EG1	EAVES GUTTER - TYPE 1
FE	FIRE EXTINGUISHER
FE-JC	FIRE EXTINGUISHER IN JOINERY CUPBOARD
FH	FIRE HYDRANT
FLA	FLASHING
FW3	FLOOR WASTE - TYPE 3
FW4	FLOOR WASTE - TYPE 4
RHYD	HYDRAULIC RISER

Description	Quantity	Unit
Picture rail	132.37	m

Legend

Description	Quantity	Unit
Picture rail	132.37	m

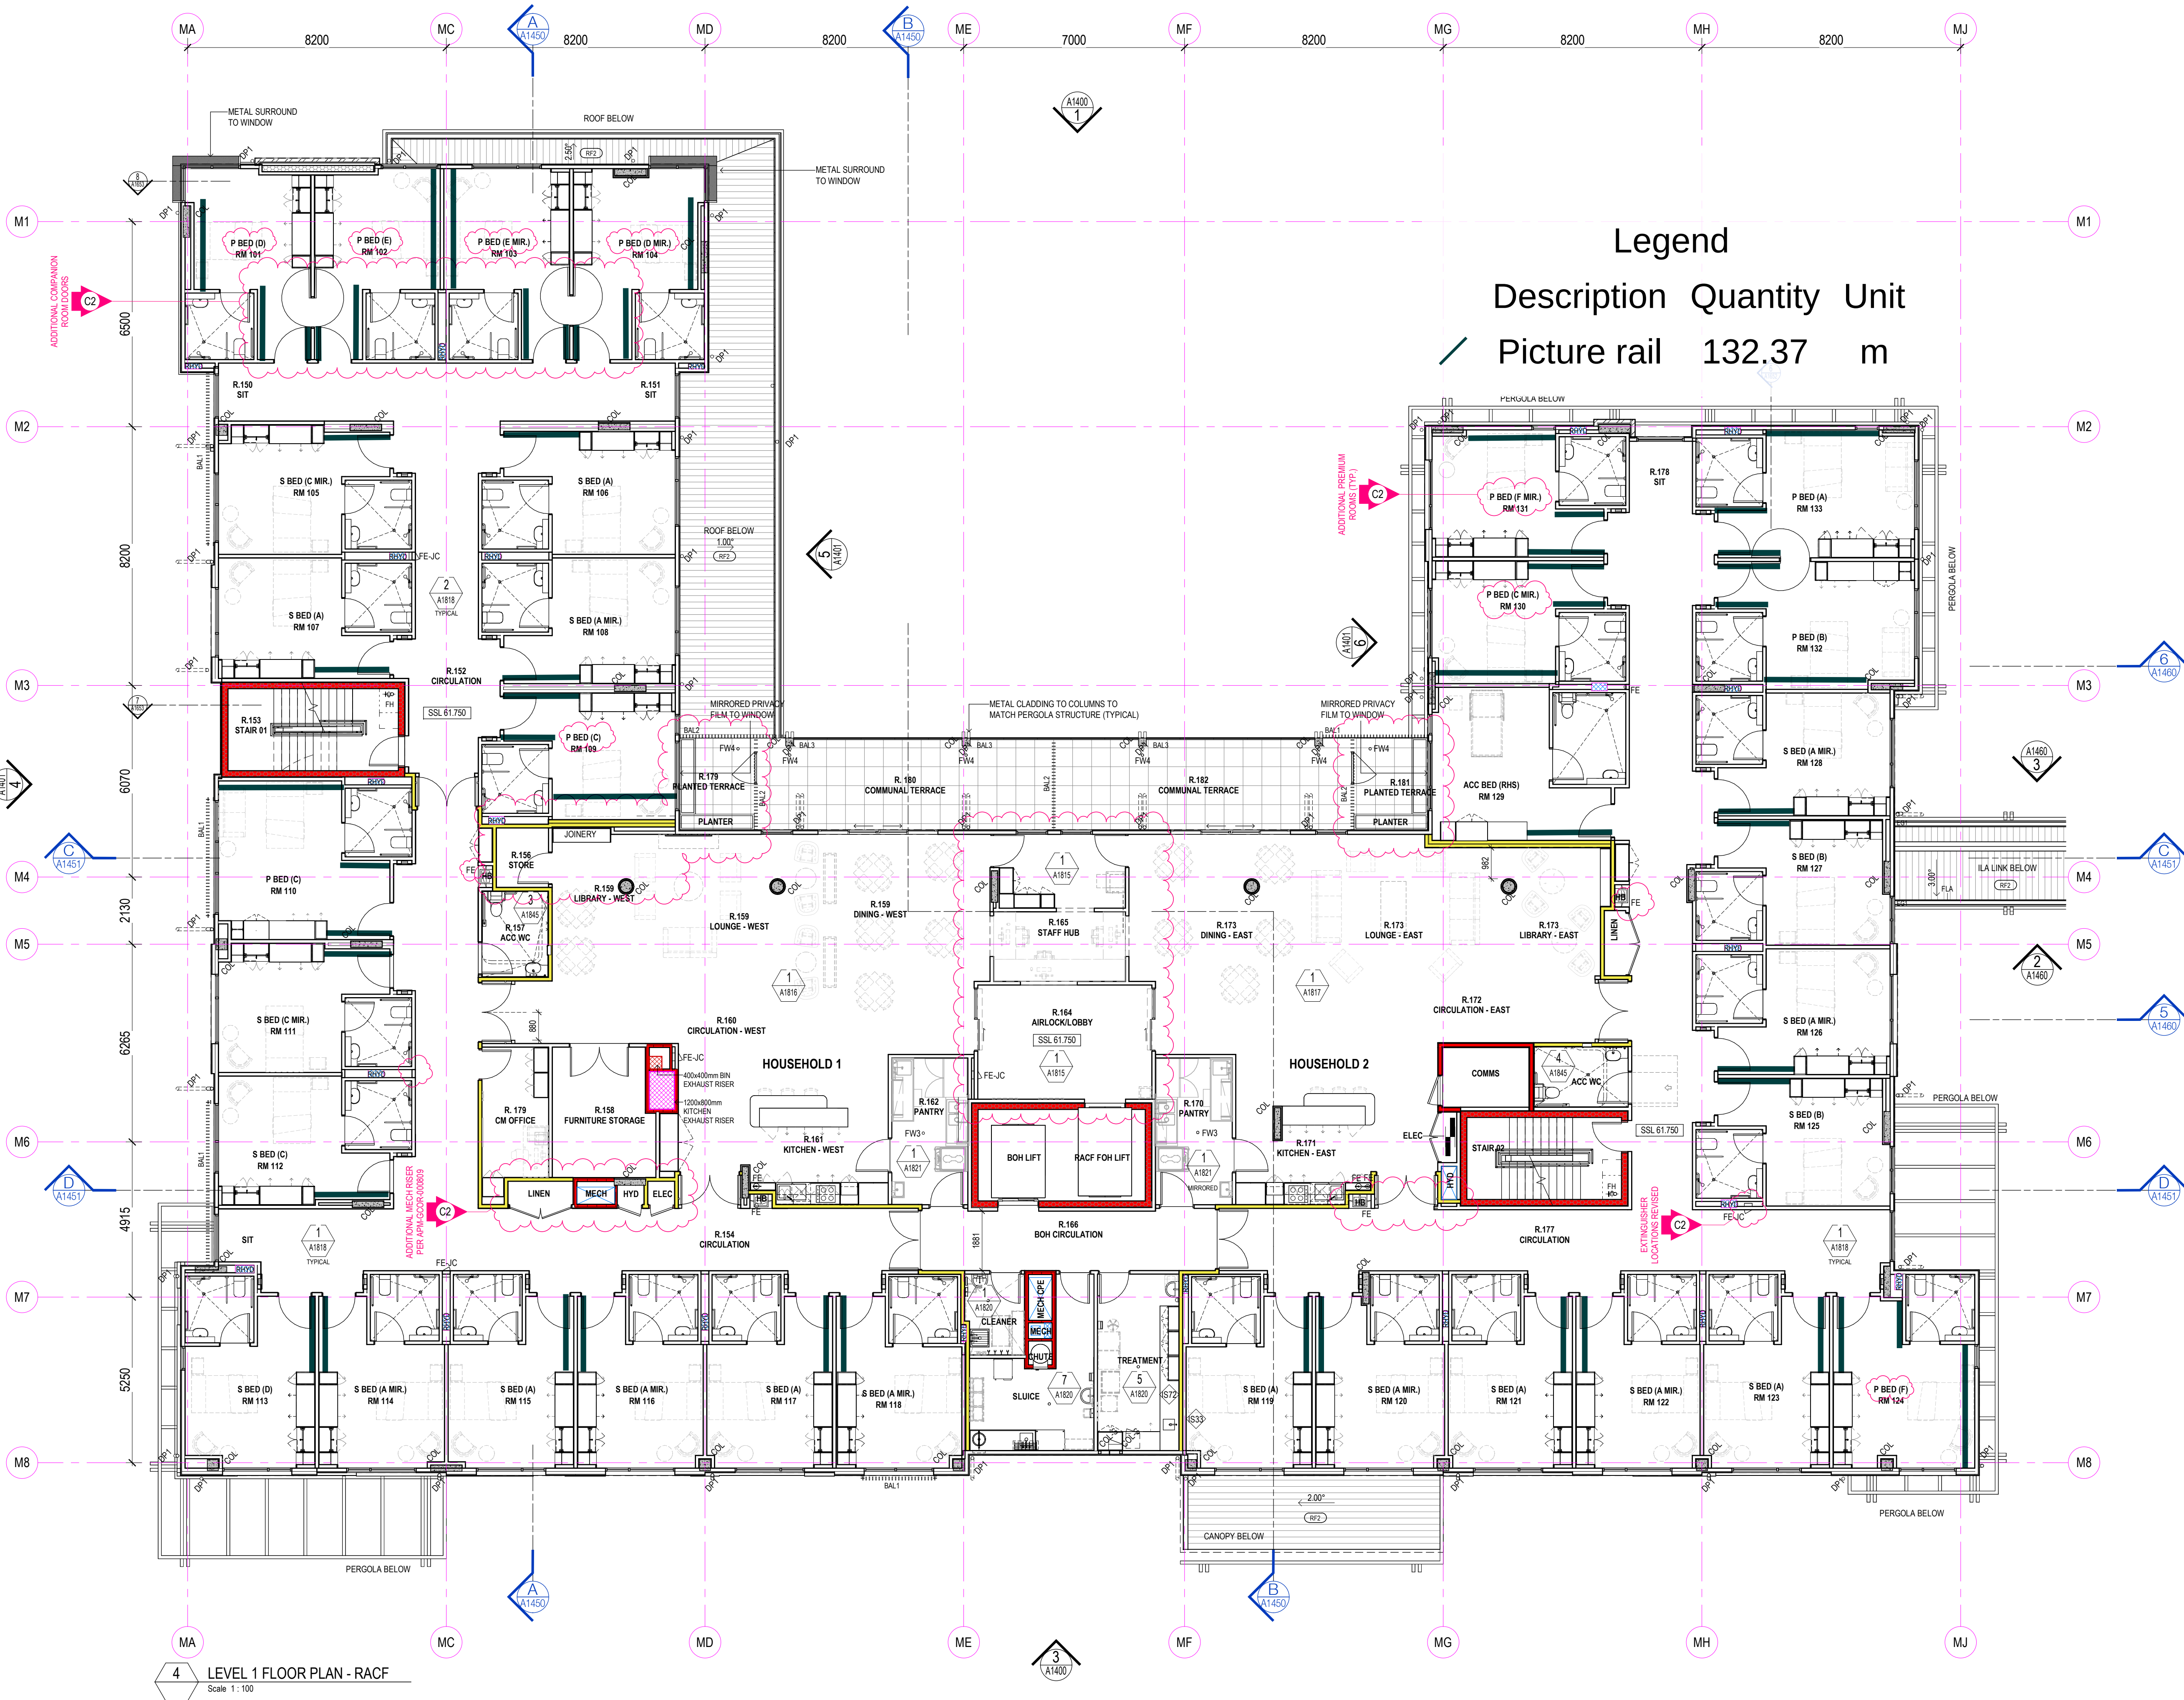

Revision/Issue	Date
P7 Consolidated Set-to-date / SMG Comments	2025.08.15
P8 Tender Pack - Doors and Windows	2025.09.15
P9 ISSUE FOR CONTRACT	2025.10.10
C1 ISSUE FOR CONSTRUCTION	2025.12.19
C2 ISSUE FOR CONSTRUCTION	2026.03.24

Clarke
Hopkins
Clarke

ClarkeHopkinsClarke
Melbourne | Wurundjeri
L9, Melbourne Connect
700 Swanston Street
Carlton VIC 3063
Telephone (03) 9419 4340
Email studio@chc.com.au
www.chc.com.au

Sydney | Gadigal Country
Suite 3, Ground Floor
91 Campbell Street
Surry Hills NSW 2010
Telephone (02) 9221 9200
Email studio@chc.com.au
www.chc.com.au

Scale	1:100 @ A1
Date	01/03/2024
Drawn	TM/NS
Architect	EL



Project
Summerset Oakleigh
52 Golf Road, Oakleigh South, VIC

Drawing
General Arrangement Plan - First Floor

Drawing No.
230185/A1203

C2

FOR CONSTRUCTION