




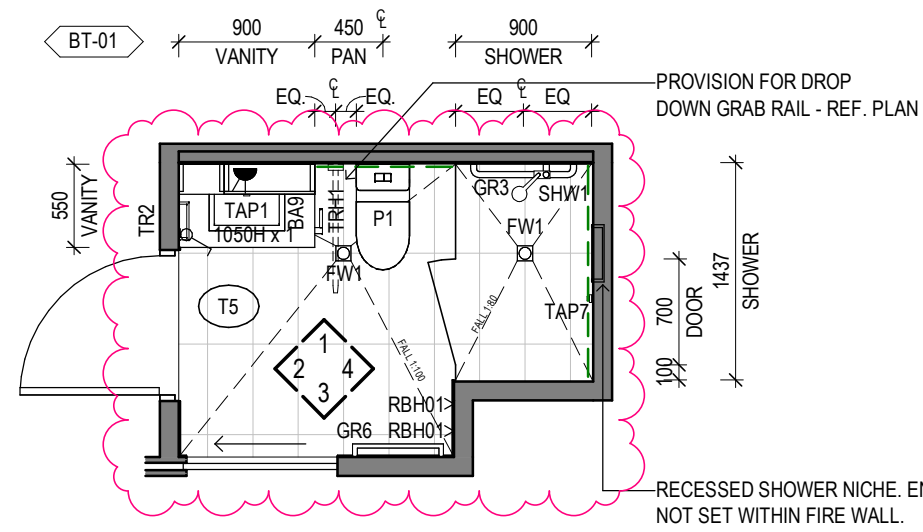


1 ILA BT-01
Scale 1: 50

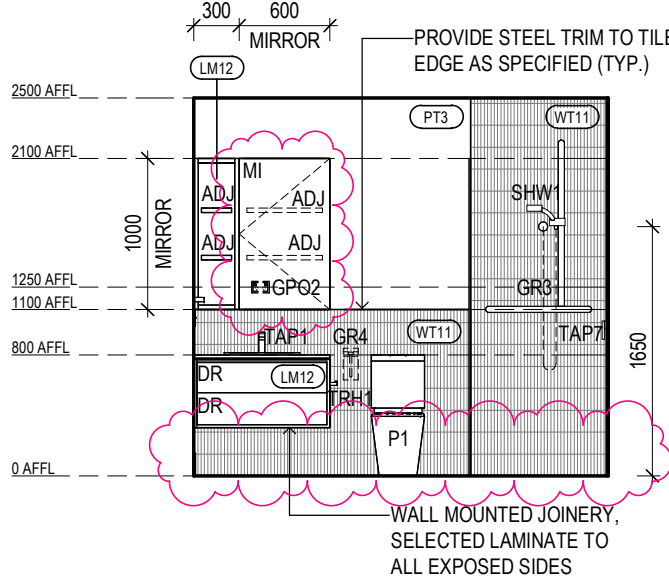


ILA BT-01
ELEVATION 1
Scale 1: 50

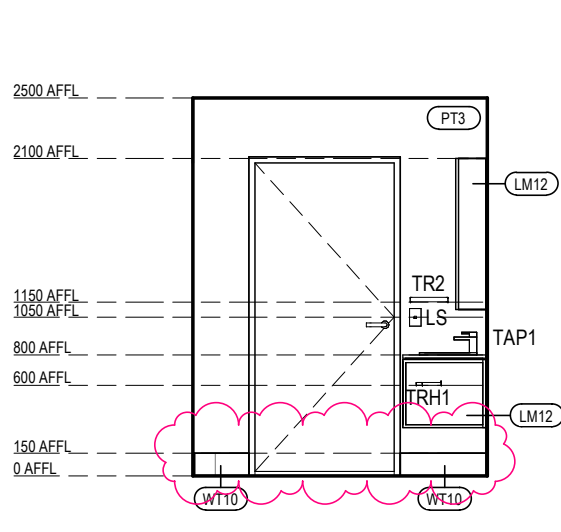


ILA BT-01
ELEVATION 2
Scale 1: 50

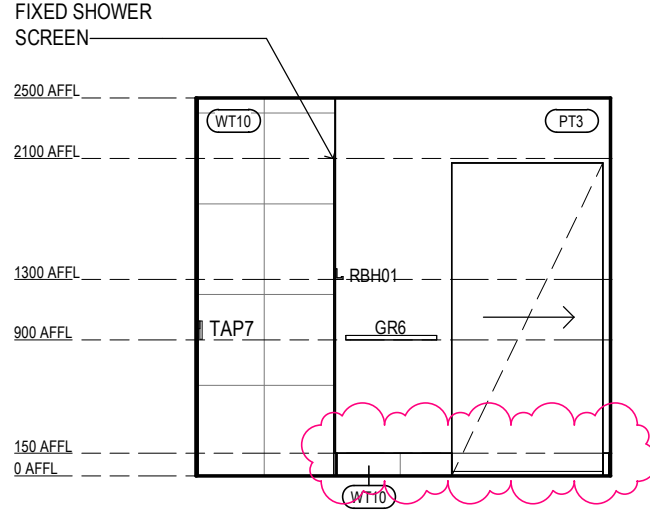


ILA BT-01
ELEVATION 3
Scale 1: 50

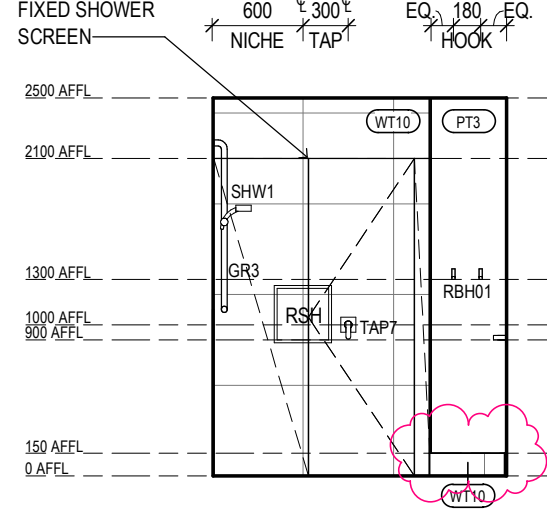


ILA BT-01
ELEVATION 4
Scale 1: 50

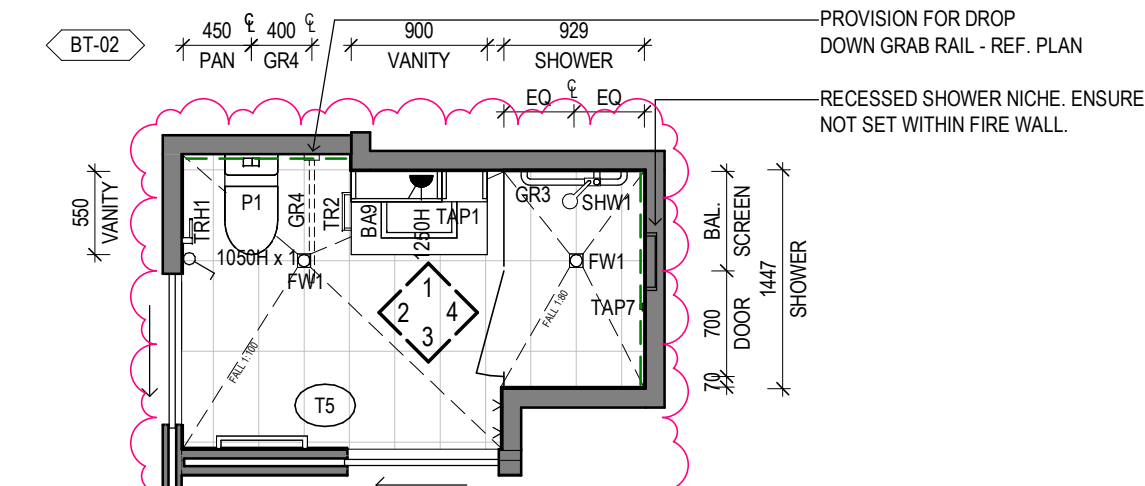


2 ILA BT-02
Scale 1: 50

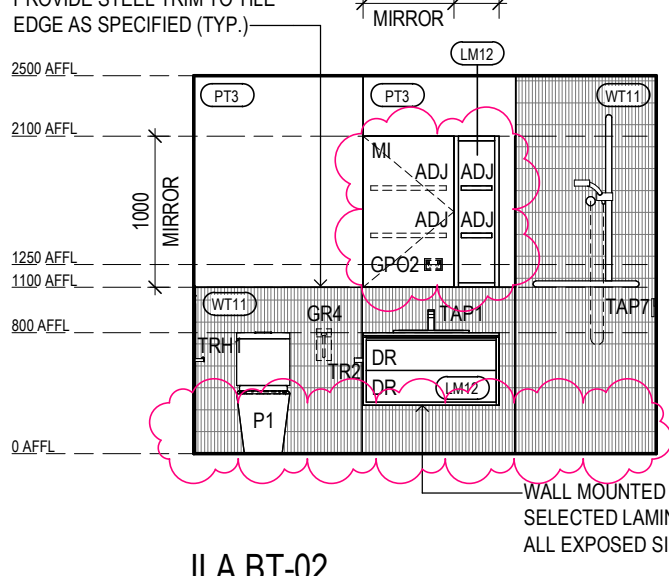


ILA BT-02
ELEVATION 1
Scale 1: 50

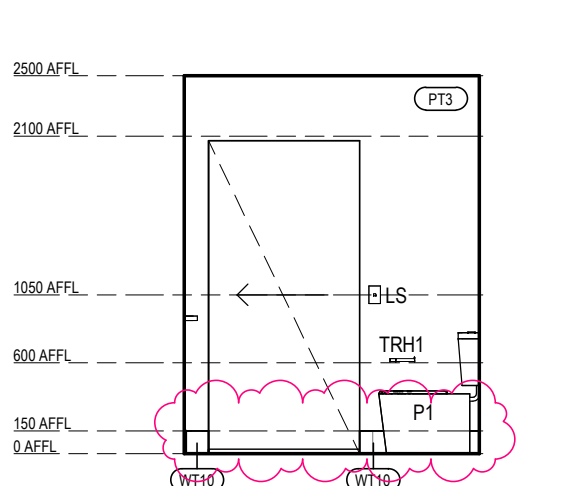


ILA BT-02
ELEVATION 2
Scale 1: 50

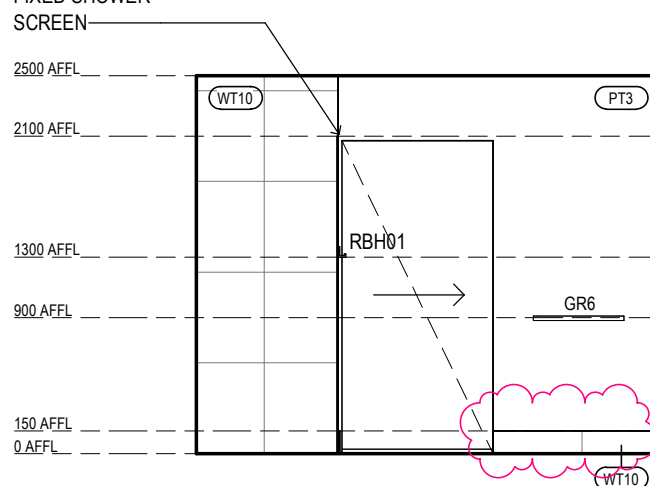


ILA BT-02
ELEVATION 3
Scale 1: 50

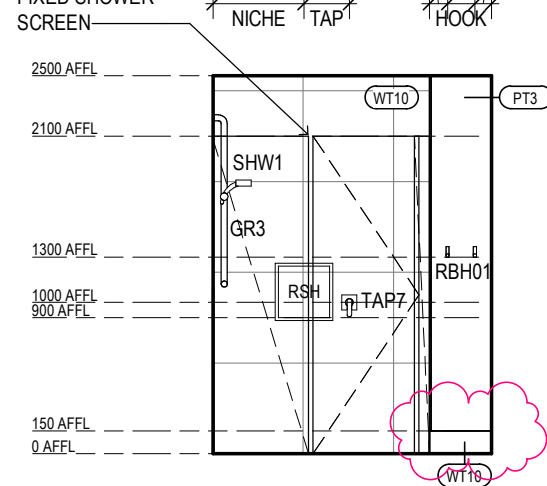


ILA BT-02
ELEVATION 4
Scale 1: 50

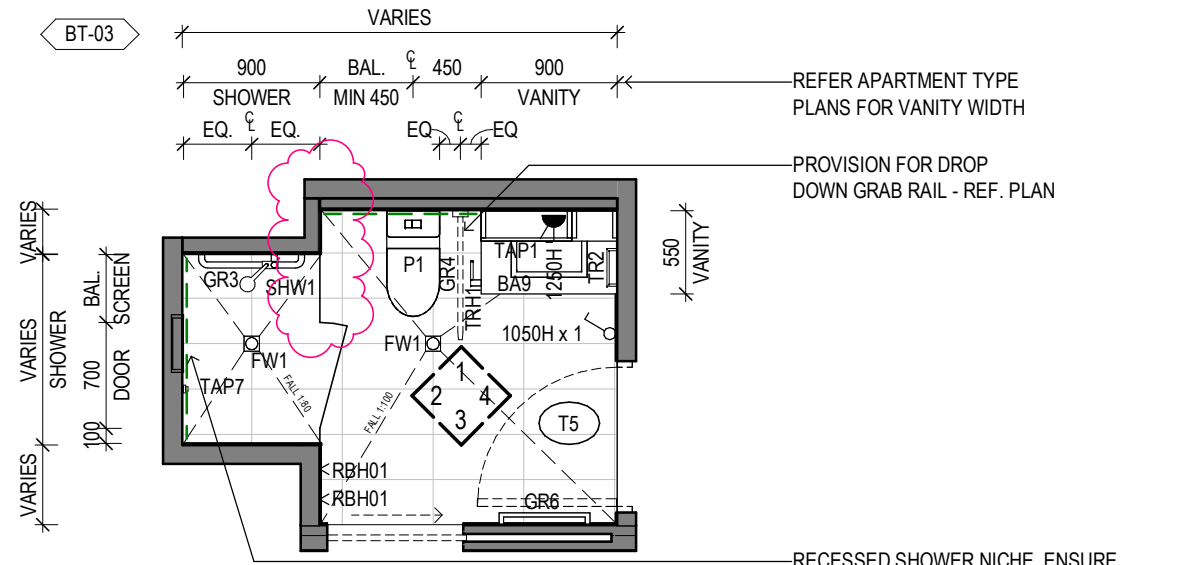


3 ILA BT-03
Scale 1: 50

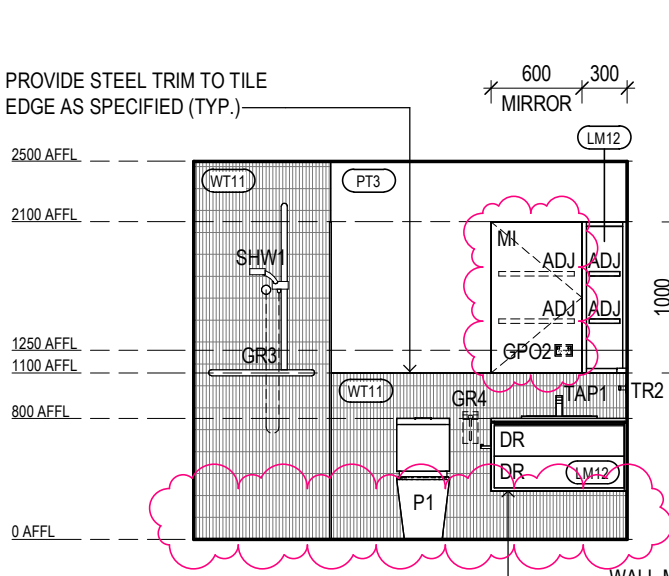


ILA BT-03
ELEVATION 1
Scale 1: 50

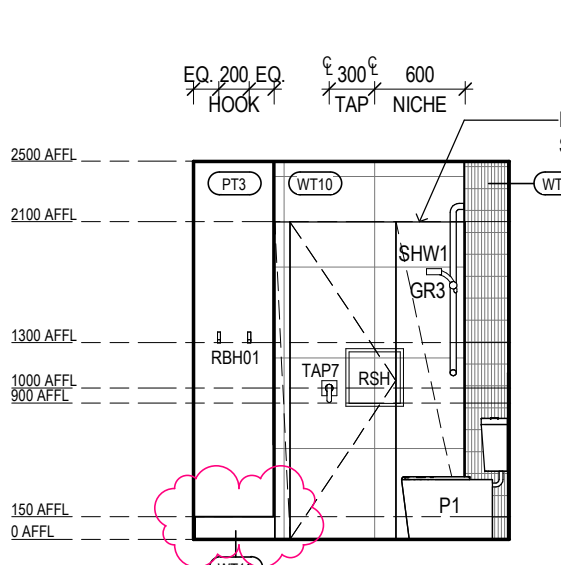


ILA BT-03
ELEVATION 2
Scale 1: 50

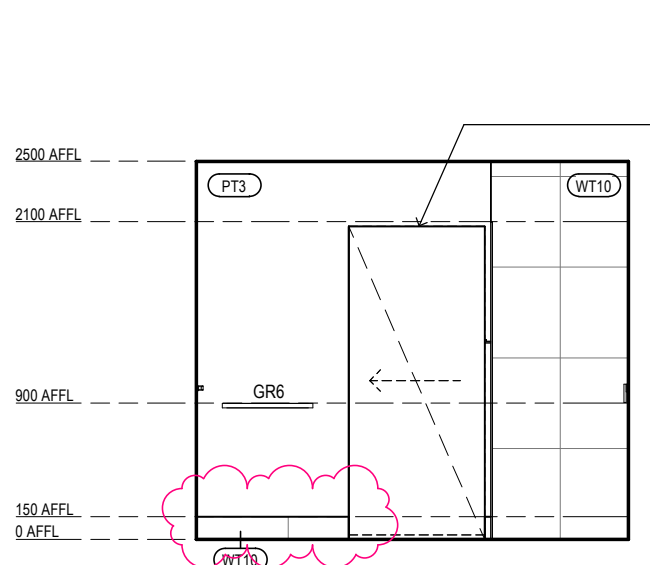


ILA BT-03
ELEVATION 3
Scale 1: 50

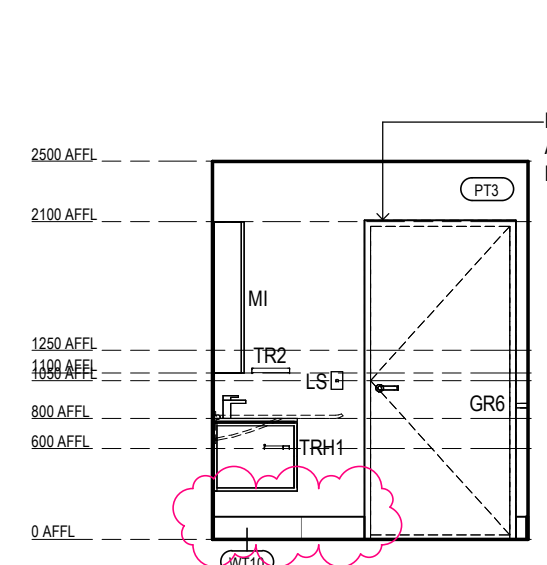


ILA BT-03
ELEVATION 4
Scale 1: 50

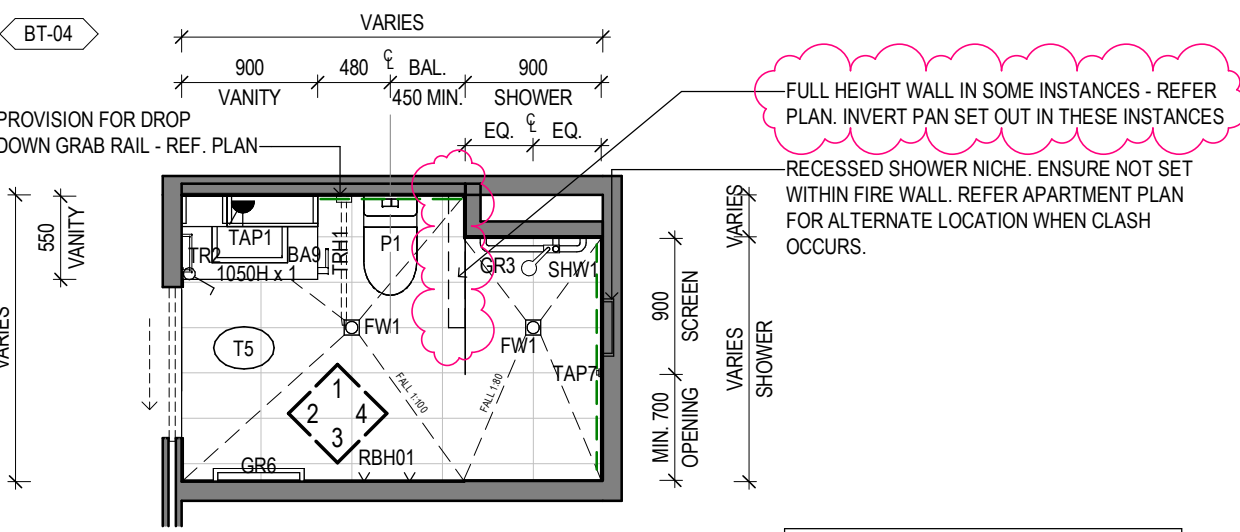


4 ILA BT-04
Scale 1: 50

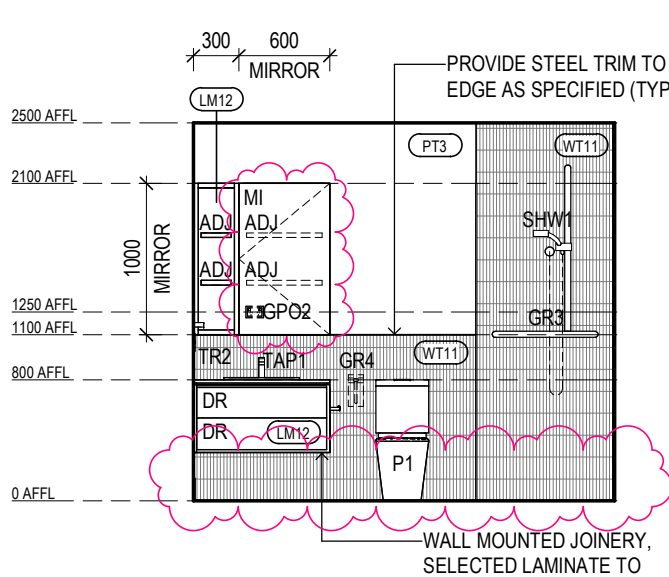


ILA BT-04
ELEVATION 1
Scale 1: 50

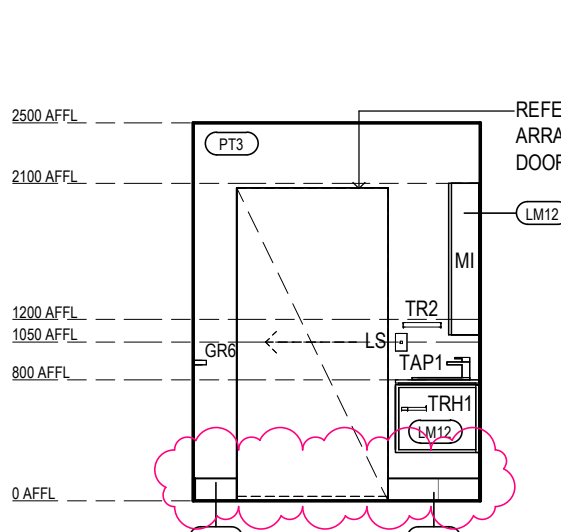


ILA BT-04
ELEVATION 2
Scale 1: 50

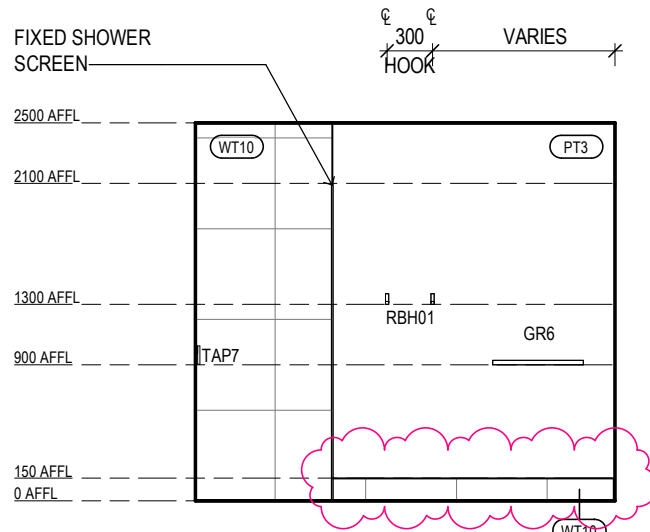


ILA BT-04
ELEVATION 3
Scale 1: 50

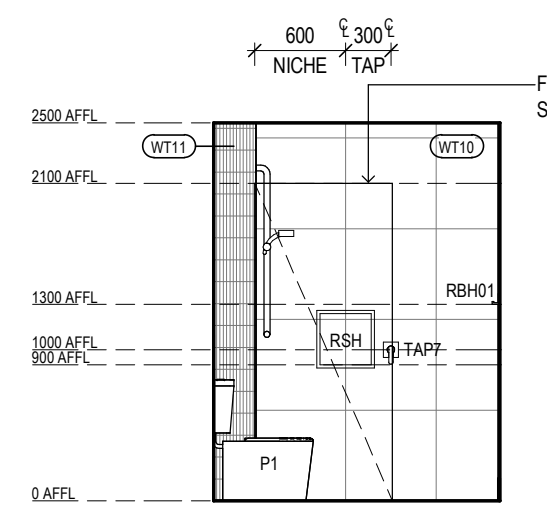


ILA BT-04
ELEVATION 4
Scale 1: 50

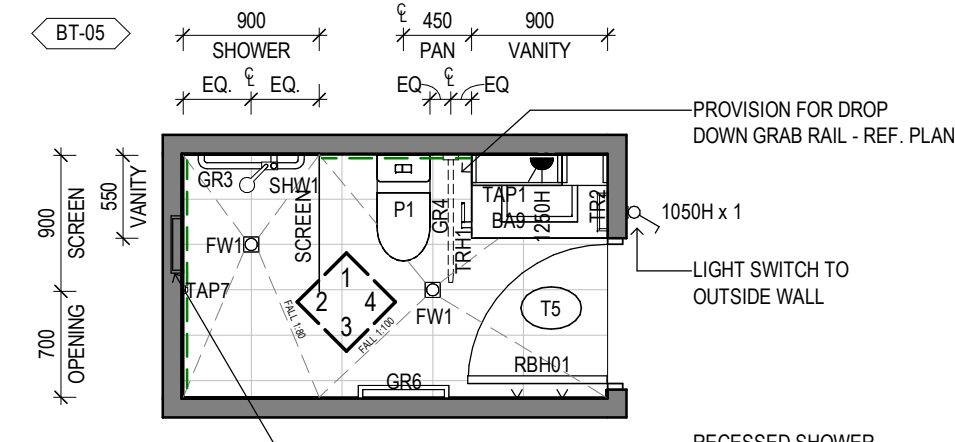


5 ILA BT-05
Scale 1: 50

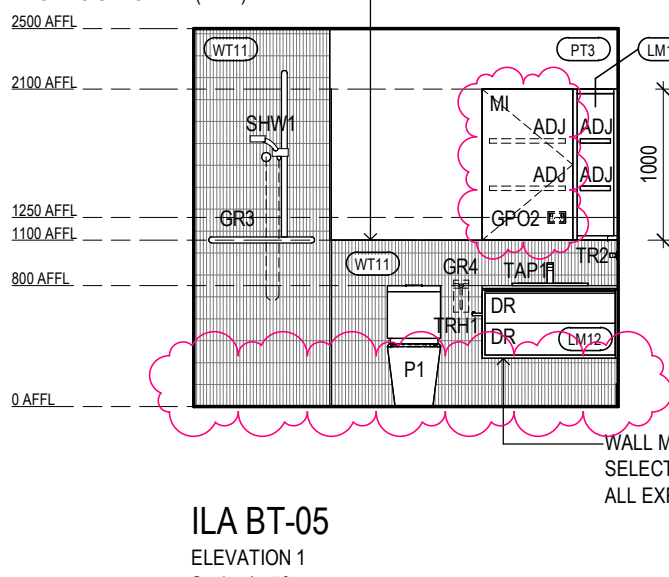


ILA BT-05
ELEVATION 1
Scale 1: 50

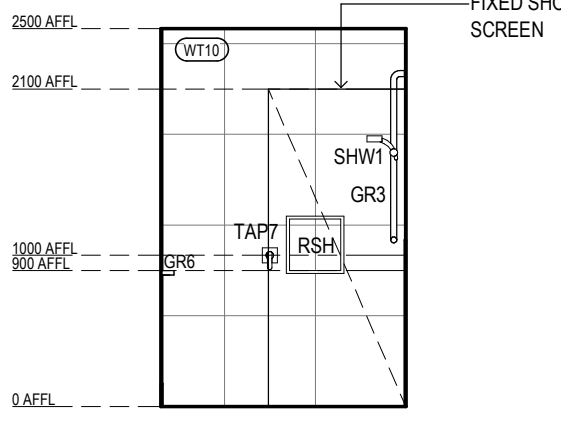

ILA BT-05
ELEVATION 2
Scale 1: 50

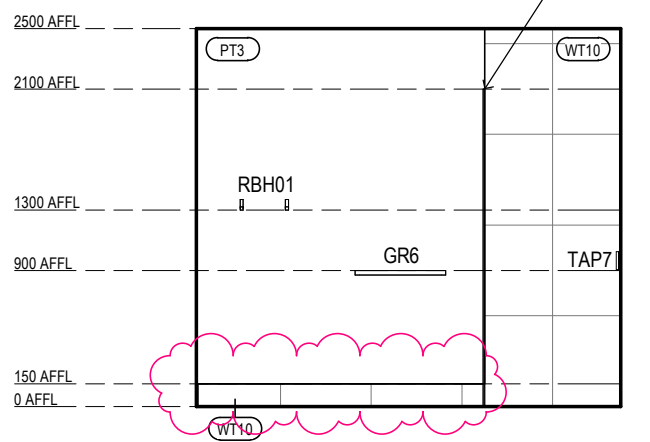

ILA BT-05
ELEVATION 3
Scale 1: 50

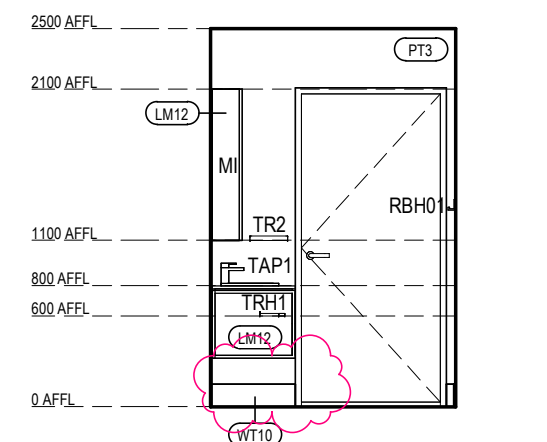

ILA BT-05
ELEVATION 4
Scale 1: 50

Legend - Internal Elevations

DRAWINGS TO BE READ IN CONJUNCTION WITH ARCHITECTURAL SPECIFICATION & MATERIALS, PRODUCTS & FINISHES SCHEDULE.

PT# PAINT FINISH TO ALL WALLS WITHIN NEW & AFFECTED ROOMS/ AREAS UNLESS OTHERWISE SHOWN

- CSE CONCRETE SEALER
- DPR DOOR PROTECTION
- GD GRAPHIC FILM
- LM LAMINATE
- MI MIRROR
- PBD PINBOARD
- PT PAINT FINISH
- REN RENDER FINISH
- SB SPLASHBACK
- ST STONE
- WB WHITEBOARD
- WP WALL PROTECTION
- WT WALL TILE
- WV WALL VINYL

NOTES:
1. LAMINATE CARCASS FOR ALL VISIBLE OPEN SHELVING, UNLESS OTHERWISE NOTED
2. MELAMINE TO ALL INTERNAL CARCASS OF JOINERY, UNLESS OTHERWISE NOTED.

--- PROVIDE NOGGINGS FOR FUTURE USE

Legend - Floor Finishes

- C CARPET
- CO CONCRETE
- E EPOXY FINISH
- L LINOLEUM
- M MATTING
- FU PAVING UNIT - TBC WITH LANDSCAPE
- R RUBBER FLOORING
- T TILING
- TF TIMBER FLOORING
- V VINYL
- LVT LUXURY VINYL TILE PLANK

--- PROTECTION RAILS OR CRASH RAILS - REFER TO MATERIAL SCHEDULE FOR DETAILS

--- WL1- REFER TO MATERIAL SCHEDULE FOR DETAILS

--- WL2- REFER TO MATERIAL SCHEDULE FOR DETAILS

NOTE:
FALLS TO ALL FLOOR WASTES IN ACCORDANCE WITH AS 3740.

Keystone Legend

- BA9 BASIN - TYPE 9
- DR DRAWER
- FW1 FLOOR WASTE - TYPE 1
- GP02 POWER OUTLET - DOUBLE
- GR3 GRAB RAIL - TYPE 3
- GR4 GRAB RAIL - TYPE 4
- GR6 GRAB RAIL - TYPE 6
- LS LIGHT SWITCH
- MI MIRROR
- P1 TOILET PAN TYPE 01
- RBH01 ROBE HOOK - TYPE 1
- RSH1 RECESSED SHOWER NICHE
- SHW1 SHOWER - TYPE 1
- TAP1 TAP - TYPE 1
- TAP7 TAP - TYPE 7
- TR2 TOWEL RAIL - TYPE 2
- TRH1 TOILET ROLL HOLDER - TYPE 1

SHOWER DOOR NOTE:
SHOWER DOORS SHOWN INDICATIVE ONLY. WHERE SHOWER LENGTH IS LESS THAN 1600mm: PROVIDE SCREEN + 700W DOOR. WHERE SHOWER LENGTH IS 1600mm OR MORE: PROVIDE 900mm SCREEN ONLY

NOTE:
ALL BATHROOM LAYOUT SHOWN DESIGN INTENT & INFORMATION ONLY:
ALLOW JOINERY TO HAVE MIRRORRED TYPE:
REFER TO GENERAL FLOOR PLAN FOR PROPER LAYOUT & SETOUT

FOR CONSTRUCTION

Revision/Issue	Date
P1 Preliminary ILA Apartment Types & Joineries	2025.08.25
P2 Tender Pack Issue	2025.09.05
P3 ISSUE FOR CONTRACT	2025.10.10
C1 ISSUE FOR CONSTRUCTION - INTERIORS	2026.04.13

Clarke Hopkins
architect

ClarkeHopkinsClarke

Melbourne | Wurundjeri
L3, Melbourne Connect
700 Swanston Street
Carlton VIC 3063
Telephone (03) 9419 4340
Email studio@chc.com.au
www.chc.com.au

Sydney | Gadigal Country
Suite 3, Ground Floor
91 Campbell Street
Sunny Hills NSW 2010
Telephone (02) 9221 9200
Email studio@chc.com.au
www.chc.com.au

Scale	As indicated @ A1
Date	01/03/2024
Drawn	TT/NS
Architect	EL

Project
Summerset Oakleigh
52 Golf Road, Oakleigh South, VIC

Drawing
Internal Elevations - Typical Bathroom & Pwdr Room - Sheet 1

Drawing No.

230185/A2822

C1