




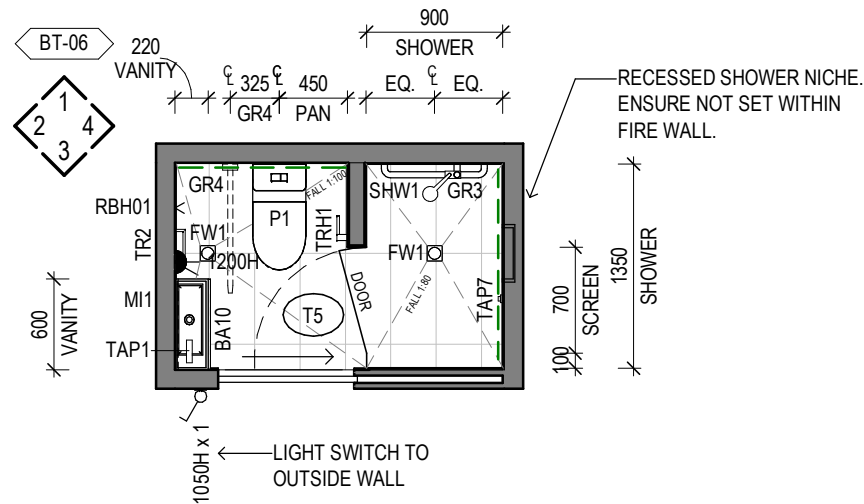


1 ILA BT-06
Scale 1 : 50

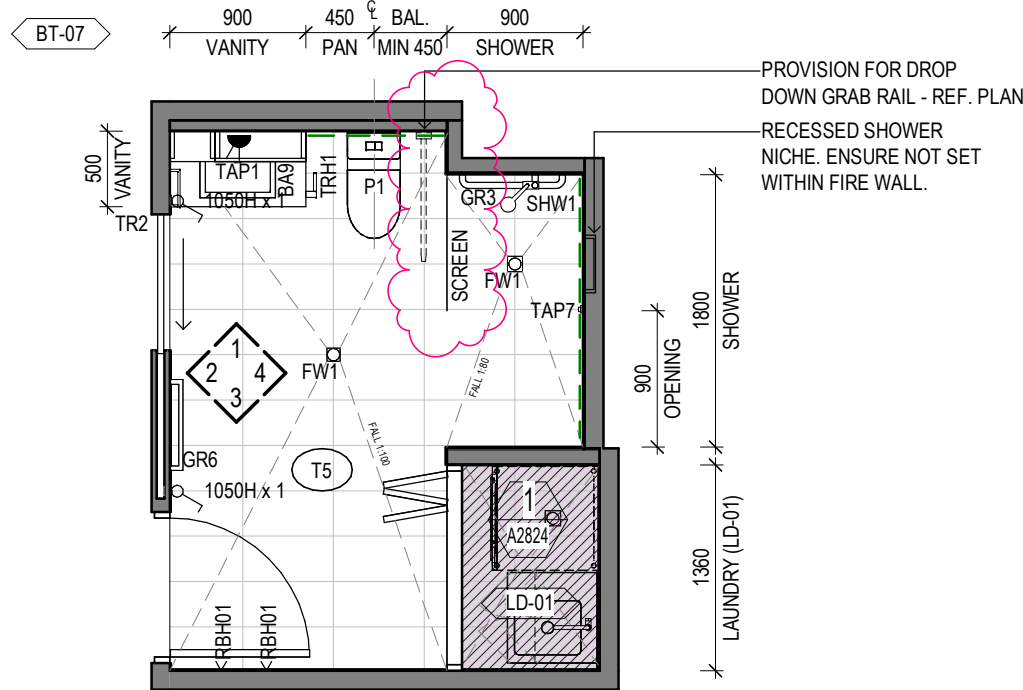


2 ILA BT-07
Scale 1 : 50

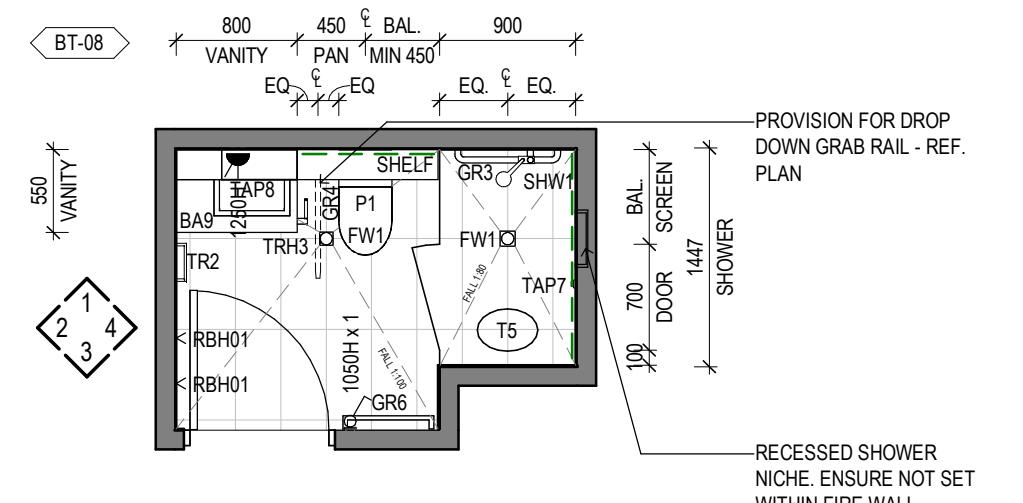


3 ILA BT-08
Scale 1 : 50

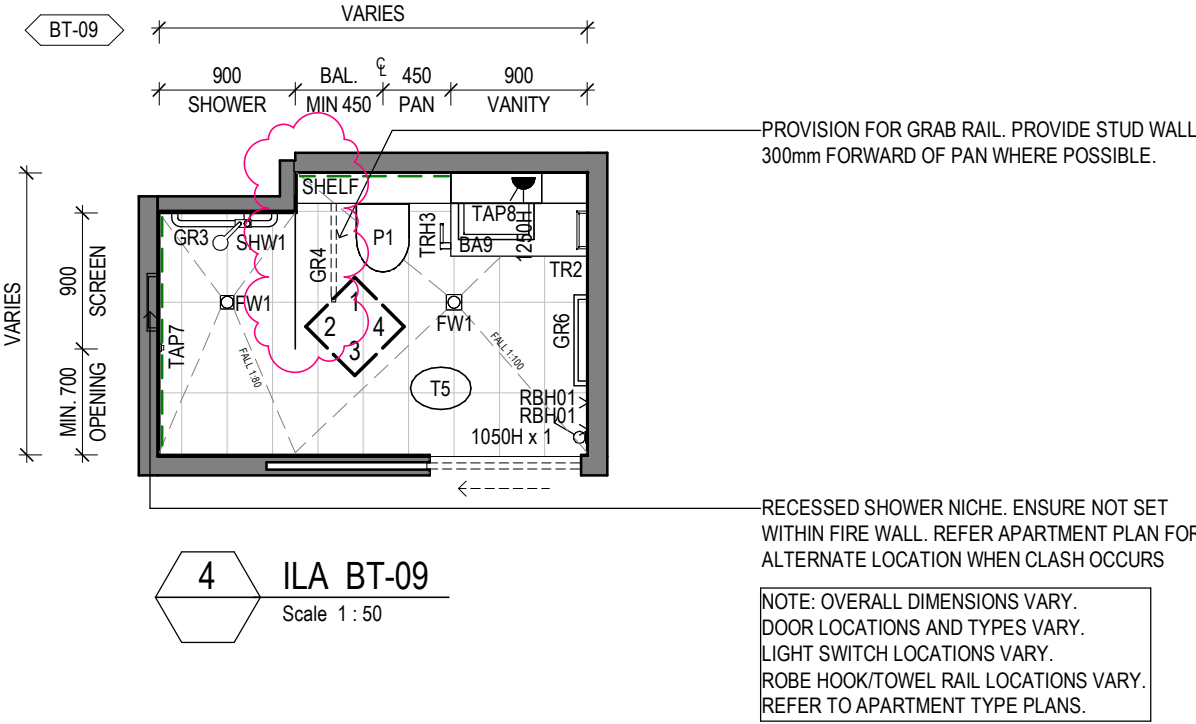


4 ILA BT-09
Scale 1 : 50

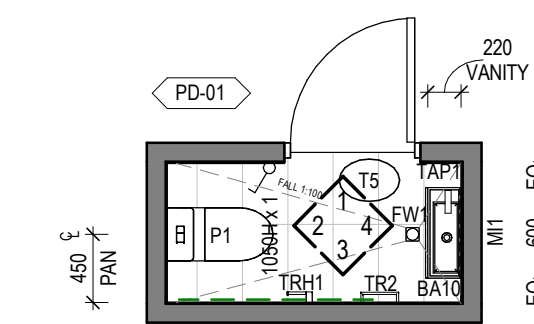


5 ILA PD-01
Scale 1 : 50

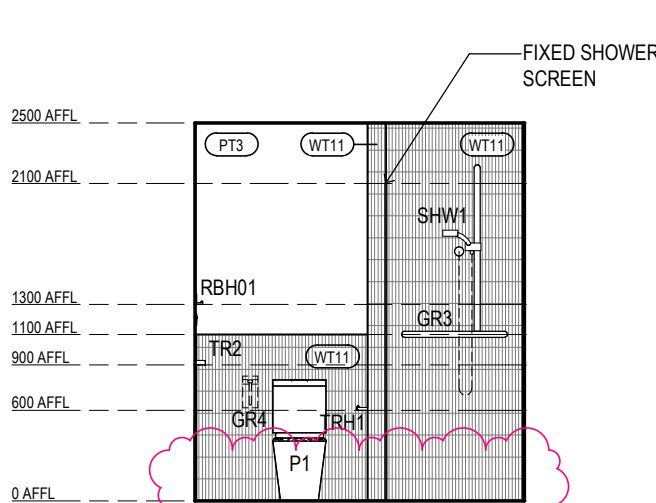


ILA BT-06
ELEVATION 1
Scale 1 : 50

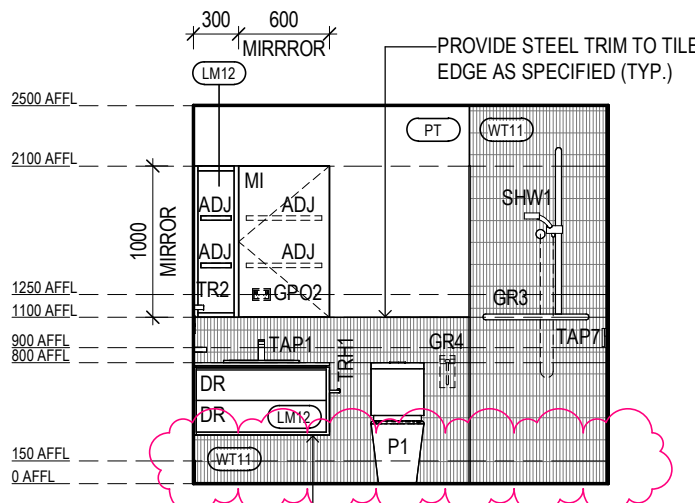


ILA BT-07
ELEVATION 1
Scale 1 : 50

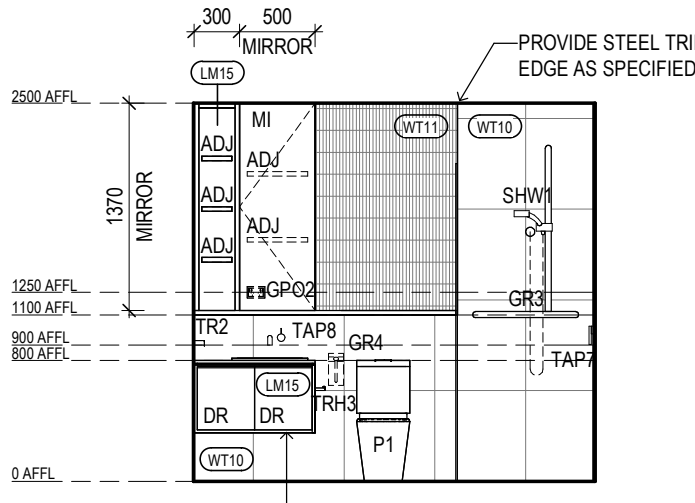


ILA BT-08
ELEVATION 1
Scale 1 : 50

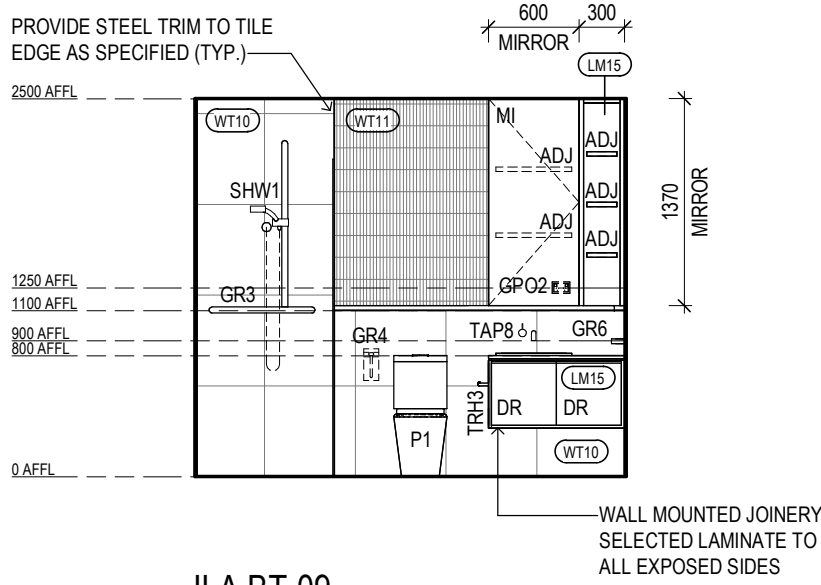


ILA BT-09
ELEVATION 1
Scale 1 : 50

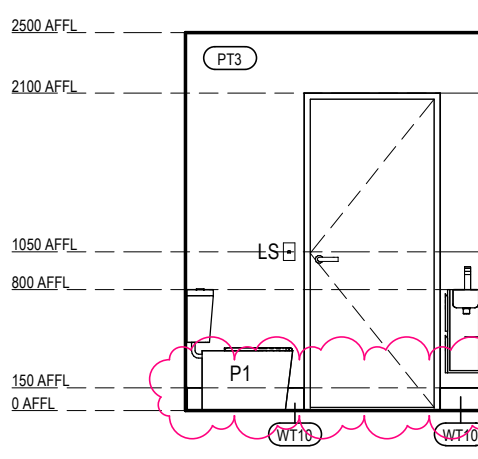


ILA PD-01
ELEVATION 1
Scale 1 : 50

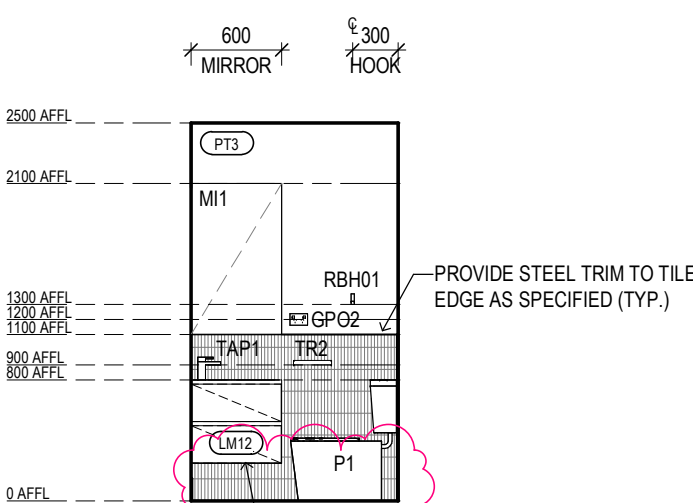


ILA BT-06
ELEVATION 2
Scale 1 : 50

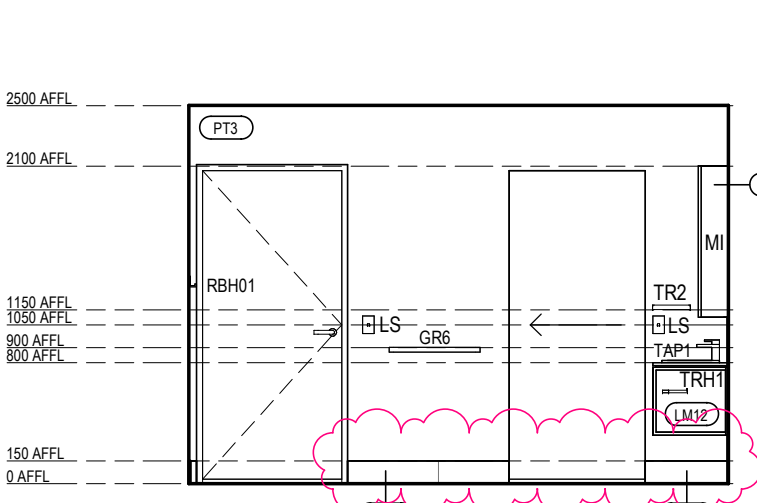


ILA BT-07
ELEVATION 2
Scale 1 : 50

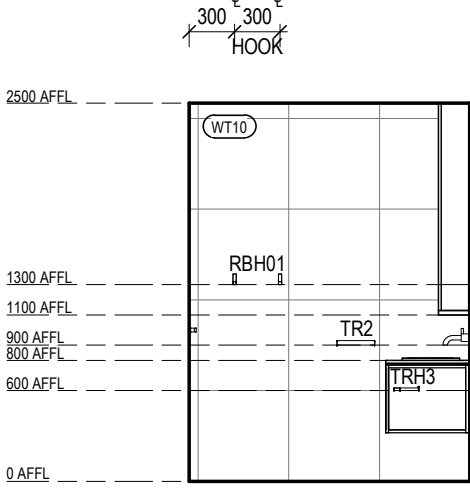


ILA BT-08
ELEVATION 2
Scale 1 : 50

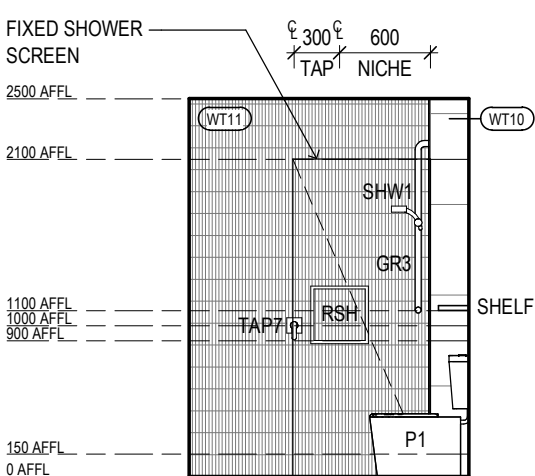


ILA BT-09
ELEVATION 2
Scale 1 : 50

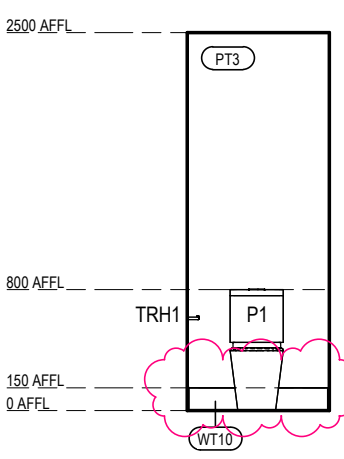


ILA PD-01
ELEVATION 2
Scale 1 : 50

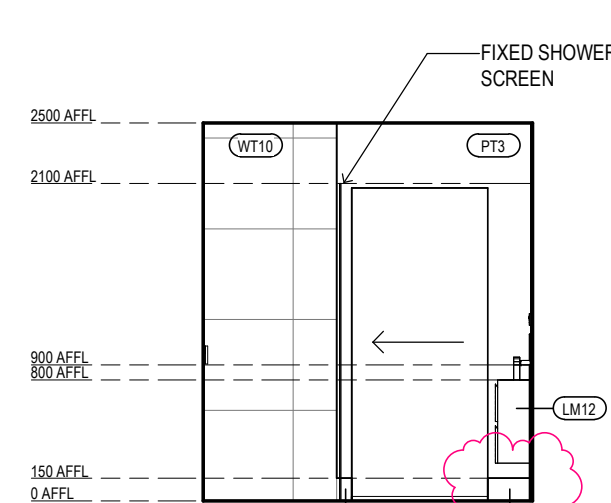


ILA BT-06
ELEVATION 3
Scale 1 : 50

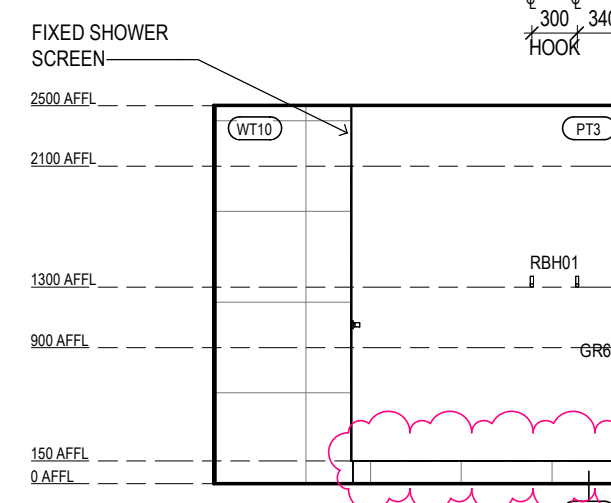


ILA BT-07
ELEVATION 3
Scale 1 : 50

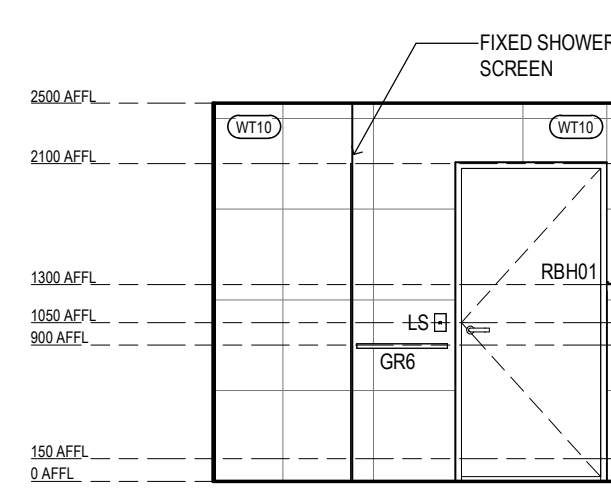


ILA BT-08
ELEVATION 3
Scale 1 : 50

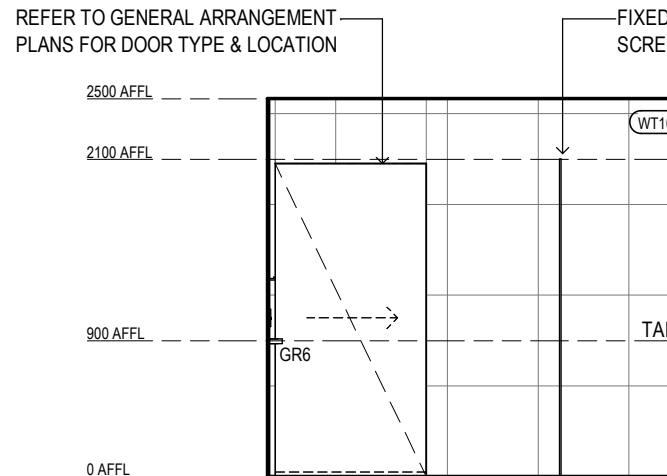


ILA BT-09
ELEVATION 3
Scale 1 : 50

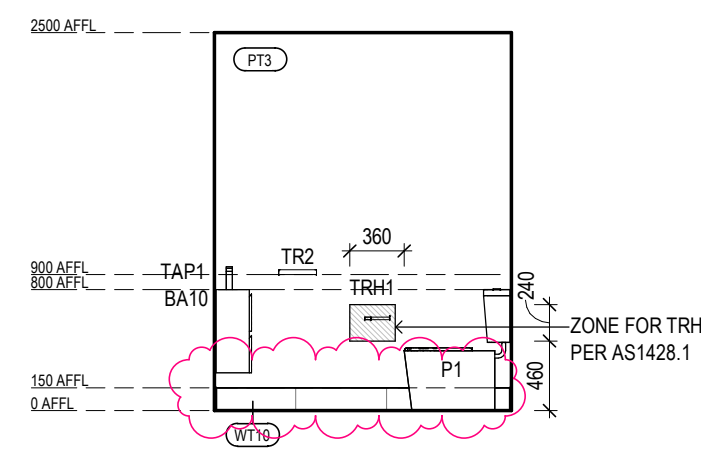


ILA PD-01
ELEVATION 3
Scale 1 : 50

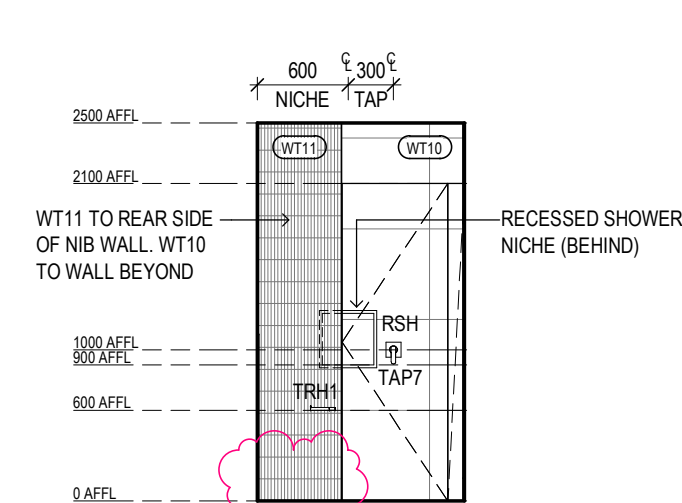


ILA BT-06
ELEVATION 4
Scale 1 : 50

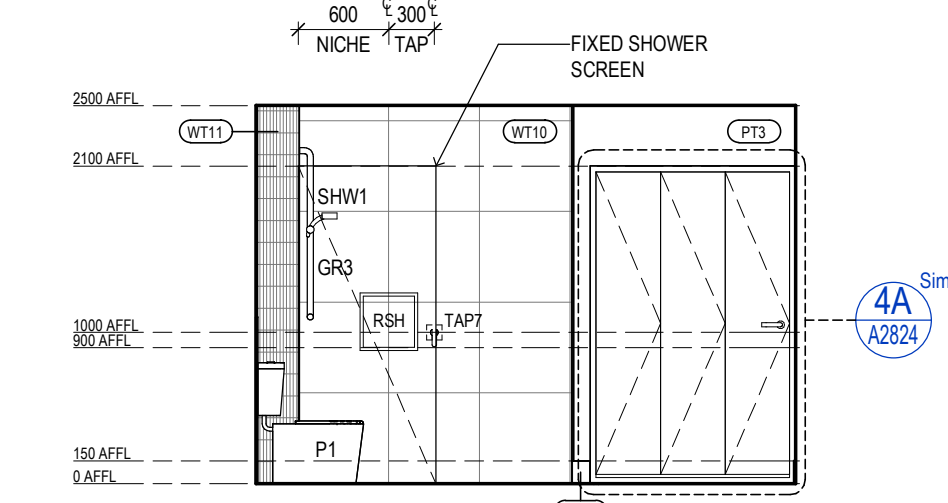


ILA BT-07
ELEVATION 4
Scale 1 : 50

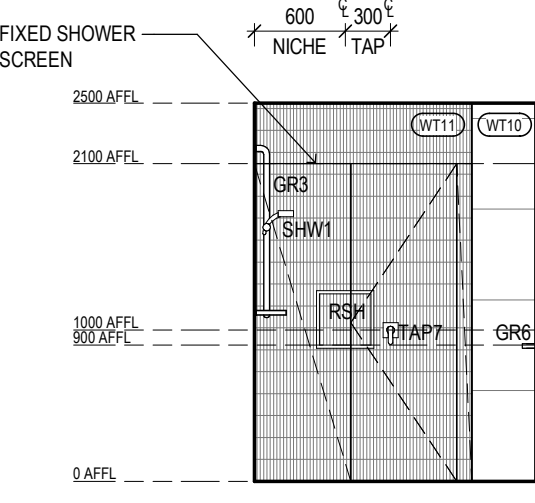

ILA BT-08
ELEVATION 4
Scale 1 : 50

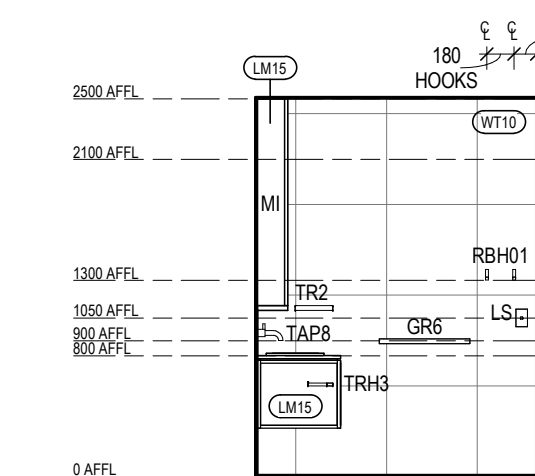

ILA BT-09
ELEVATION 4
Scale 1 : 50

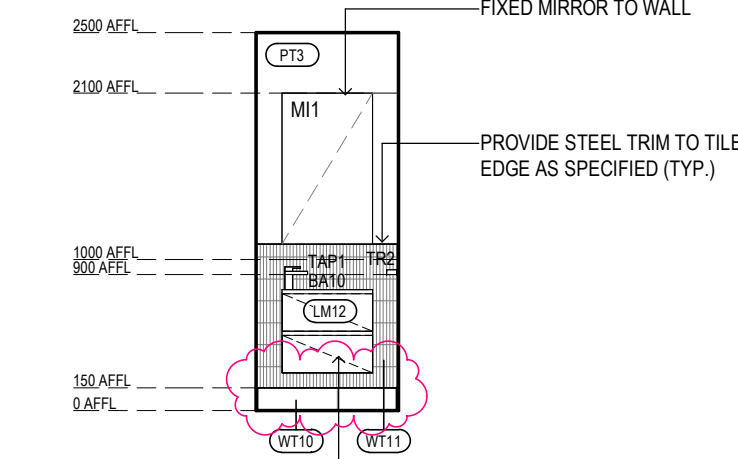

ILA PD-01
ELEVATION 4
Scale 1 : 50

Legend - Internal Elevations

DRAWINGS TO BE READ IN CONJUNCTION WITH ARCHITECTURAL SPECIFICATION & MATERIALS, PRODUCTS & FINISHES SCHEDULE.

PT# PAINT FINISH TO ALL WALLS WITHIN NEW & AFFECTED ROOMS/ AREAS UNLESS OTHERWISE SHOWN

- CSE CONCRETE SEALER
- DPR DOOR PROTECTION
- GD GRAPHIC FILM
- LM LAMINATE
- MI MIRROR
- PBD PINBOARD
- PT PAINT FINISH
- REN RENDER FINISH
- SB SPLASHBACK
- ST STONE
- WB WHITEBOARD
- WP WALL PROTECTION
- WT WALL TILE
- WV WALL VINYL

NOTES:
1. LAMINATE CARCASS FOR ALL VISIBLE OPEN SHELVING, UNLESS OTHERWISE NOTED
2. MELAMINE TO ALL INTERNAL CARCASS OF JOINERY, UNLESS OTHERWISE NOTED.

--- PROVIDE NOGGINGS FOR FUTURE USE

Legend - Floor Finishes

- C CARPET
- CO CONCRETE
- E EPOXY FINISH
- L LINOLEUM
- M MATTING
- PU PAVING UNIT - TBC WITH LANDSCAPE
- R RUBBER FLOORING
- T TILING
- TF TIMBER FLOORING
- V VINYL
- LVT LUXURY VINYL TILE PLANK

--- PROTECTION RAILS OR CRASH RAILS - REFER TO MATERIAL SCHEDULE FOR DETAILS

--- WL1- REFER TO MATERIAL SCHEDULE FOR DETAILS

--- WL2- REFER TO MATERIAL SCHEDULE FOR DETAILS

NOTE:

FALLS TO ALL FLOOR WASTES IN ACCORDANCE WITH AS 3740.

Keystone Legend

- BA9 BASIN - TYPE 9
- BA10 BASIN - TYPE 10
- DR DRAWER
- FW1 FLOOR WASTE - TYPE 1
- GP02 POWER OUTLET - DOUBLE
- GR3 GRAB RAIL - TYPE 3
- GR4 GRAB RAIL - TYPE 4
- GR6 GRAB RAIL - TYPE 6
- LS LIGHT SWITCH
- MI MIRROR
- M1 MIRROR - TYPE 1
- P1 TOILET PAN TYPE 01
- RBH01 ROBE HOOK - TYPE 1
- RSH RECESSED SHOWER NICHE
- SHW1 SHOWER - TYPE 1
- TAP - TYPE 1
- TAP7 TAP - TYPE 7
- TAP8 TAP - TYPE 8
- TR2 TOWEL RAIL - TYPE 2
- TRH1 TOILET ROLL HOLDER - TYPE 1
- TRH3 TOILET ROLL HOLDER - TYPE 3

SHOWER DOOR NOTE:

SHOWER DOORS SHOWN INDICATIVE ONLY. WHERE SHOWER LENGTH IS LESS THAN 1600mm: PROVIDE SCREEN + 700W DOOR WHERE SHOWER LENGTH IS 1600mm OR MORE: PROVIDE 900mm SCREEN ONLY

NOTE:
ALL BATHROOM LAYOUT SHOWN DESIGN INTENT & INFORMATION ONLY:
ALLOW JOINERY TO HAVE MIRRORRED TYPE:
REFER TO GENERAL FLOOR PLAN FOR PROPER LAYOUT & SETOUT

FOR CONSTRUCTION

Clarke
Hopkins
Clarke

ClarkeHopkinsClarke

Melbourne | Wurundjeri
L3, Melbourne Connect
700 Swanston Street
Carlton VIC 3063
Telephone (03) 9419 4340
Email studio@chc.com.au
www.chc.com.au

Sydney | Gadigal Country
Suite 3, Ground Floor
91 Campbell Street
Surry Hills NSW 2010
Telephone (02) 9221 9200
Email studio@chc.com.au
www.chc.com.au

Scale As indicated @ A1
Date 01/03/2024
Drawn NS
Architect EL

Project
Summerset Oakleigh
52 Golf Road, Oakleigh South, VIC

Drawing
Internal Elevations - Typical Bathroom &
Pwdr Room - Sheet 2

Drawing No.

230185/A2823

C1

Revision/Issue
P1 Tender Pack - Doors and Windows
P2 ISSUE FOR CONTRACT
C1 ISSUE FOR CONSTRUCTION - INTERIORS

Date
2025.09.15
2025.10.10
2026.04.13