


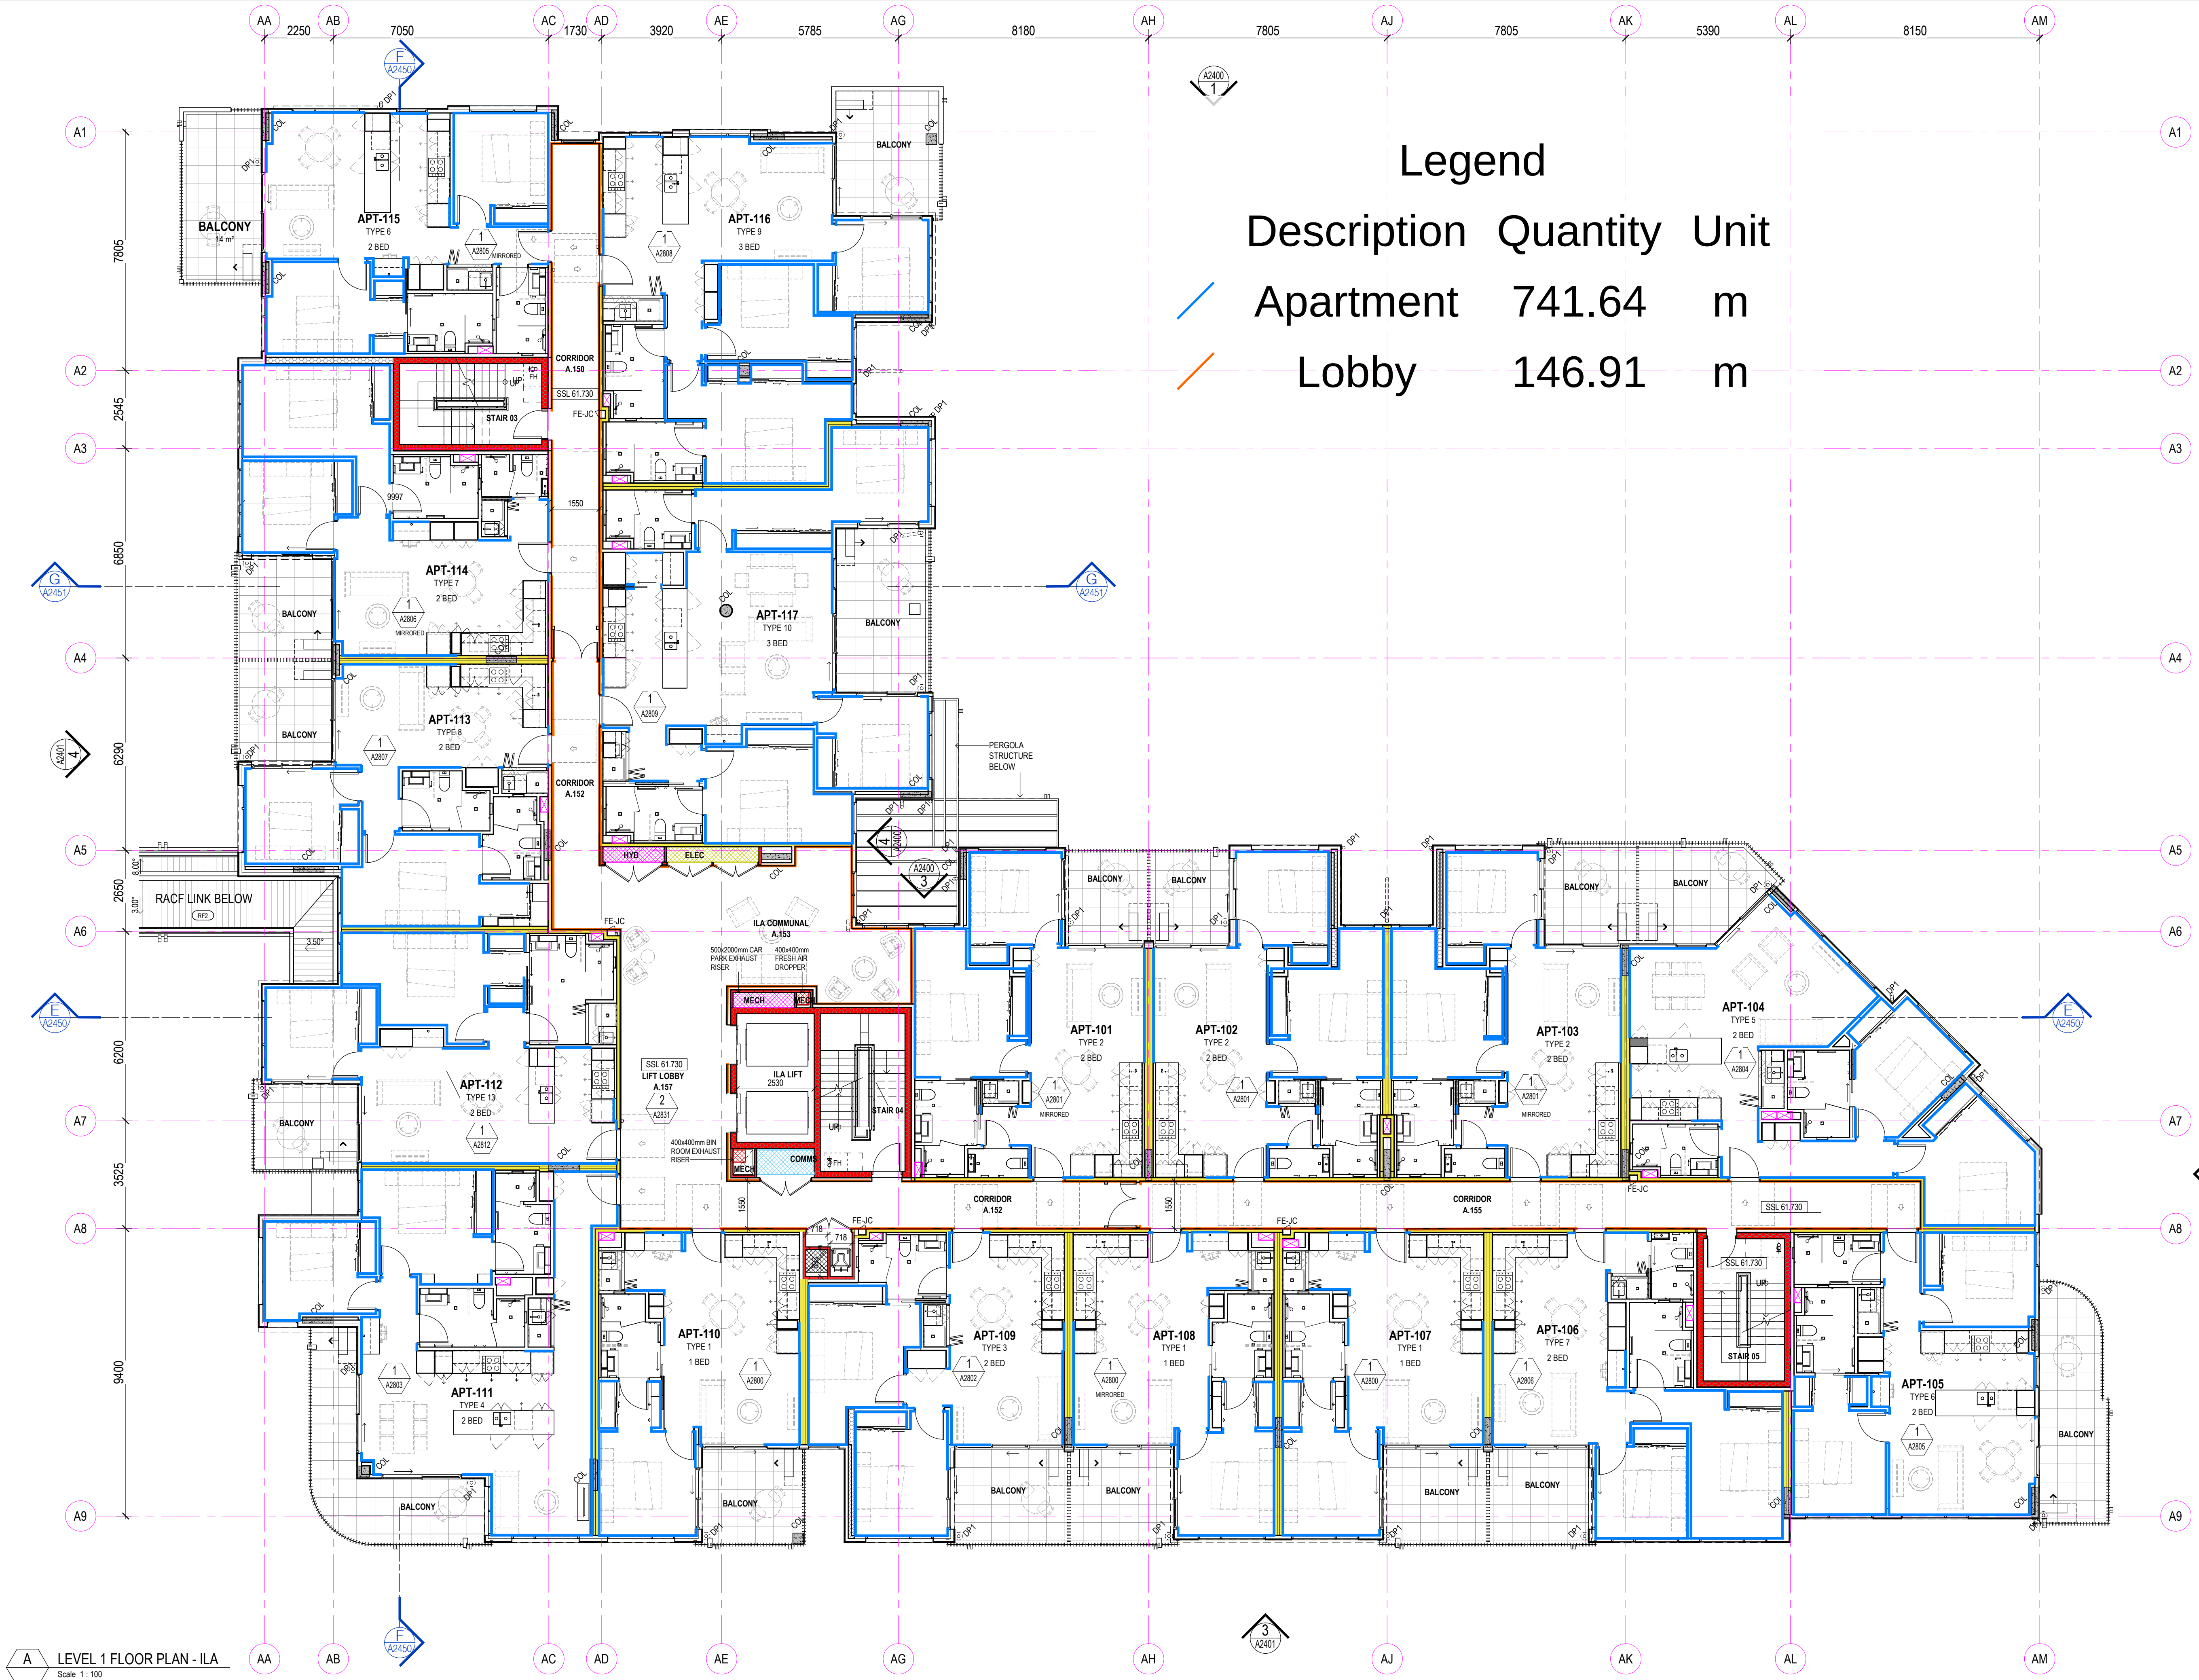

Legend		
Description	Quantity	Unit
Apartment	741.64	m
Lobby	146.91	m

General Notes

BUILDER TO VIEW THE SITE DURING THE TENDER PERIOD TO SATISFY THEMSELVES OF THE LATENT SITE CONDITIONS AND FULL EXTENT OF WORK AS REQUIRED TO ALLOW FOR THE COMPLETION OF ALL WORKS AS DETAILED IN ALL DOCUMENTATION.

ALL DOCUMENTS ARE TO BE REVIEWED IN CONJUNCTION WITH RELEVANT CONSULTANTS DRAWINGS AND SPECIFICATIONS.

CONTRACTOR TO USE 92MM METAL STUD FRAMING UNLESS NOTED OTHERWISE. REFER TO ACOUSTIC REPORT AND FIRE/SMOKE COMPARTMENT PLANS FOR WALLS THAT EXTEND TO UNDERSIDE OF SLAB AND ROOF SHEETING.

ALLOW FOR WALL STRENGTHENING BEHIND WALL MOUNTED FIXTURES AND FITTINGS INCLUDING BUT NOT LIMITED TO GRABRAILS, HANDRAILS, EQUIPMENT HOOKS, DRUG SAFES.

ALL FIRE, SMOKE, ACOUSTIC WALLS, CORRIDOR WALLS TO BEDROOMS AND APARTMENTS ARE FULL HEIGHT TO UNDERSIDE OF SLAB OR SHEET METAL ROOF.

IMPACT RESISTANT PLASTERBOARD TO BE INSTALED FROM 0 AFFL TO 1200 AFFL (TYPICALLY TO ALL STORES AND CORRIDORS).

ONLY CORRIDORS WITHOUT DADO PANELS REQUIRE IMPACT RESISTANT PLASTERBOARD.

ALLOW FOR FURRING CHANNELS AND LINING TO ALL CONCRETE COLUMNS. LINING TO MATCH WITH LINING OF ASSOCIATED ROOM.

Legend - General

WALL TYPE - REFER TO WALL SET-OUT PLANS & WALL TYPES SHEET FOR DETAILS

RELATIVE LEVEL

PROPOSED FINISH LEVEL

ABBREVIATIONS

COL COLUMN

DP1 DOWNPIPE - TYPE 1

FE-JC FIRE EXTINGUISHER IN JOINERY CUPBOARD

FH FIRE HYDRANT

LEVEL 1 FLOOR PLAN - ILA
Scale 1:100

Revision/Issue	Date
P6 Updated GA Set	2025.08.21
P7 BUILDING PERMIT ISSUE	2025.10.08
C1 ISSUE FOR CONSTRUCTION	2025.12.19
C2 ISSUE FOR CONSTRUCTION	2026.03.24
C3 ISSUE FOR CONSTRUCTION	2026.04.14

Clarke Hopkins
architect

ClarkeHopkinsClarke

Melbourne | Wurundjeri
L3, Melbourne Connect
700 Swanston Street
Carlton VIC 3063
Telephone (03) 9419 4340
Email studio@chc.com.au
www.chc.com.au

Sydney | Gadigal Country
Suite 3, Ground Floor
91 Campbell Street
Surry Hills NSW 2010
Telephone (02) 9221 9200
Email studio@chc.com.au
www.chc.com.au

Scale	1:100 @ A1
Date	01/03/2024
Drawn	TM
Architect	EL

Project
Summerset Oakleigh
52 Golf Road, Oakleigh South, VIC

Drawing
General Arrangement Plan - First Floor

Drawing No.
230185/A2201
C3

FOR CONSTRUCTION