




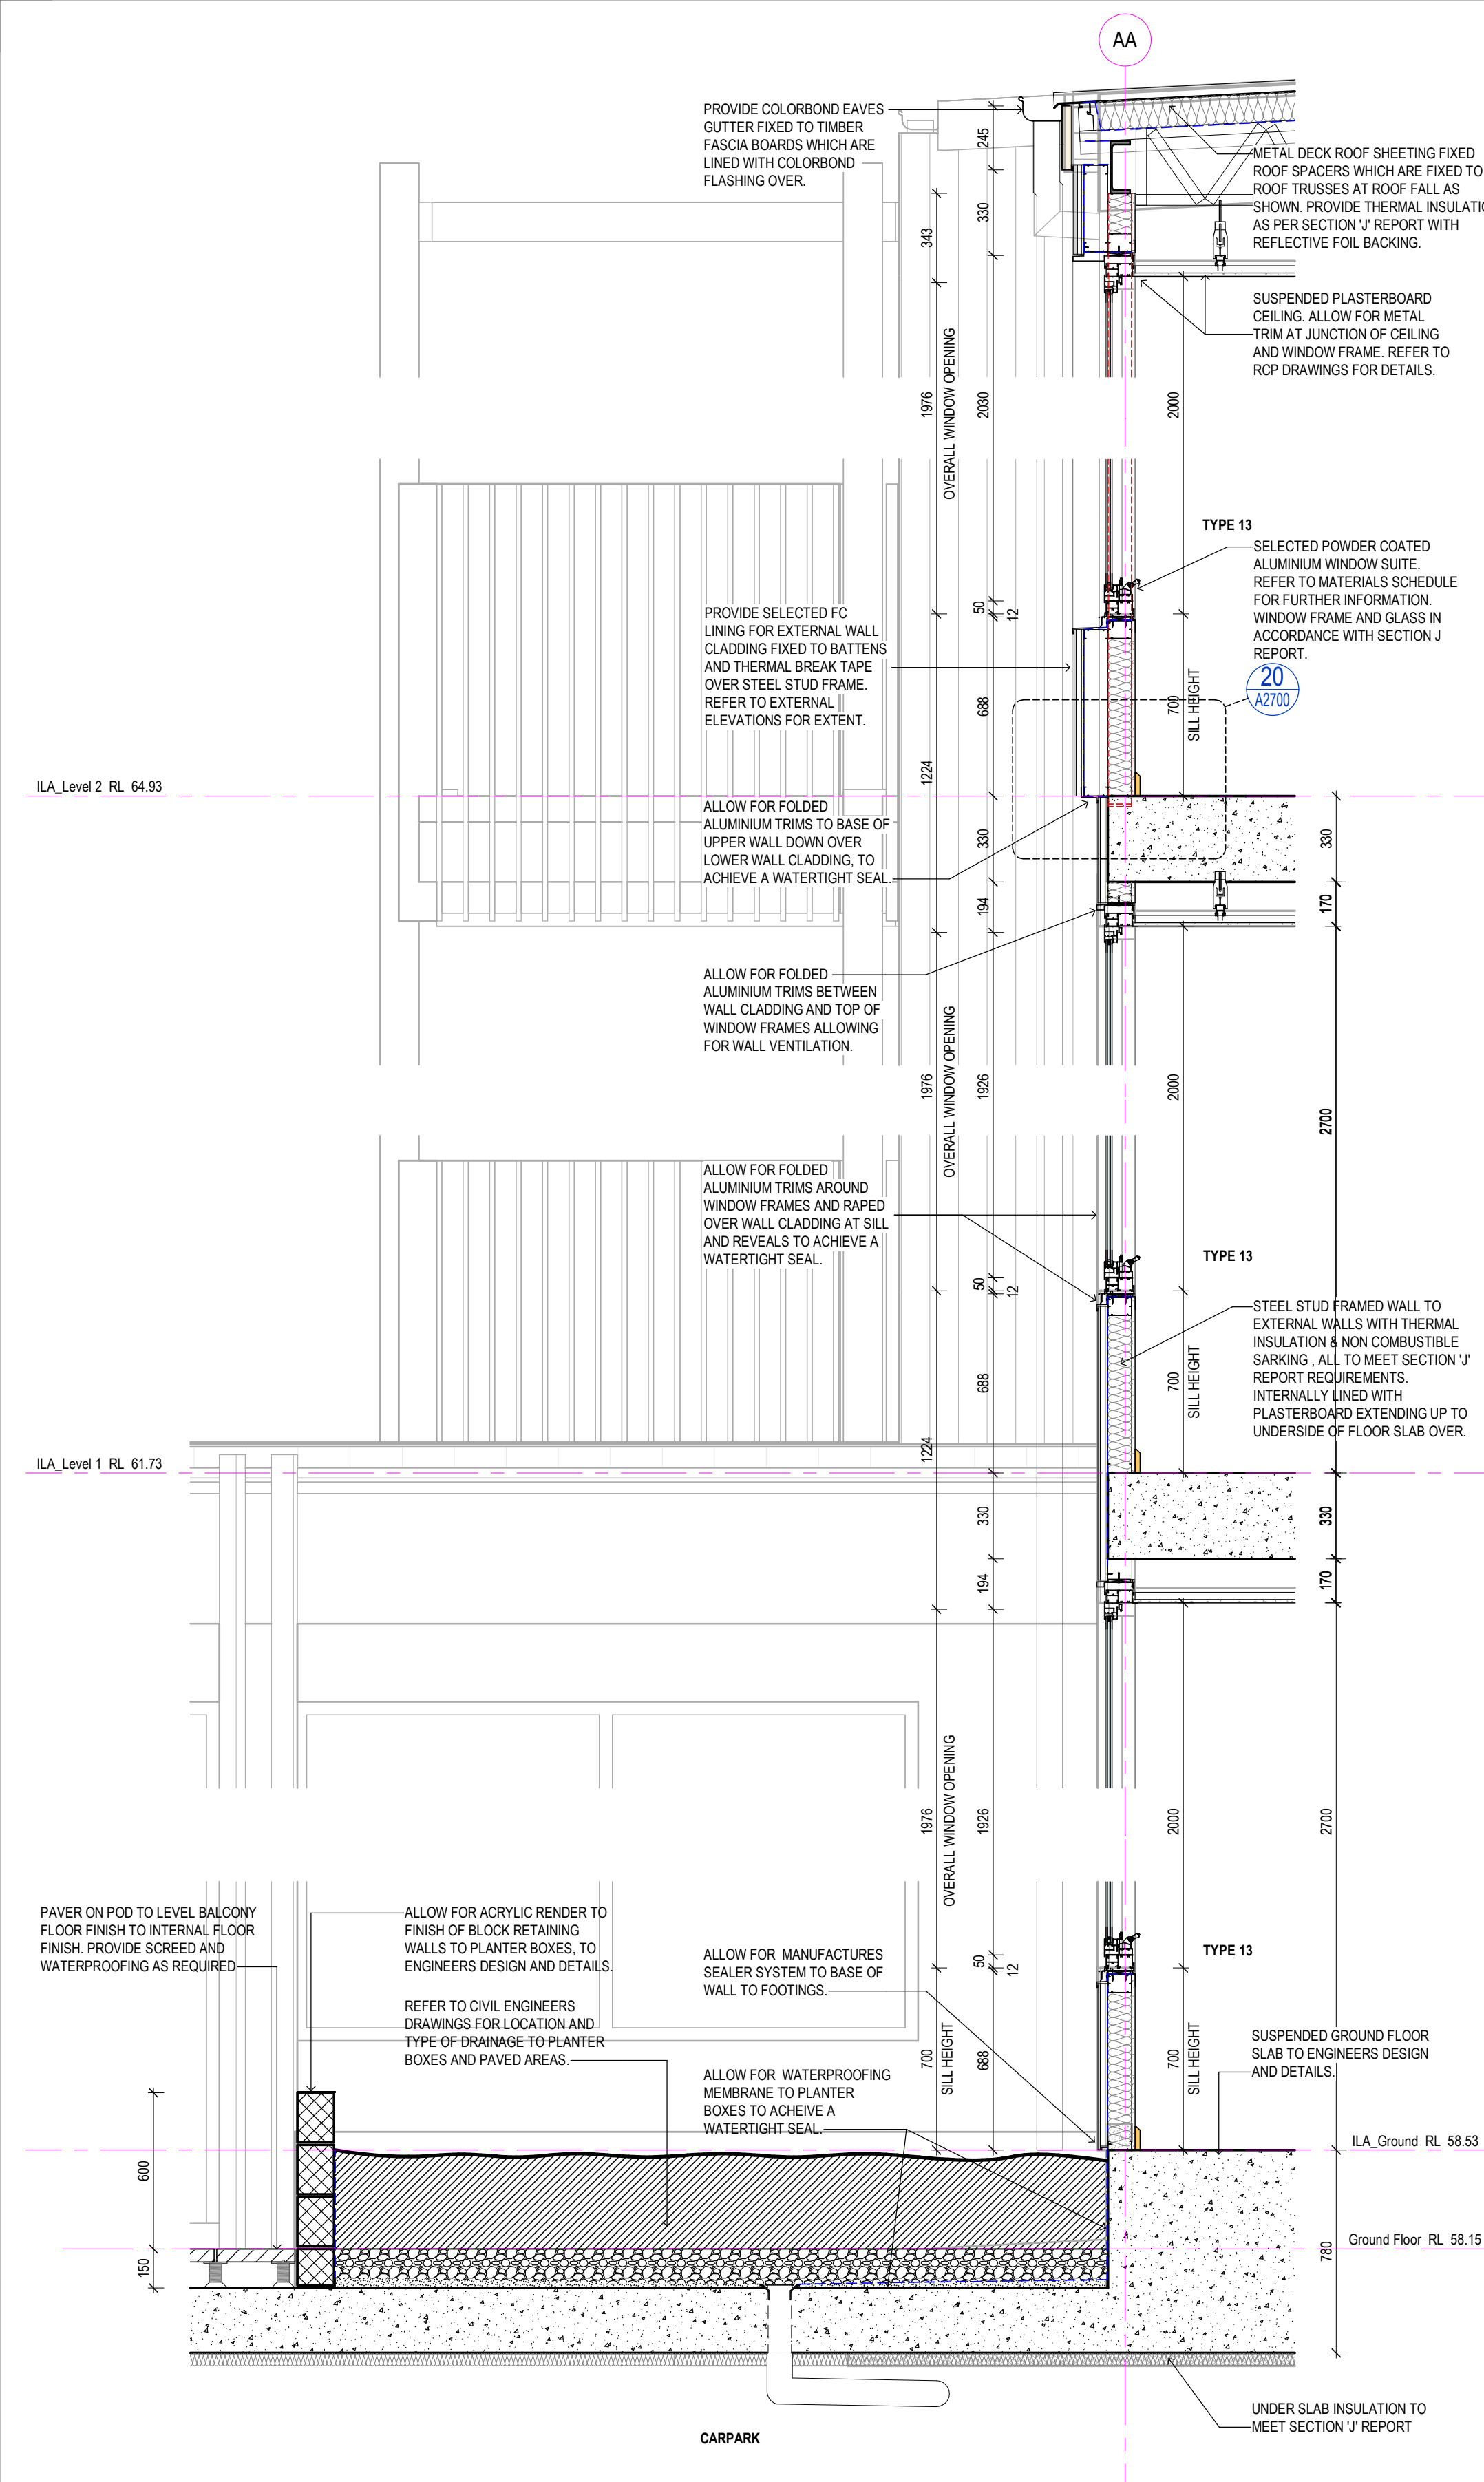

1
E ILA - WALL SECTION 01
Scale 1:20

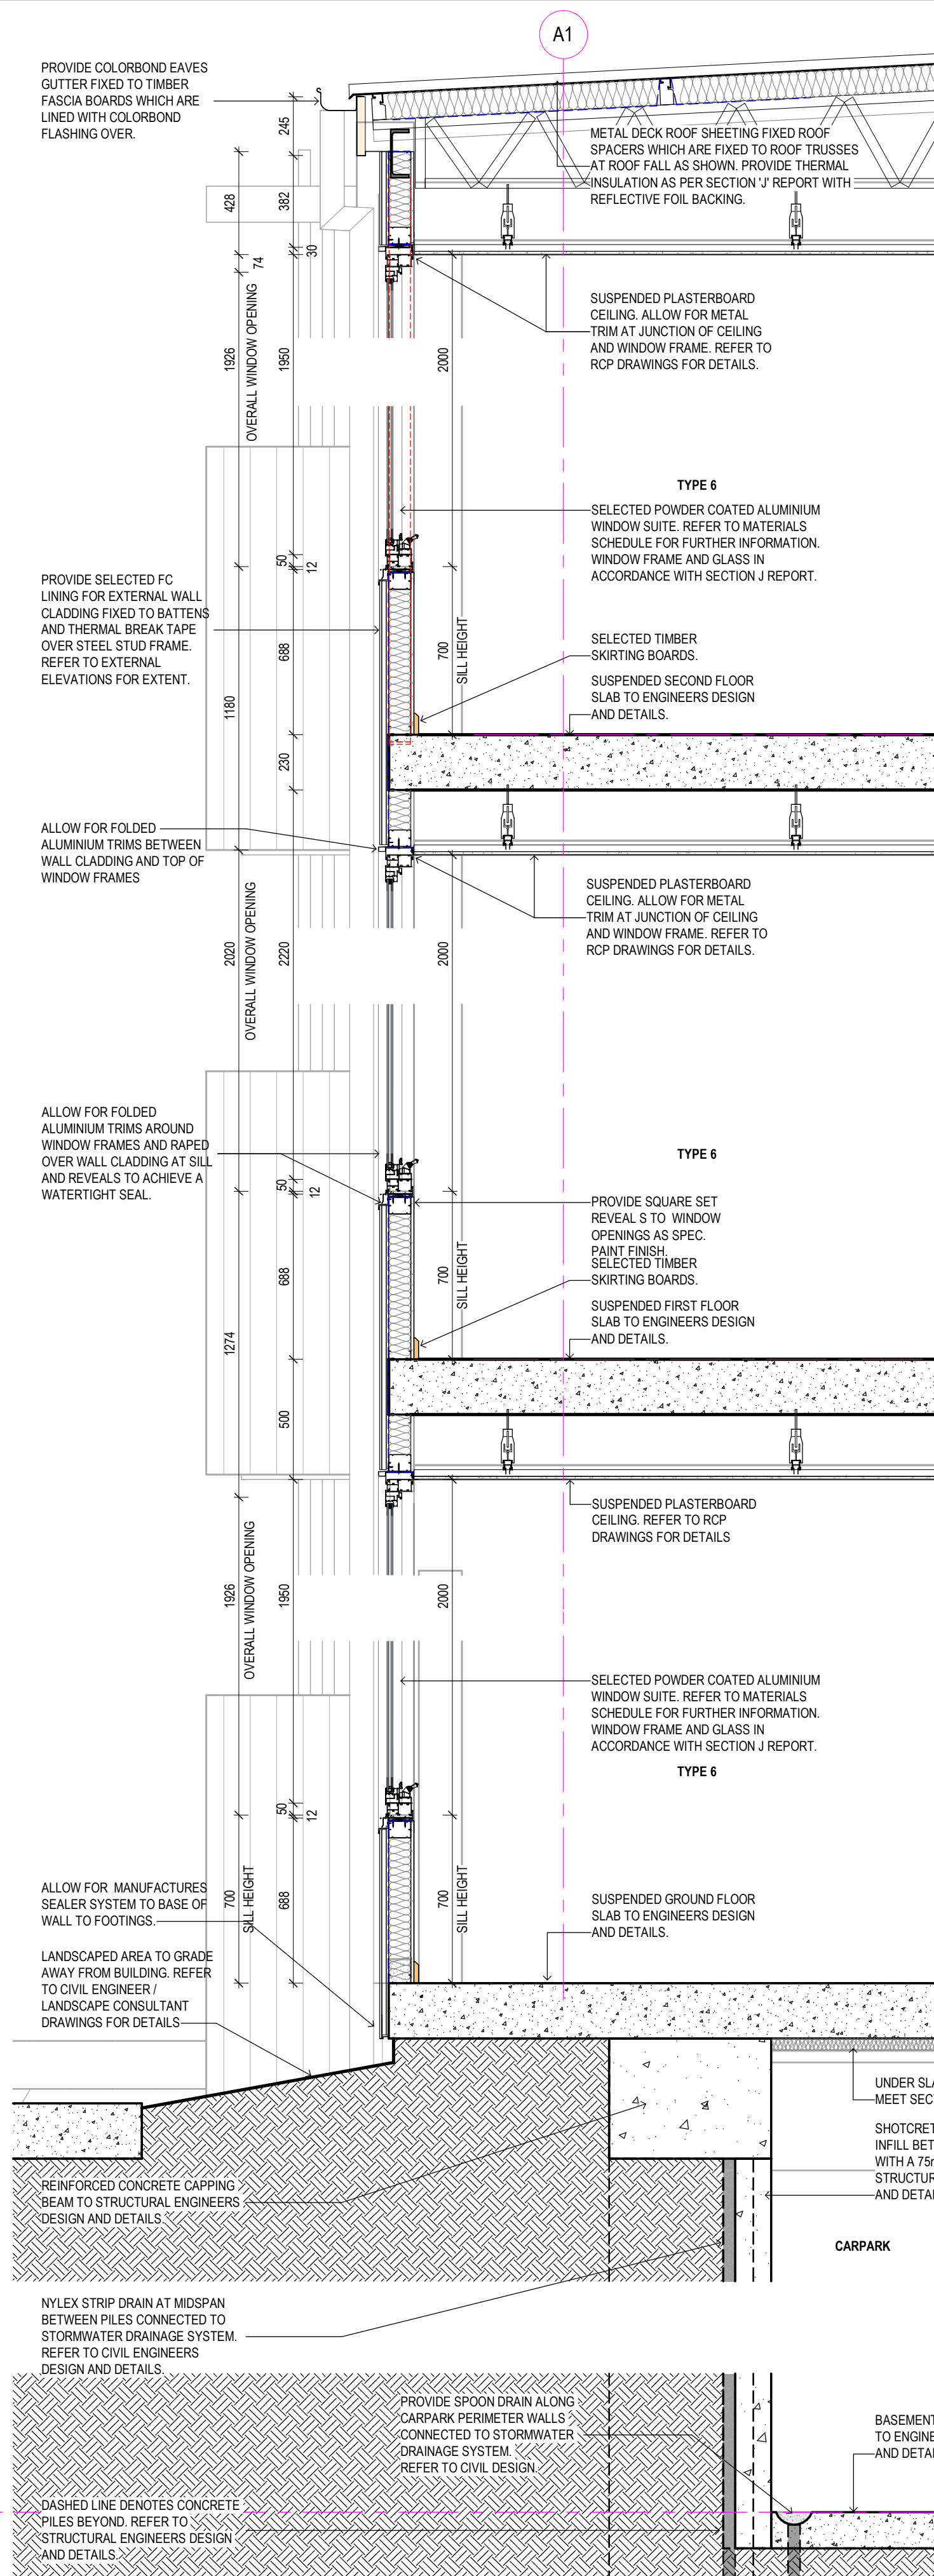

2
F ILA - WALL SECTION 02
Scale 1:20

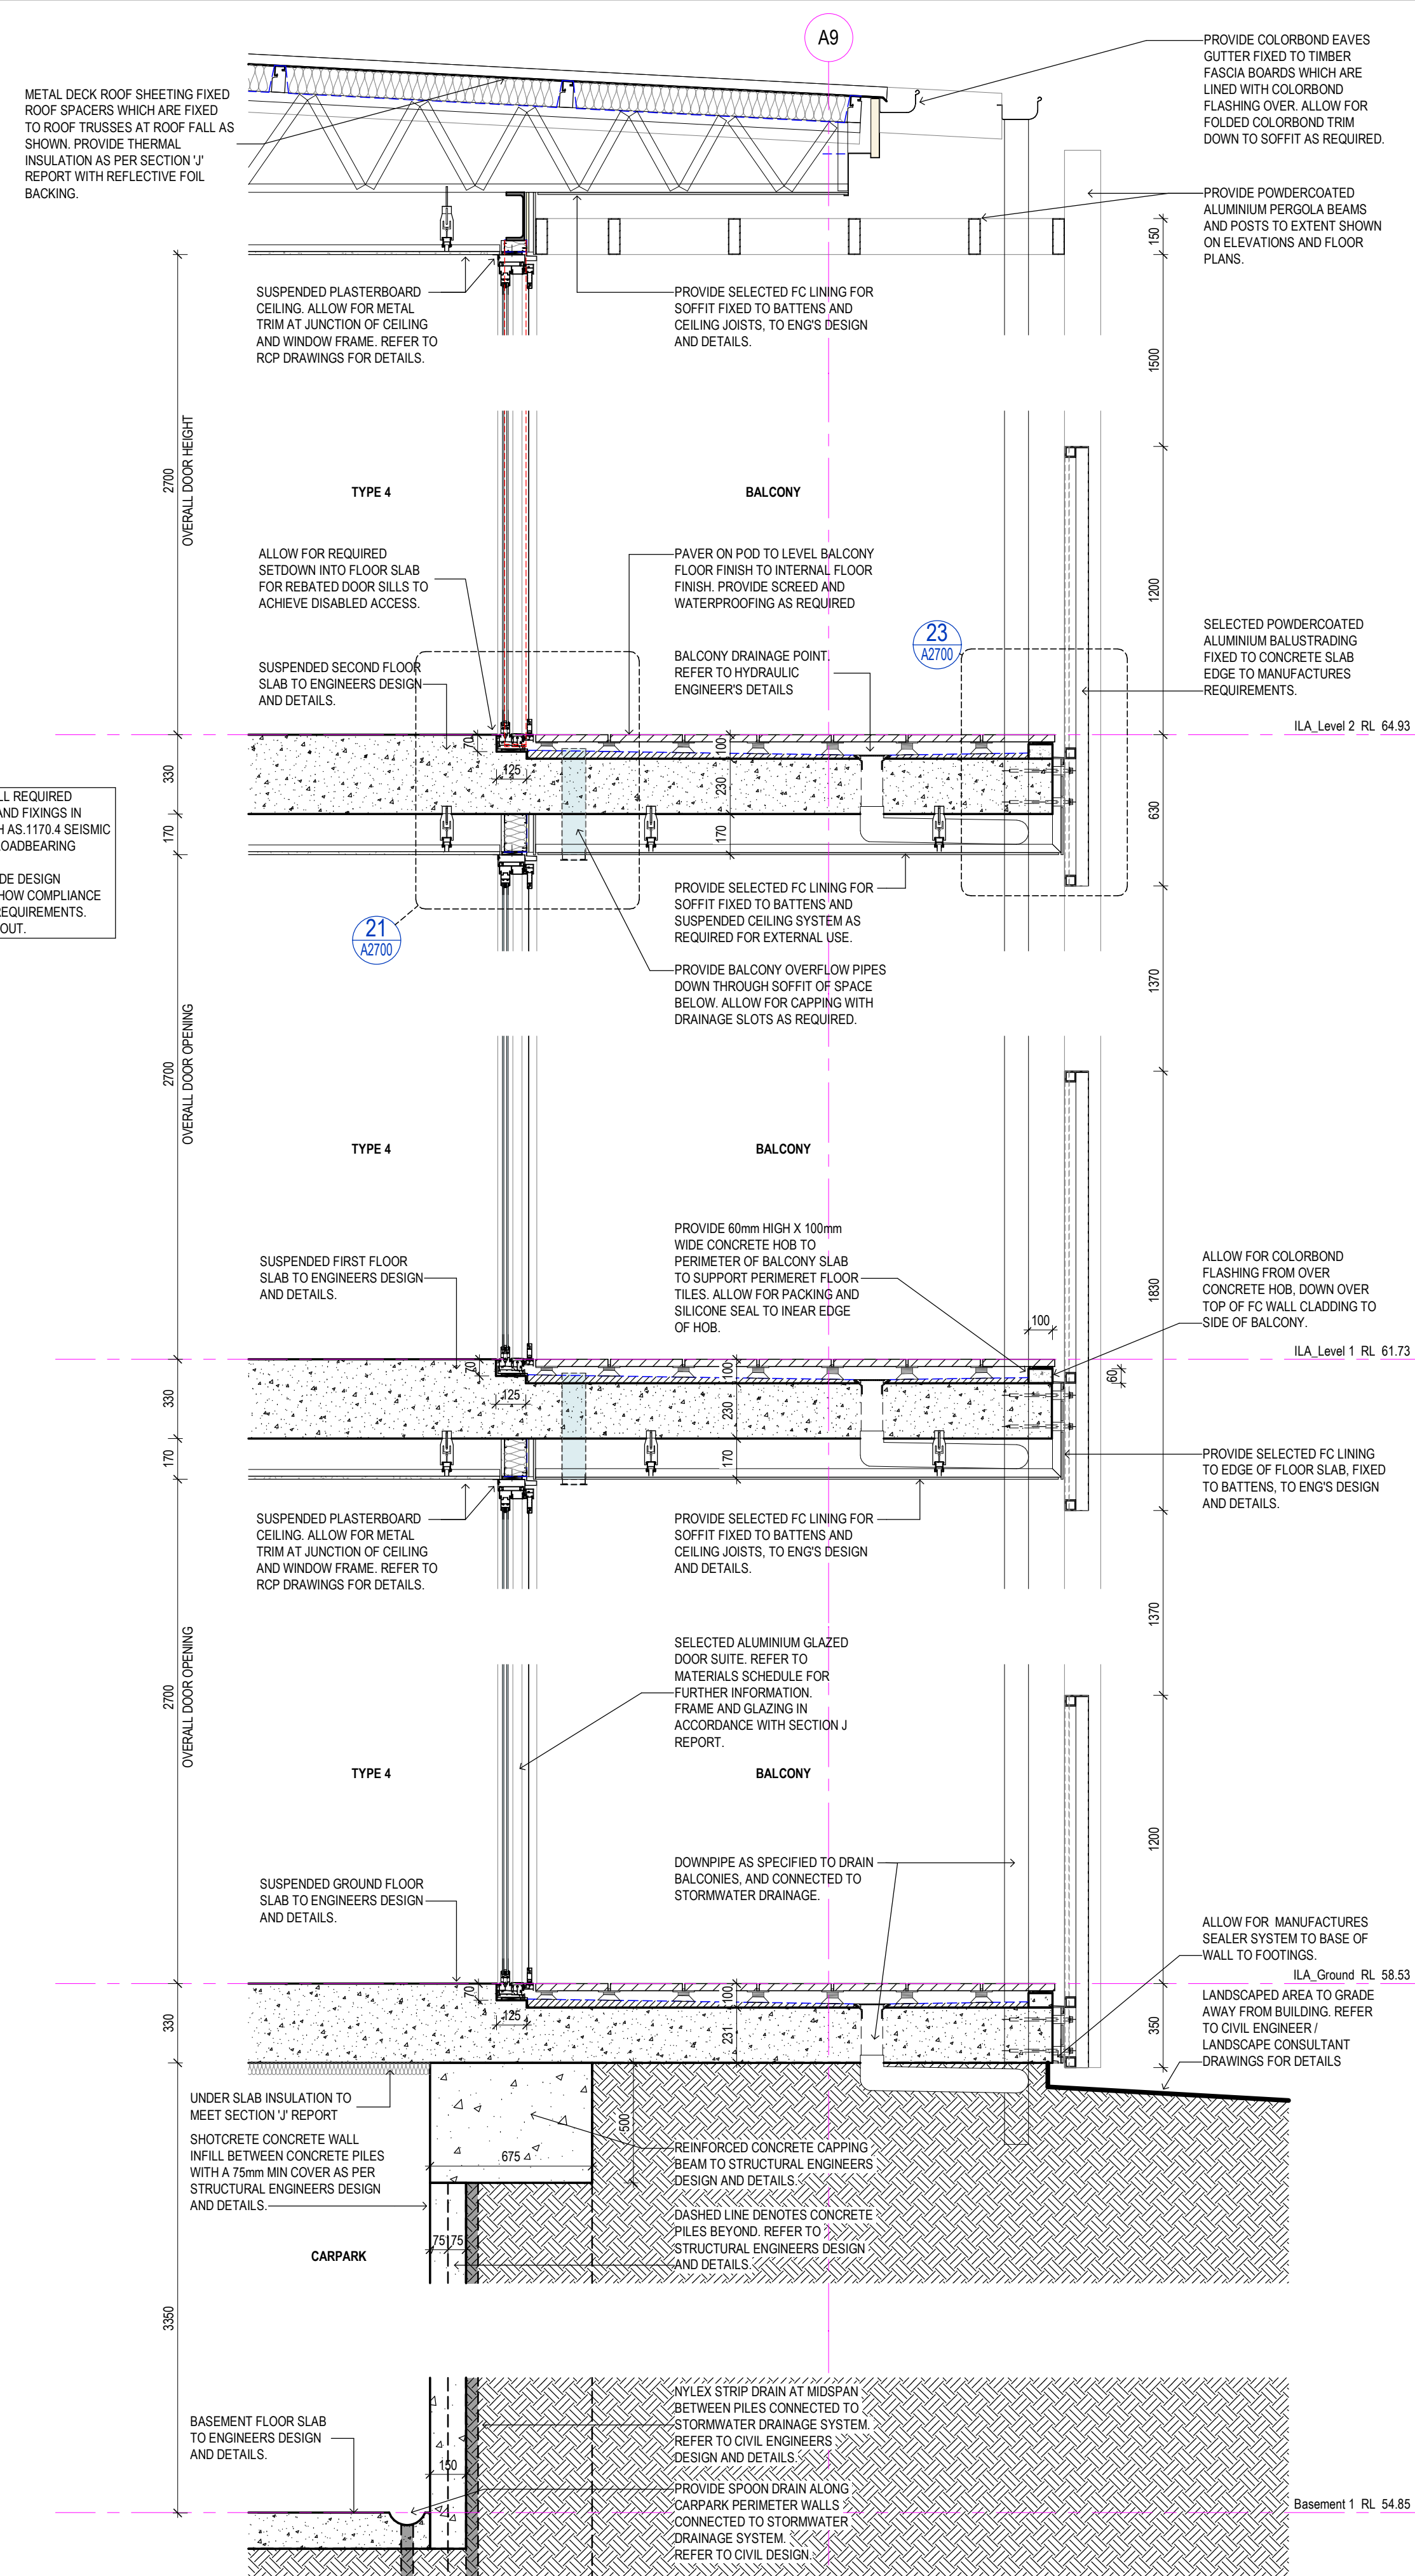

3
F ILA - WALL SECTION 03
Scale 1:20

FOR CONSTRUCTION

Revision/Issue	Date
a Issue for Coordination - 90% DD	2024.03.28
b Issued for Coordination - 100% DD	2024.04.12
P1 ISSUE FOR CONTRACT	2025.10.14
C1 ISSUE FOR CONSTRUCTION	2025.12.19

Clarke Hopkins
architects

ClarkeHopkinsClarke
Melbourne | Wurundjeri
L3, Melbourne Connect
700 Swanston Street
Carlton VIC 3063
Telephone (03) 9419 4340
Email studio@chc.com.au
www.chc.com.au

Sydney | Gadigal Country
Suite 3, Ground Floor
91 Campbell Street
Surry Hills NSW 2010
Telephone (02) 9221 9200
Email studio@chc.com.au
www.chc.com.au

Scale	1:20 @ A1
Date	01/03/2024
Drawn	SG
Architect	EL

Project
Summerset Oakleigh
52 Golf Road, Oakleigh South, VIC

Drawing
Wall Sections - Sheet 1

Drawing No.
230185/A2650
c1