




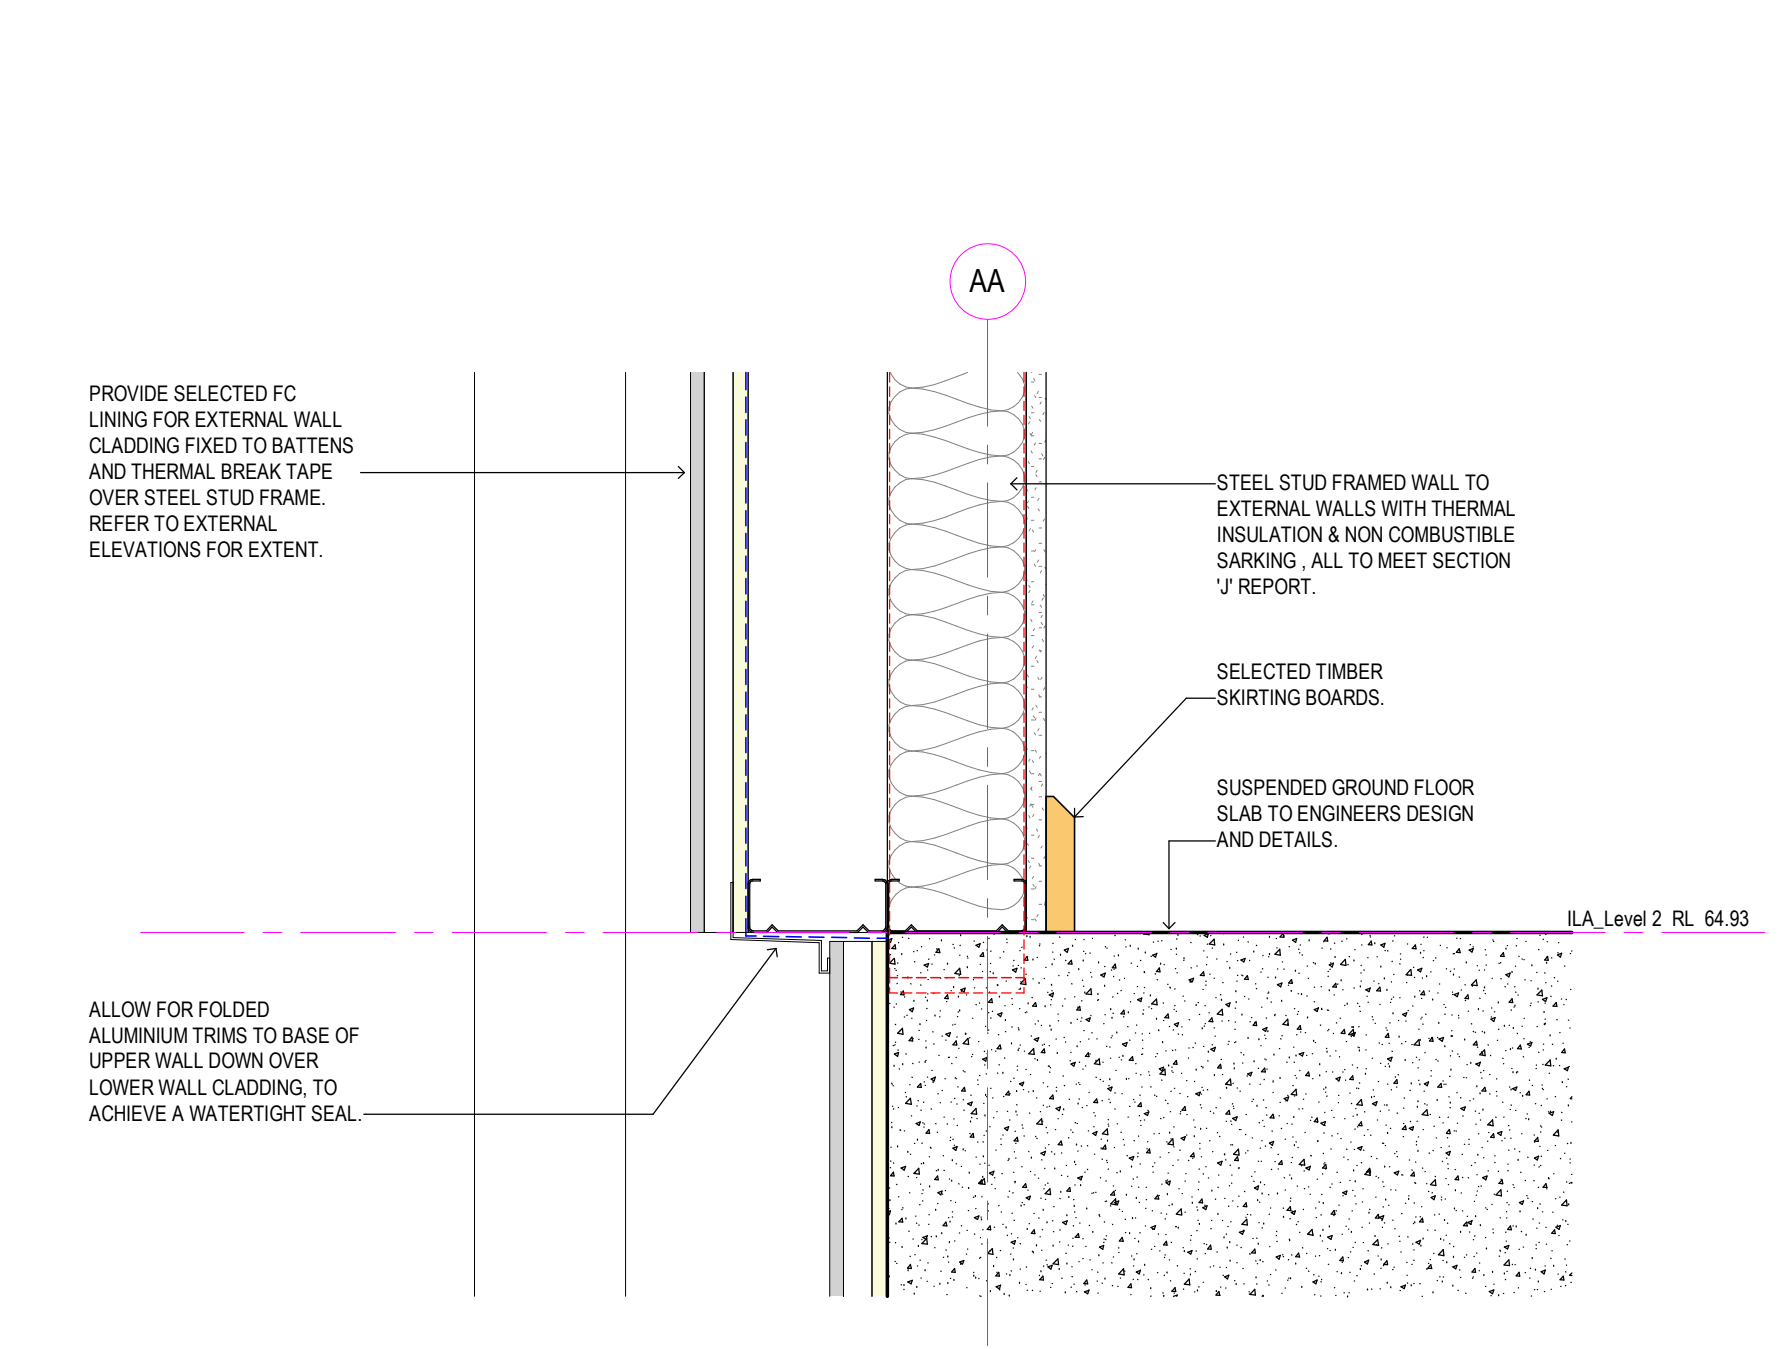


20 DETAIL 20
Scale 1:5

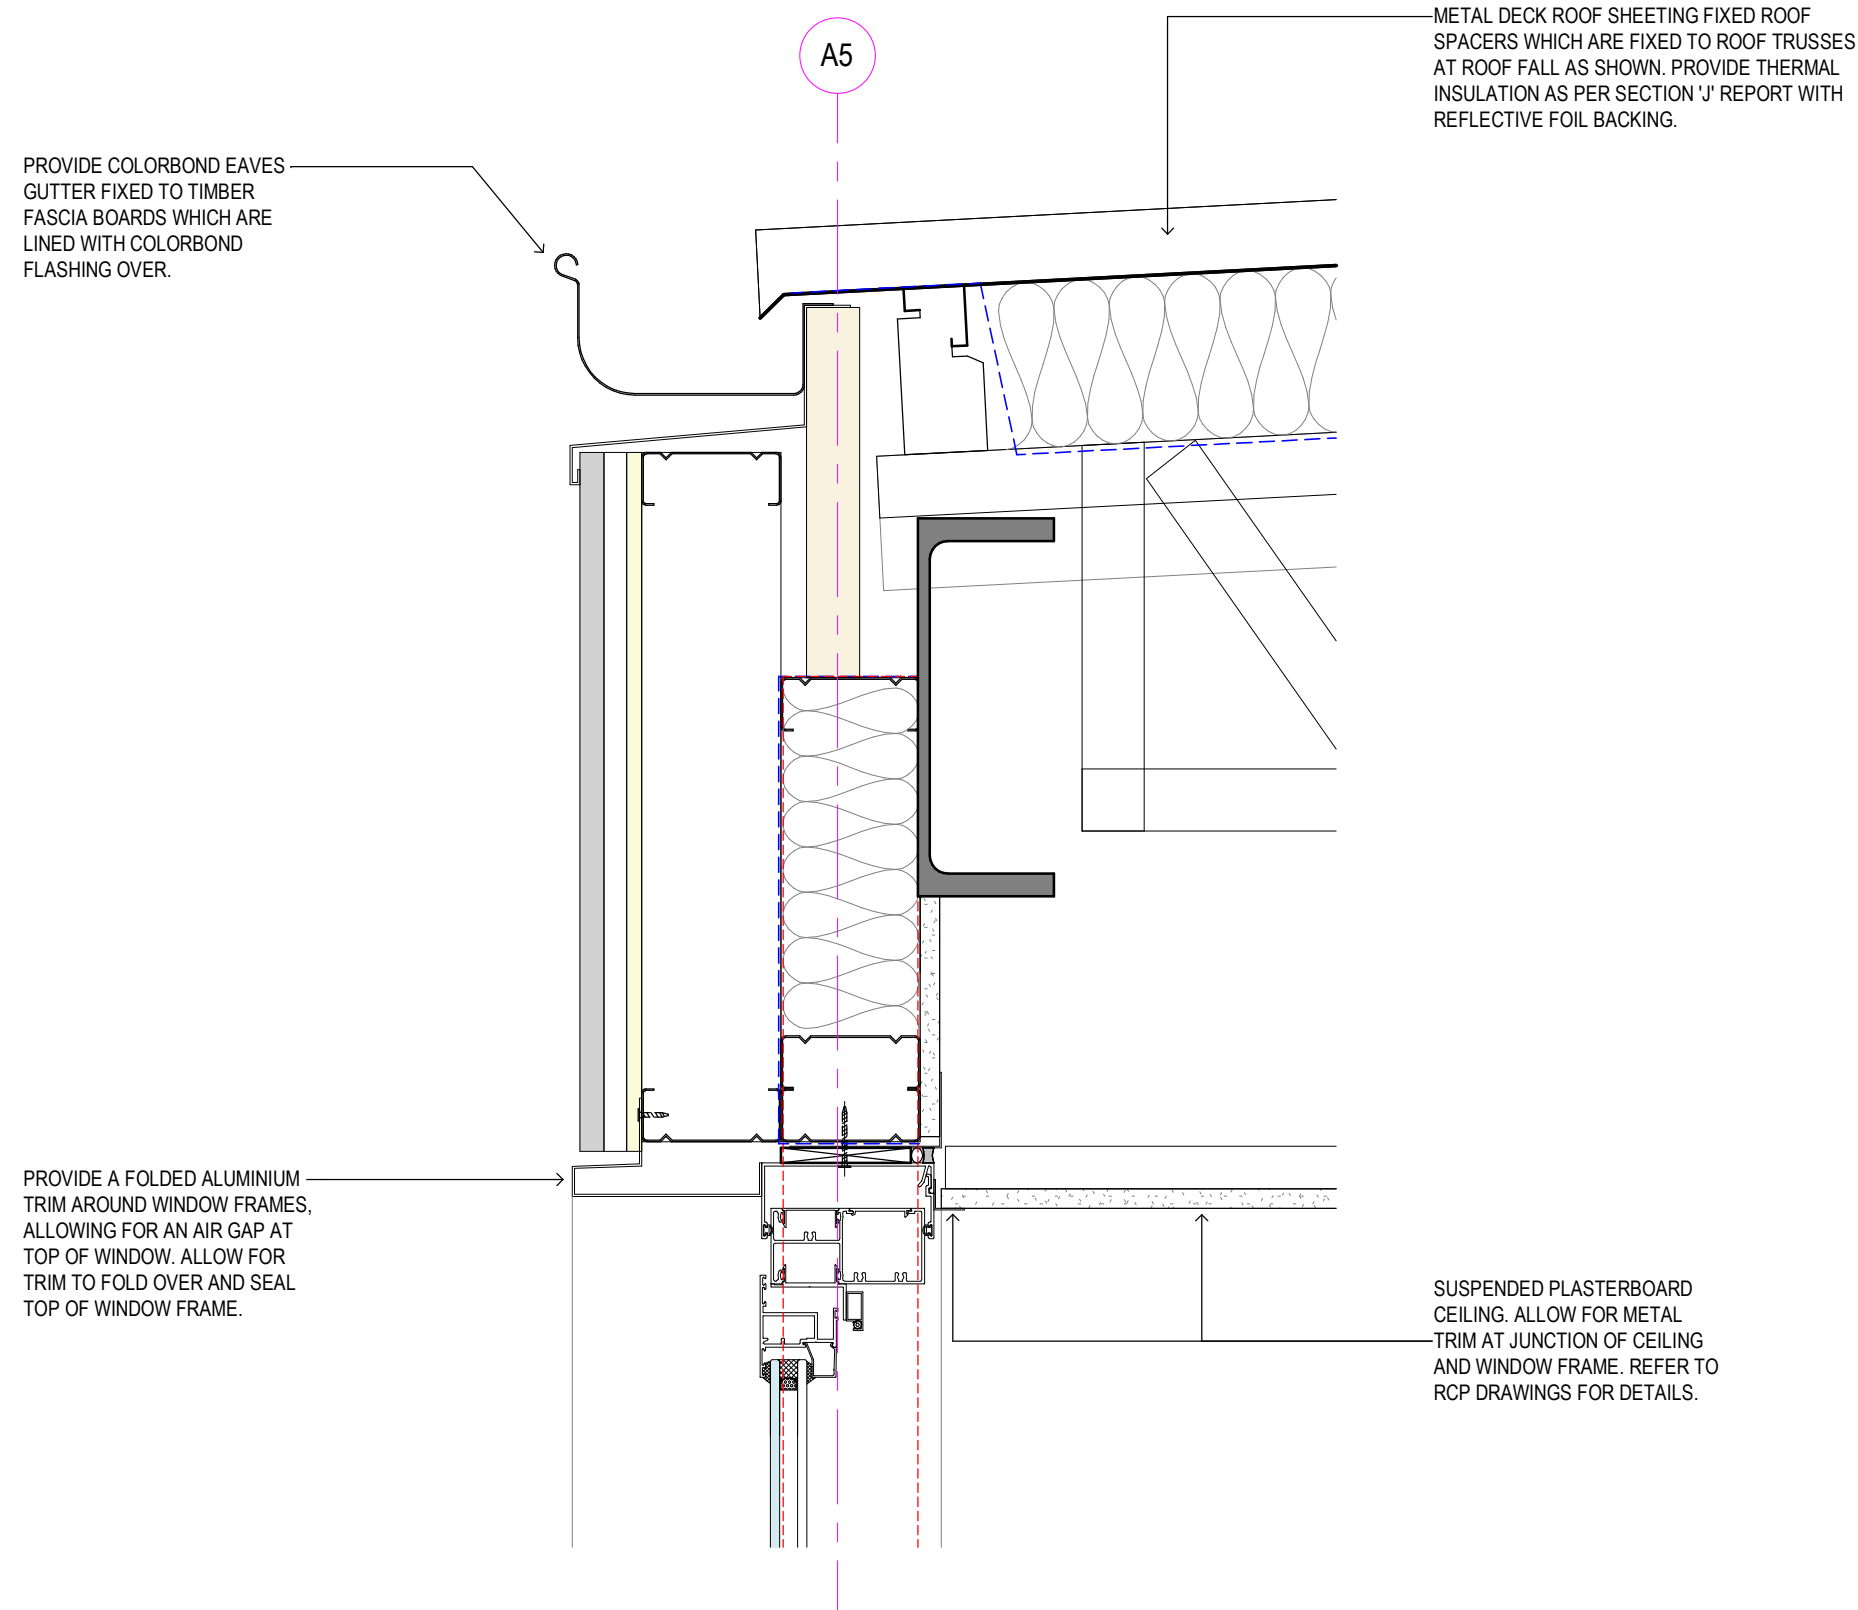

22 DETAIL 22
Scale 1:5

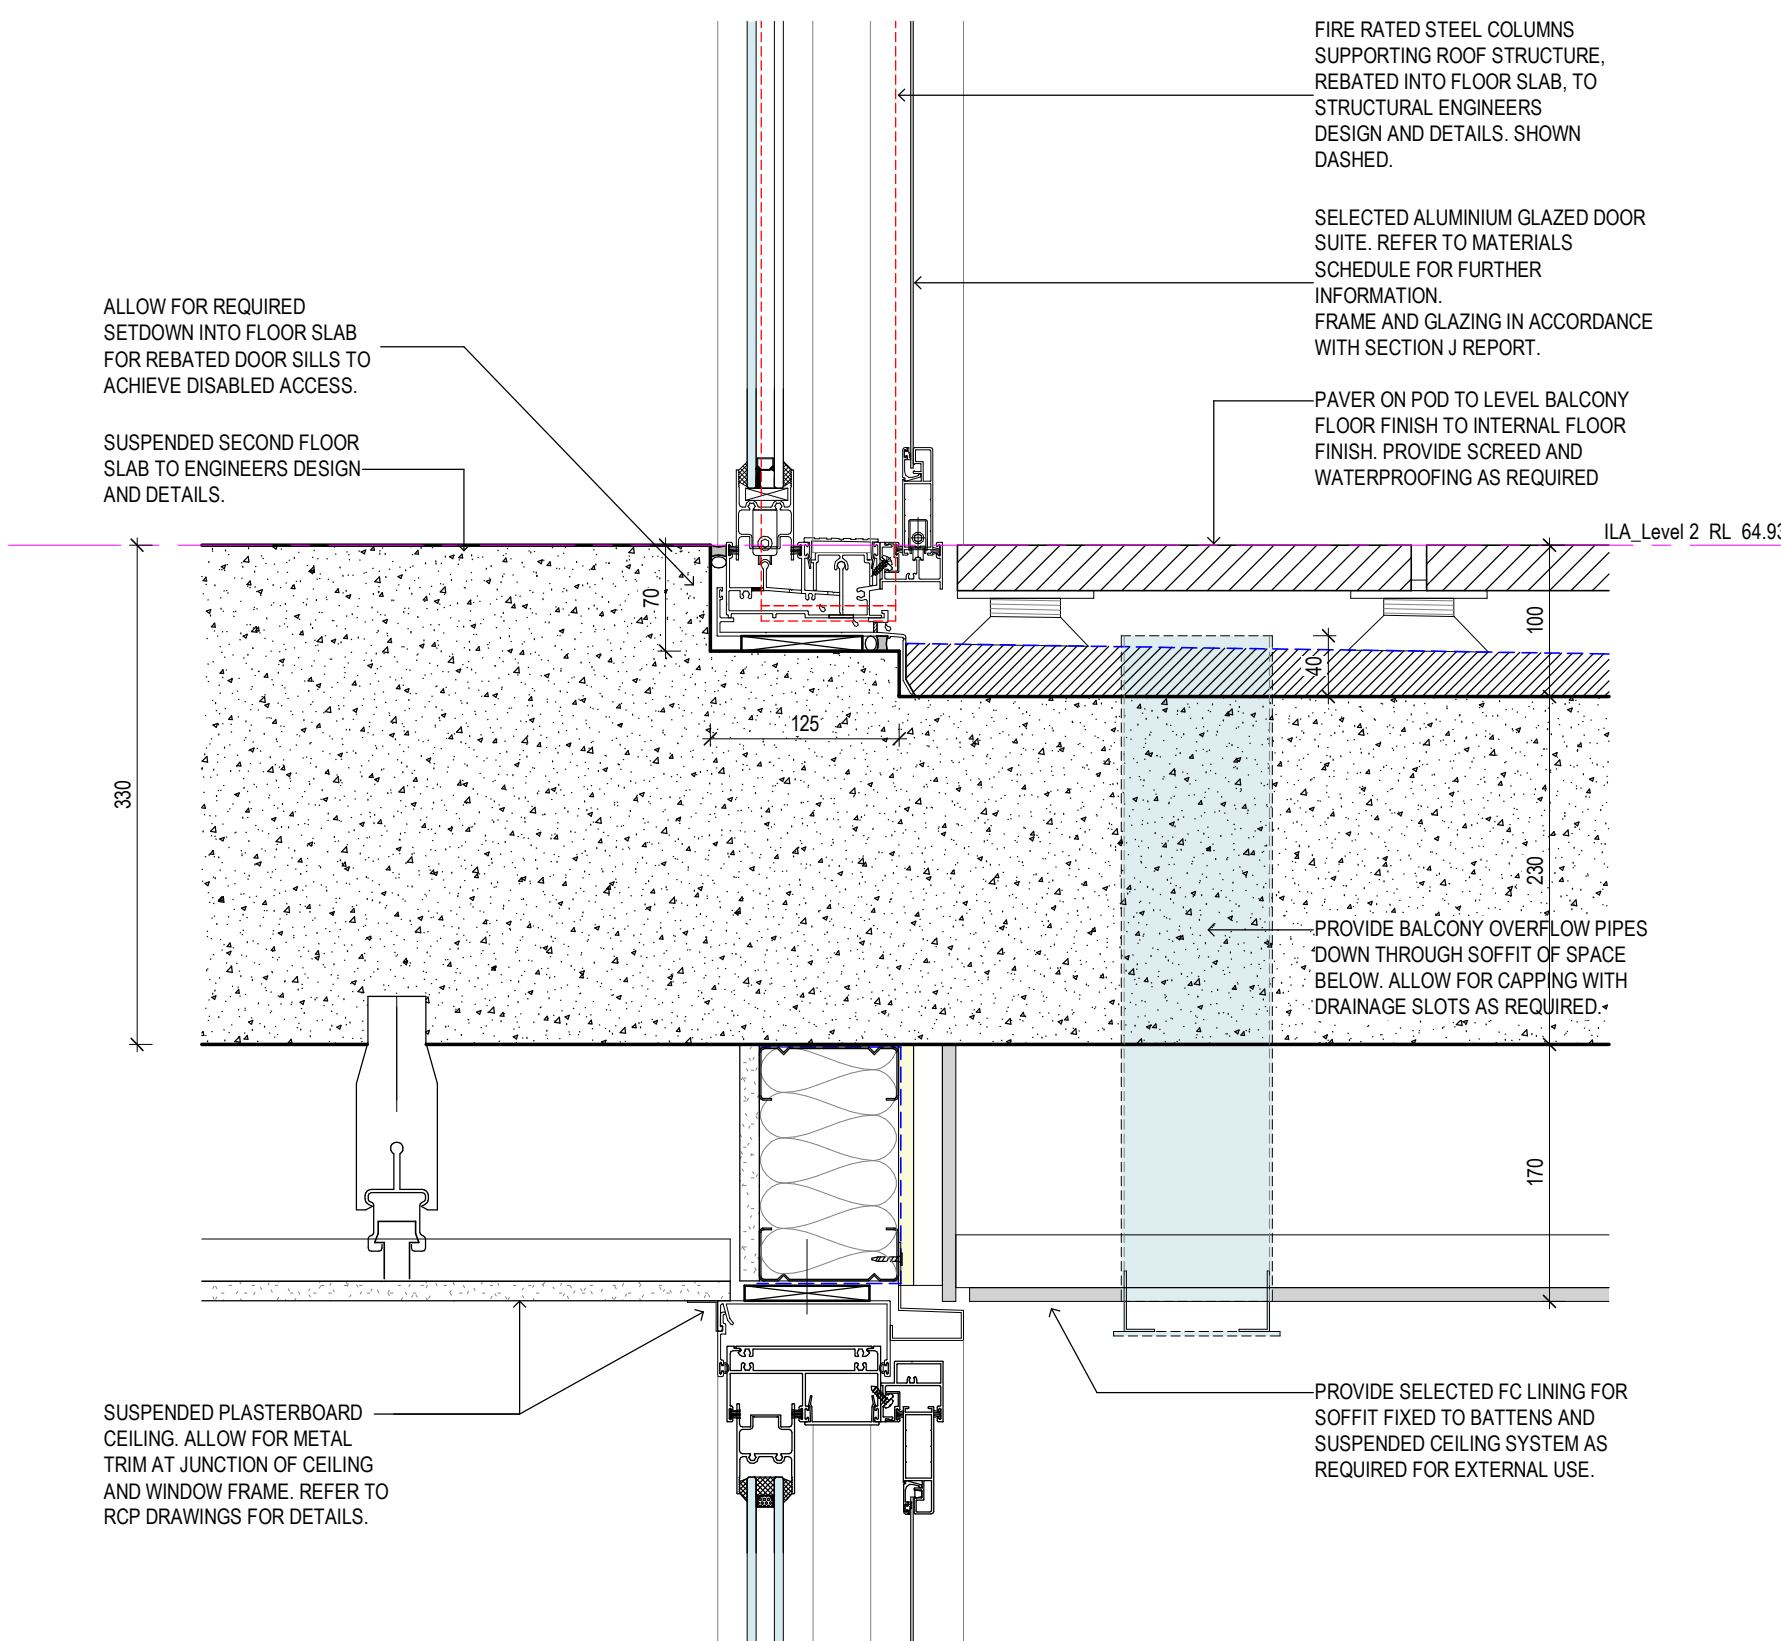


21 DETAIL 21
Scale 1:5

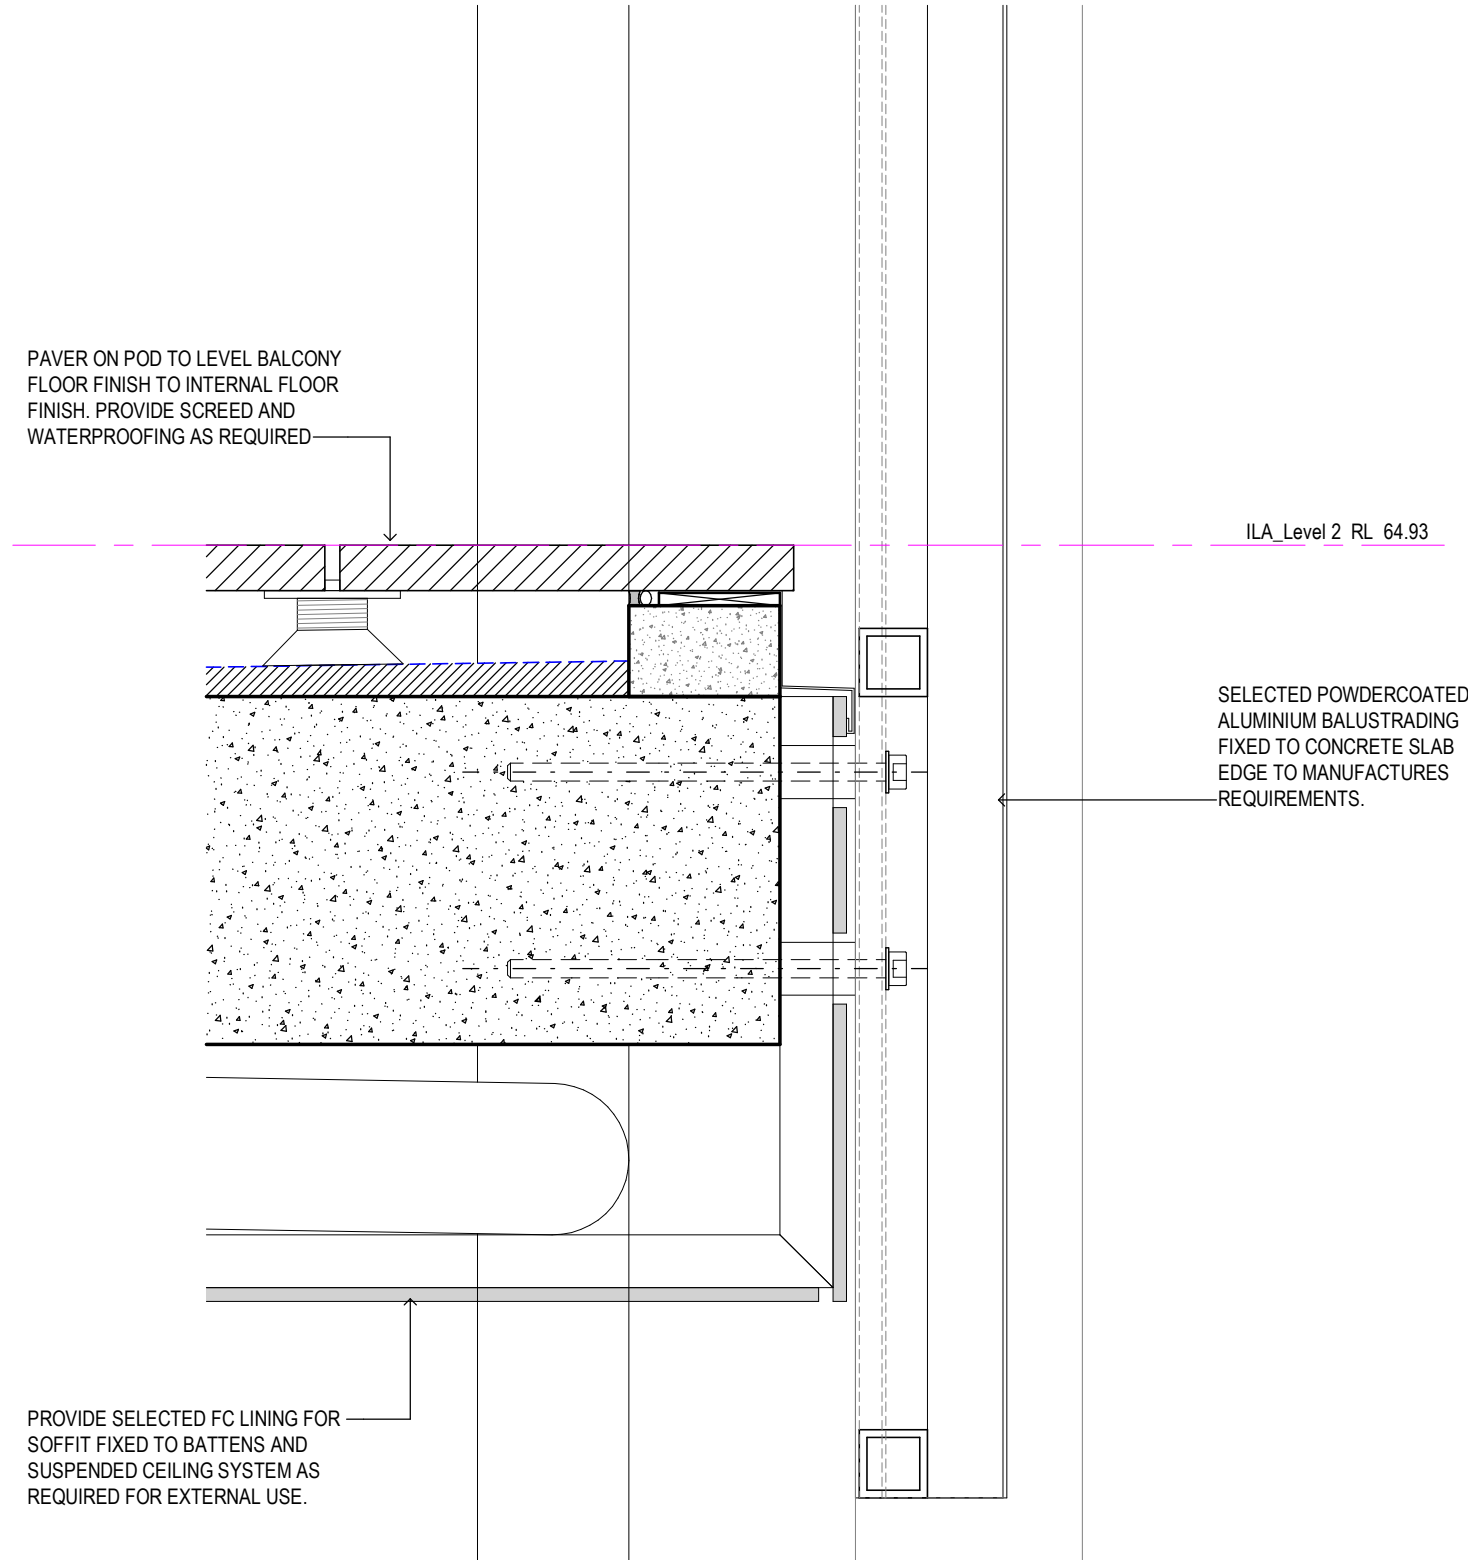

23 DETAIL 23
Scale 1:5

Revision/Issue	Date
C1 ISSUE FOR CONSTRUCTION	2025.12.19

 

**Clarke
Hopkins
Architects**

ClarkeHopkinsClarke

Melbourne | Wurundjeri
L9, Melbourne Connect
700 Swanston Street
Carlton VIC 3063
Telephone (03) 9419 4340
Email studio@chc.com.au
www.chc.com.au

Sydney | Gadigal Country
Suite 3, Ground Floor
91 Campbell Street
Surry Hills NSW 2010
Telephone (02) 9221 9200
Email studio@chc.com.au
www.chc.com.au

Scale	1:5 @ A1
Date	01/03/2024
Drawn	SG
Architect	EL

Project	Summerset Oakleigh 52 Golf Road, Oakleigh South, VIC
---------	---

Drawing	Section Details - Sheet 1
---------	---------------------------

Drawing No.	230185/A2700	C1
-------------	--------------	----

FOR CONSTRUCTION