




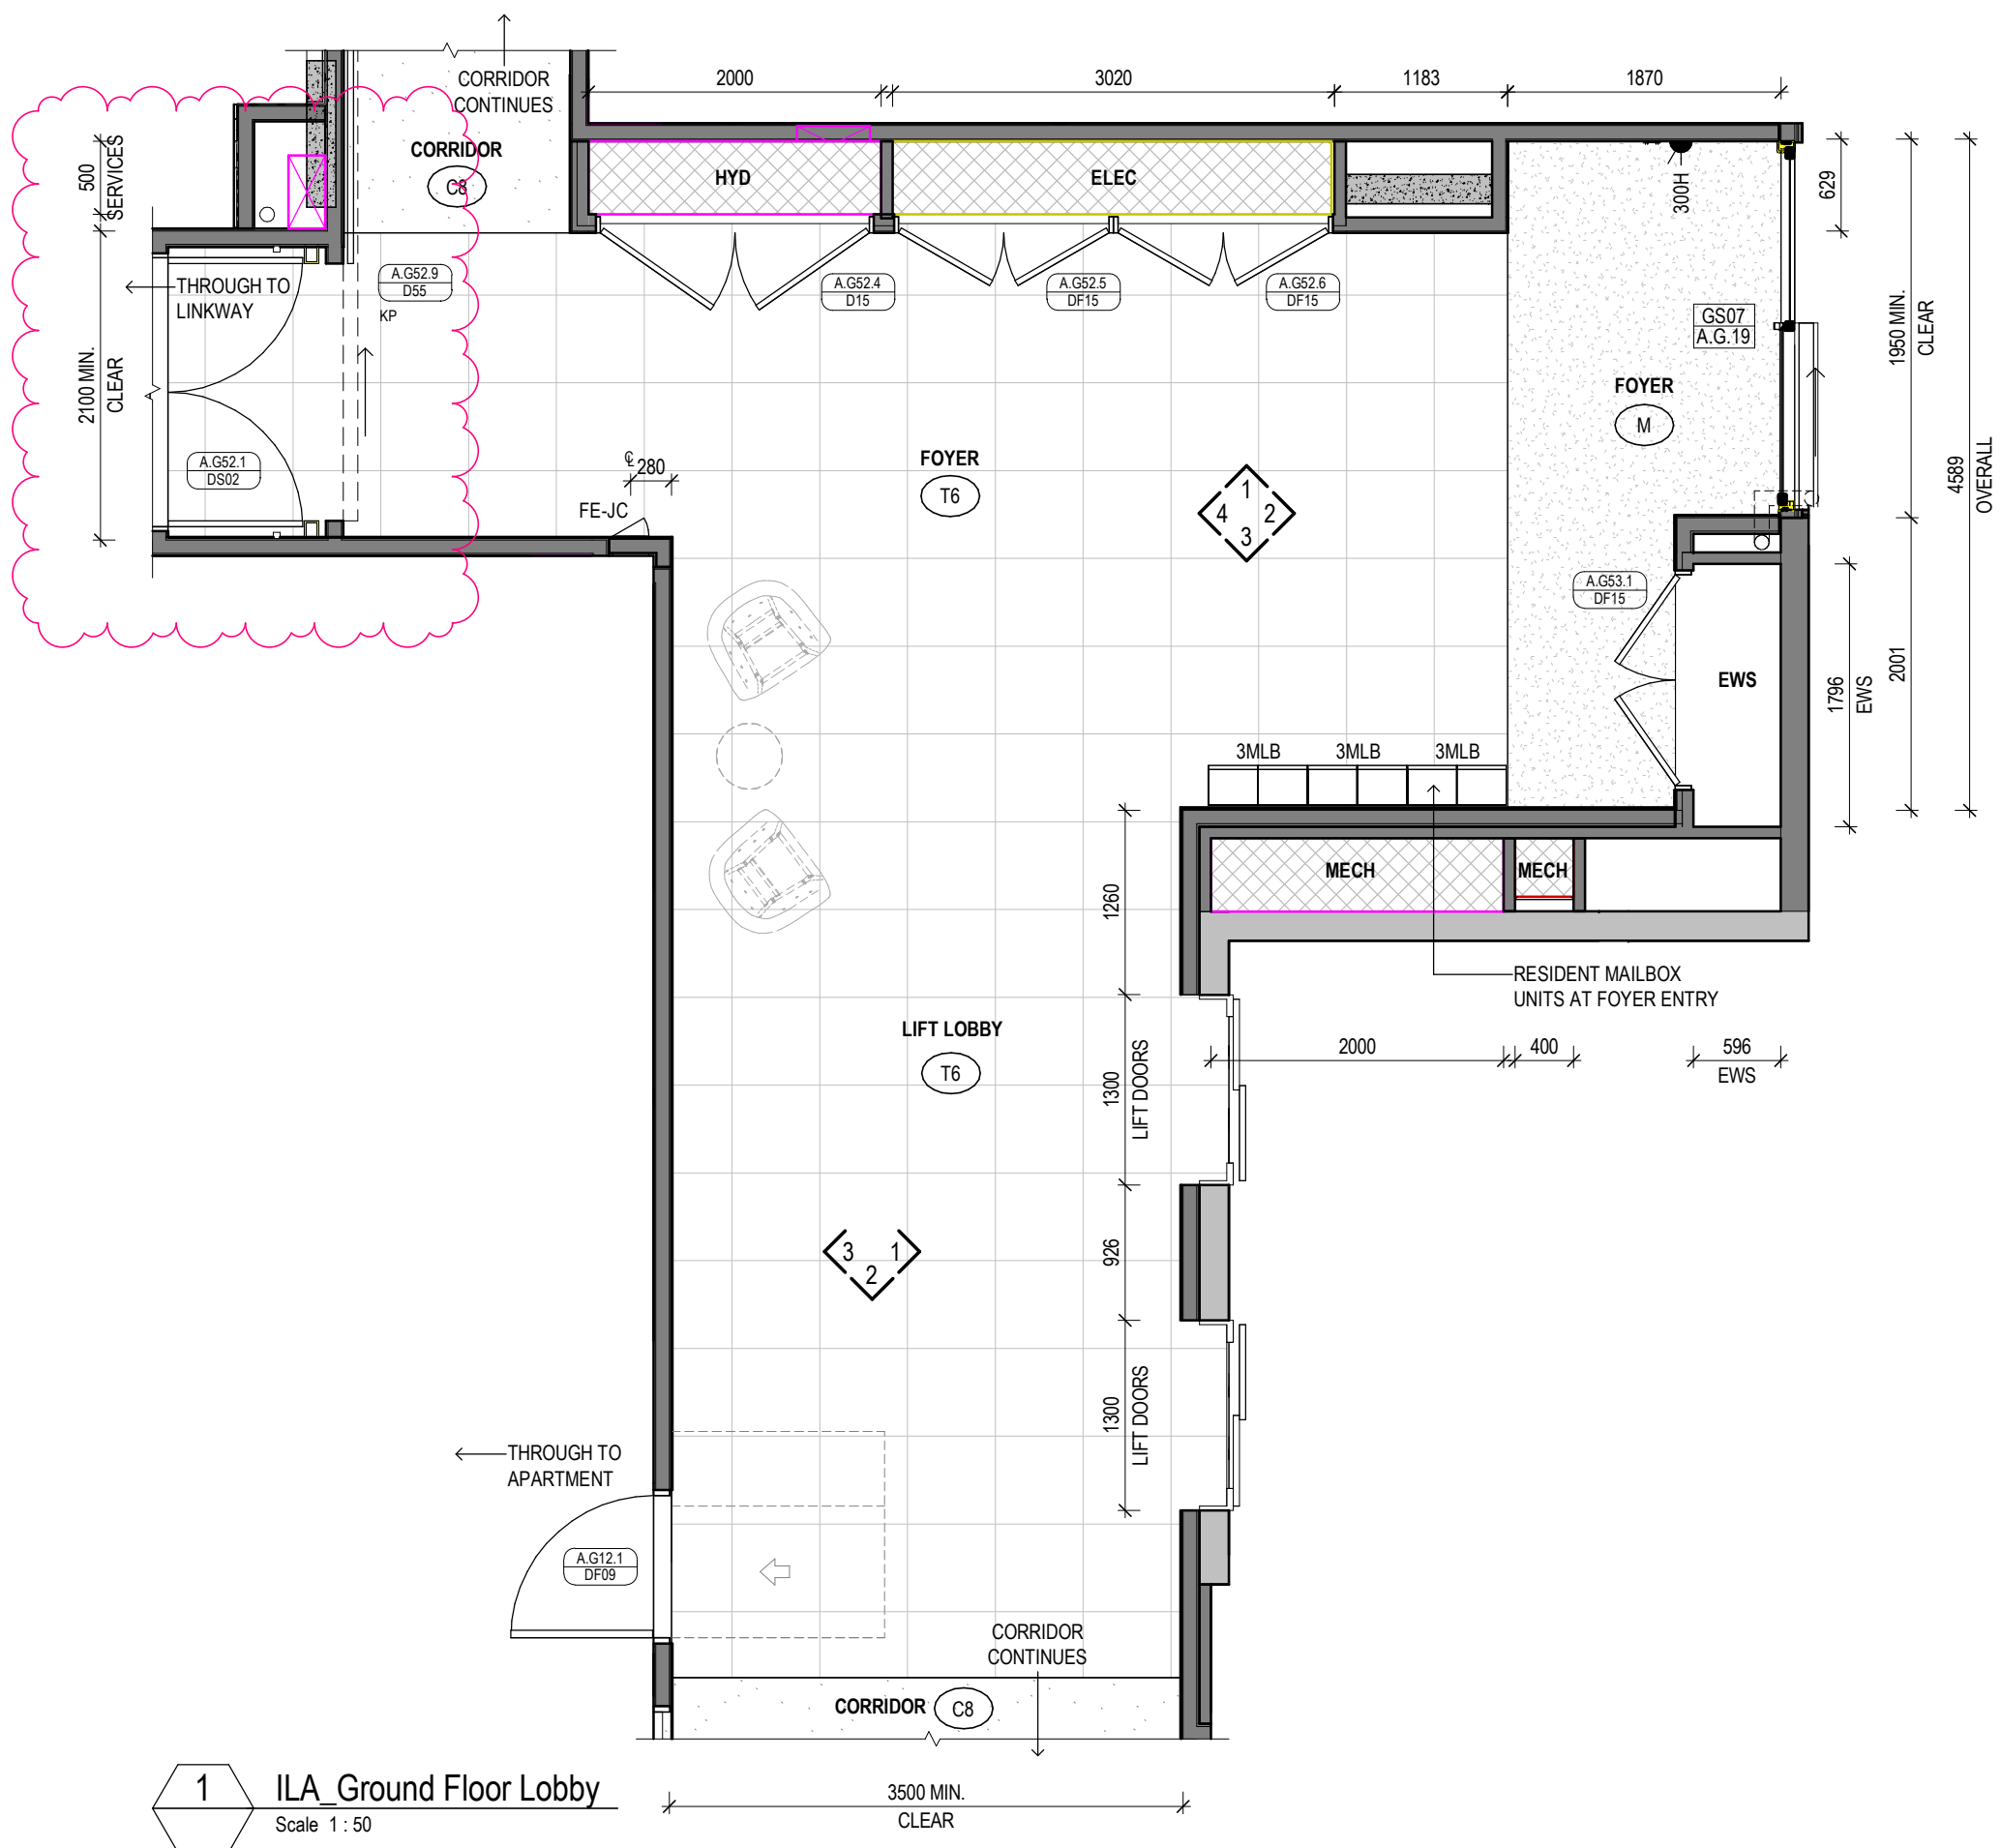


1 ILA Ground Floor Lobby
Scale 1 : 50

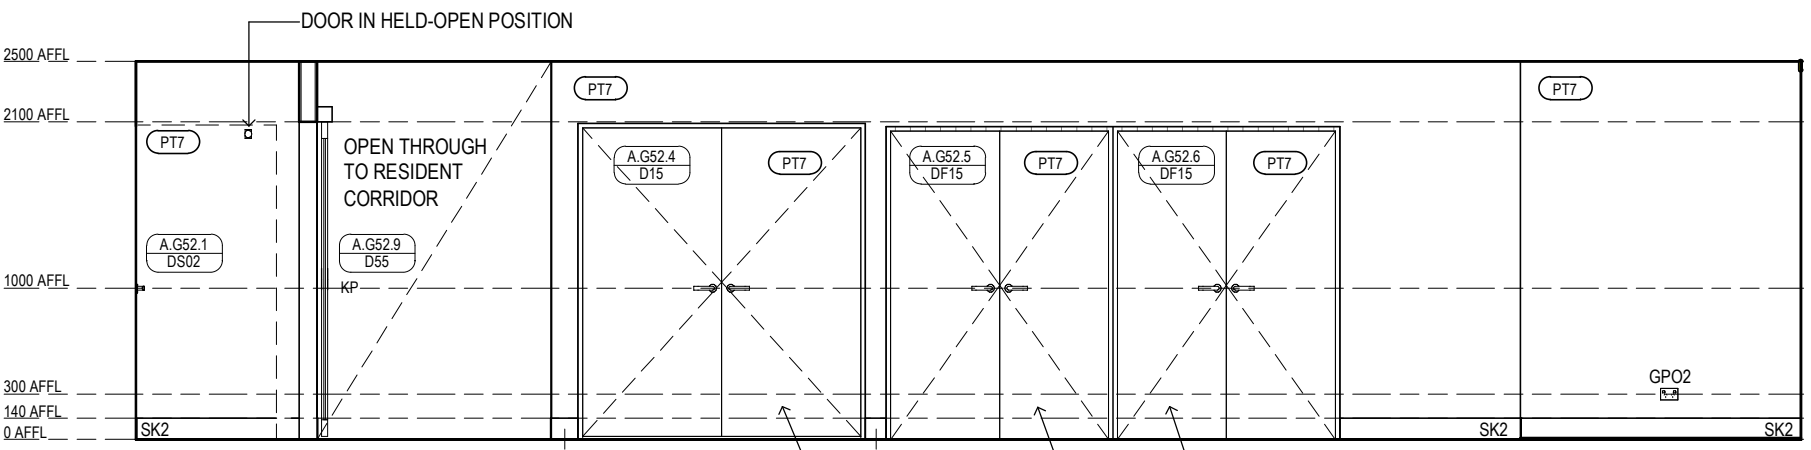


ILA GROUND FLOOR - FOYER
ELEVATION 1
Scale 1 : 50

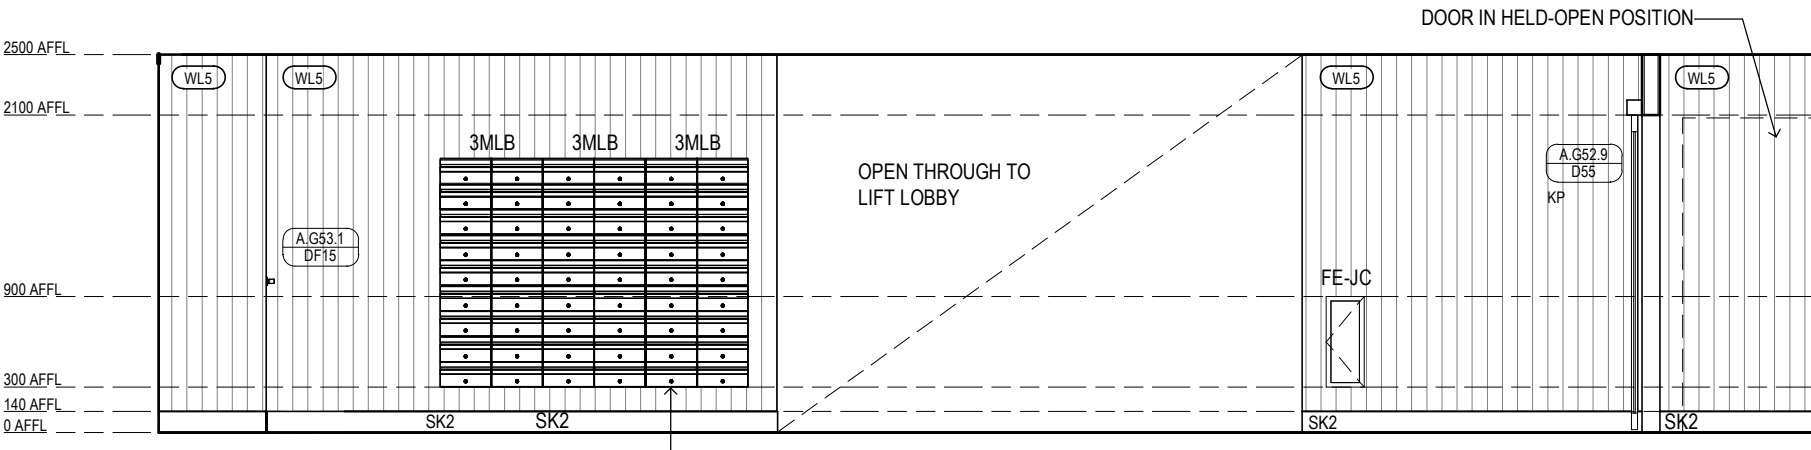


ILA GROUND FLOOR - FOYER
ELEVATION 3
Scale 1 : 50

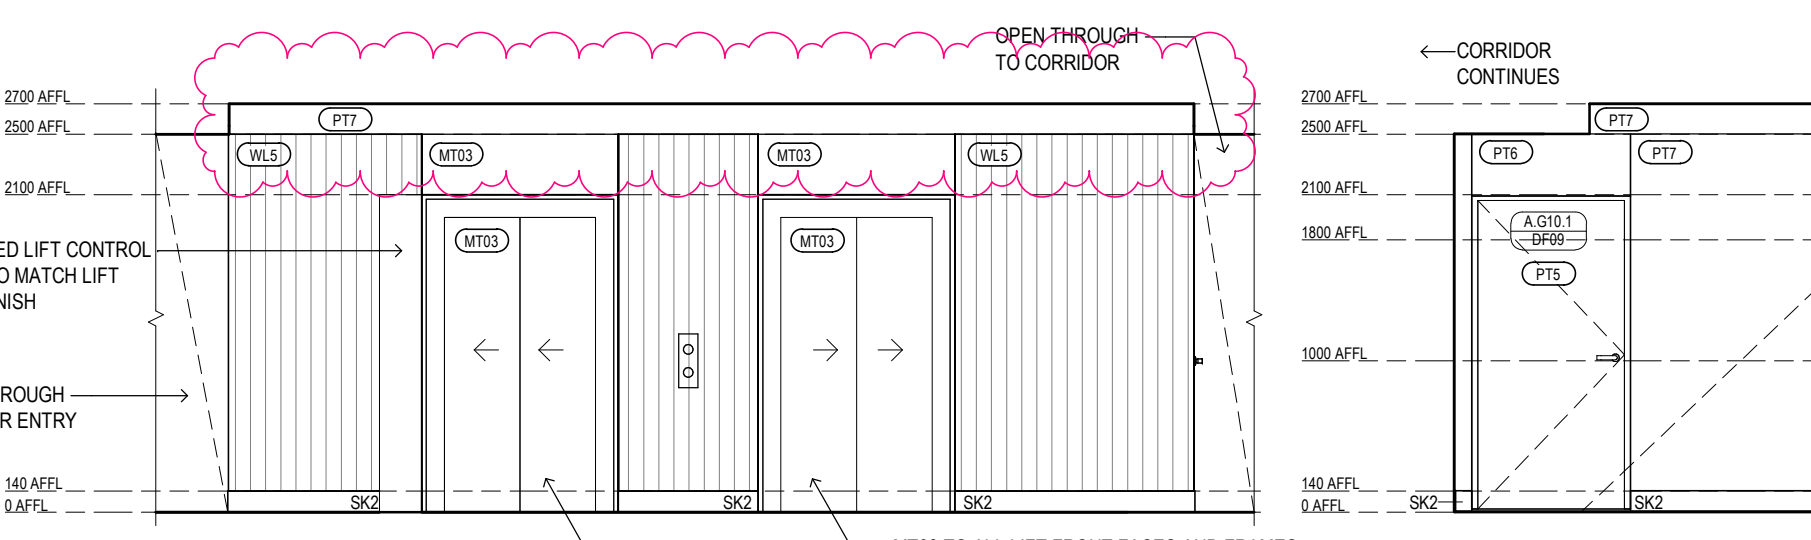


ILA GROUND FLOOR - LIFT LOBBY
ELEVATION 1
Scale 1 : 50

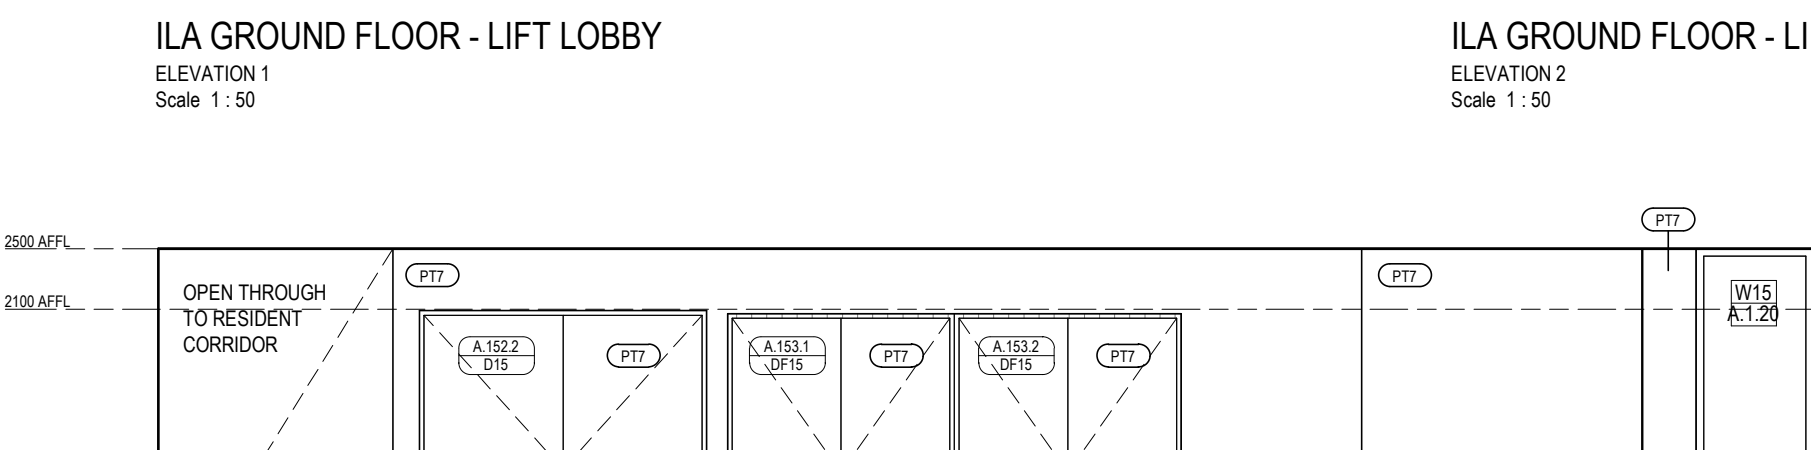


ILA GROUND FLOOR - LIFT LOBBY
ELEVATION 2
Scale 1 : 50

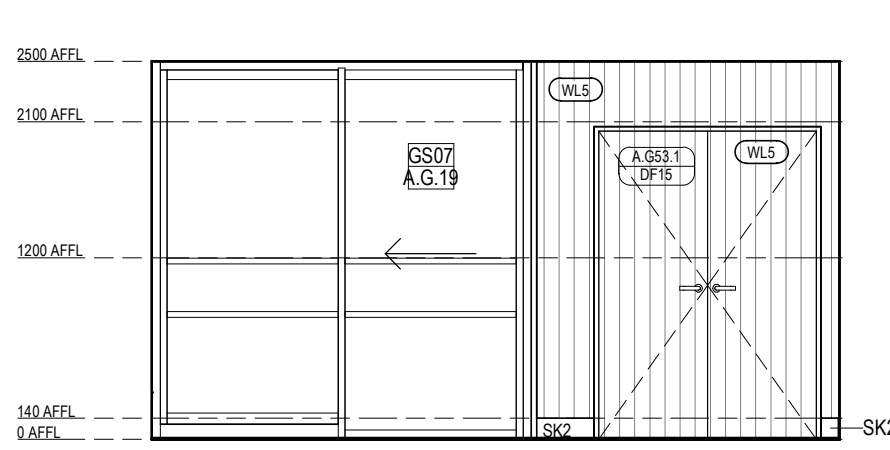


ILA GROUND FLOOR - FOYER
ELEVATION 2
Scale 1 : 50

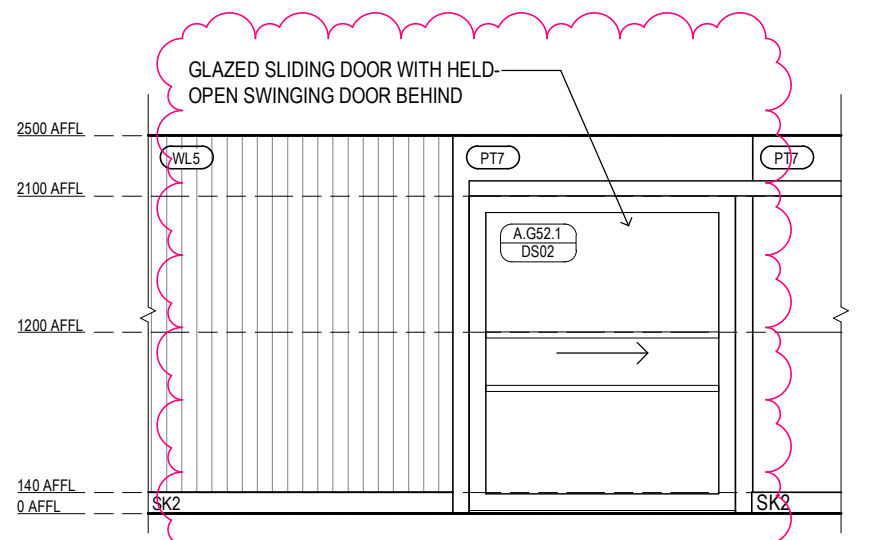


ILA GROUND FLOOR - FOYER
ELEVATION 4
Scale 1 : 50

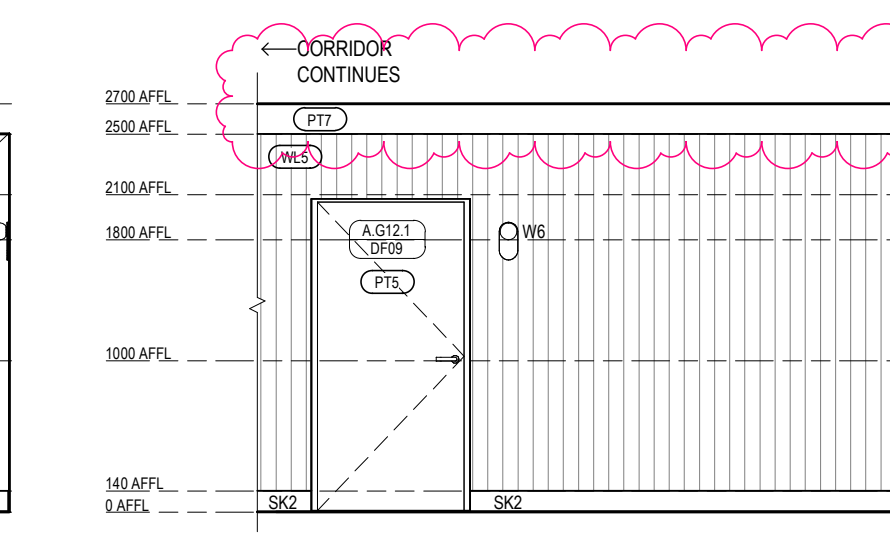


ILA Ground Floor Lift Lobby
ELEVATION 3
Scale 1 : 50

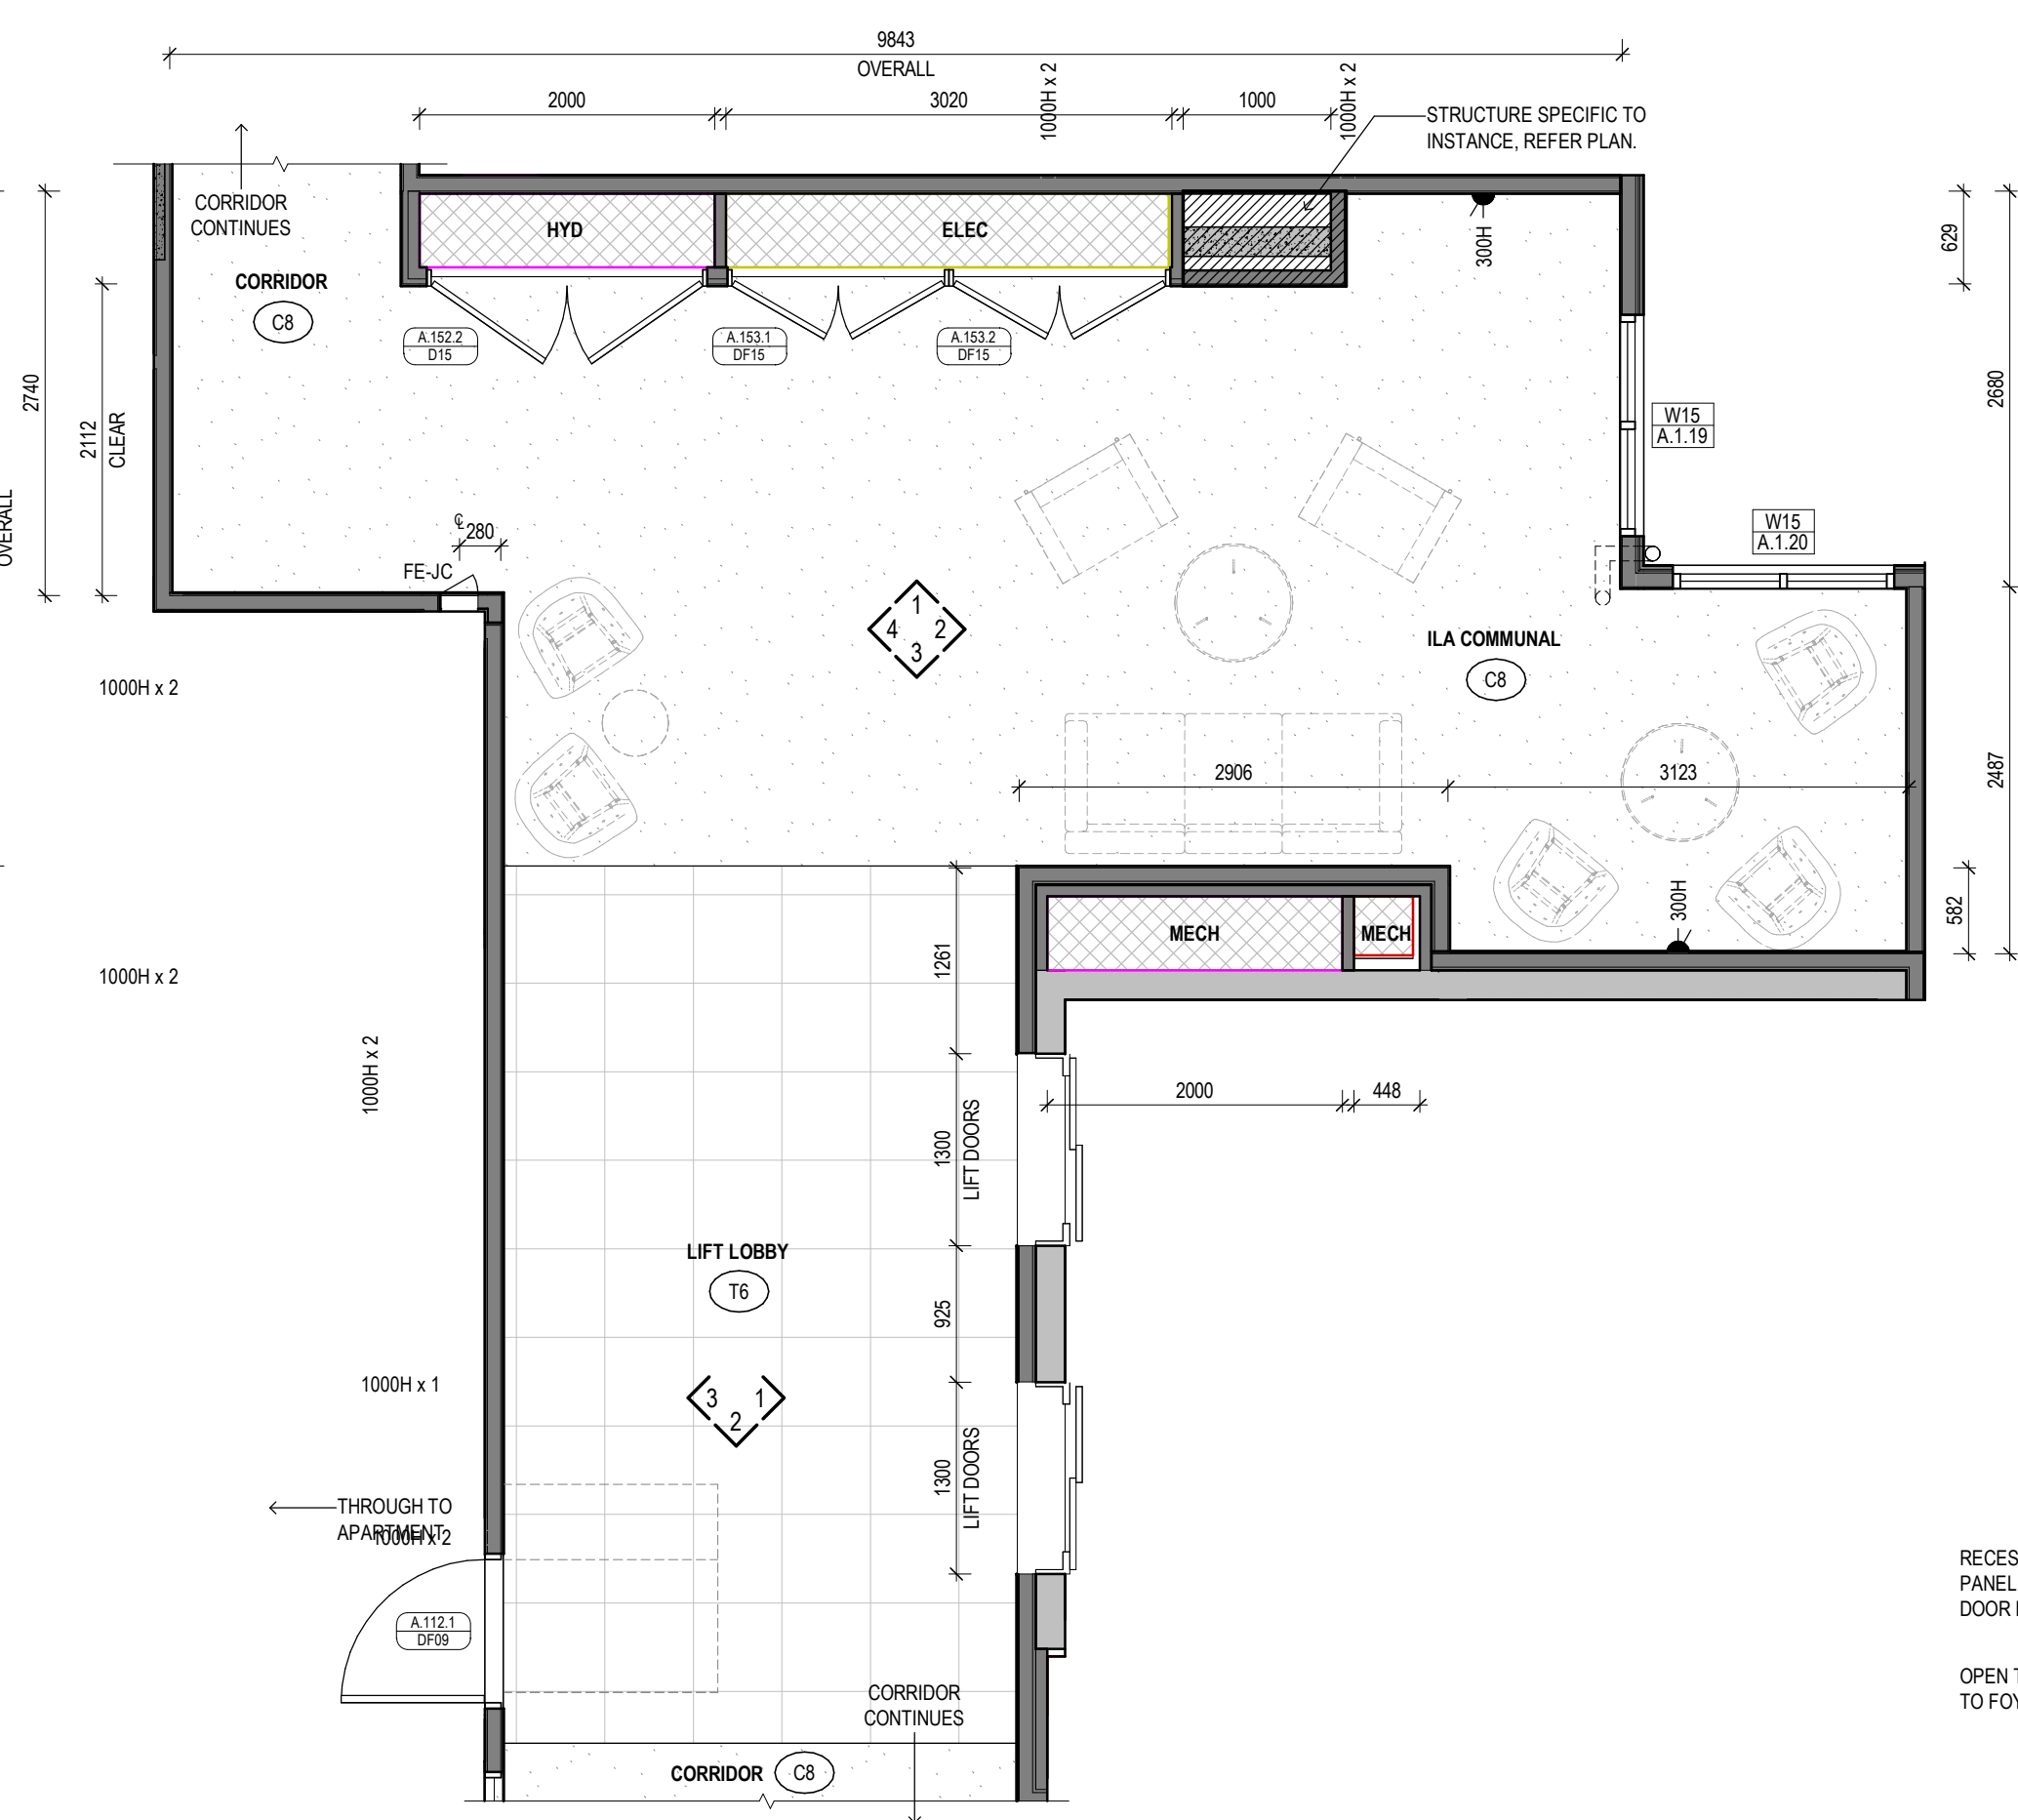


2 ILA L1+2 Lobby and Communal Space
Scale 1 : 50

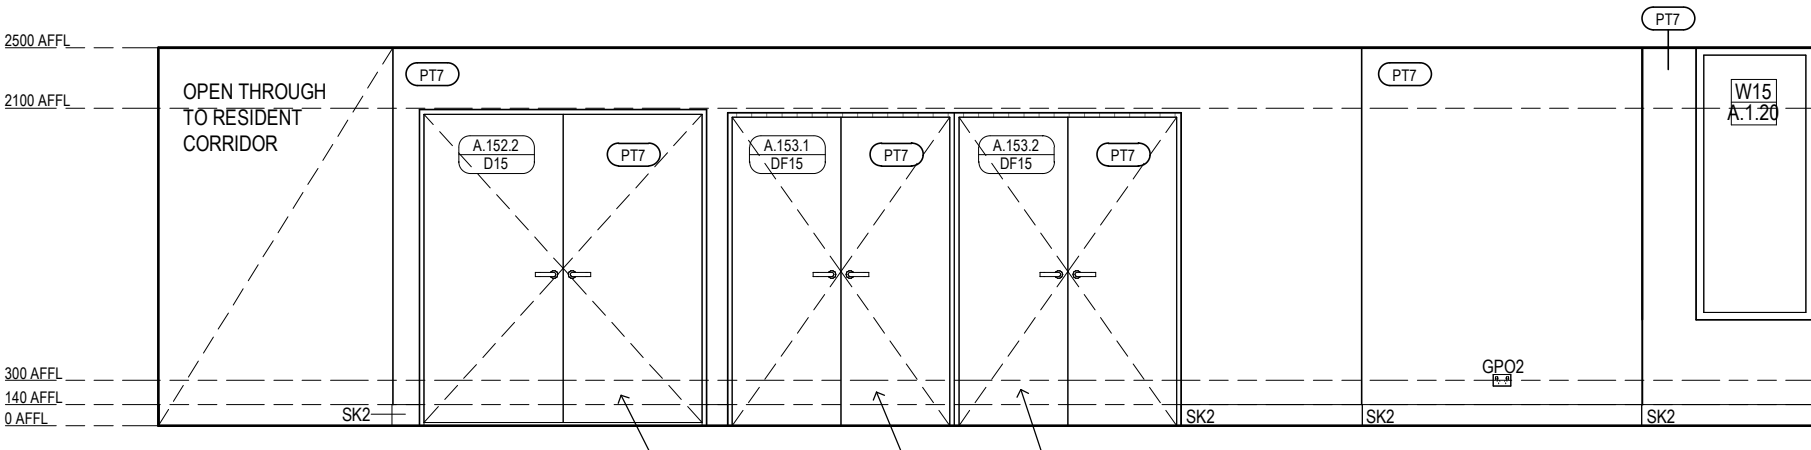


ILA L1 + L2 COMMUNAL SPACE
ELEVATION 1
Scale 1 : 50

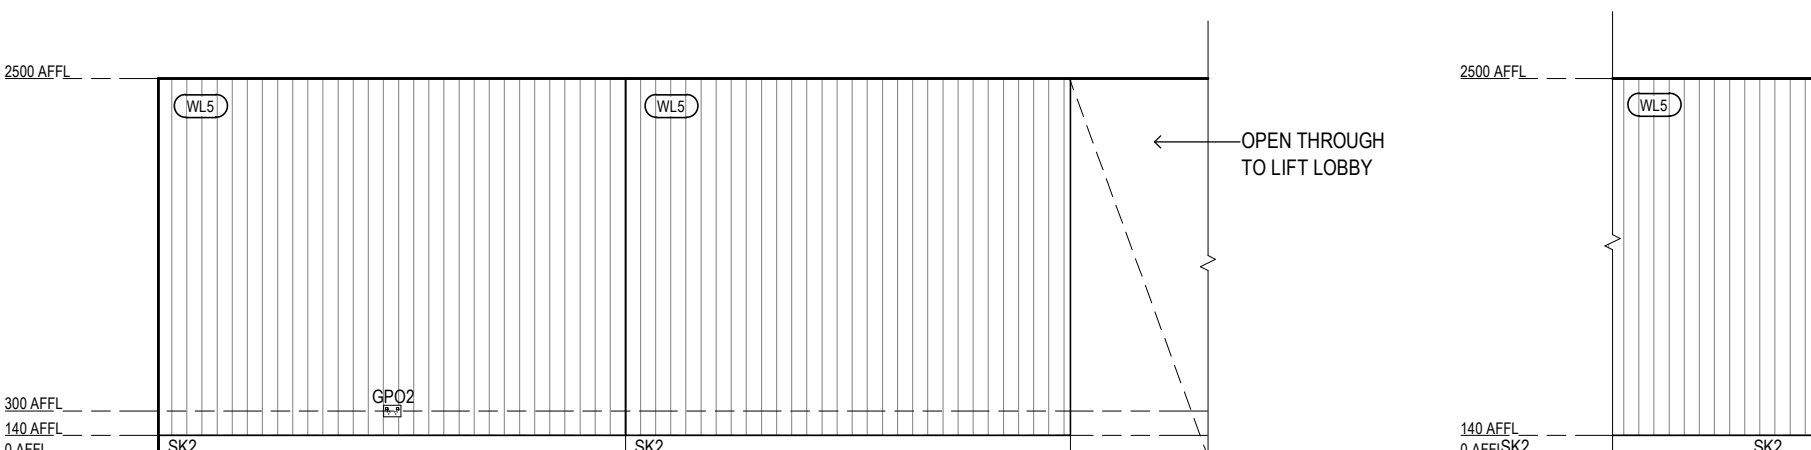


ILA L1 + L2 COMMUNAL SPACE
ELEVATION 3
Scale 1 : 50

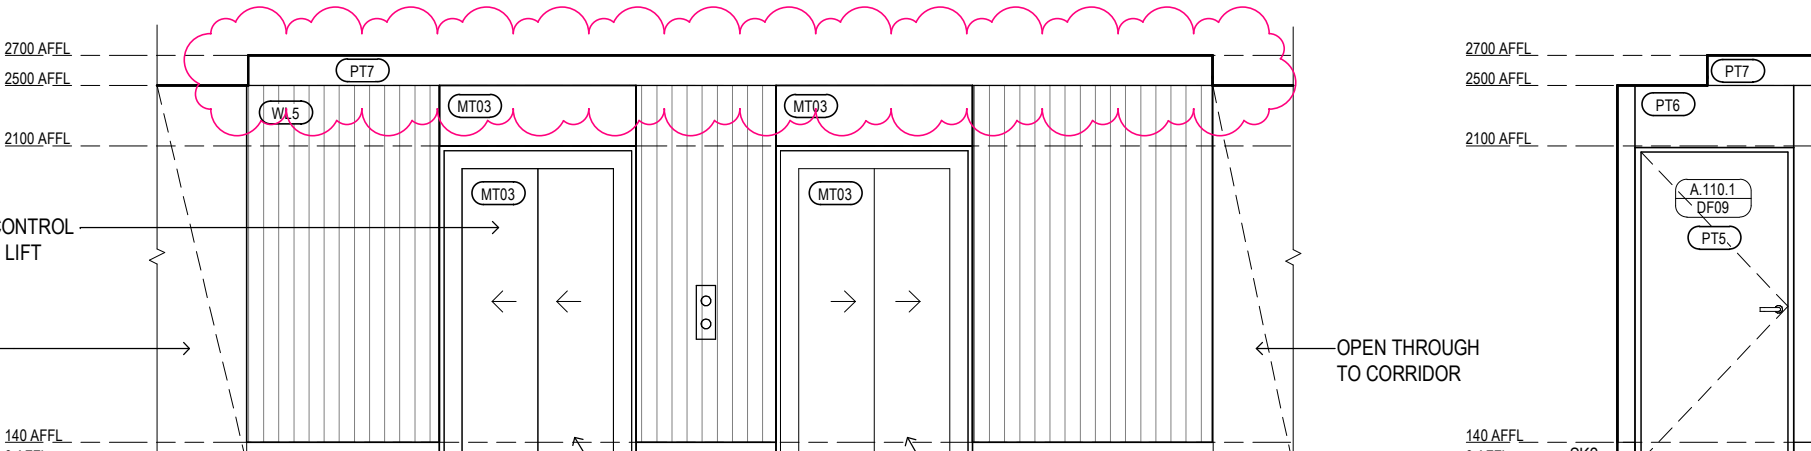


ILA L1 + L2 LIFT LOBBY
ELEVATION 1
Scale 1 : 50

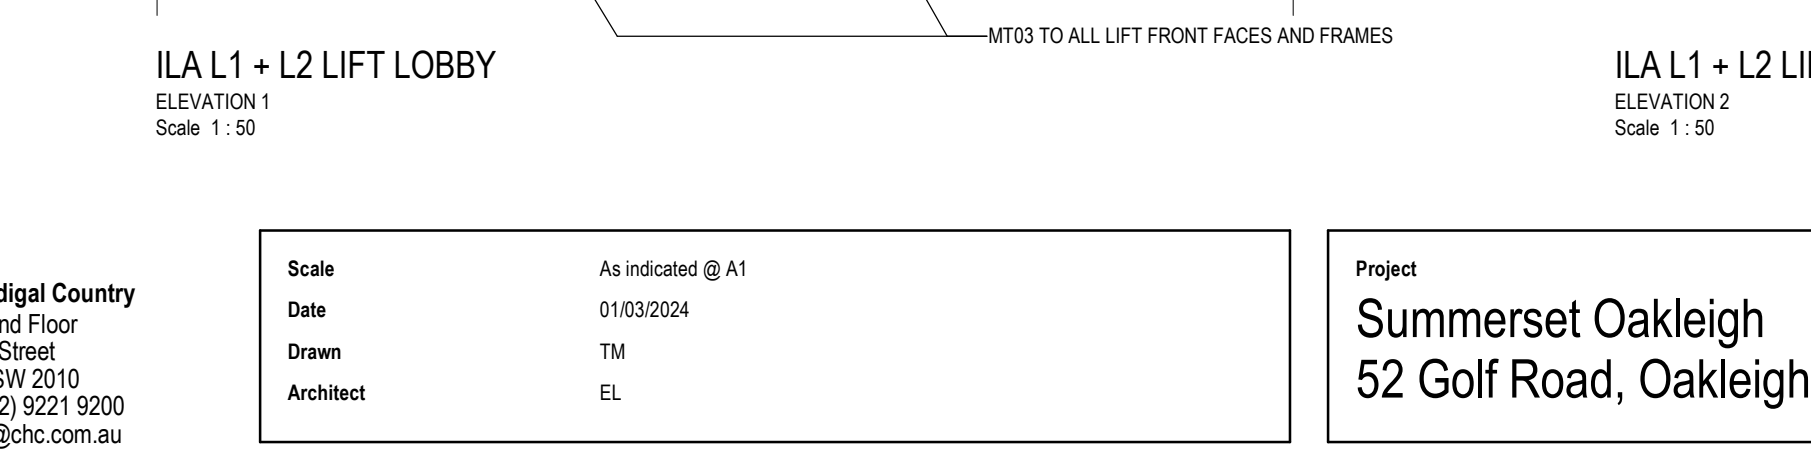


ILA L1 + L2 LIFT LOBBY
ELEVATION 2
Scale 1 : 50

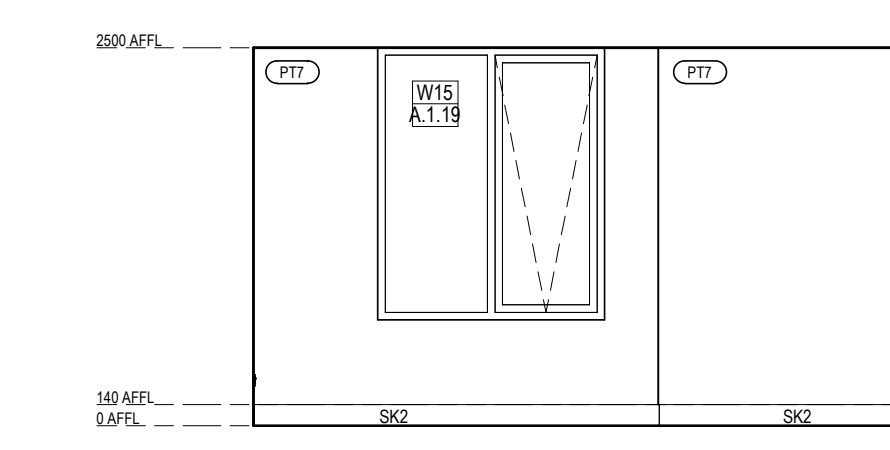

ILA L1 + L2 COMMUNAL SPACE
ELEVATION 2
Scale 1 : 50

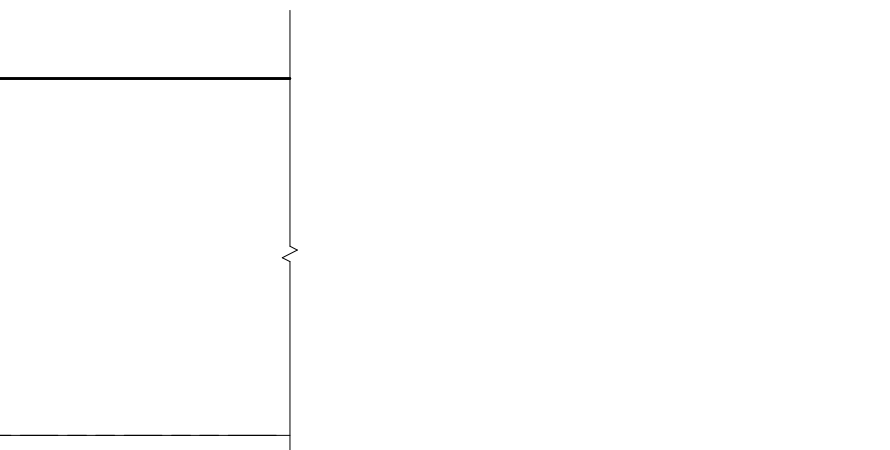

ILA L1 + L2 COMMUNAL SPACE
ELEVATION 4
Scale 1 : 50

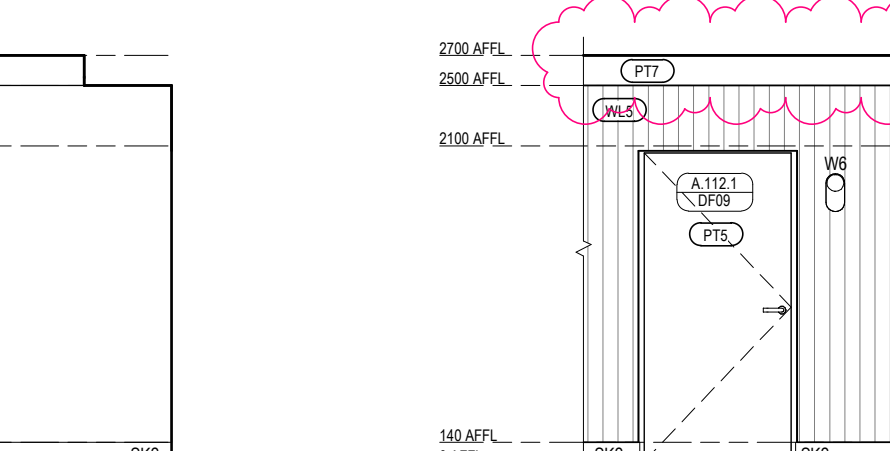

ILA L1 + L2 LIFT LOBBY
ELEVATION 3
Scale 1 : 50

Legend - Internal Elevations

DRAWINGS TO BE READ IN CONJUNCTION WITH ARCHITECTURAL SPECIFICATION & MATERIALS, PRODUCTS & FINISHES SCHEDULE.

PT# PAINT FINISH TO ALL WALLS WITHIN NEW & AFFECTED ROOMS/ AREAS UNLESS OTHERWISE SHOWN

- CSE CONCRETE SEALER
- DPR DOOR PROTECTION
- GD GRAPHIC FILM
- LM LAMINATE
- MI MIRROR
- PBD PINBOARD
- PT PAINT FINISH
- REN RENDER FINISH
- SB SPLASHBACK
- ST STONE
- WB WHITEBOARD
- WP WALL PROTECTION
- WT WALL TILE
- WV WALL VINYL

NOTES:
1. LAMINATE CARCASS FOR ALL VISIBLE OPEN SHELVING, UNLESS OTHERWISE NOTED
2. MELAMINE TO ALL INTERNAL CARCASS OF JOINERY, UNLESS OTHERWISE NOTED.

--- PROVIDE NOGGINGS FOR FUTURE USE

Legend - Floor Finishes

- C CARPET
- CO CONCRETE
- E EPOXY FINISH
- L LINOLEUM
- M MATTING
- FU PAVING UNIT - TBC WITH LANDSCAPE
- R RUBBER FLOORING
- T TILING
- TF TIMBER FLOORING
- V VINYL
- LVT LUXURY VINYL TILE PLANK

--- PROTECTION RAILS OR CRASH RAILS - REFER TO MATERIAL SCHEDULE FOR DETAILS

--- WL1- REFER TO MATERIAL SCHEDULE FOR DETAILS

--- WL2- REFER TO MATERIAL SCHEDULE FOR DETAILS

NOTE:
FALLS TO ALL FLOOR WASTES IN ACCORDANCE WITH AS 3740.

Keystone Legend

- 3MLB MAIL BOX
- FE-JC FIRE EXTINGUISHER IN JOINERY CUPBOARD
- GPO2 POWER OUTLET - DOUBLE
- SK2 SKIRTING - TYPE 2
- W6 WALL LIGHT - TYPE 6

FOR CONSTRUCTION

Revision/Issue	Date
P1 Linkway Comments/Preliminary Issue	2025.09.04
P2 Tender Pack Issue	2025.09.05
P3 ISSUE FOR CONTRACT	2025.10.10
C1 ISSUE FOR CONSTRUCTION - INTERIORS	2026.04.13

Clarke
Hopkins
Clarke

ClarkeHopkinsClarke
Melbourne | Wurundjeri
L3, Melbourne Connect
700 Swanston Street
Carlton VIC 3063
Telephone (03) 9419 4340
Email studio@chc.com.au
www.chc.com.au

Sydney | Gadigal Country
Suite 3, Ground Floor
91 Campbell Street
Surry Hills NSW 2010
Telephone (02) 9221 9200
Email studio@chc.com.au
www.chc.com.au

Scale	As indicated @ A1
Date	01/03/2024
Drawn	TM
Architect	EL

Project
Summerset Oakleigh
52 Golf Road, Oakleigh South, VIC

Drawing
Internal Elevations - Lobby and Communal
Space - Sheet 1

Drawing No.
230185/A2831
C1