



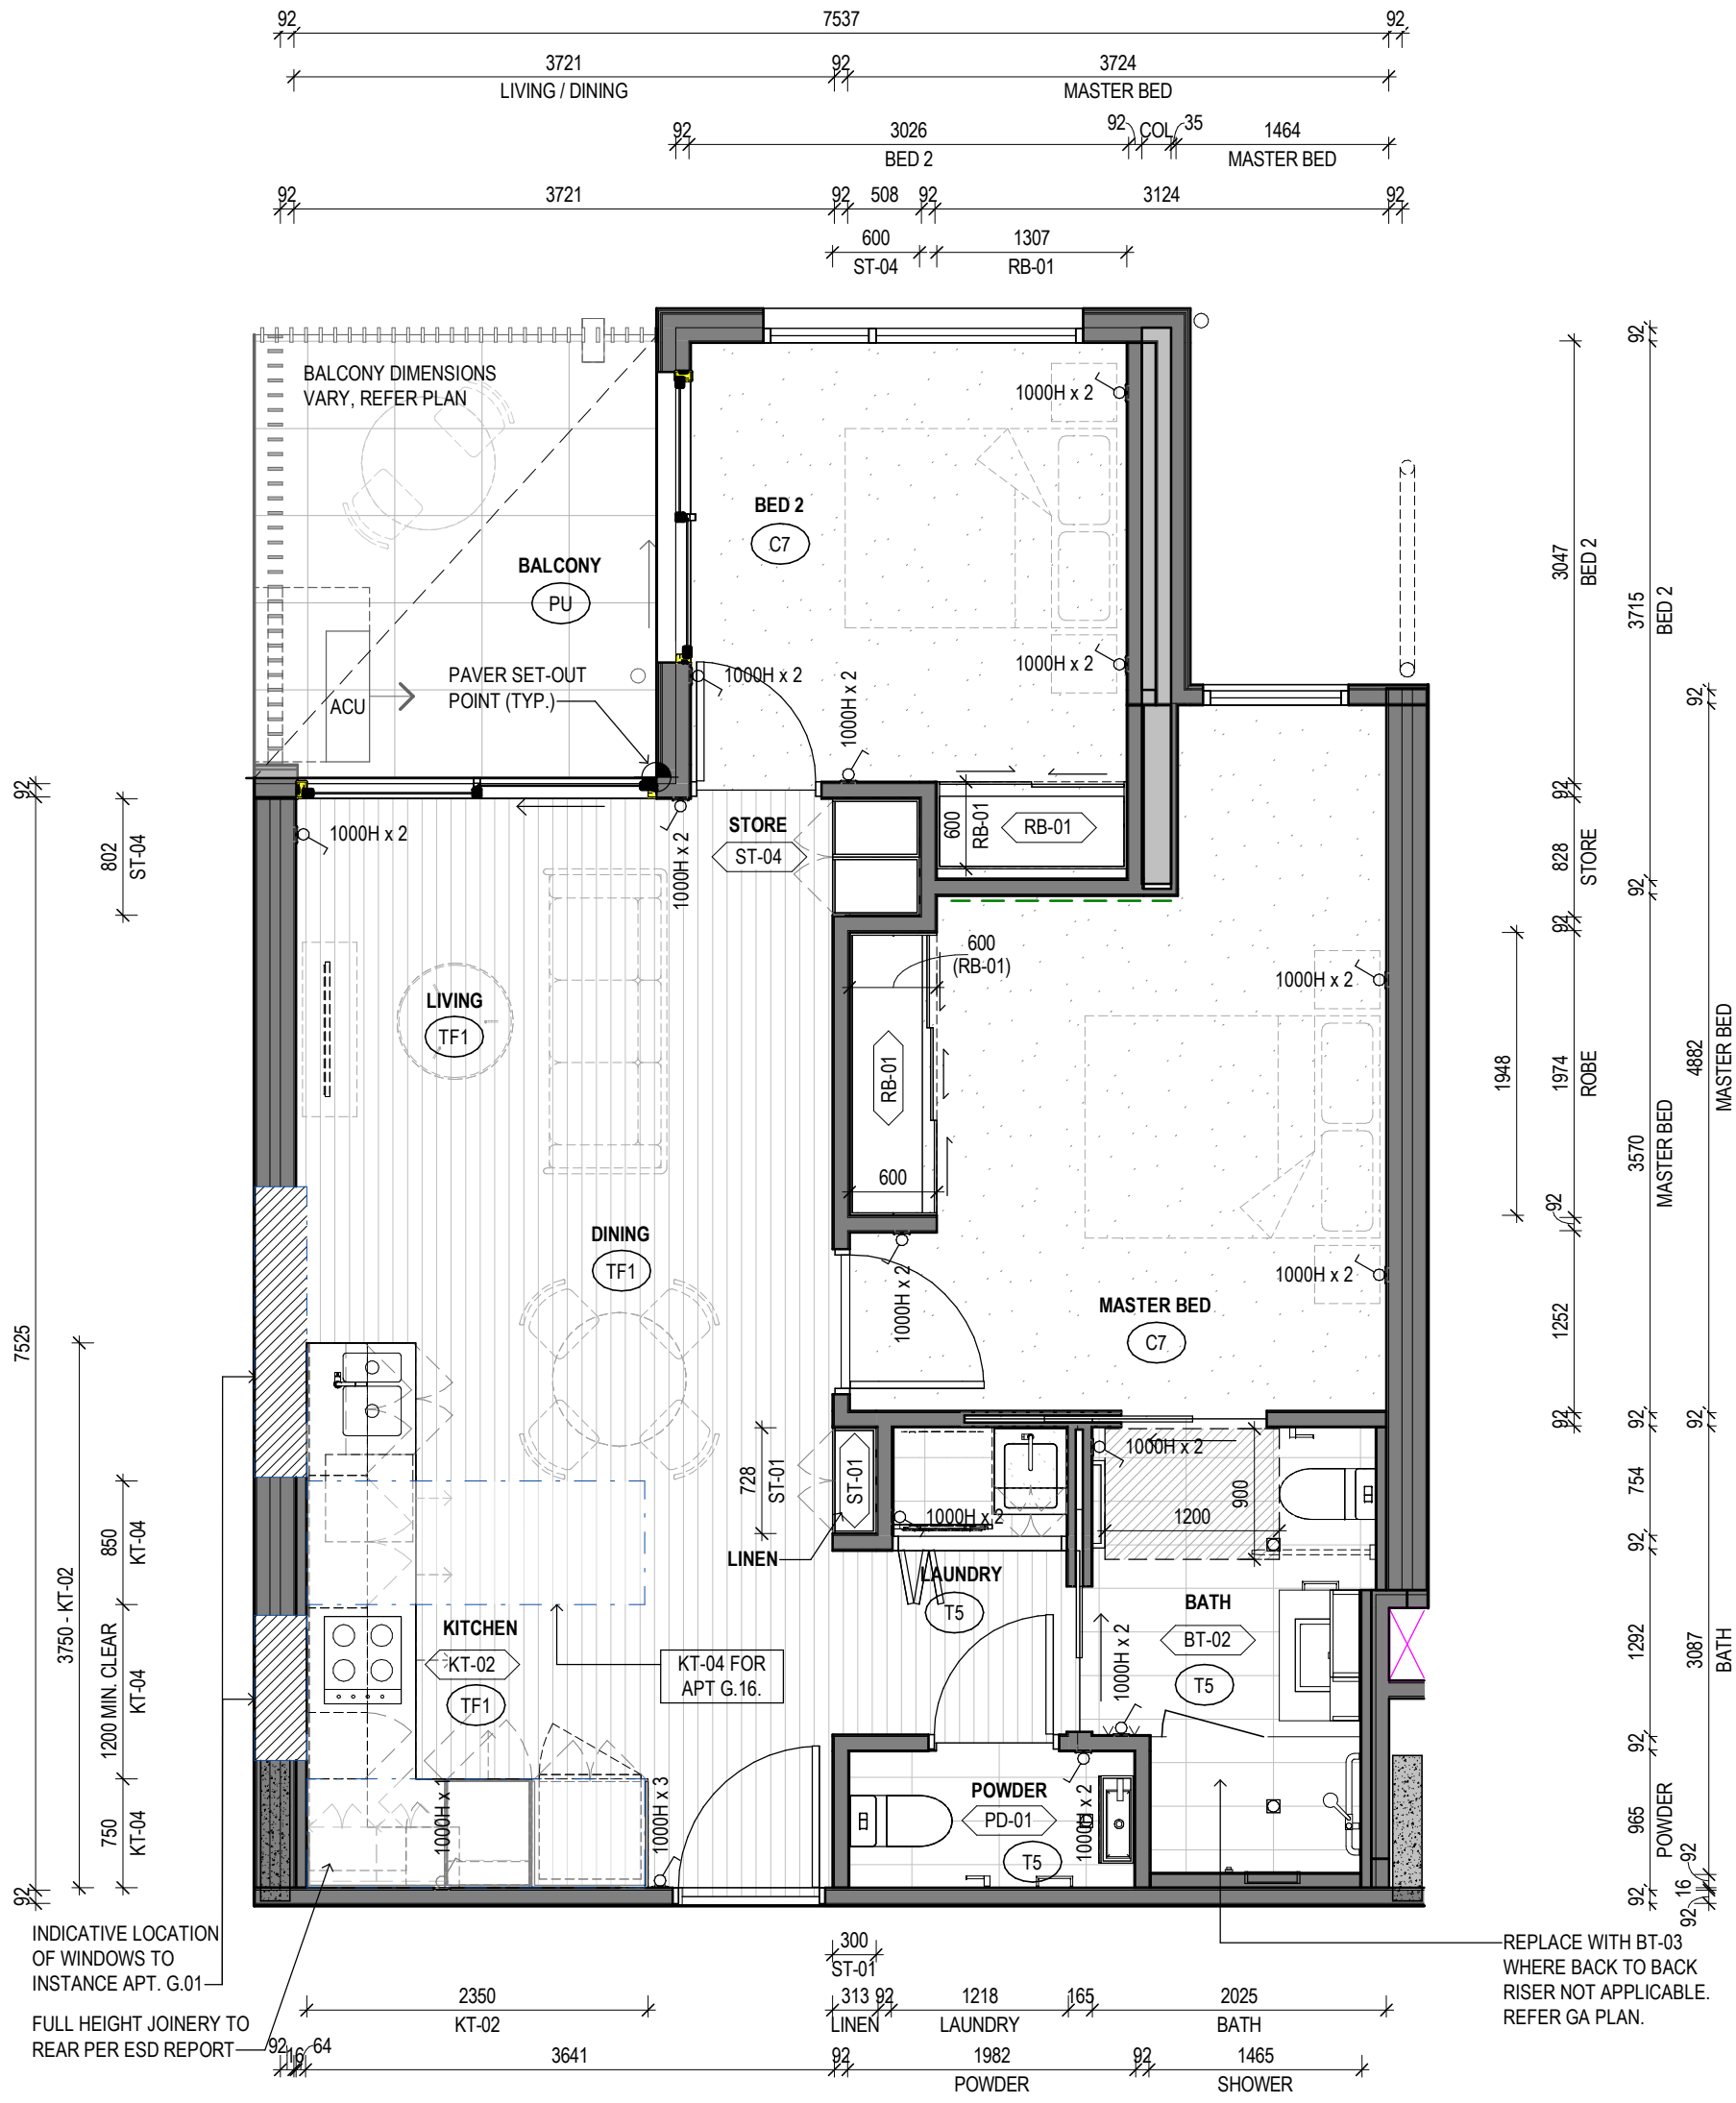


1 ILA Type 2
Scale 1: 50

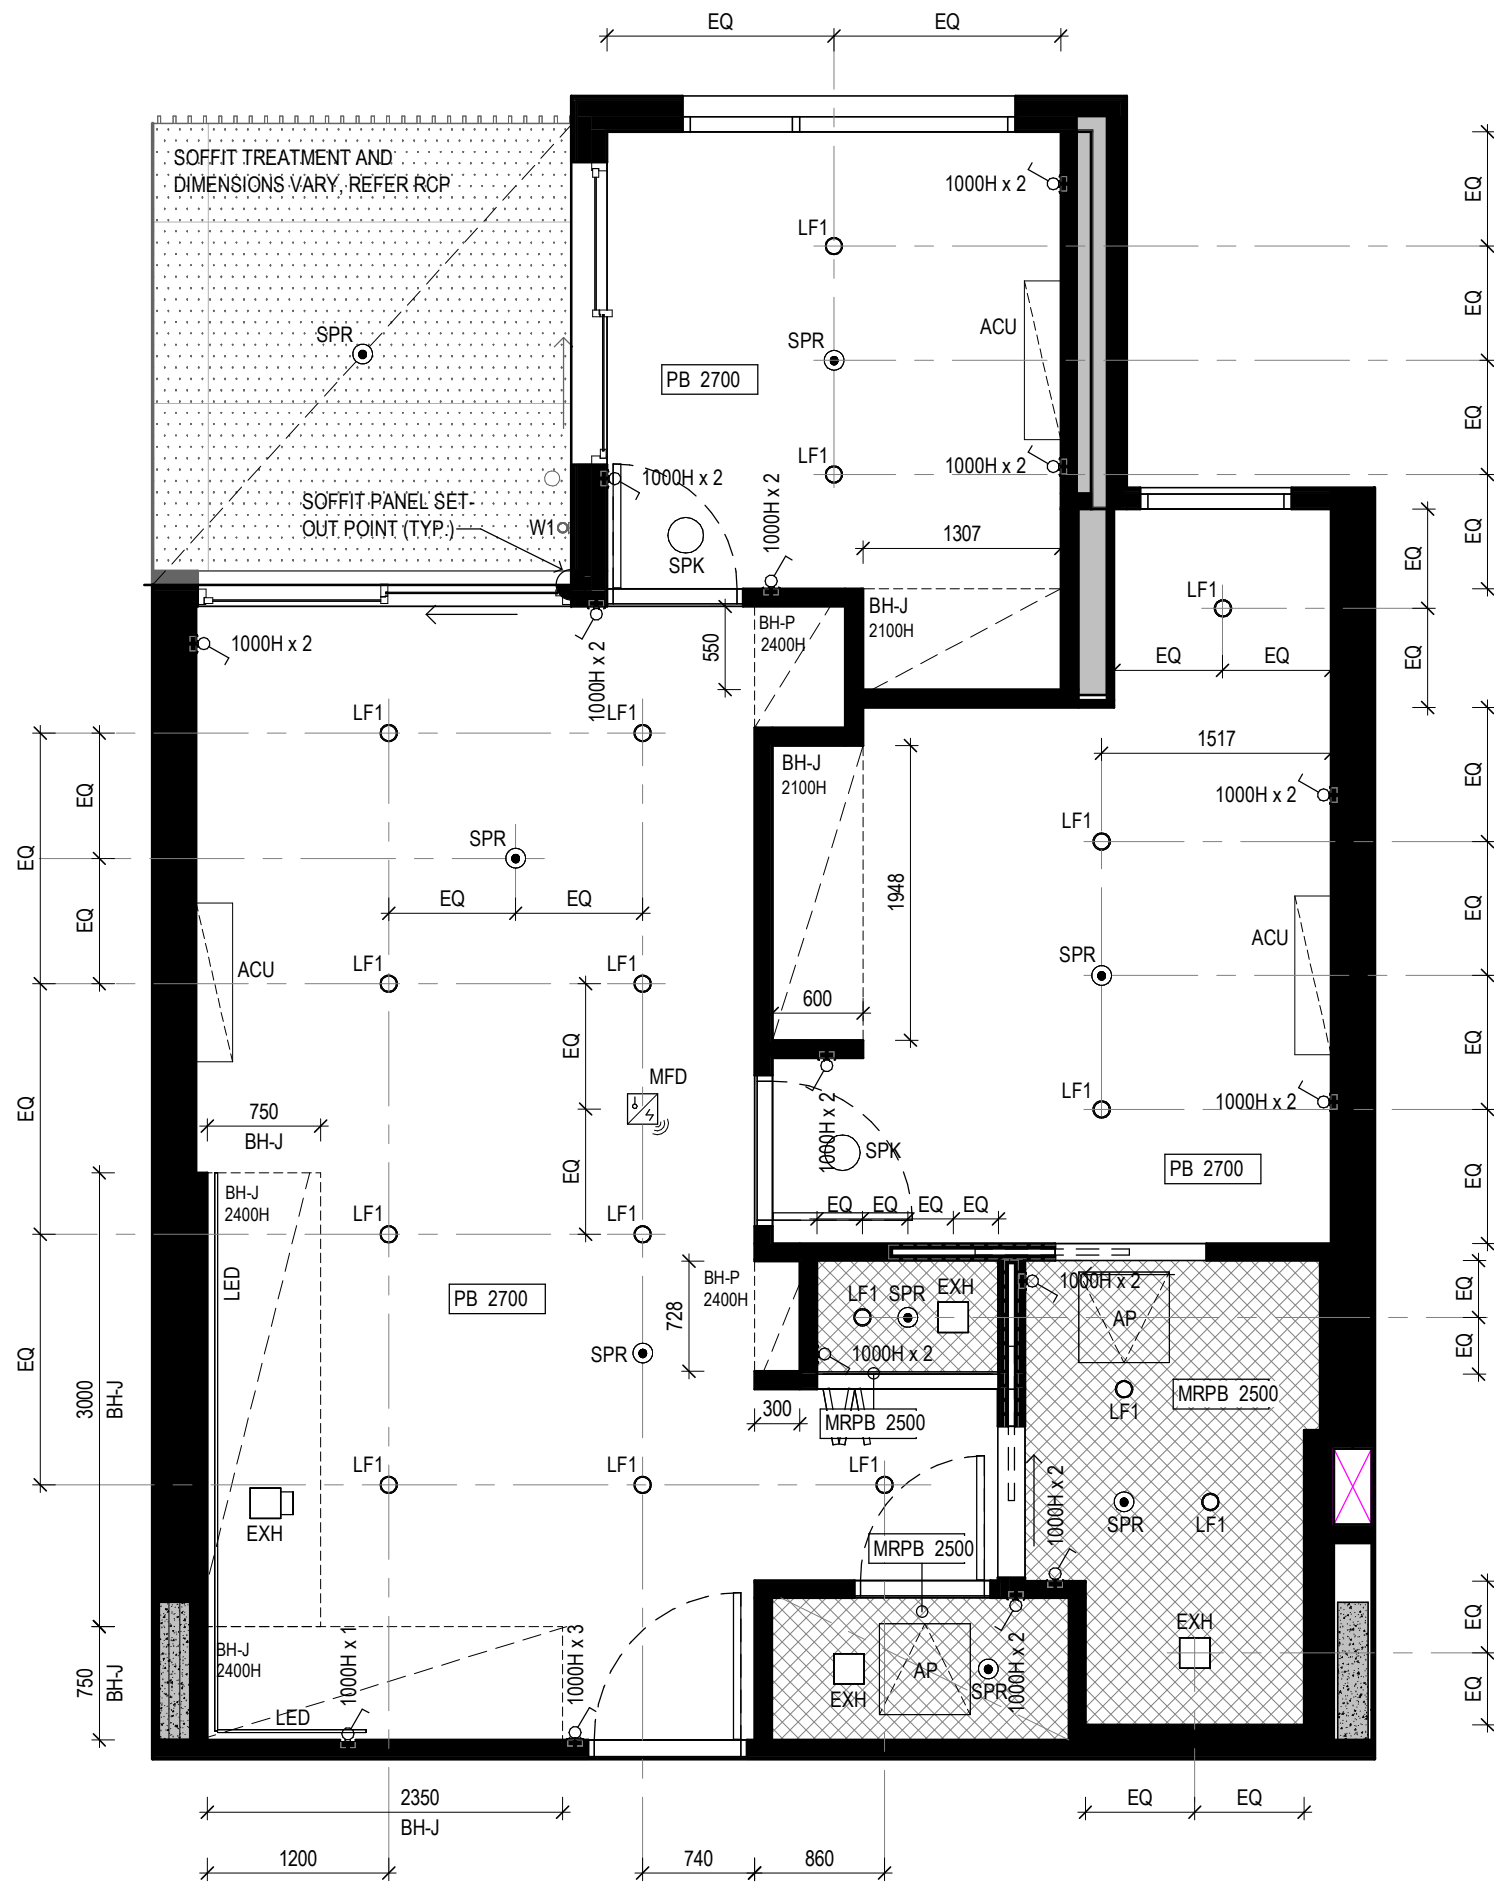


2 ILA Type 2 RCP
Scale 1: 50

NOTE: REFER TO ELECTRICAL ENGINEER DRAWINGS FOR TYPICAL LIGHTING/CEILING SERVICES LOCATIONS & SPECIFICATION.


Key Plan - ILA Ground Floor

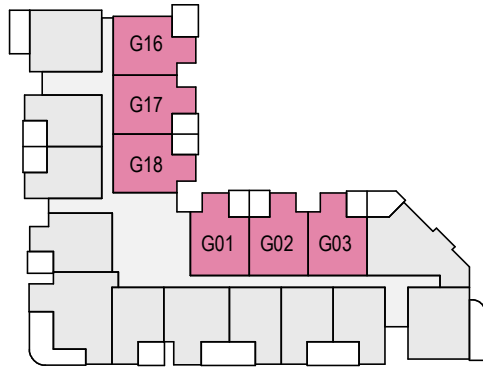

Key Plan - ILA Level 1

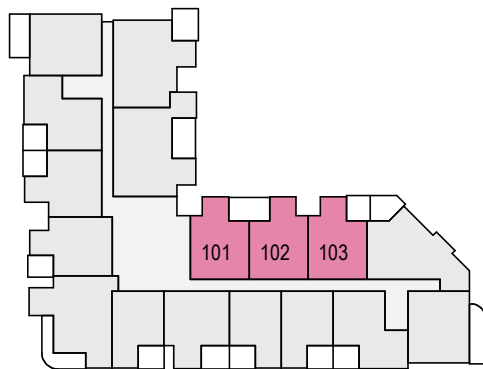

Key Plan - ILA Level 2

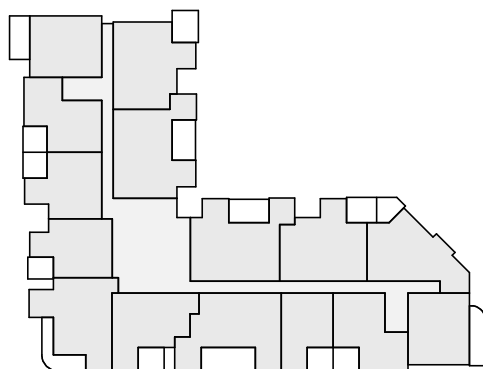

ALLOW FOR MIRRORED CONFIGURATIONS IN ILA LAYOUTS

--- PROVIDE NOGGINGS FOR FUTURE SUPPORT

ILA Finish Types - Type 2				
Level	Apt Number	No. of Bed	Finish Type	Mirrored
ILA_Ground	APT-G01	2 BED	STANDARD	Yes
ILA_Ground	APT-G02	2 BED	STANDARD	No
ILA_Ground	APT-G03	2 BED	STANDARD	Yes
ILA_Ground	APT-G16	2 BED	STANDARD	No
ILA_Ground	APT-G17	2 BED	STANDARD	Yes
ILA_Ground	APT-G18	2 BED	STANDARD	No
ILA_Level 1	APT-101	2 BED	STANDARD	Yes
ILA_Level 1	APT-102	2 BED	STANDARD	No
ILA_Level 1	APT-103	2 BED	STANDARD	Yes

Keynote Legend

ACU	AIR CONDITIONING UNIT
AP	ACCESS PANEL
BH-J	BULKHEAD - JOINERY TYPE
BH-P	BULKHEAD - PLASTERBOARD TYPE
EXH	EXHAUST
LED	LED STRIP LIGHT - RECESSED
LF1	LIGHT FITTING - REFER TO ELECTRICAL ENGINEER SPECIFICATION
MFD	MULTI-FUNCTION DEVICE (THERMAL, SMOKE, WIFI)
SPK	ANNUNCIATOR SPEAKER
SPR	SPRINKLER
W1	WALL LIGHT - TYPE 1

FOR CONSTRUCTION

Revision/Issue	Date
b Issued for Coordination - 100% DD	2024.04.12
P1 Preliminary ILA Apartment Types & Joineries	2025.08.25
P2 Tender Pack Issue	2025.09.05
P3 ISSUE FOR CONTRACT	2025.10.10
G1 ISSUE FOR CONSTRUCTION - INTERIORS	2026.04.13

Clarke
Hopkins
Clarke

ClarkeHopkinsClarke
Melbourne | Wurundjeri
L3, Melbourne Connect
700 Swanston Street
Carlton VIC 3063
Telephone (03) 9419 4340
Email studio@chc.com.au
www.chc.com.au

Sydney | Gadigal Country
Suite 3, Ground Floor
91 Campbell Street
Surry Hills NSW 2010
Telephone (02) 9221 9200
Email studio@chc.com.au
www.chc.com.au

Scale	As indicated @ A1
Date	01/03/2024
Drawn	TM
Architect	EL

Project
Summerset Oakleigh
52 Golf Road, Oakleigh South, VIC

Drawing
ILA - Apartment Type 2 Plan & RCP

Drawing No.
230185/A2801
C1