



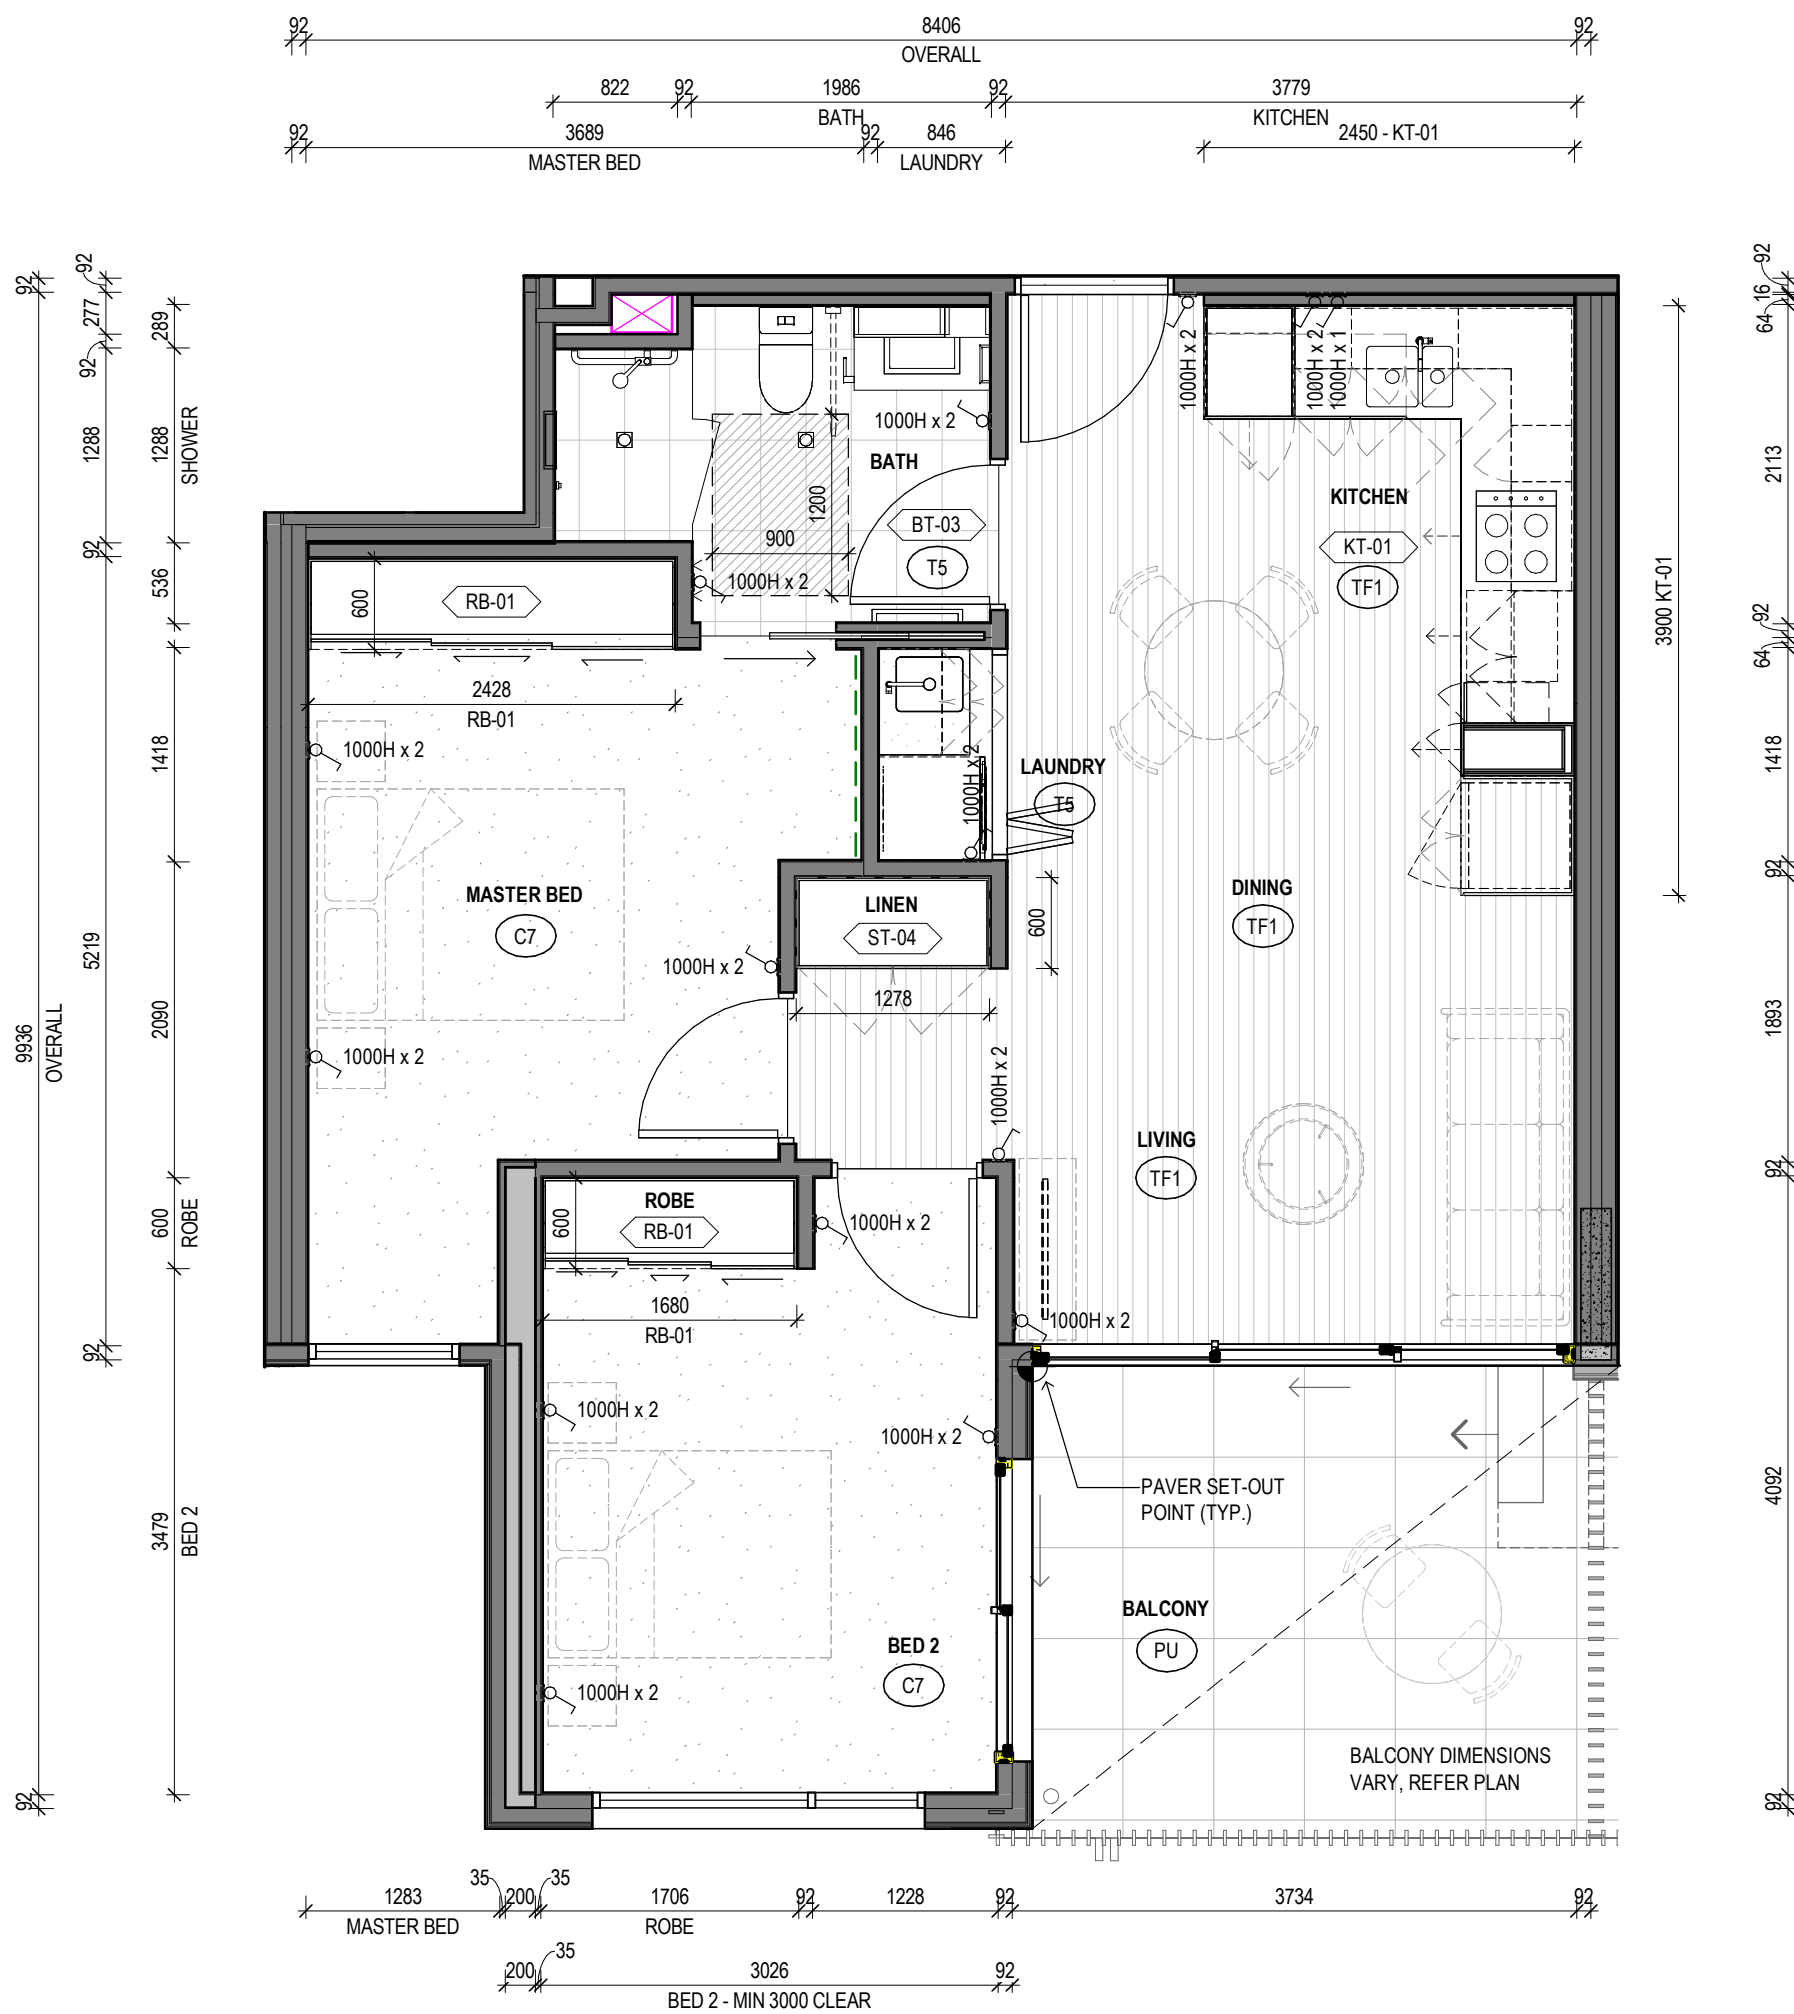

1 ILA Type 3
Scale 1: 50

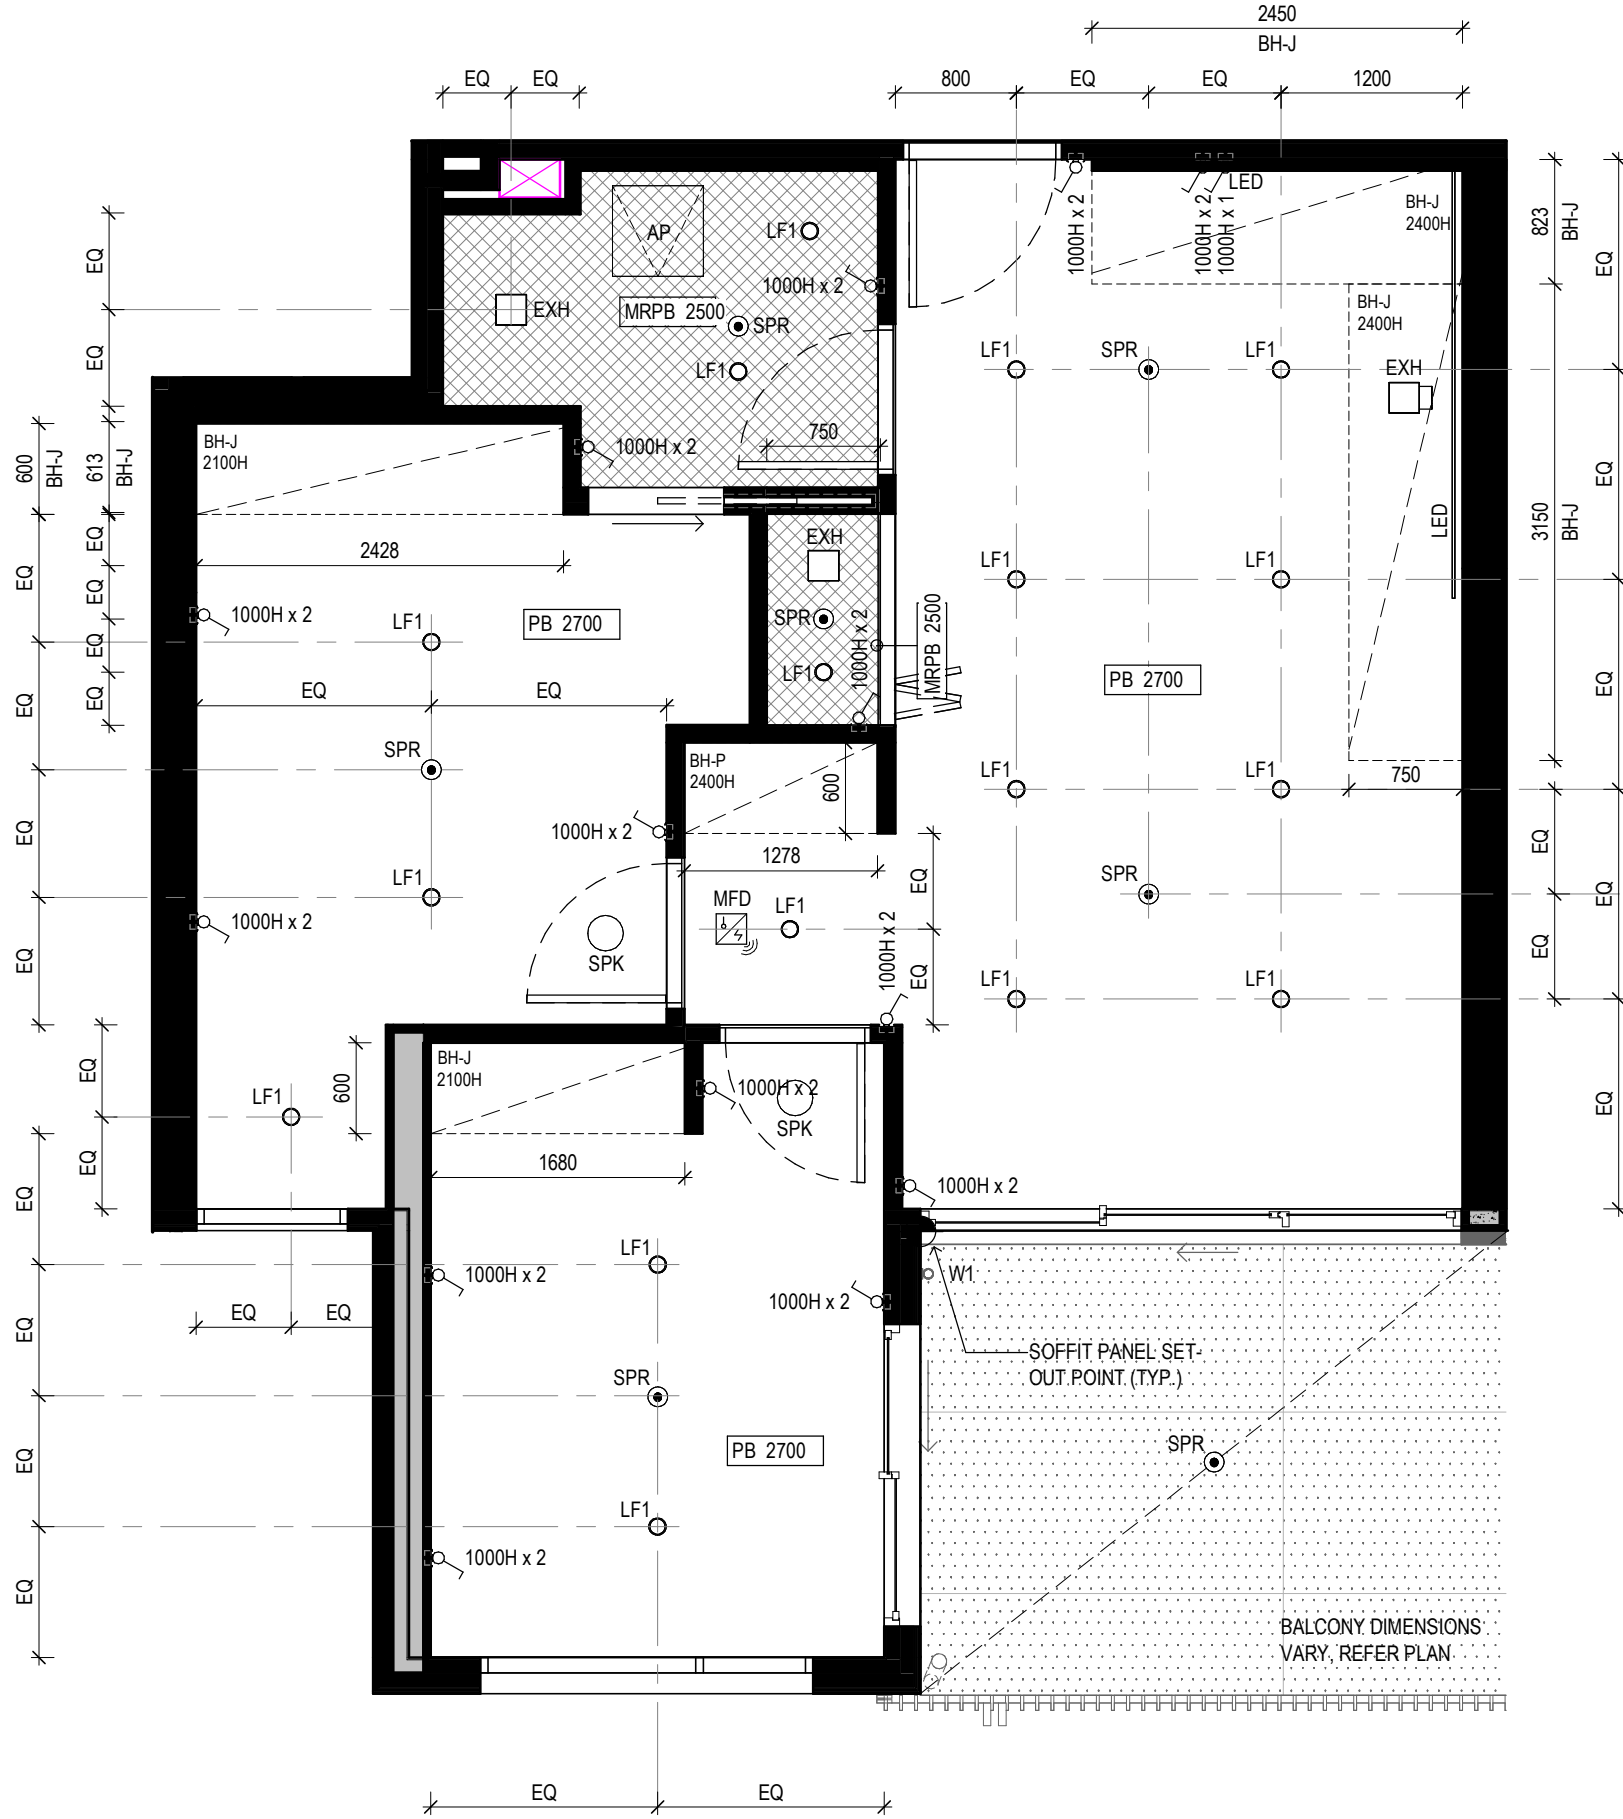


2 ILA Type 3 RCP
Scale 1: 50
NOTE: REFER TO ELECTRICAL ENGINEER DRAWINGS FOR TYPICAL LIGHTING/CEILING SERVICES LOCATIONS & SPECIFICATION.


Key Plan - ILA Ground Floor



Key Plan - ILA Level 1

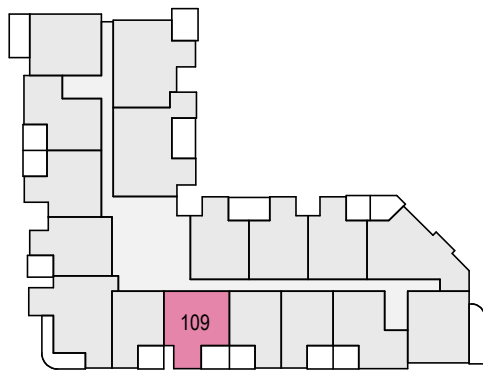

Key Plan - ILA Level 2

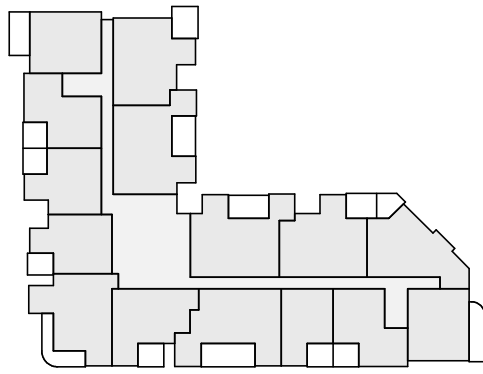

ALLOW FOR MIRRORED CONFIGURATIONS IN ILA LAYOUTS

--- PROVIDE NOGGINGS FOR FUTURE SUPPORT

ILA Finish Types - Type 3				
Level	Apt Number	No. of Bed	Finish Type	Mirrored
ILA_Ground	APT-G09	2 BED	STANDARD	Yes
ILA_Level 1	APT-109	2 BED	STANDARD	Yes

Keynote Legend

AP	ACCESS PANEL
BH-J	BULKHEAD - JOINERY TYPE
BH-P	BULKHEAD - PLASTERBOARD TYPE
EXH	EXHAUST
LED	LED STRIP LIGHT - RECESSED
LF1	LIGHT FITTING - REFER TO ELECTRICAL ENGINEER SPECIFICATION
MFD	MULTI-FUNCTION DEVICE (THERMAL, SMOKE, WIFI)
SPK	ANNUNCIATOR SPEAKER
SPR	SPRINKLER
W1	WALL LIGHT - TYPE 1