



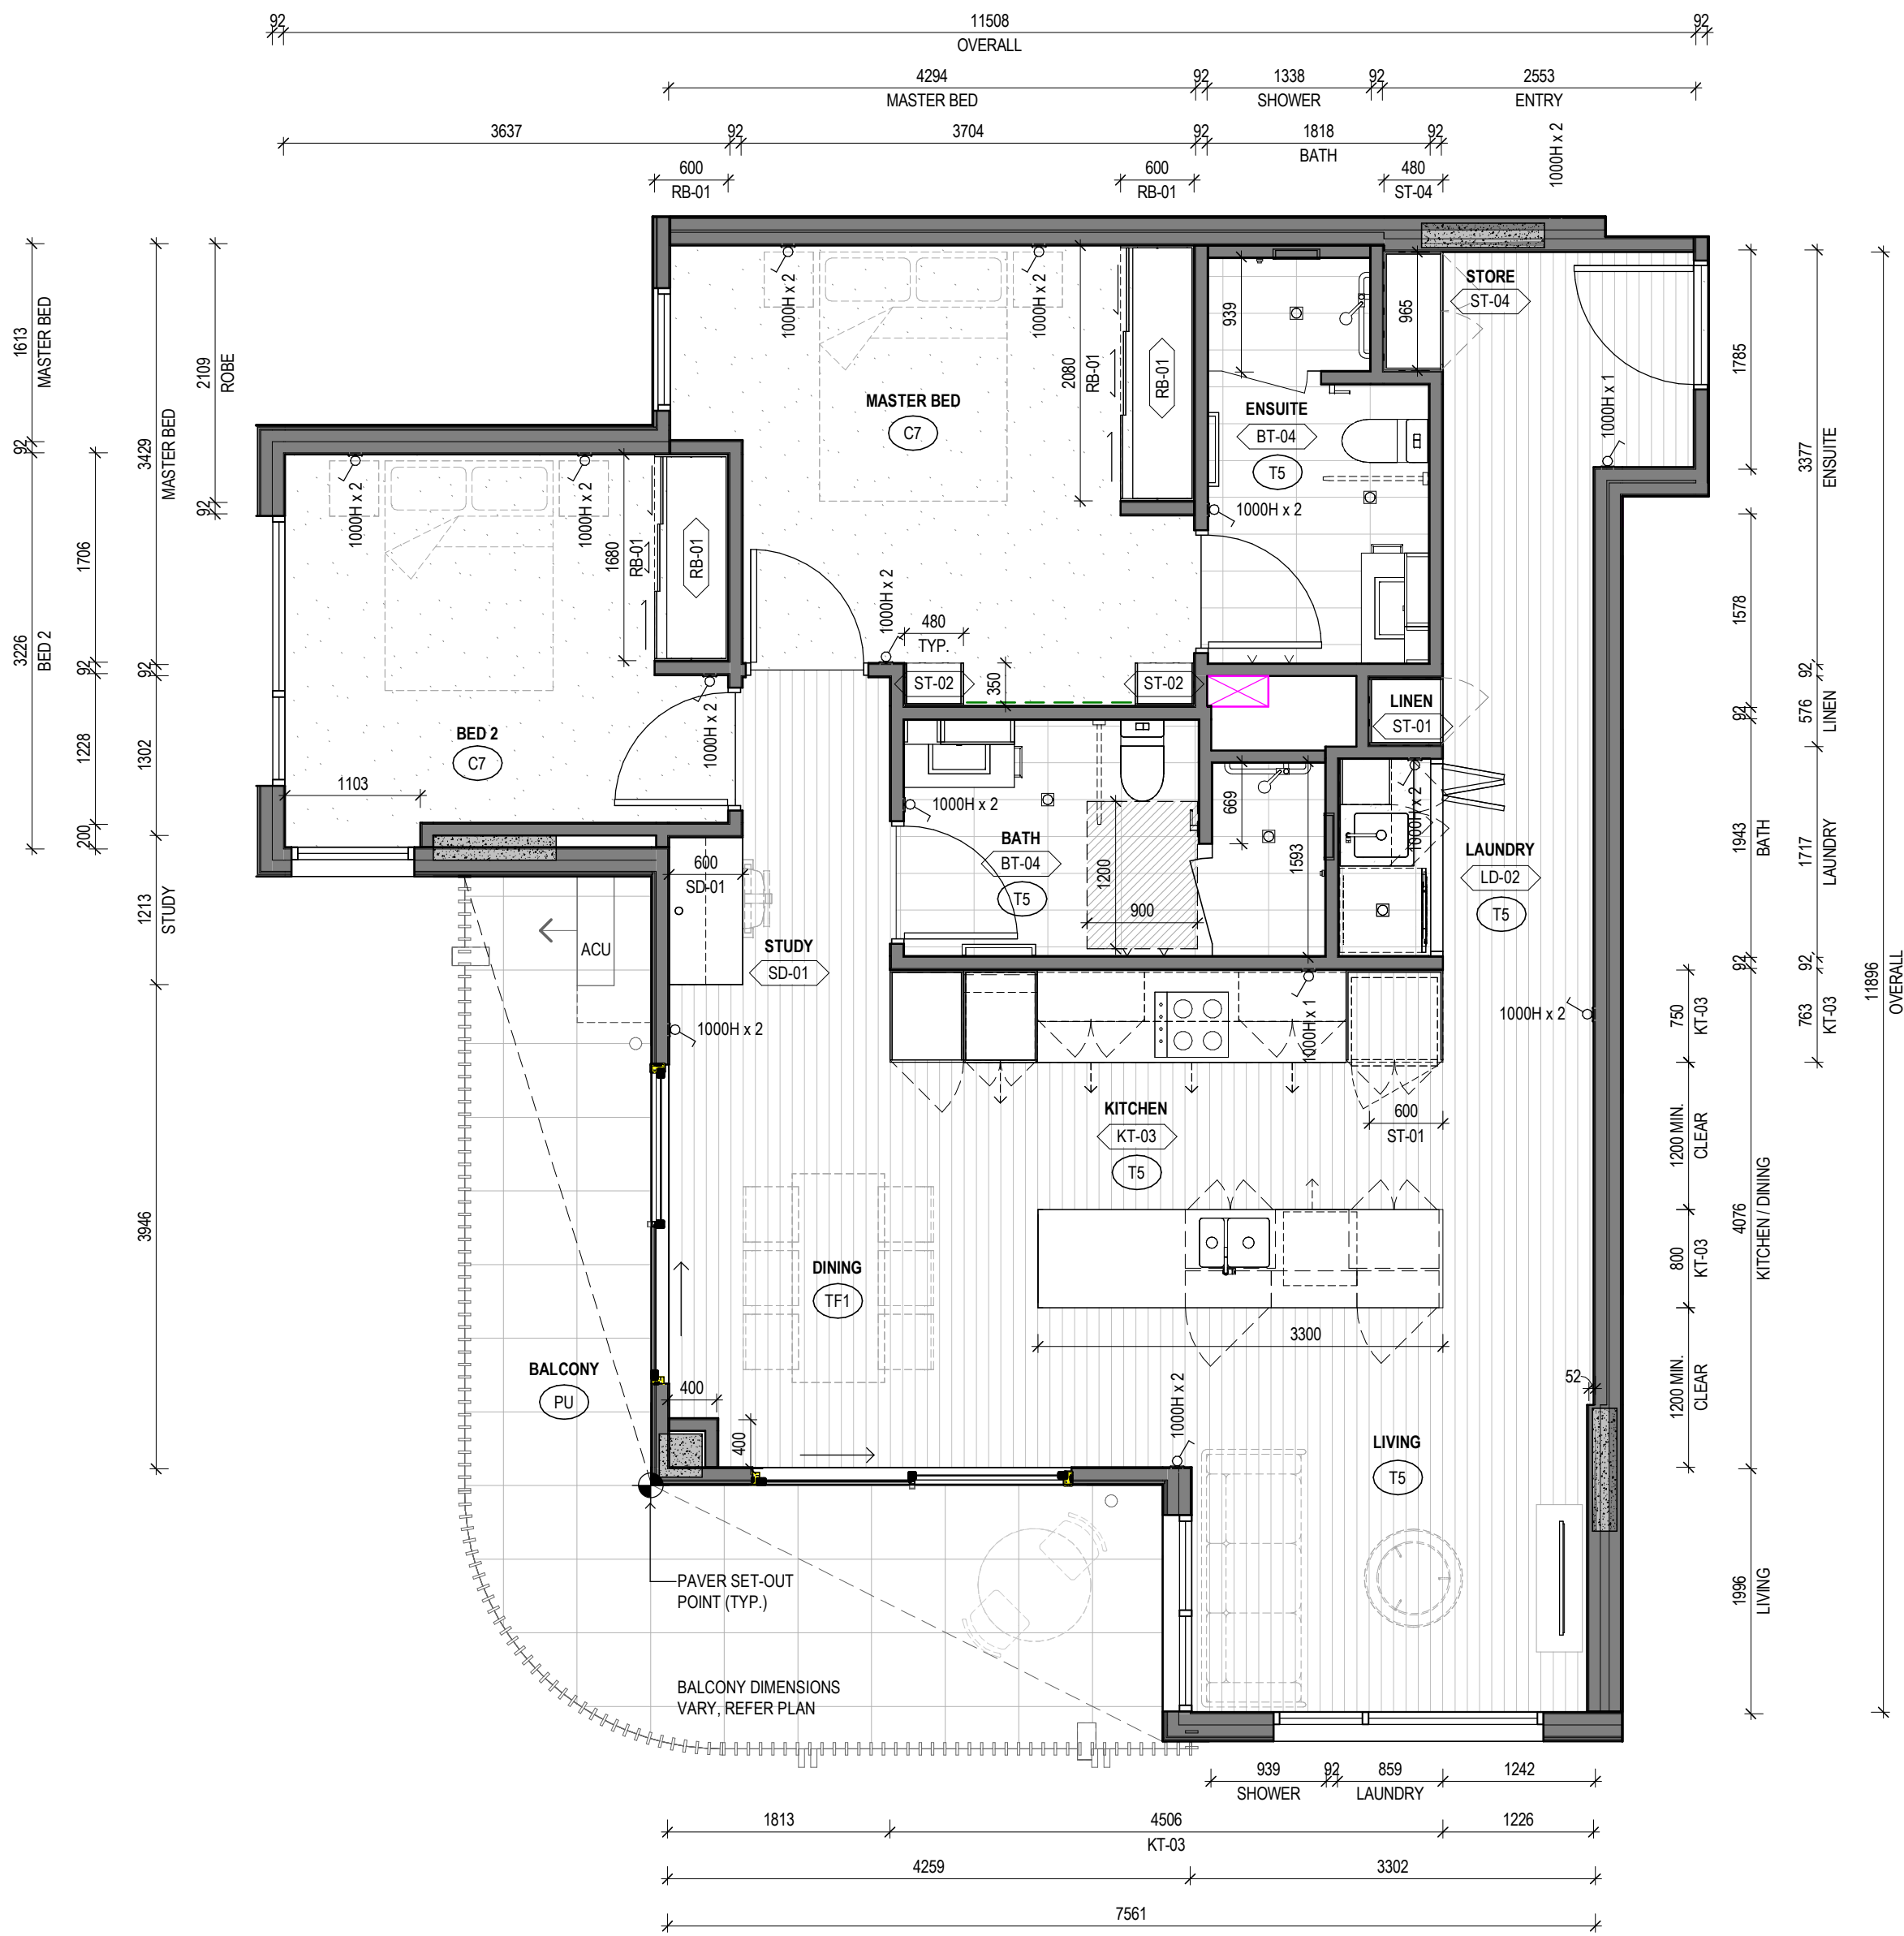


1 ILA Type 4
Scale 1 : 50

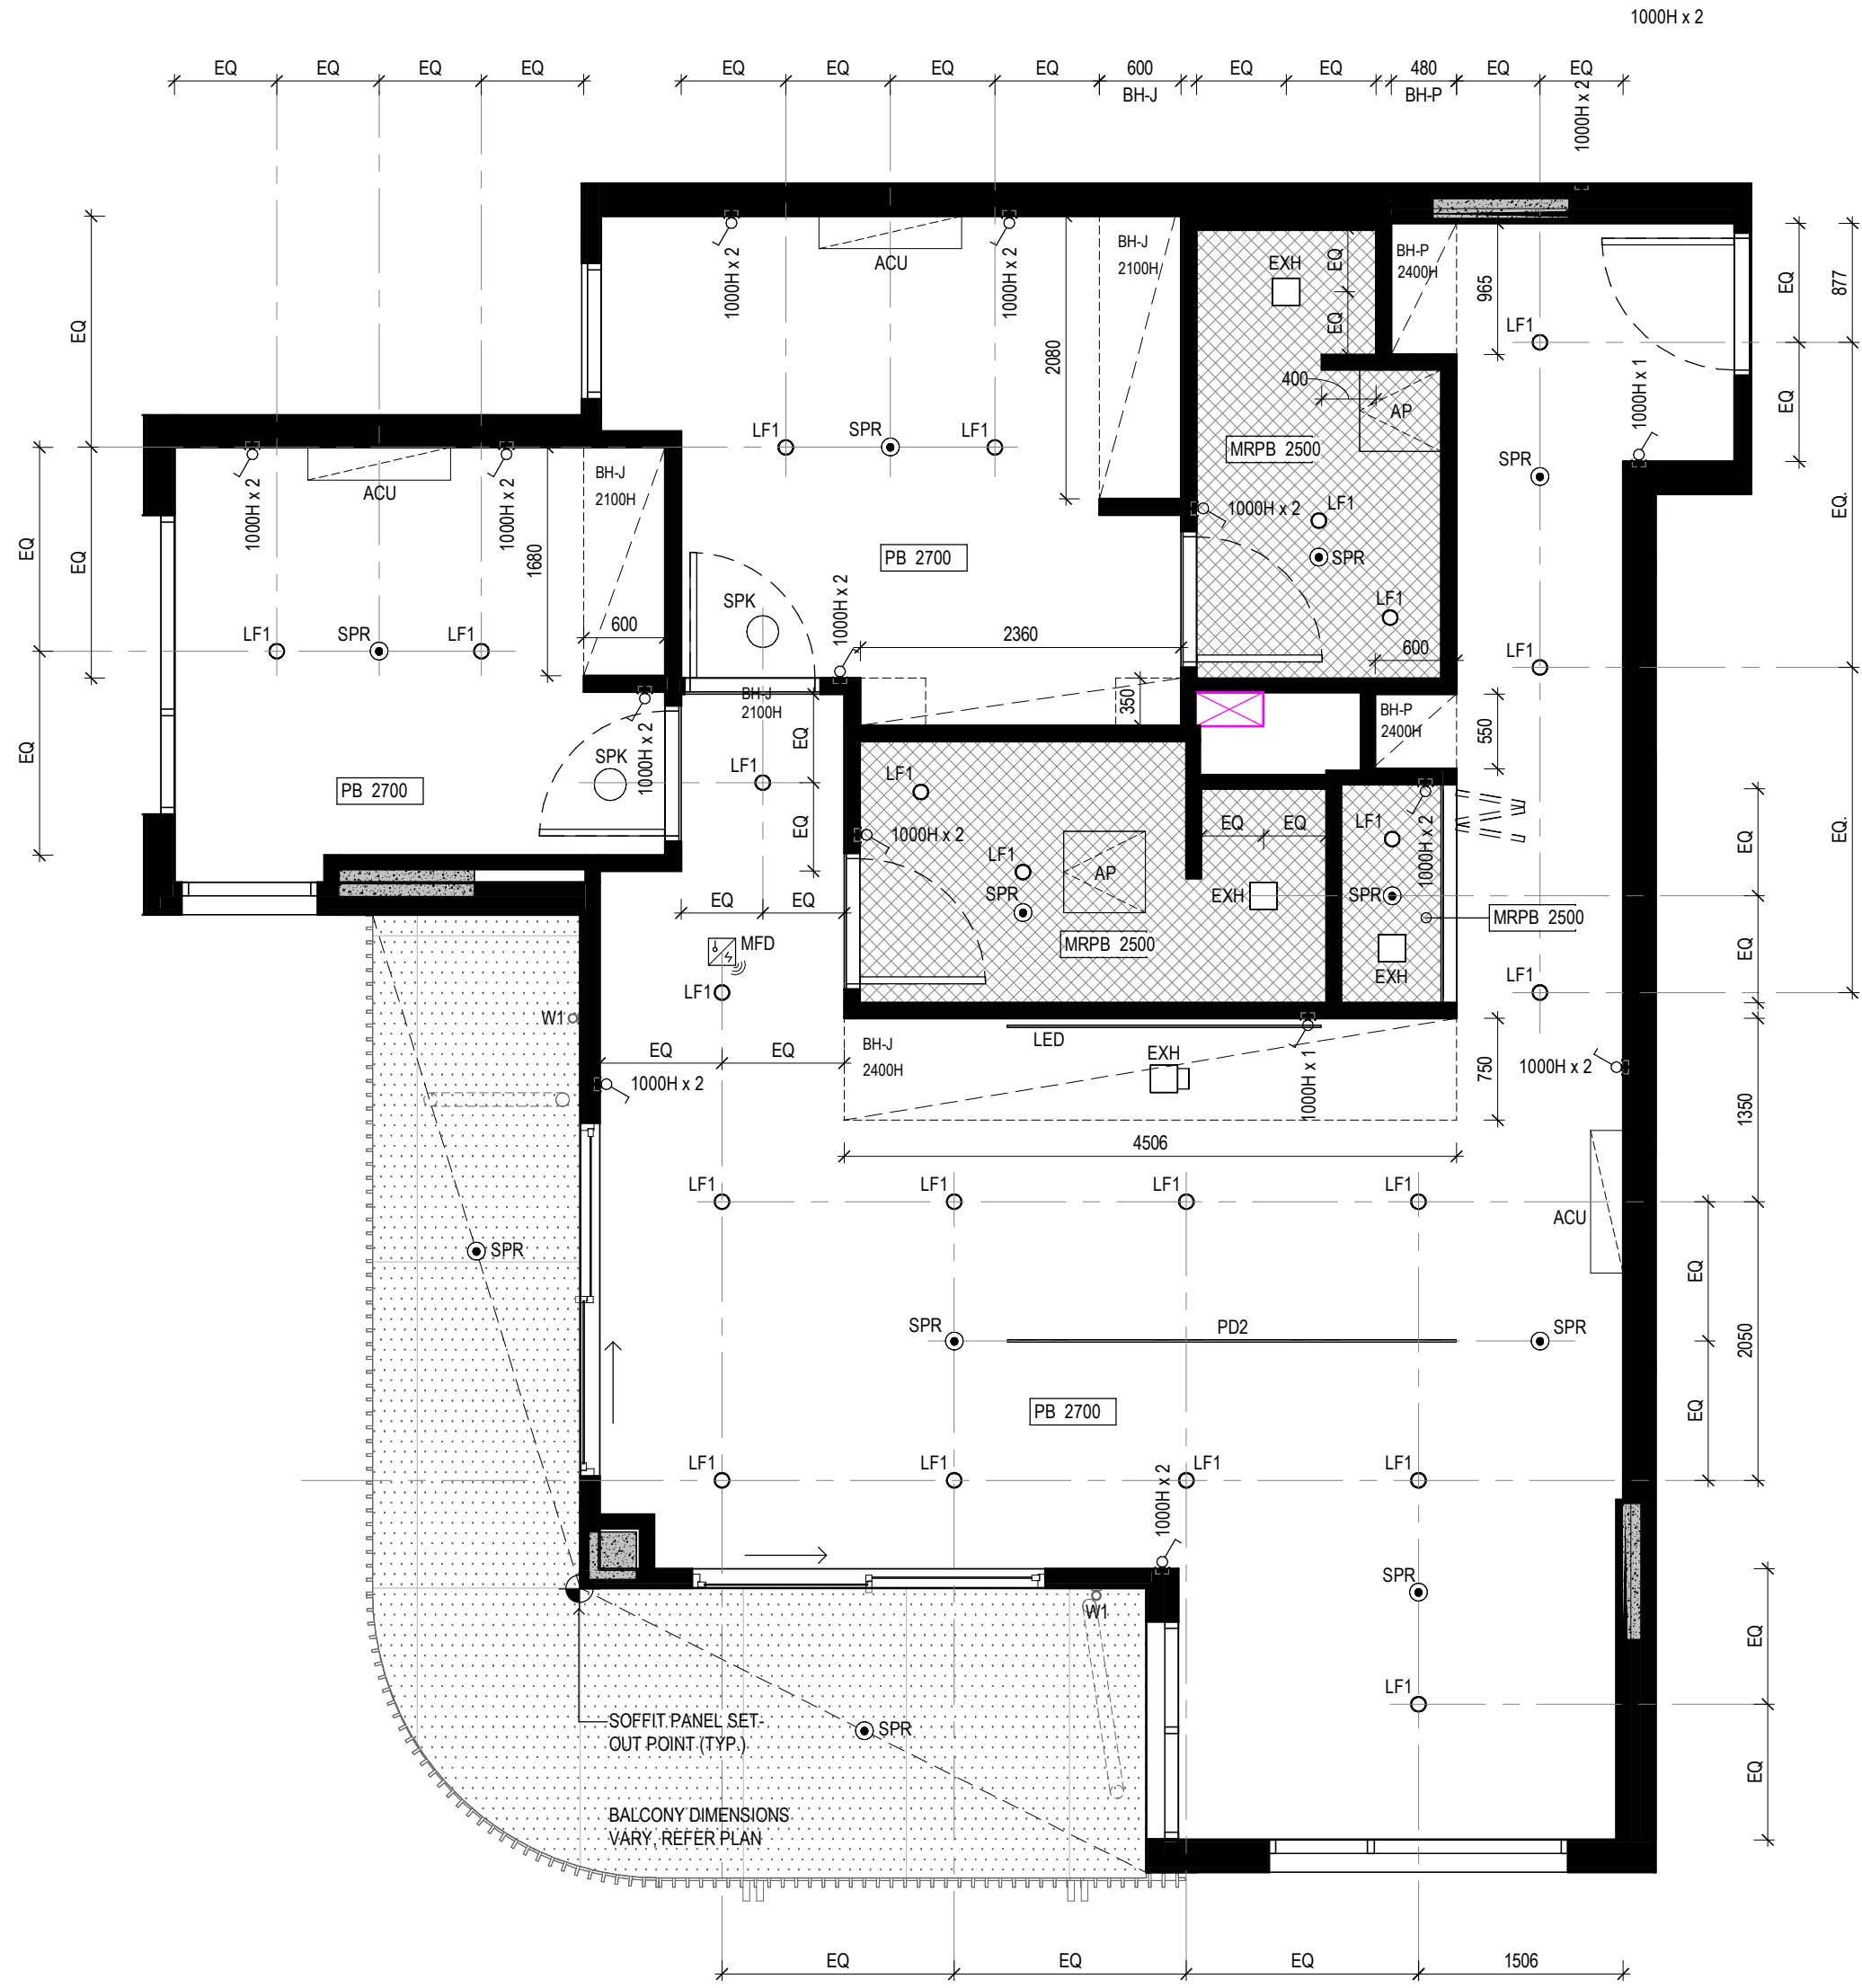


2 ILA Type 4 RCP
Scale 1 : 50

NOTE: REFER TO ELECTRICAL ENGINEER
DRAWINGS FOR TYPICAL LIGHTING/CEILING
SERVICES LOCATIONS & SPECIFICATION.


Key Plan - ILA Ground Floor

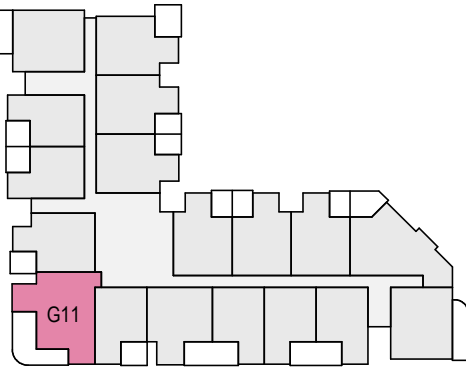

Key Plan - ILA Level 1

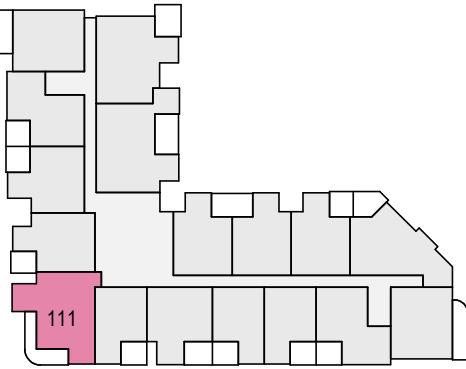

Key Plan - ILA Level 2

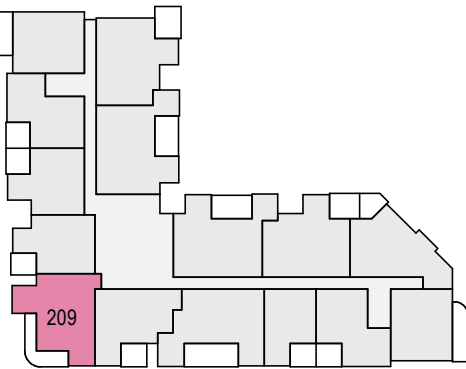

ALLOW FOR MIRRORED CONFIGURATIONS IN ILA LAYOUTS

--- PROVIDE NOGGINGS FOR FUTURE SUPPORT

ILA Finish Types - Type 4				
Level	Apt Number	No. of Bed	Finish Type	Mirrored
ILA_Ground	APT-G11	2 BED	STANDARD	No
ILA_Level 1	APT-111	2 BED	STANDARD	No
ILA_Level 2	APT-209	2 BED	STANDARD	No

Keynote Legend

ACU	AIR CONDITIONING UNIT
AP	ACCESS PANEL
BH-J	BULKHEAD - JOINERY TYPE
BH-P	BULKHEAD - PLASTERBOARD TYPE
EXH	EXHAUST
LED	LED STRIP LIGHT - RECESSED
LF1	LIGHT FITTING - REFER TO ELECTRICAL ENGINEER SPECIFICATION
MFD	MULTI-FUNCTION DEVICE (THERMAL, SMOKE, WIFI)
PD2	PENDANT LIGHT - TYPE 2
SPK	ANNUNCIATOR SPEAKER
SPR	SPRINKLER
W1	WALL LIGHT - TYPE 1

FOR CONSTRUCTION

Clarke
Hopkins
Clarke

ClarkeHopkinsClarke
Melbourne | Wurundjeri
L3, Melbourne Connect
700 Swanston Street
Carlton VIC 3063
Telephone (03) 9419 4340
Email studio@chc.com.au
www.chc.com.au

Sydney | Gadigal Country
Suite 3, Ground Floor
91 Campbell Street
Surry Hills NSW 2010
Telephone (02) 9221 9200
Email studio@chc.com.au
www.chc.com.au

Scale As indicated @ A1
Date 01/03/2024
Drawn TM
Architect EL

Project
Summerset Oakleigh
52 Golf Road, Oakleigh South, VIC

Drawing
ILA - Apartment Type 4 Plan & RCP

Drawing No.
230185/A2803

C1