


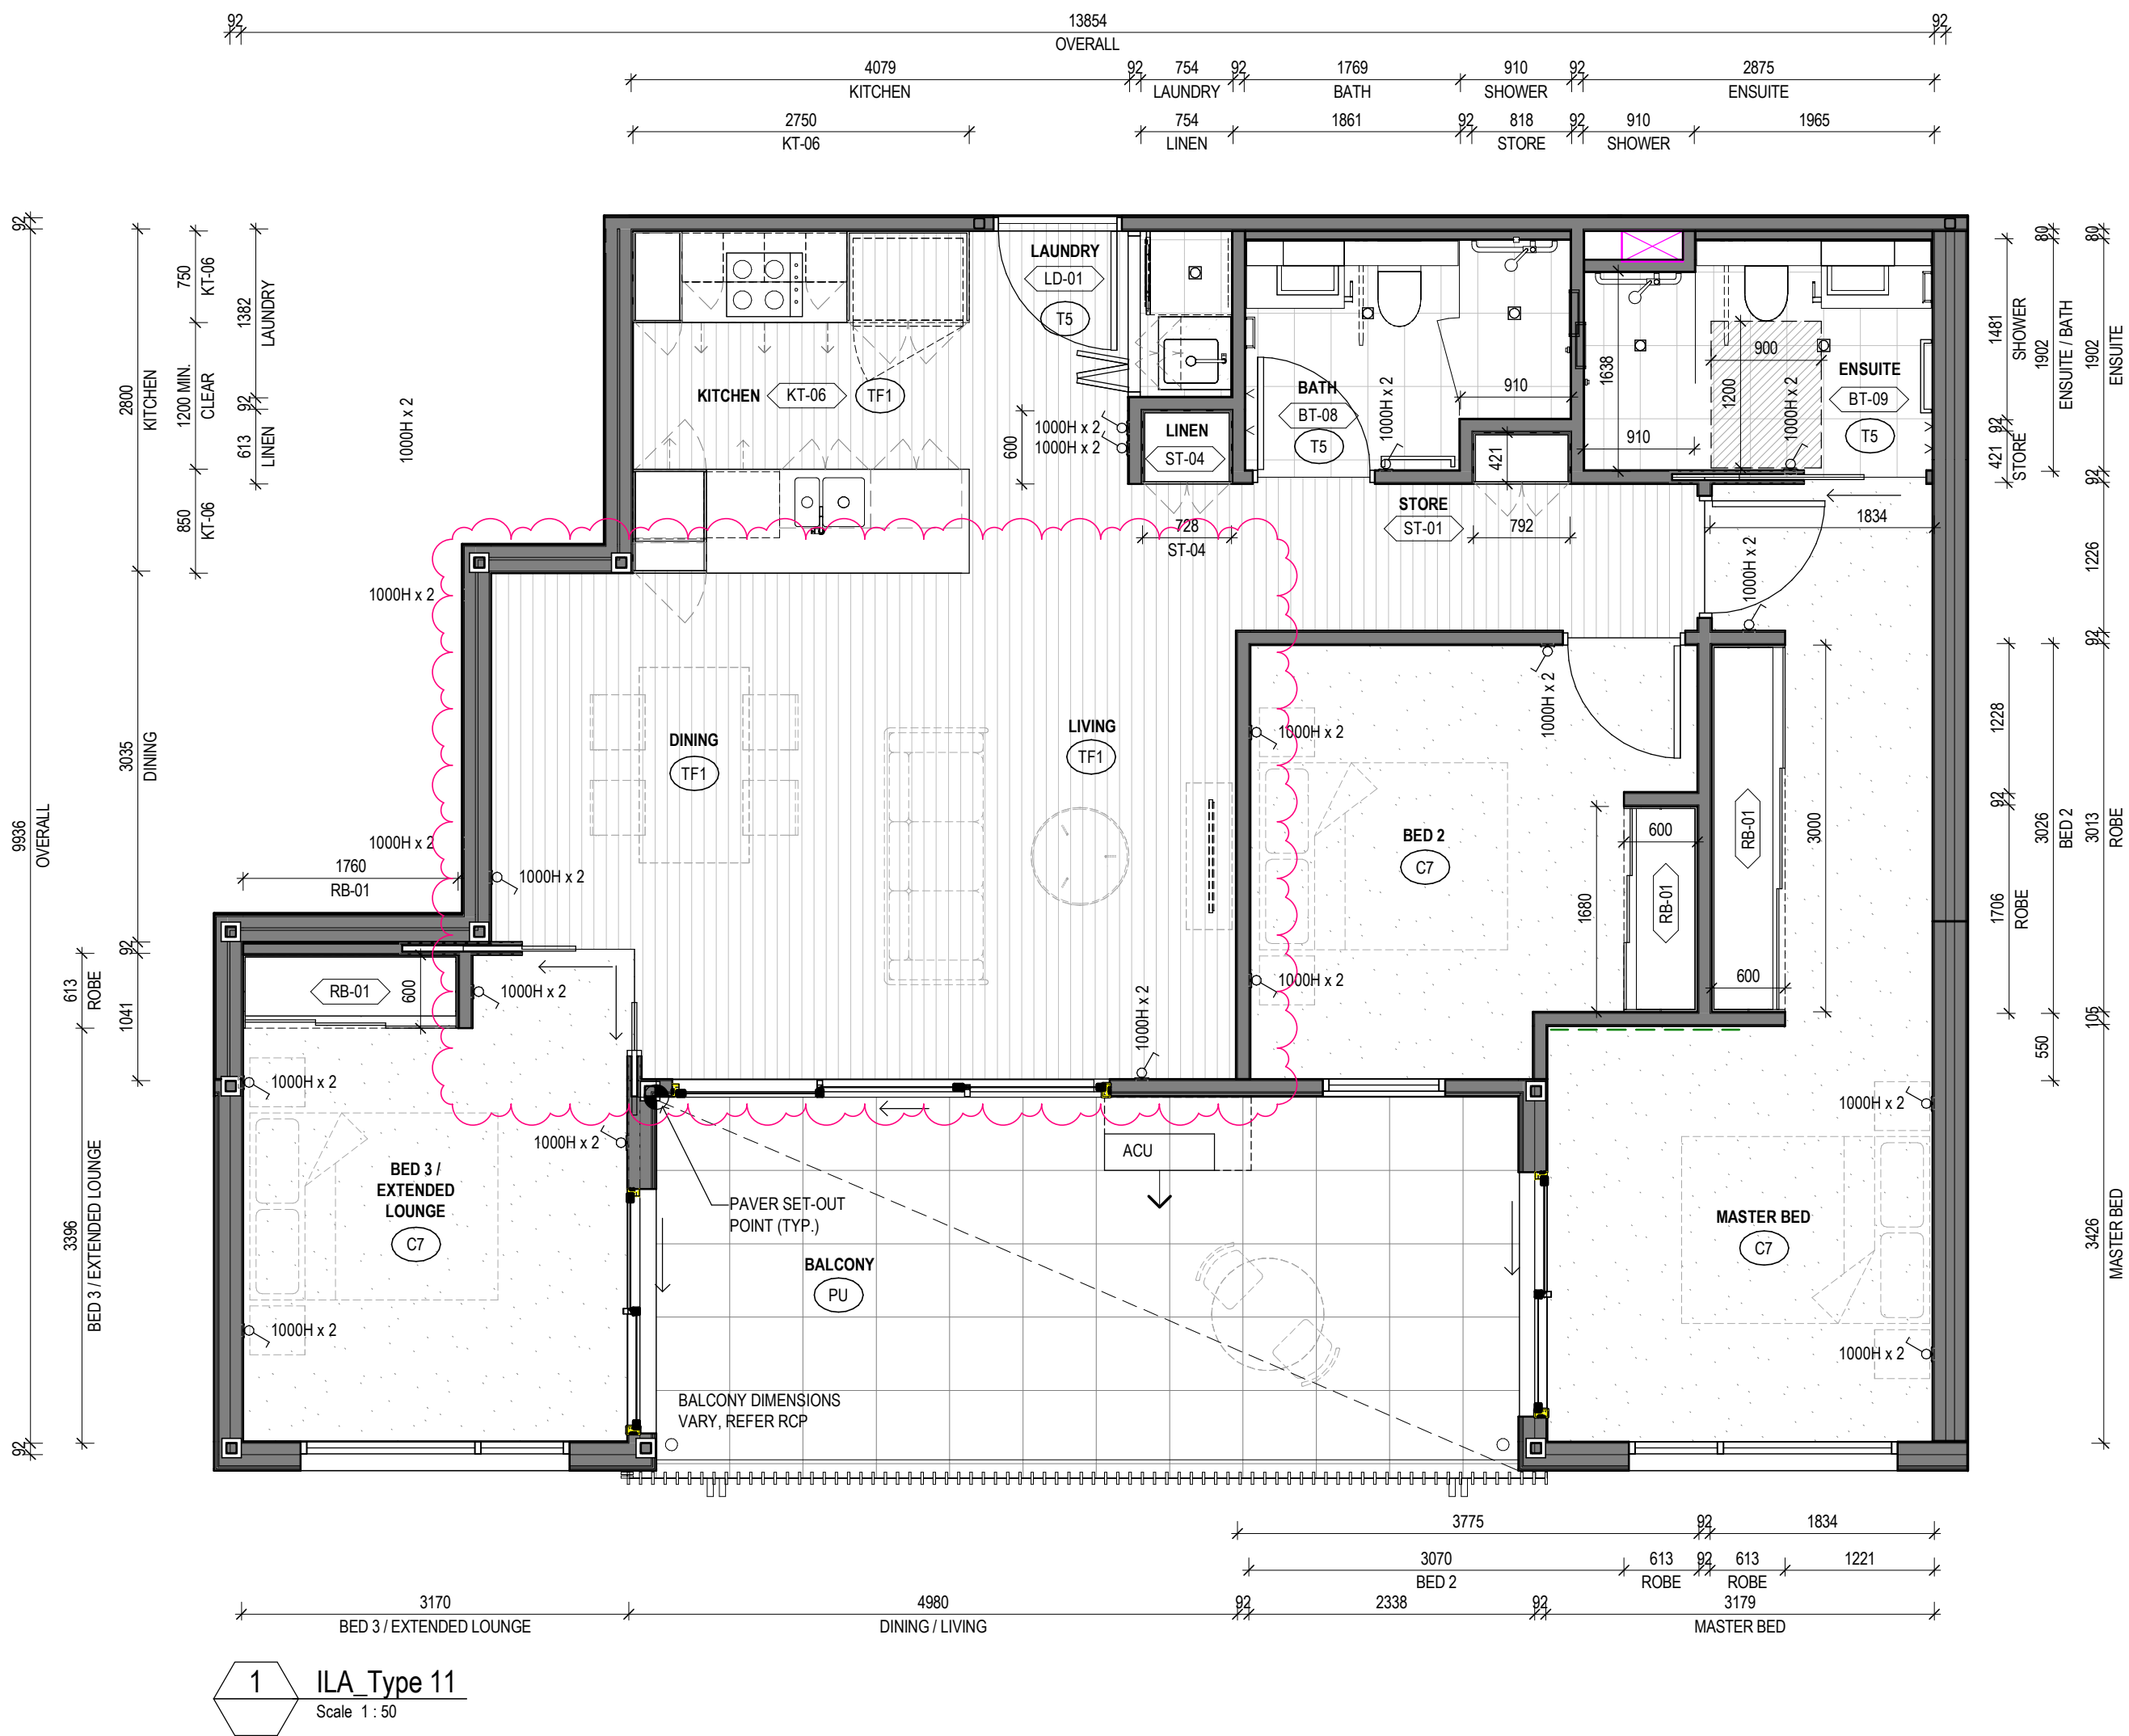


2 ILA Type 11 RCP
Scale 1:50


NOTE: REFER TO ELECTRICAL ENGINEER DRAWINGS FOR TYPICAL LIGHTING/CEILING SERVICES LOCATIONS & SPECIFICATION.




Key Plan - ILA Ground Floor

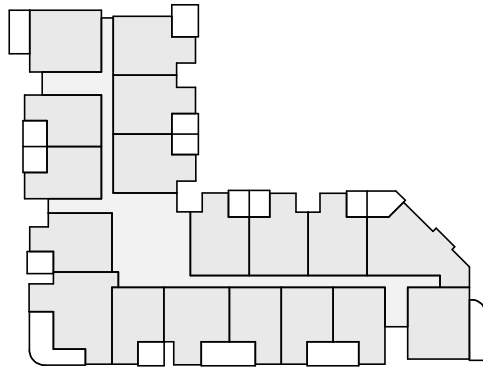

Key Plan - ILA Level 1

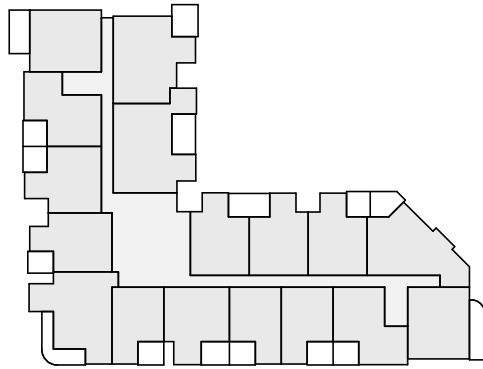

Key Plan - ILA Level 2

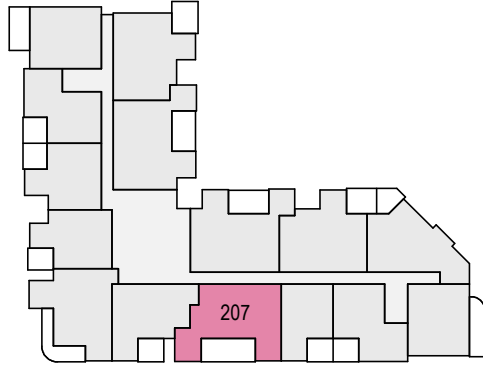

ALLOW FOR MIRRORED CONFIGURATIONS IN ILA LAYOUTS

--- PROVIDE NOGGINGS FOR FUTURE SUPPORT

ILA Finish Types - Type 11				
Level	Apt Number	No. of Bed	Finish Type	Mirrored
ILA_Level 2	APT-207	3 BED	PREMIUM	No

Keynote Legend

ACU	AIR CONDITIONING UNIT
AP	ACCESS PANEL
BH-J	BULKHEAD - JOINERY TYPE
BH-P	BULKHEAD - PLASTERBOARD TYPE
EXH	EXHAUST
LED	LED STRIP LIGHT - RECESSED
LF1	LIGHT FITTING - REFER TO ELECTRICAL ENGINEER SPECIFICATION
MFD	MULTI-FUNCTION DEVICE (THERMAL, SMOKE, WIF)
PD2	PENDANT LIGHT - TYPE 2
SPK	ANNUNCIATOR SPEAKER
SPR	SPRINKLER
W1	WALL LIGHT - TYPE 1