



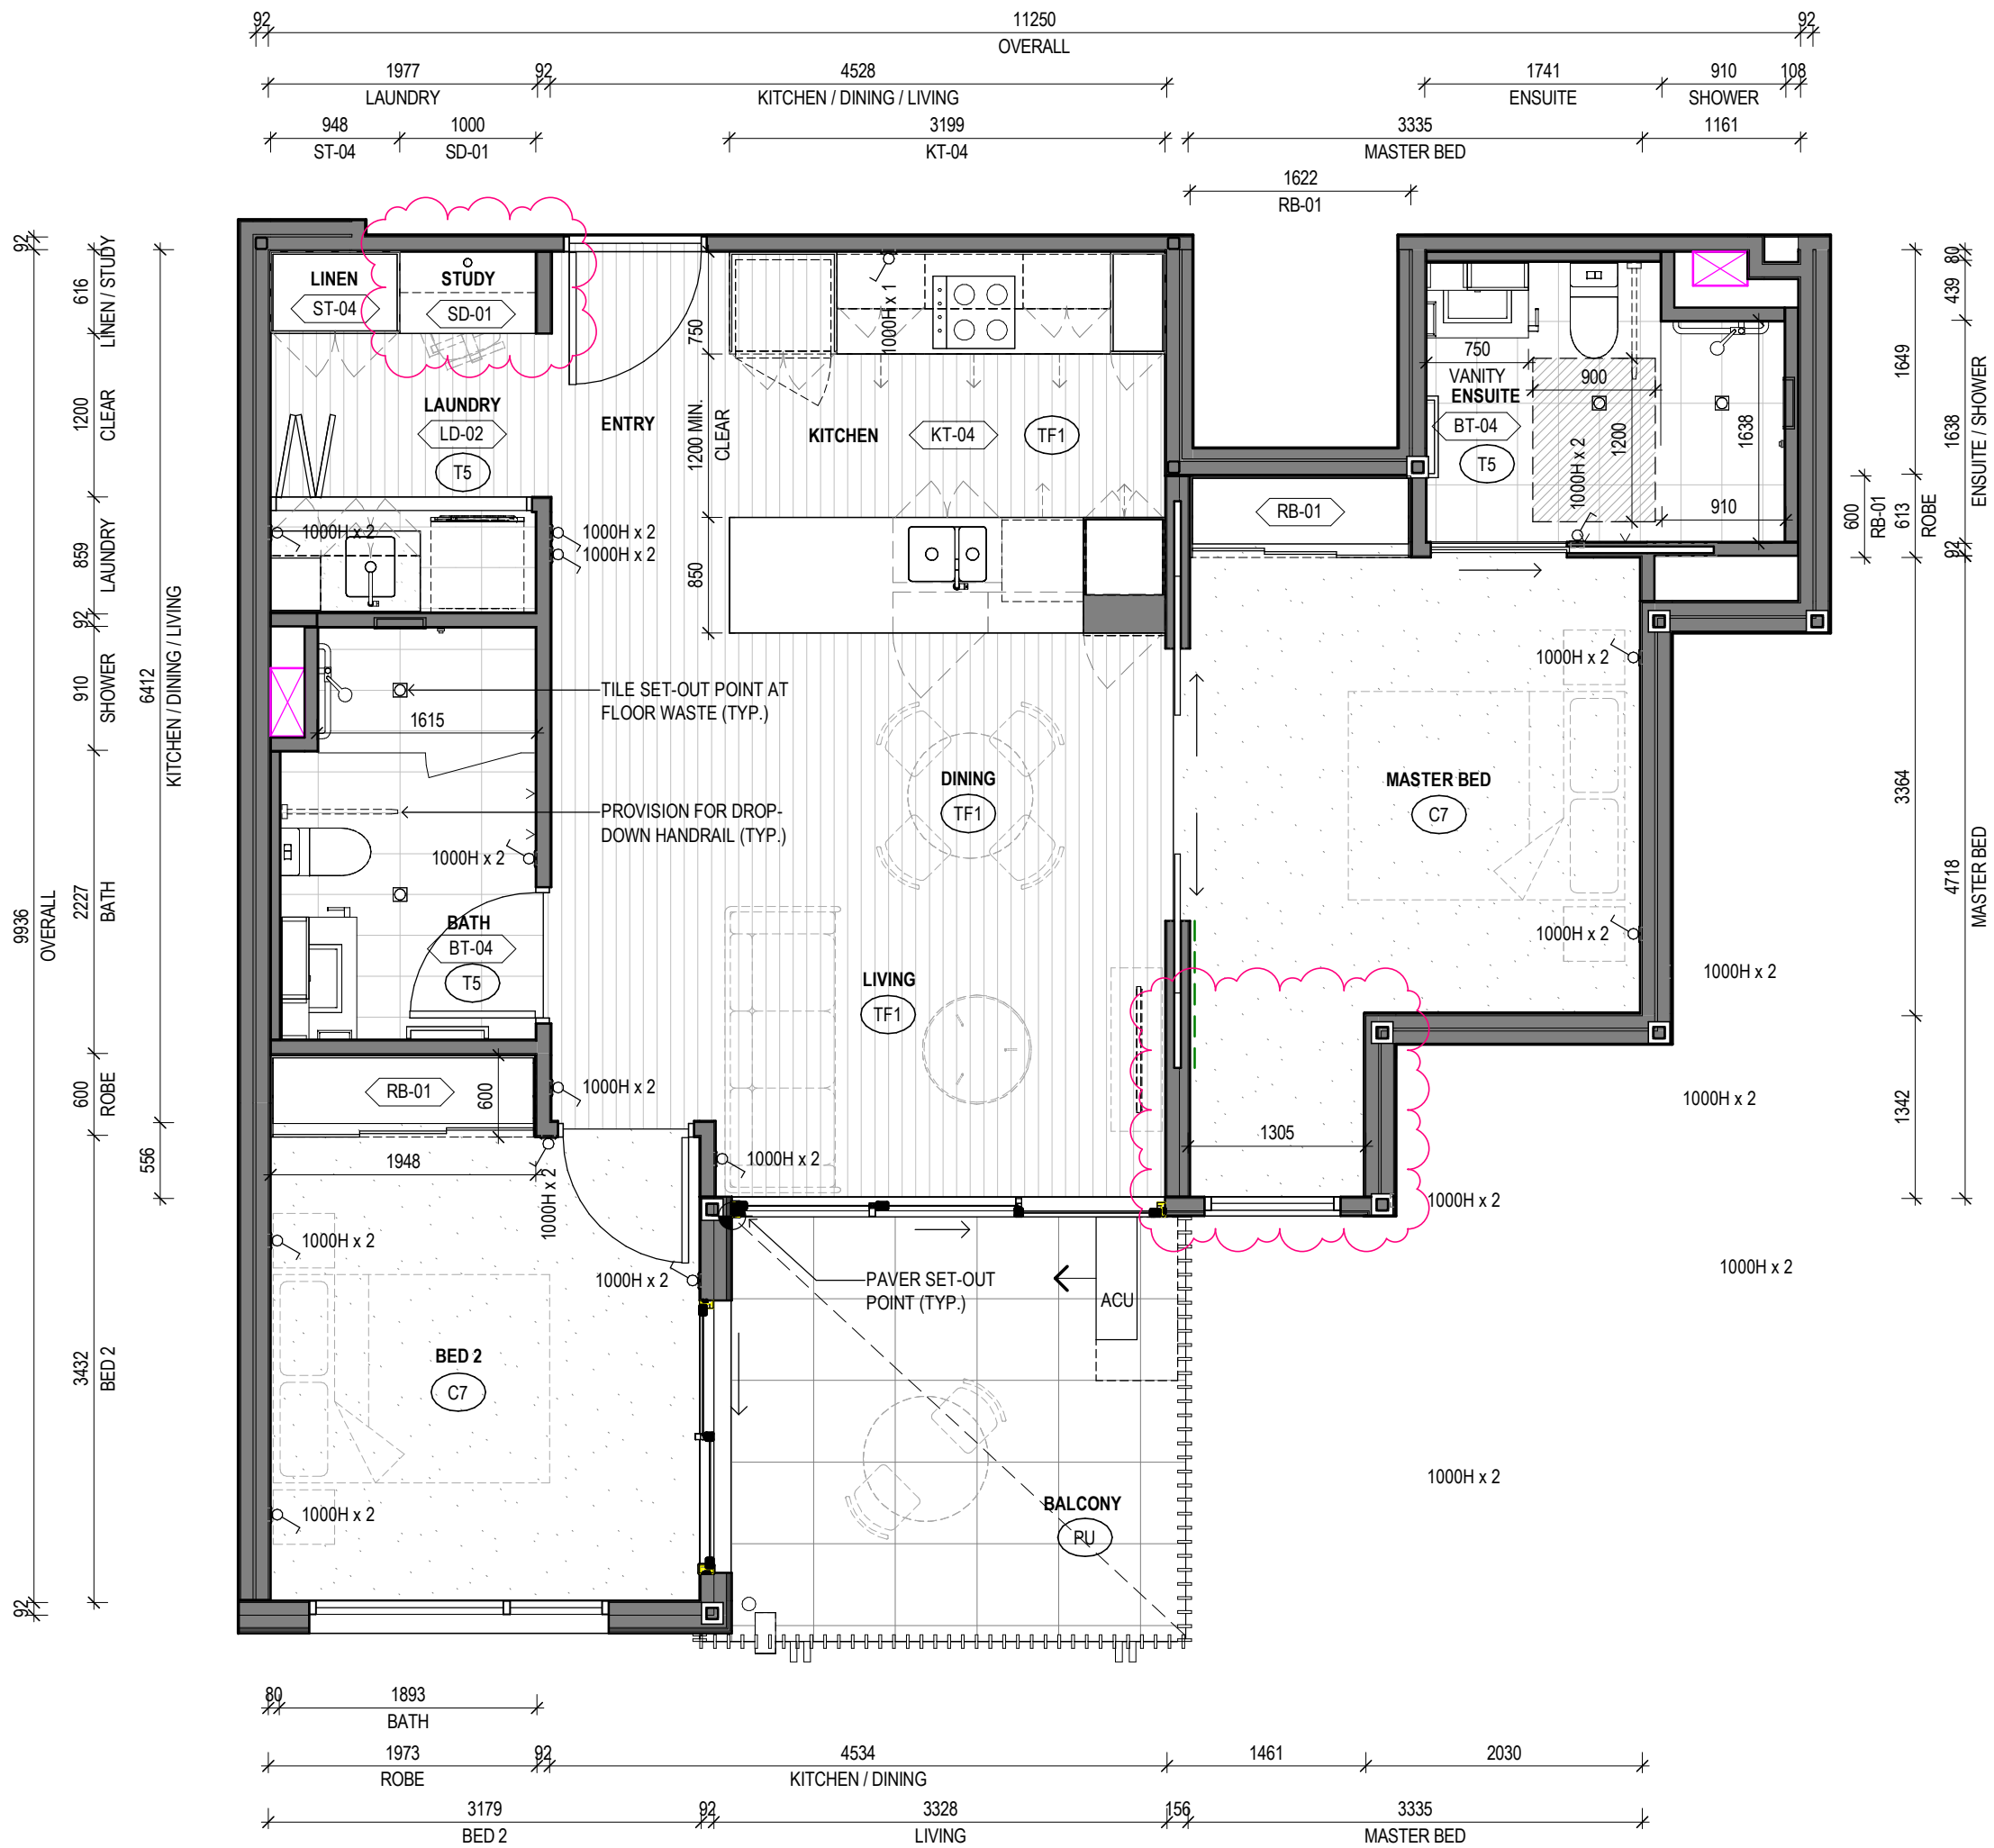


1 ILA Type 12
Scale 1:50

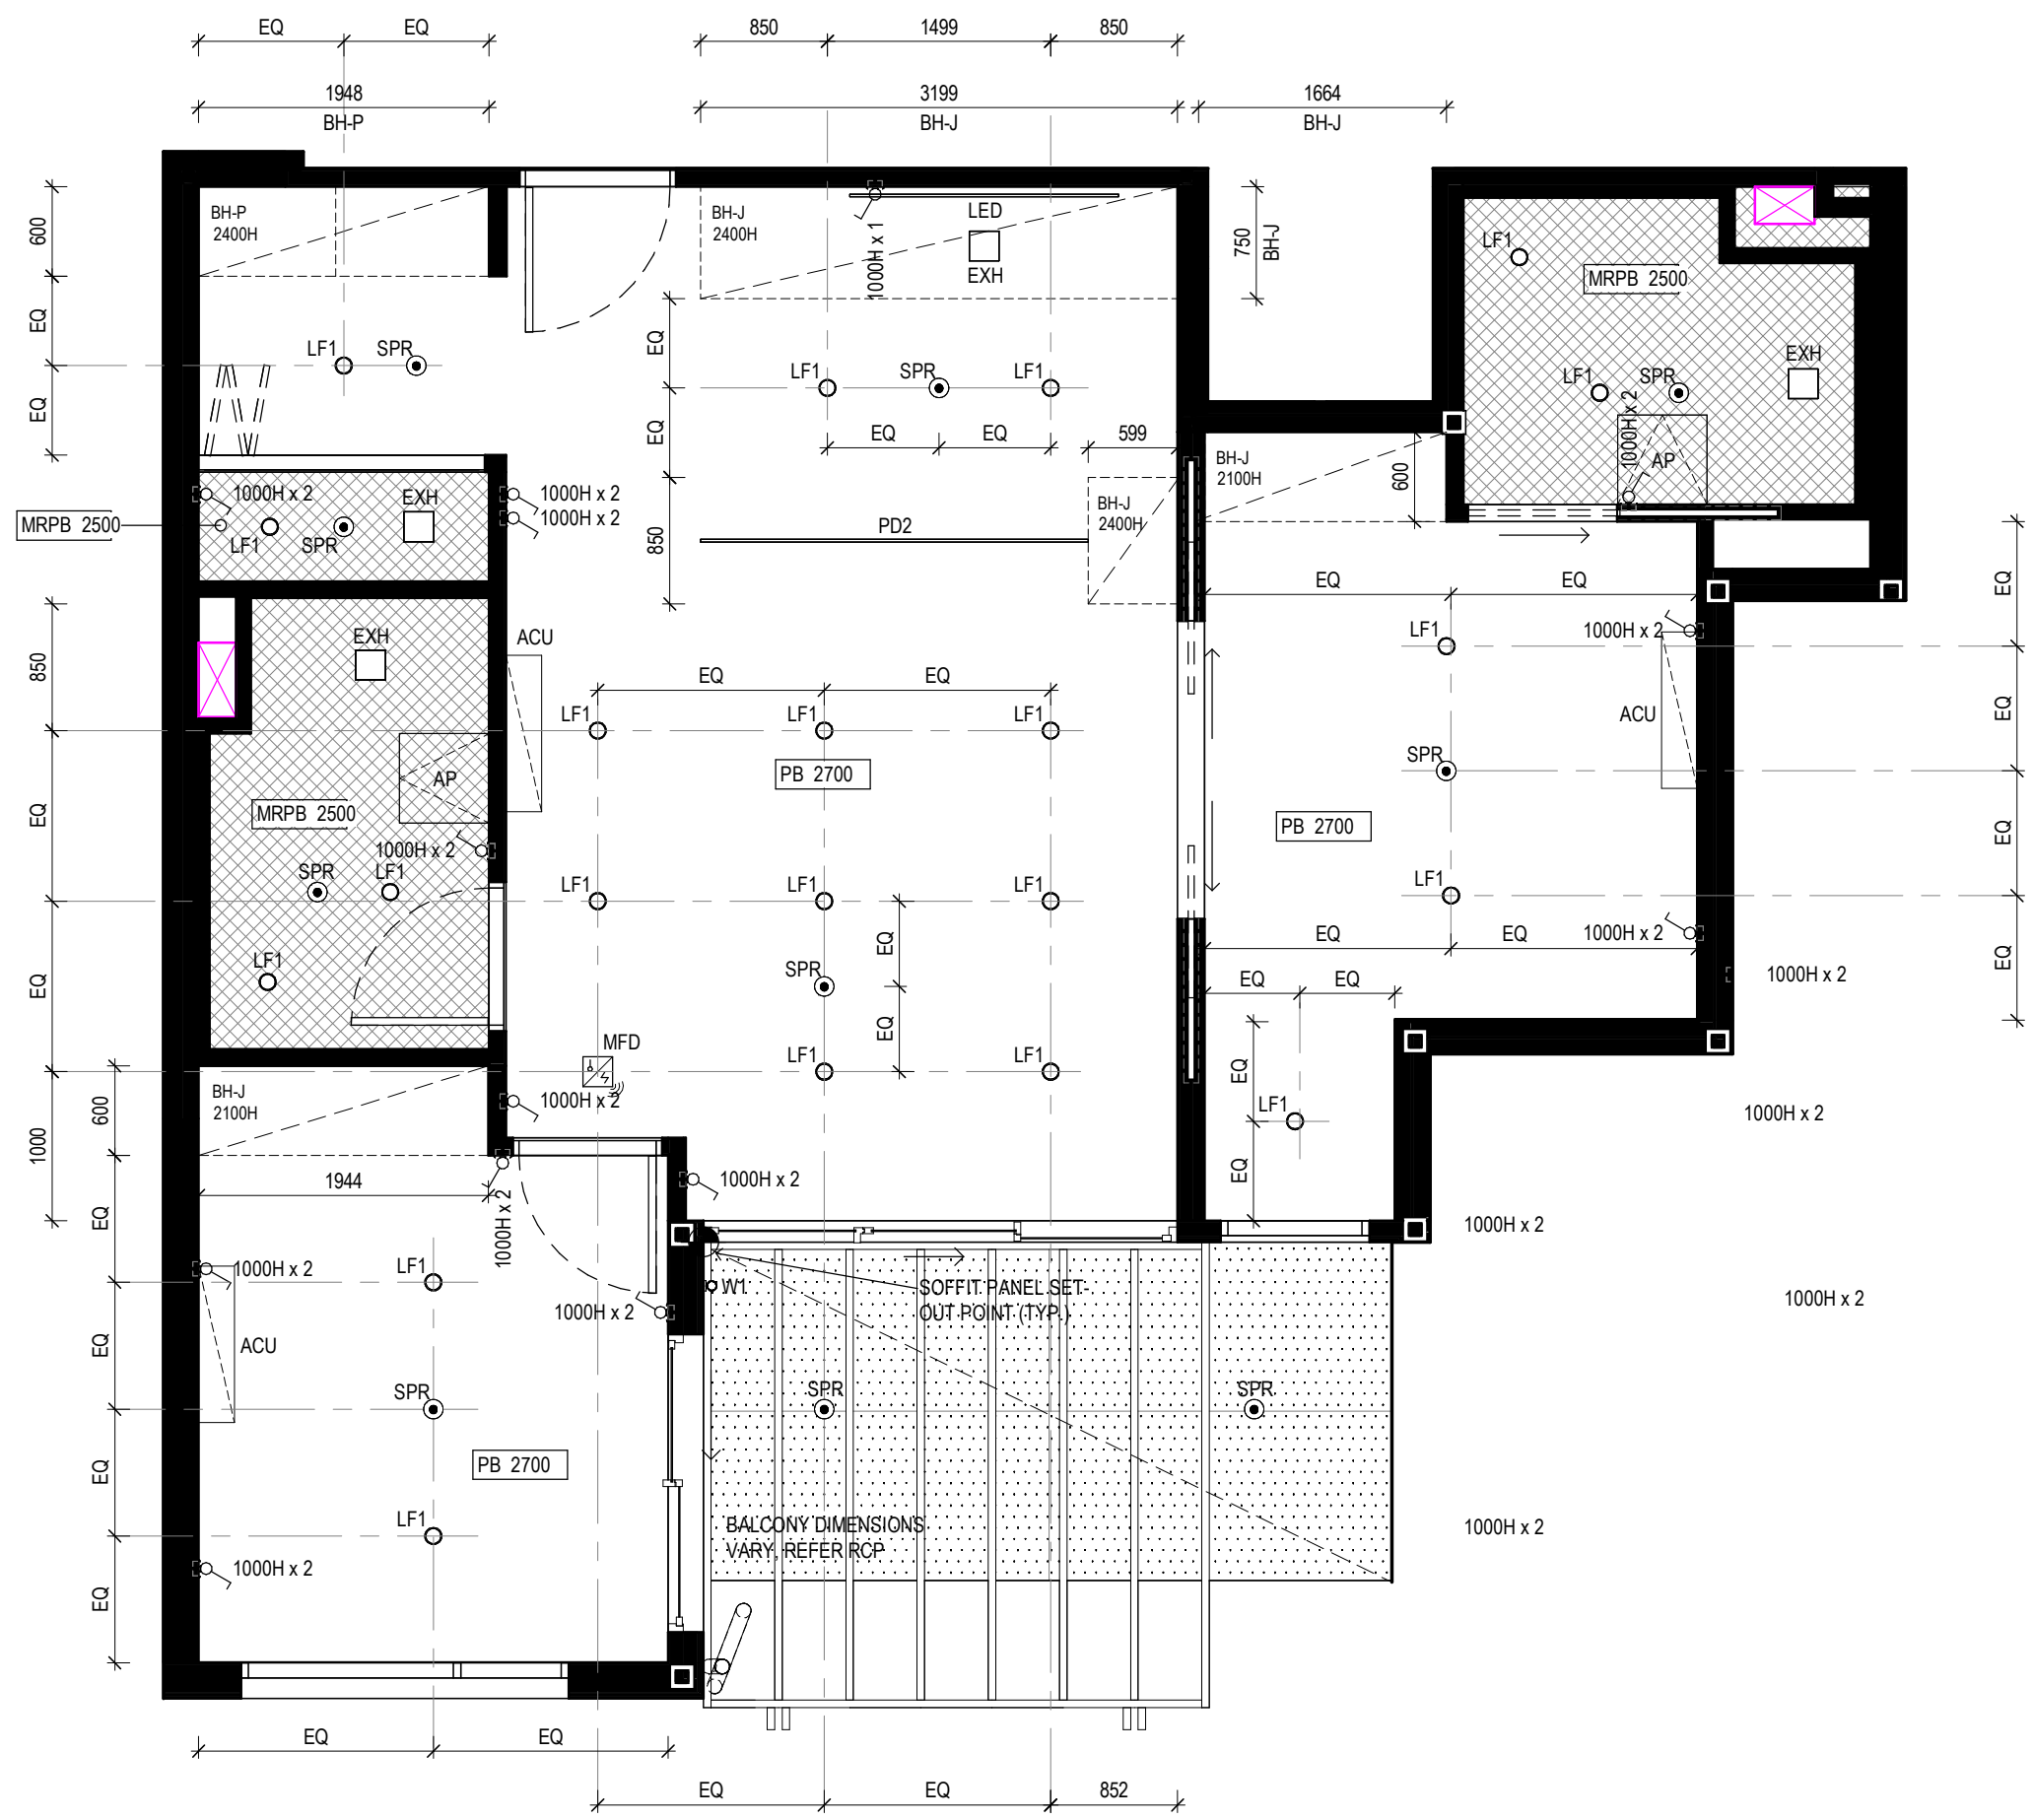


2 ILA Type 12 RCP
Scale 1:50

NOTE: REFER TO ELECTRICAL ENGINEER
DRAWINGS FOR TYPICAL LIGHTING/CEILING
SERVICES LOCATIONS & SPECIFICATION.


Key Plan - ILA Ground Floor

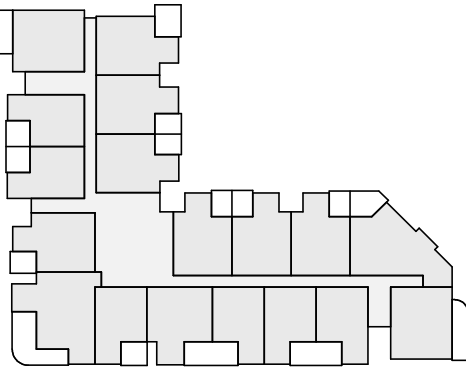

Key Plan - ILA Level 1

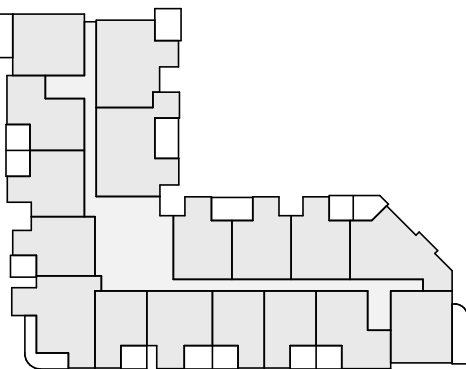

Key Plan - ILA Level 2

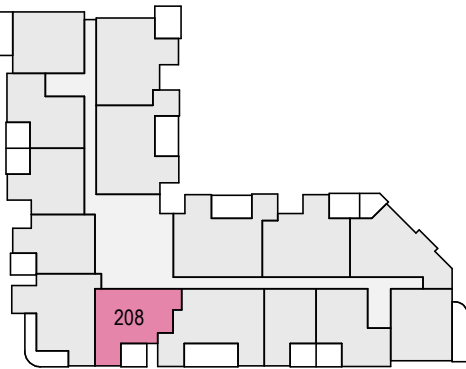

ALLOW FOR MIRRORED CONFIGURATIONS IN ILA LAYOUTS

--- PROVIDE NOGGINGS FOR FUTURE SUPPORT

ILA Finish Types - Type 12				
Level	Apt Number	No. of Bed	Finish Type	Mirrored
ILA_Level 2	APT-208	2 BED	STANDARD	No

Keynote Legend

ACU	AIR CONDITIONING UNIT
AP	ACCESS PANEL
BH-J	BULKHEAD - JOINERY TYPE
BH-P	BULKHEAD - PLASTERBOARD TYPE
EXH	EXHAUST
LED	LED STRIP LIGHT - RECESSED
LF1	LIGHT FITTING - REFER TO ELECTRICAL ENGINEER SPECIFICATION
MFD	MULTI-FUNCTION DEVICE (THERMAL, SMOKE, WIFI)
PD2	PENDANT LIGHT - TYPE 2
SPR	SPRINKLER
W1	WALL LIGHT - TYPE 1

FOR CONSTRUCTION

Drawing No.
230185/A2811

C1

Clarke
Hopkins
Clarke

ClarkeHopkinsClarke
Melbourne | Wurundjeri
L3, Melbourne Connect
700 Swanston Street
Carlton VIC 3063
Telephone (03) 9419 4340
Email studio@chc.com.au
www.chc.com.au

Sydney | Gadigal Country
Suite 3, Ground Floor
91 Campbell Street
Sunny Hills NSW 2010
Telephone (02) 9221 9200
Email studio@chc.com.au
www.chc.com.au

Scale
Date
Drawn
Architect

As indicated @ A1
01/03/2024
TM/NS
EL

Project
Summerset Oakleigh
52 Golf Road, Oakleigh South, VIC

Drawing
ILA - Apartment Type 12 Plan & RCP

Revision/Issue	Date
b Issued for Coordination - 100% DD	2024.04.12
P1 Preliminary ILA Apartment Types & Joineries	2025.08.25
P2 Tender Pack Issue	2025.09.05
P3 ISSUE FOR CONTRACT	2025.10.10
C1 ISSUE FOR CONSTRUCTION - INTERIORS	2026.04.13