
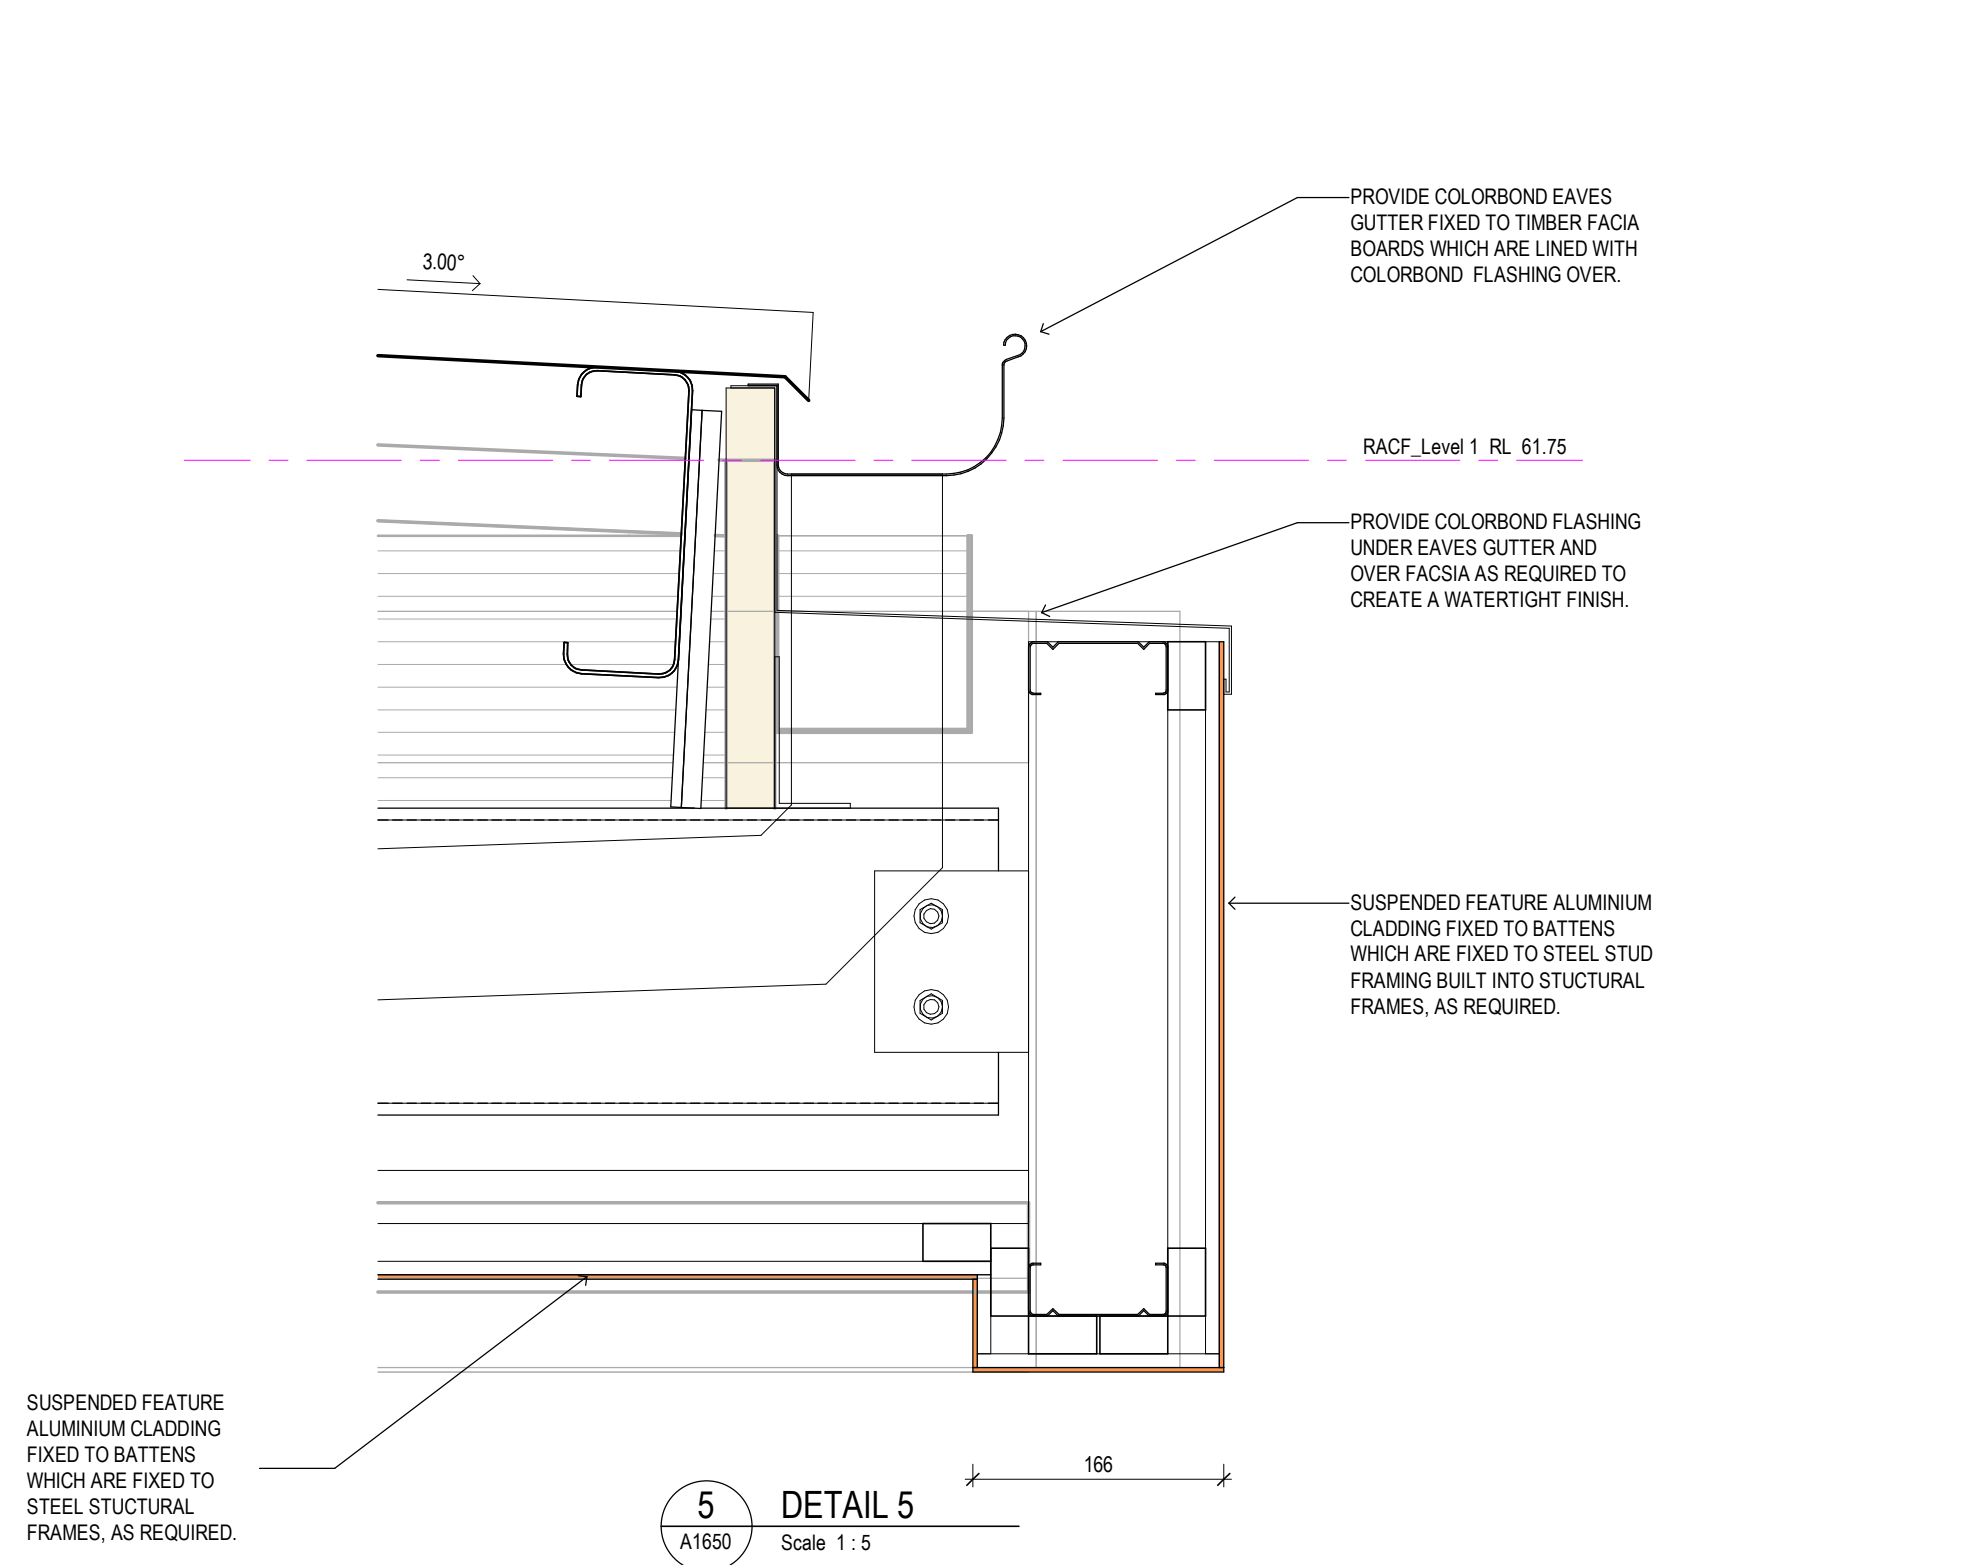
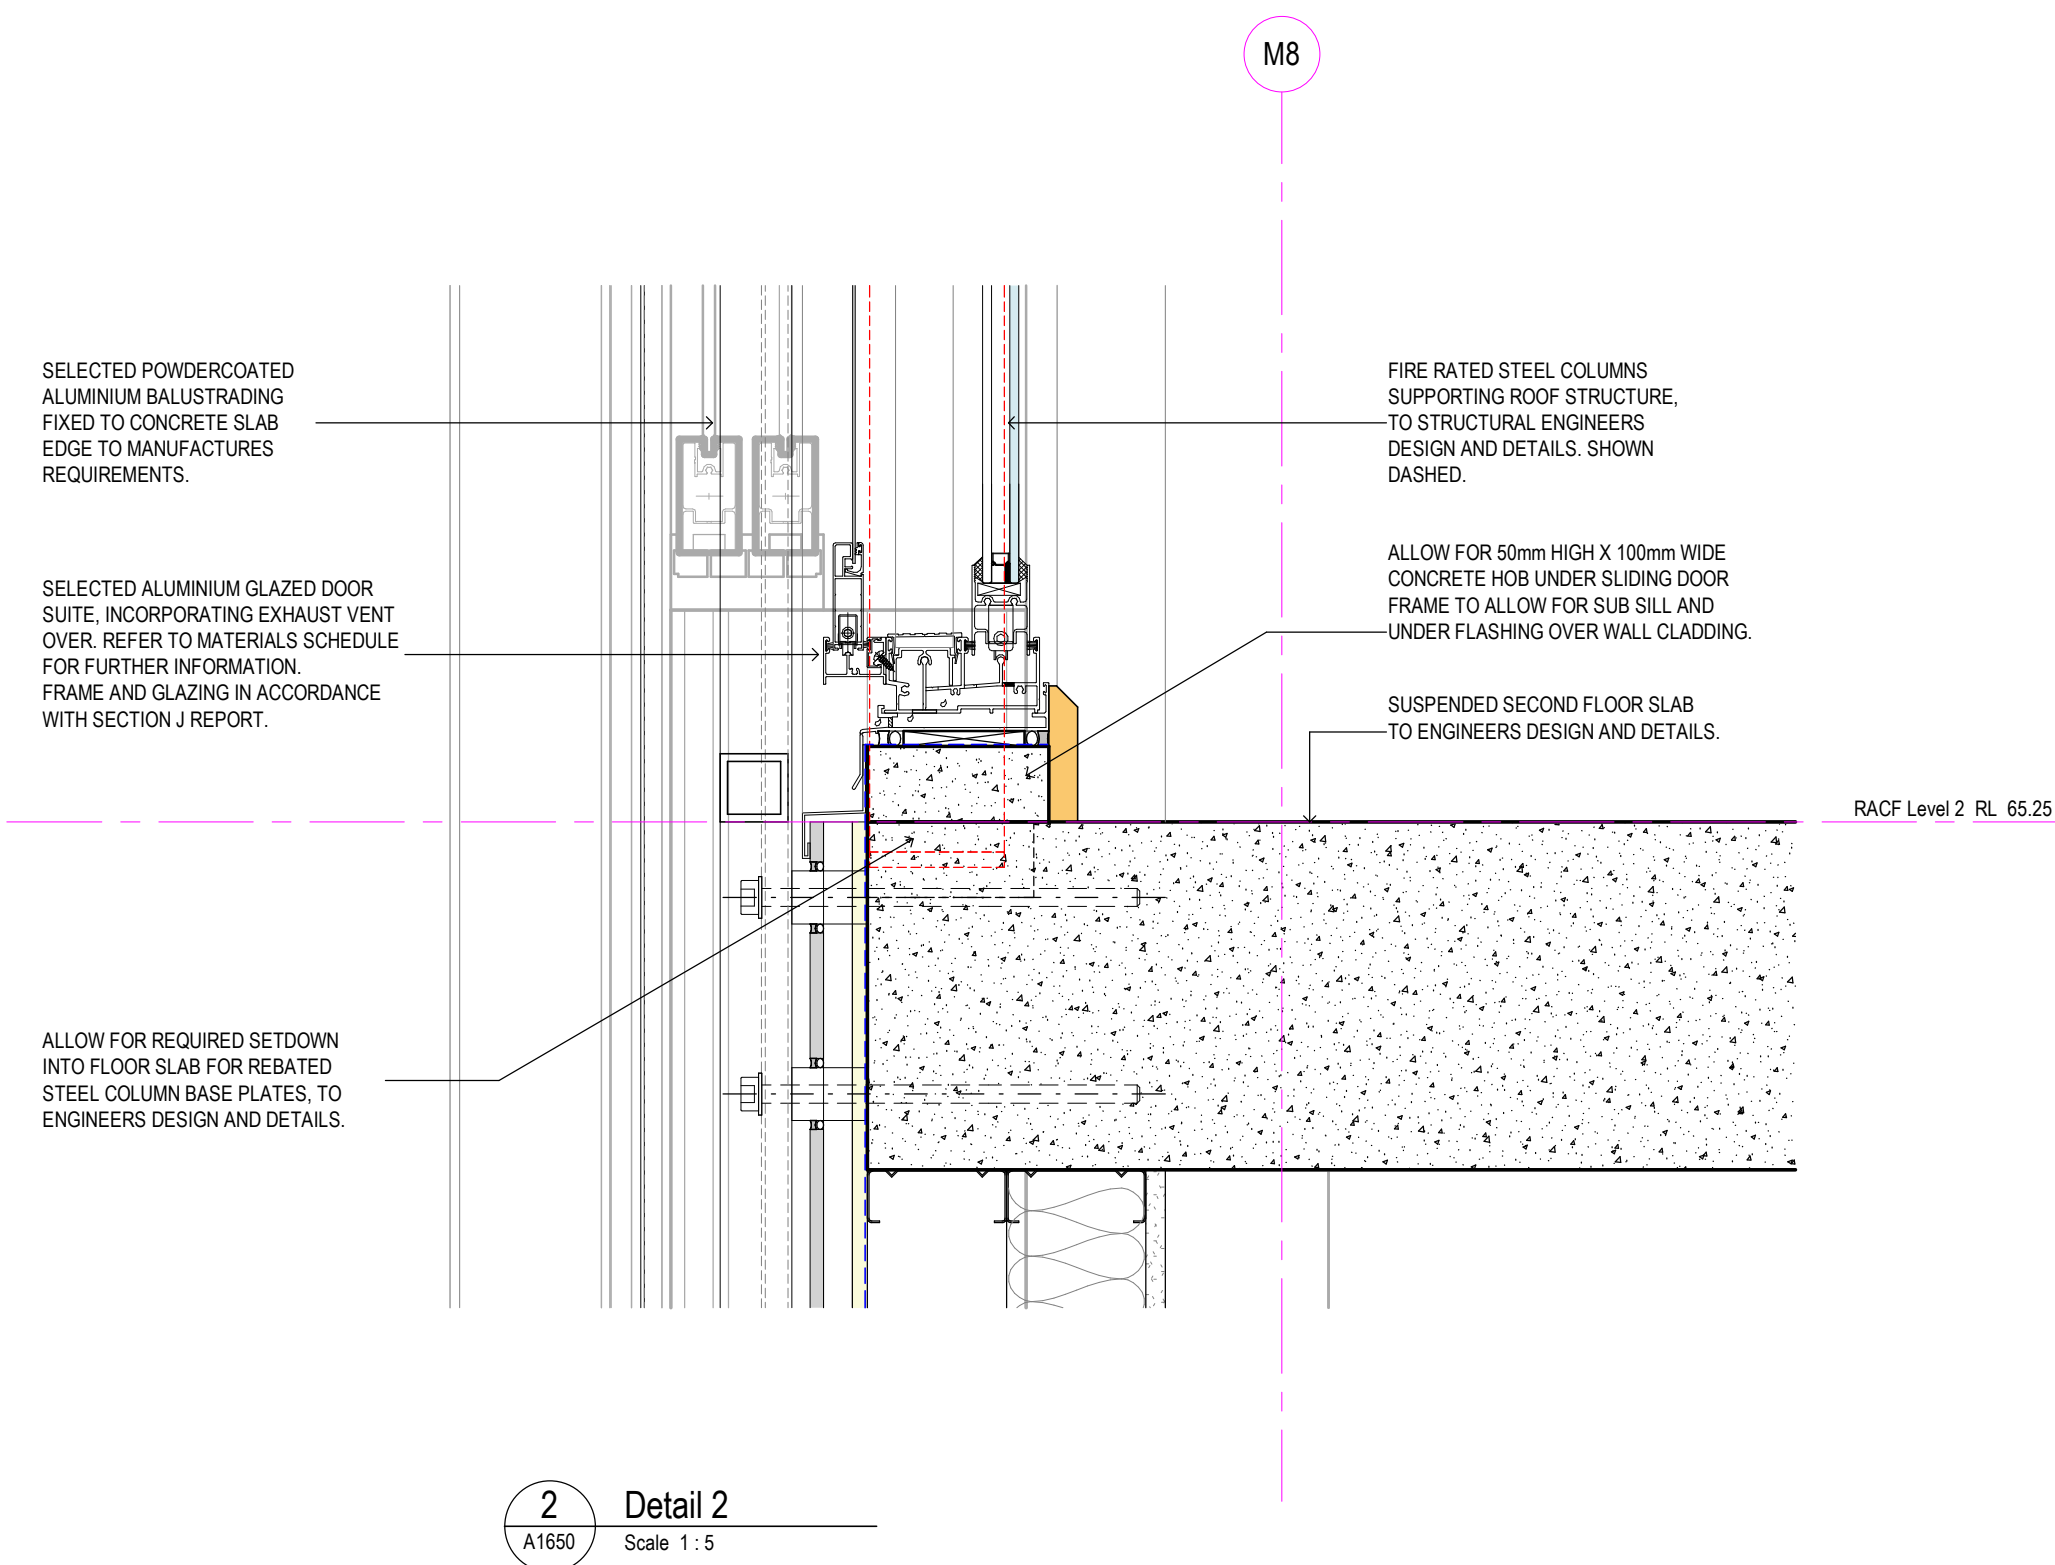
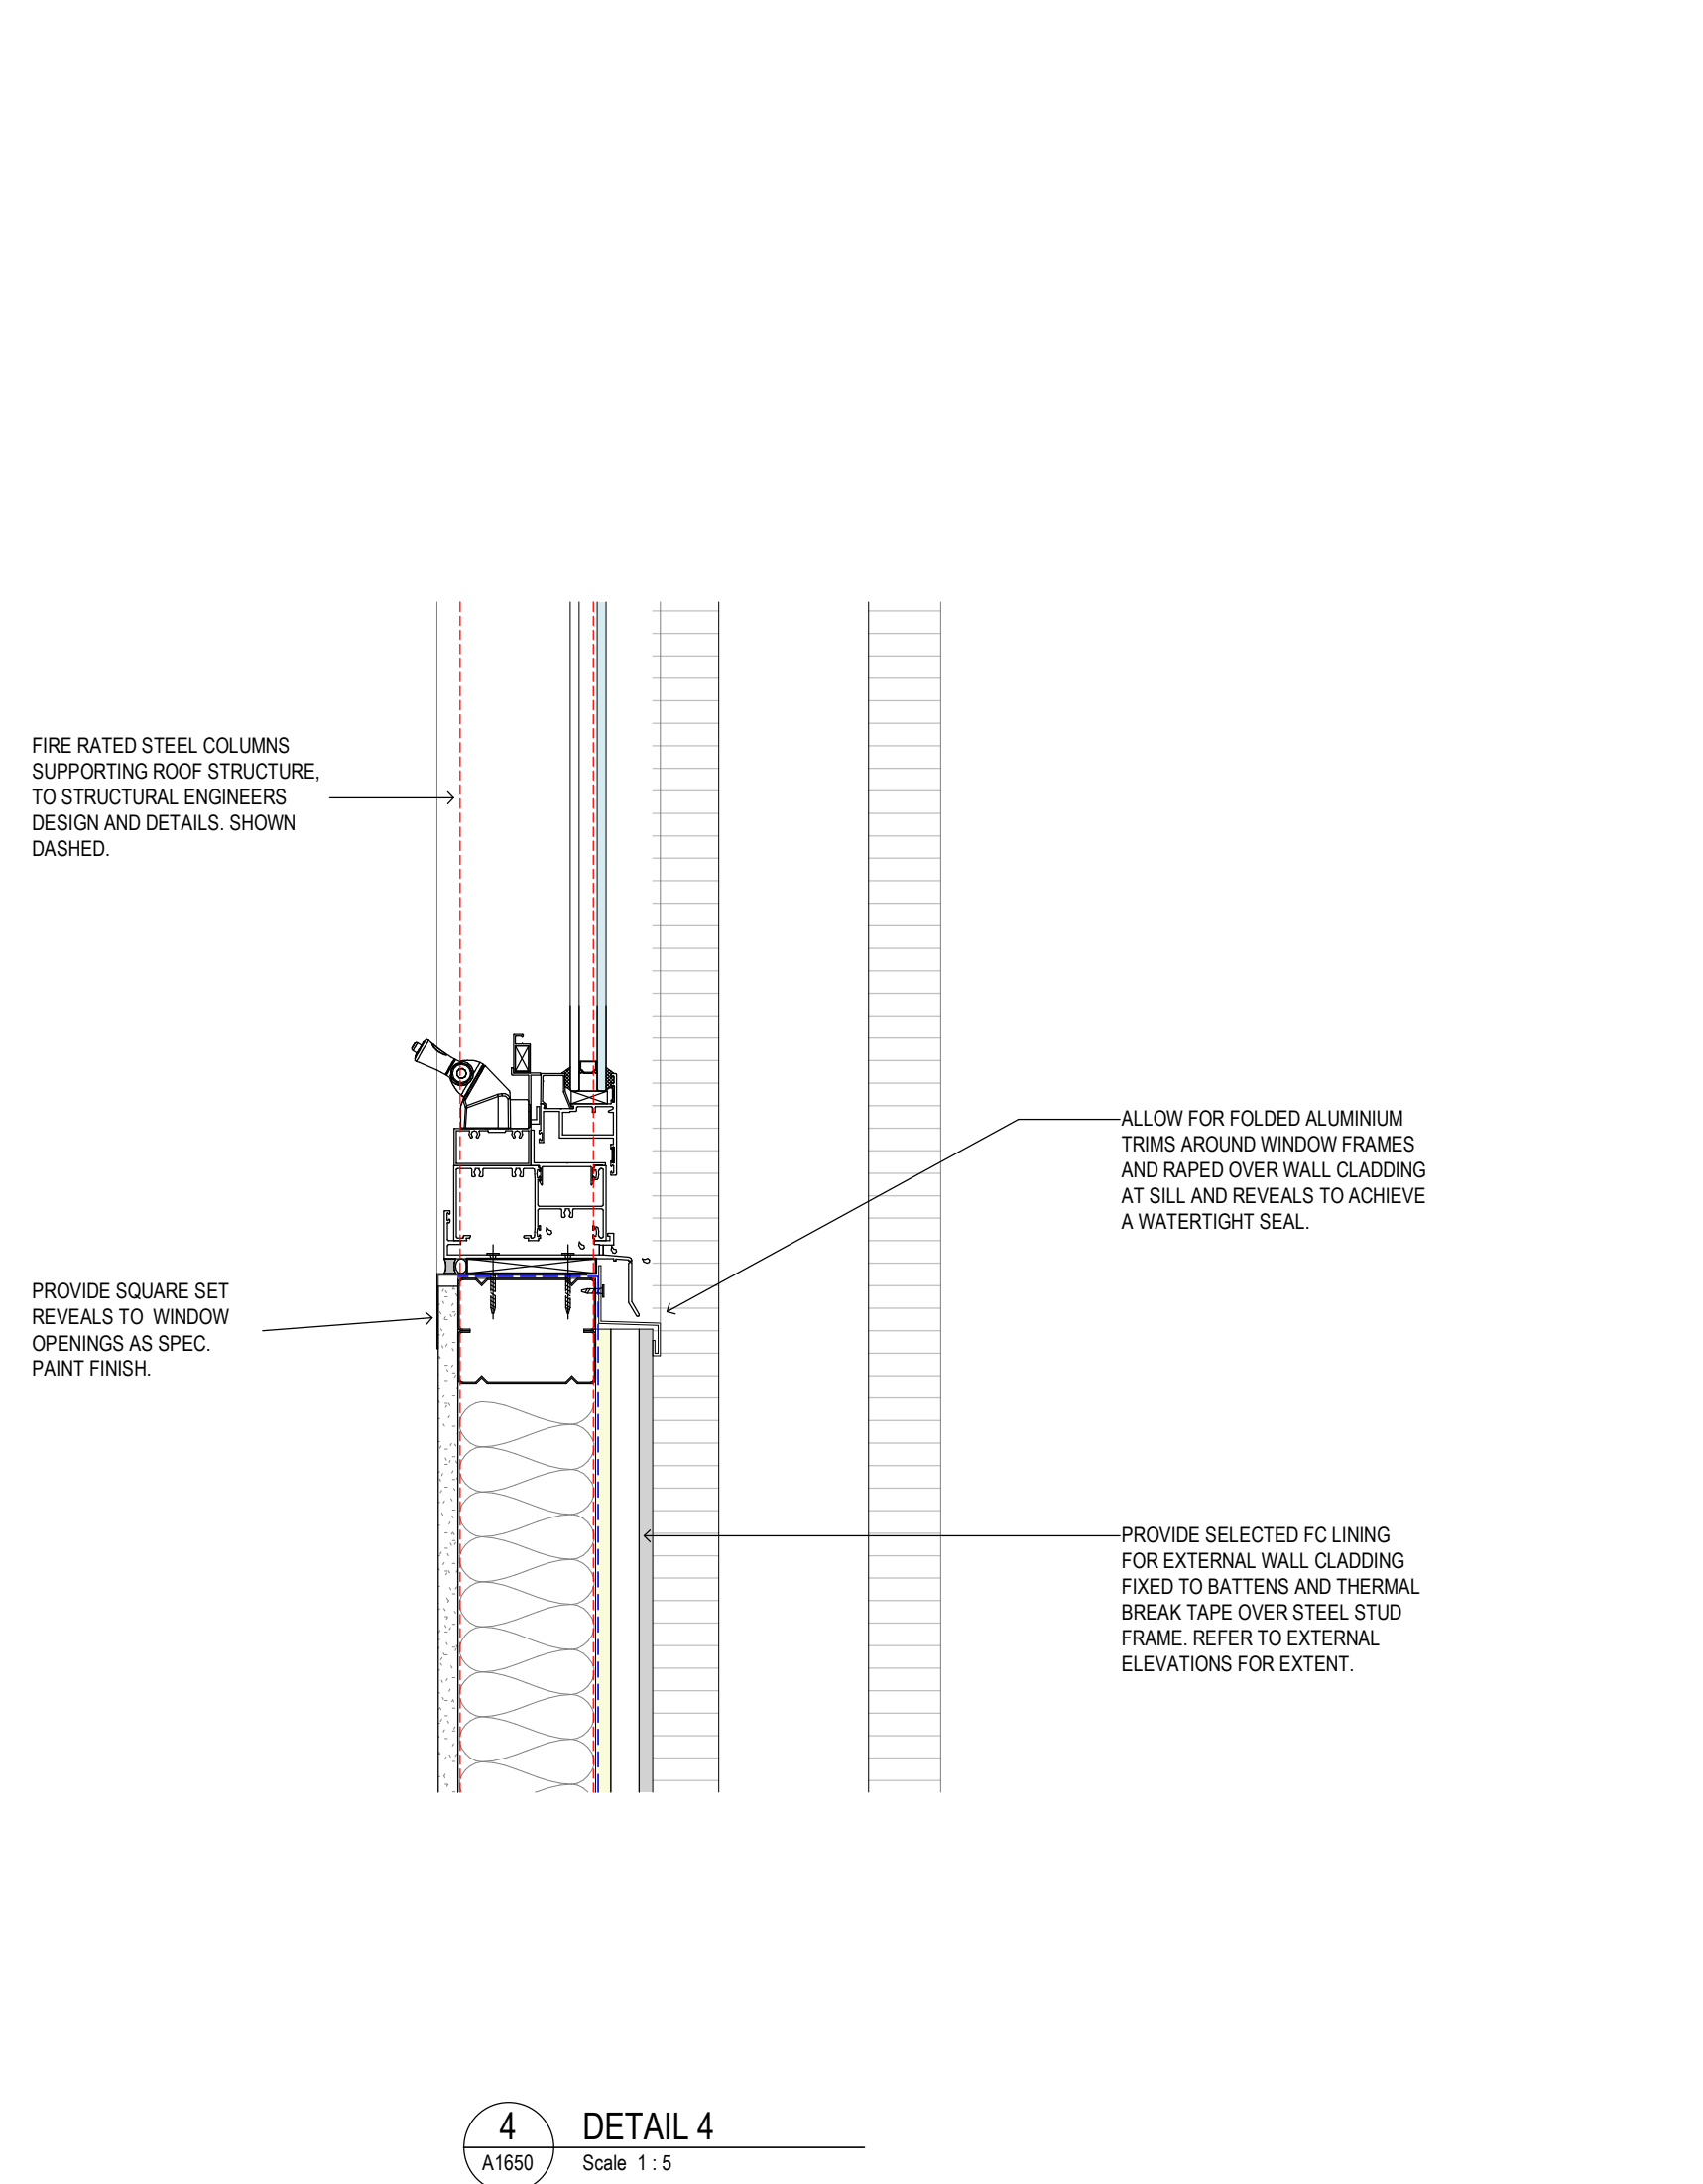
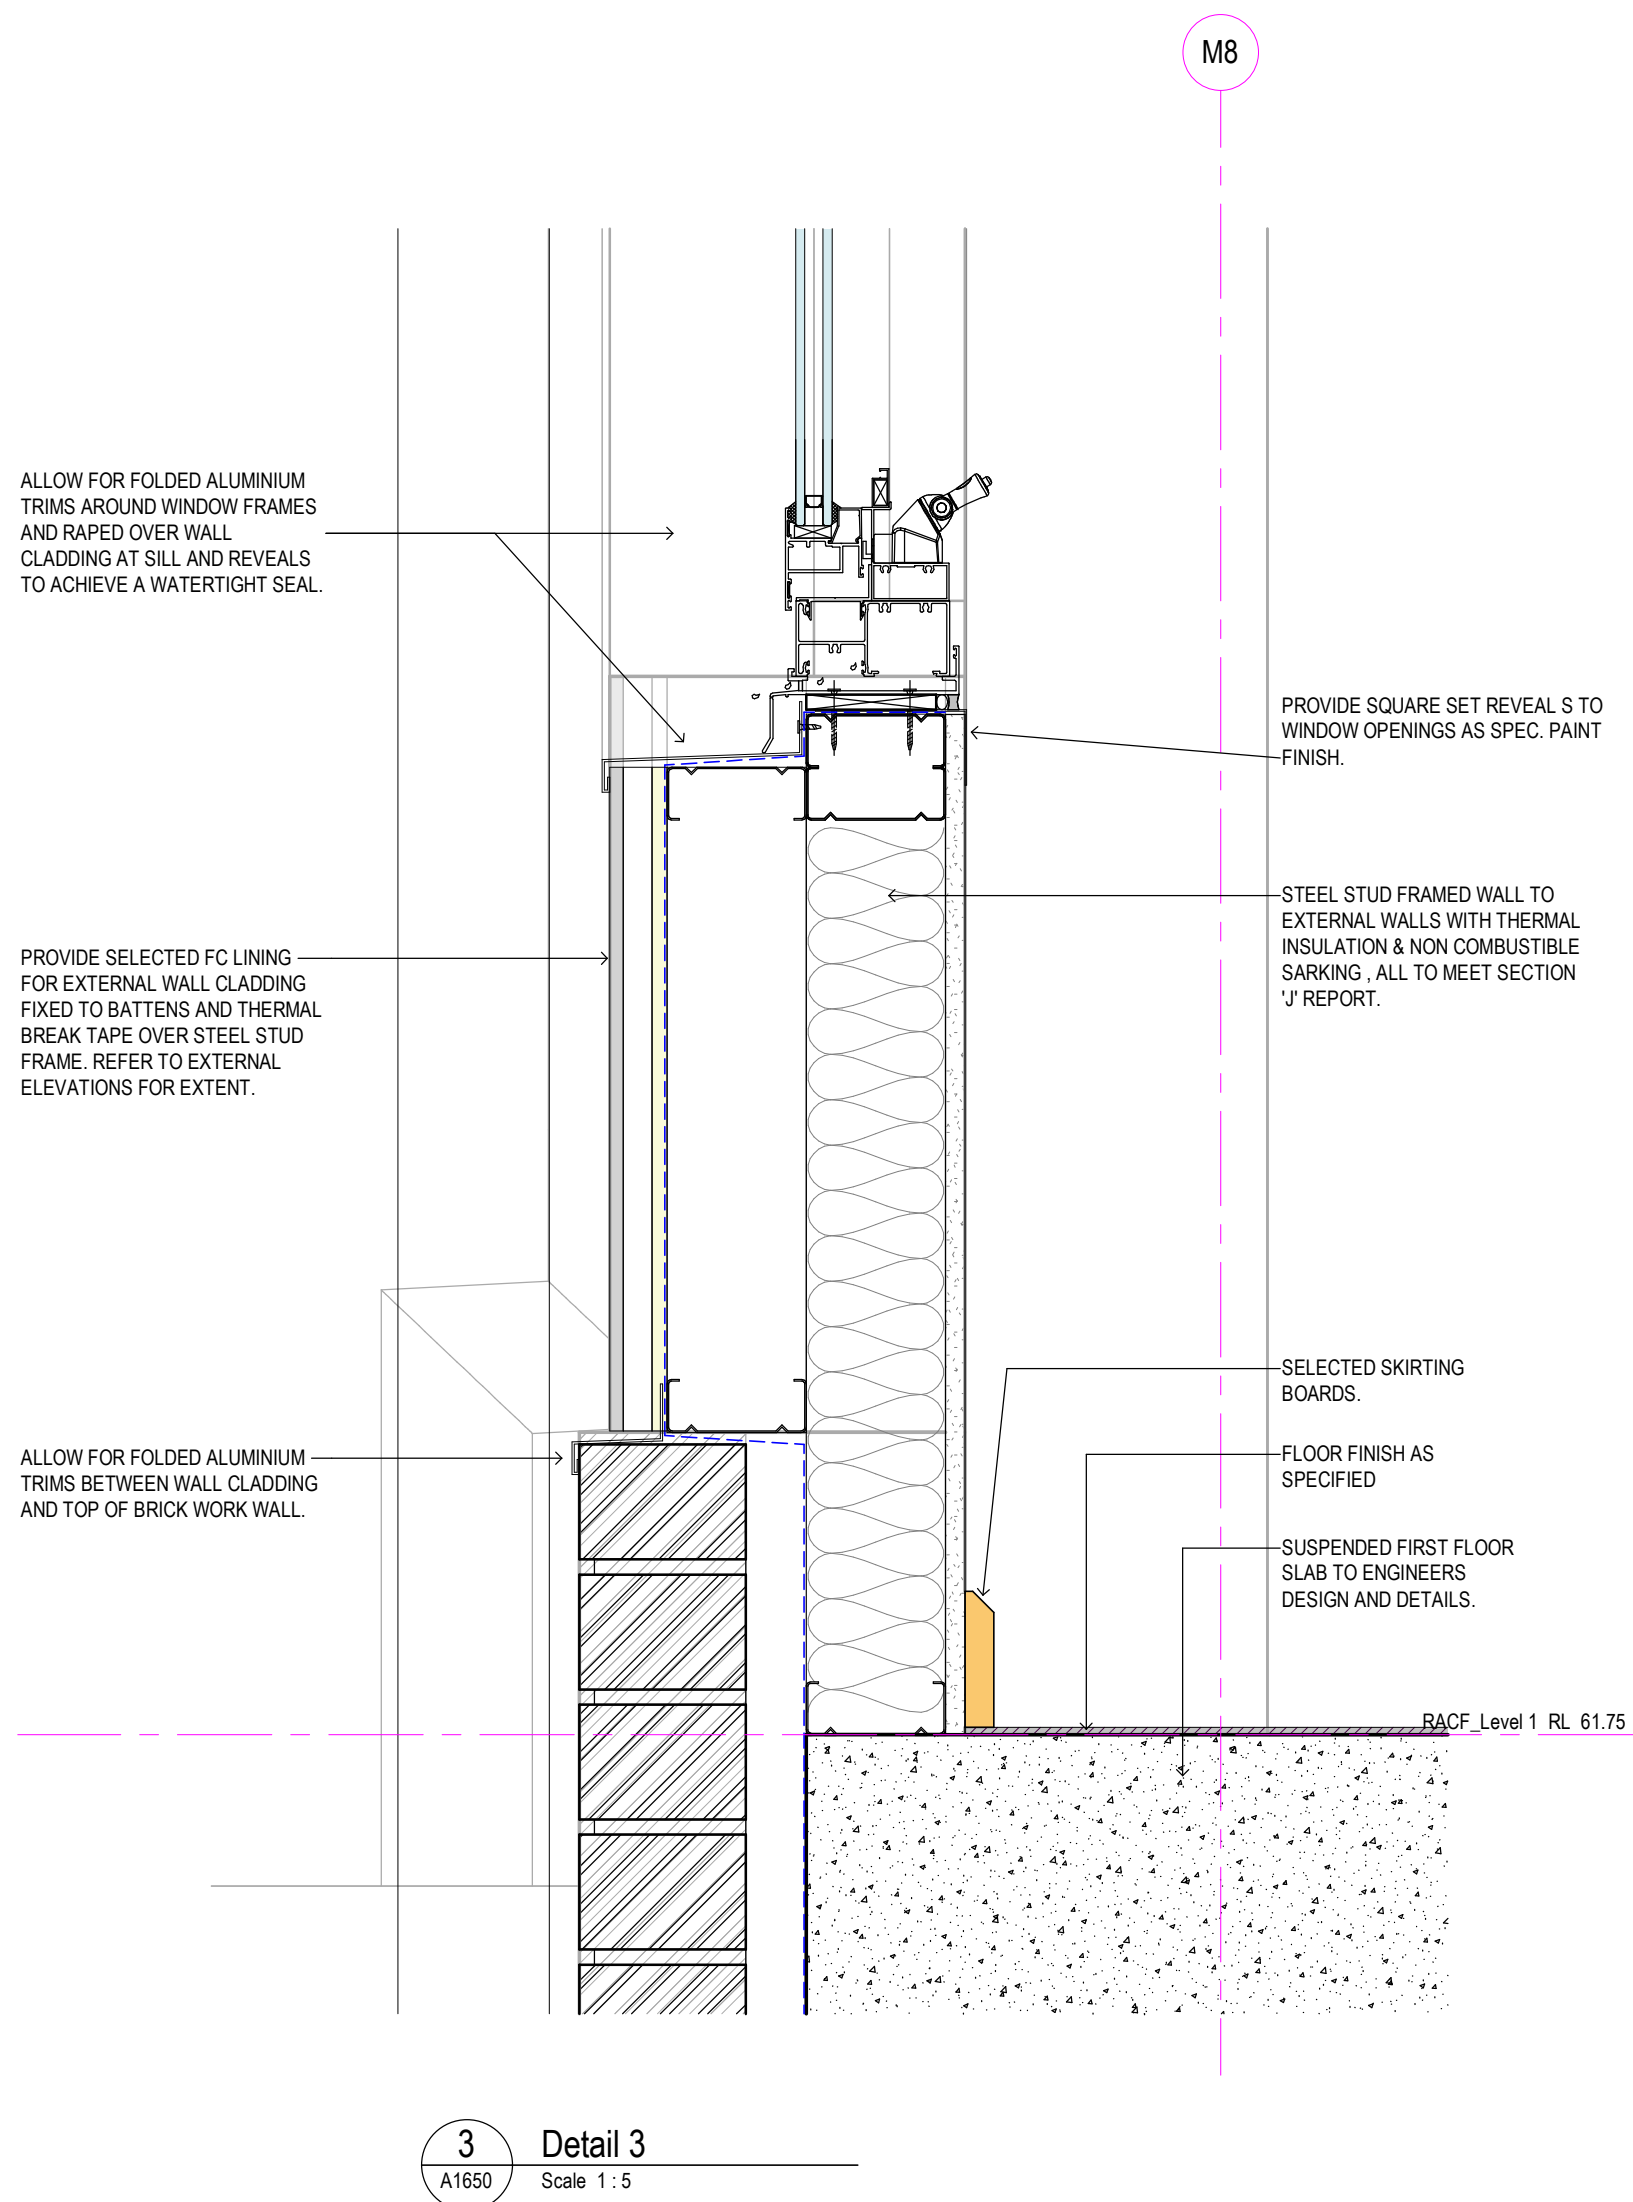


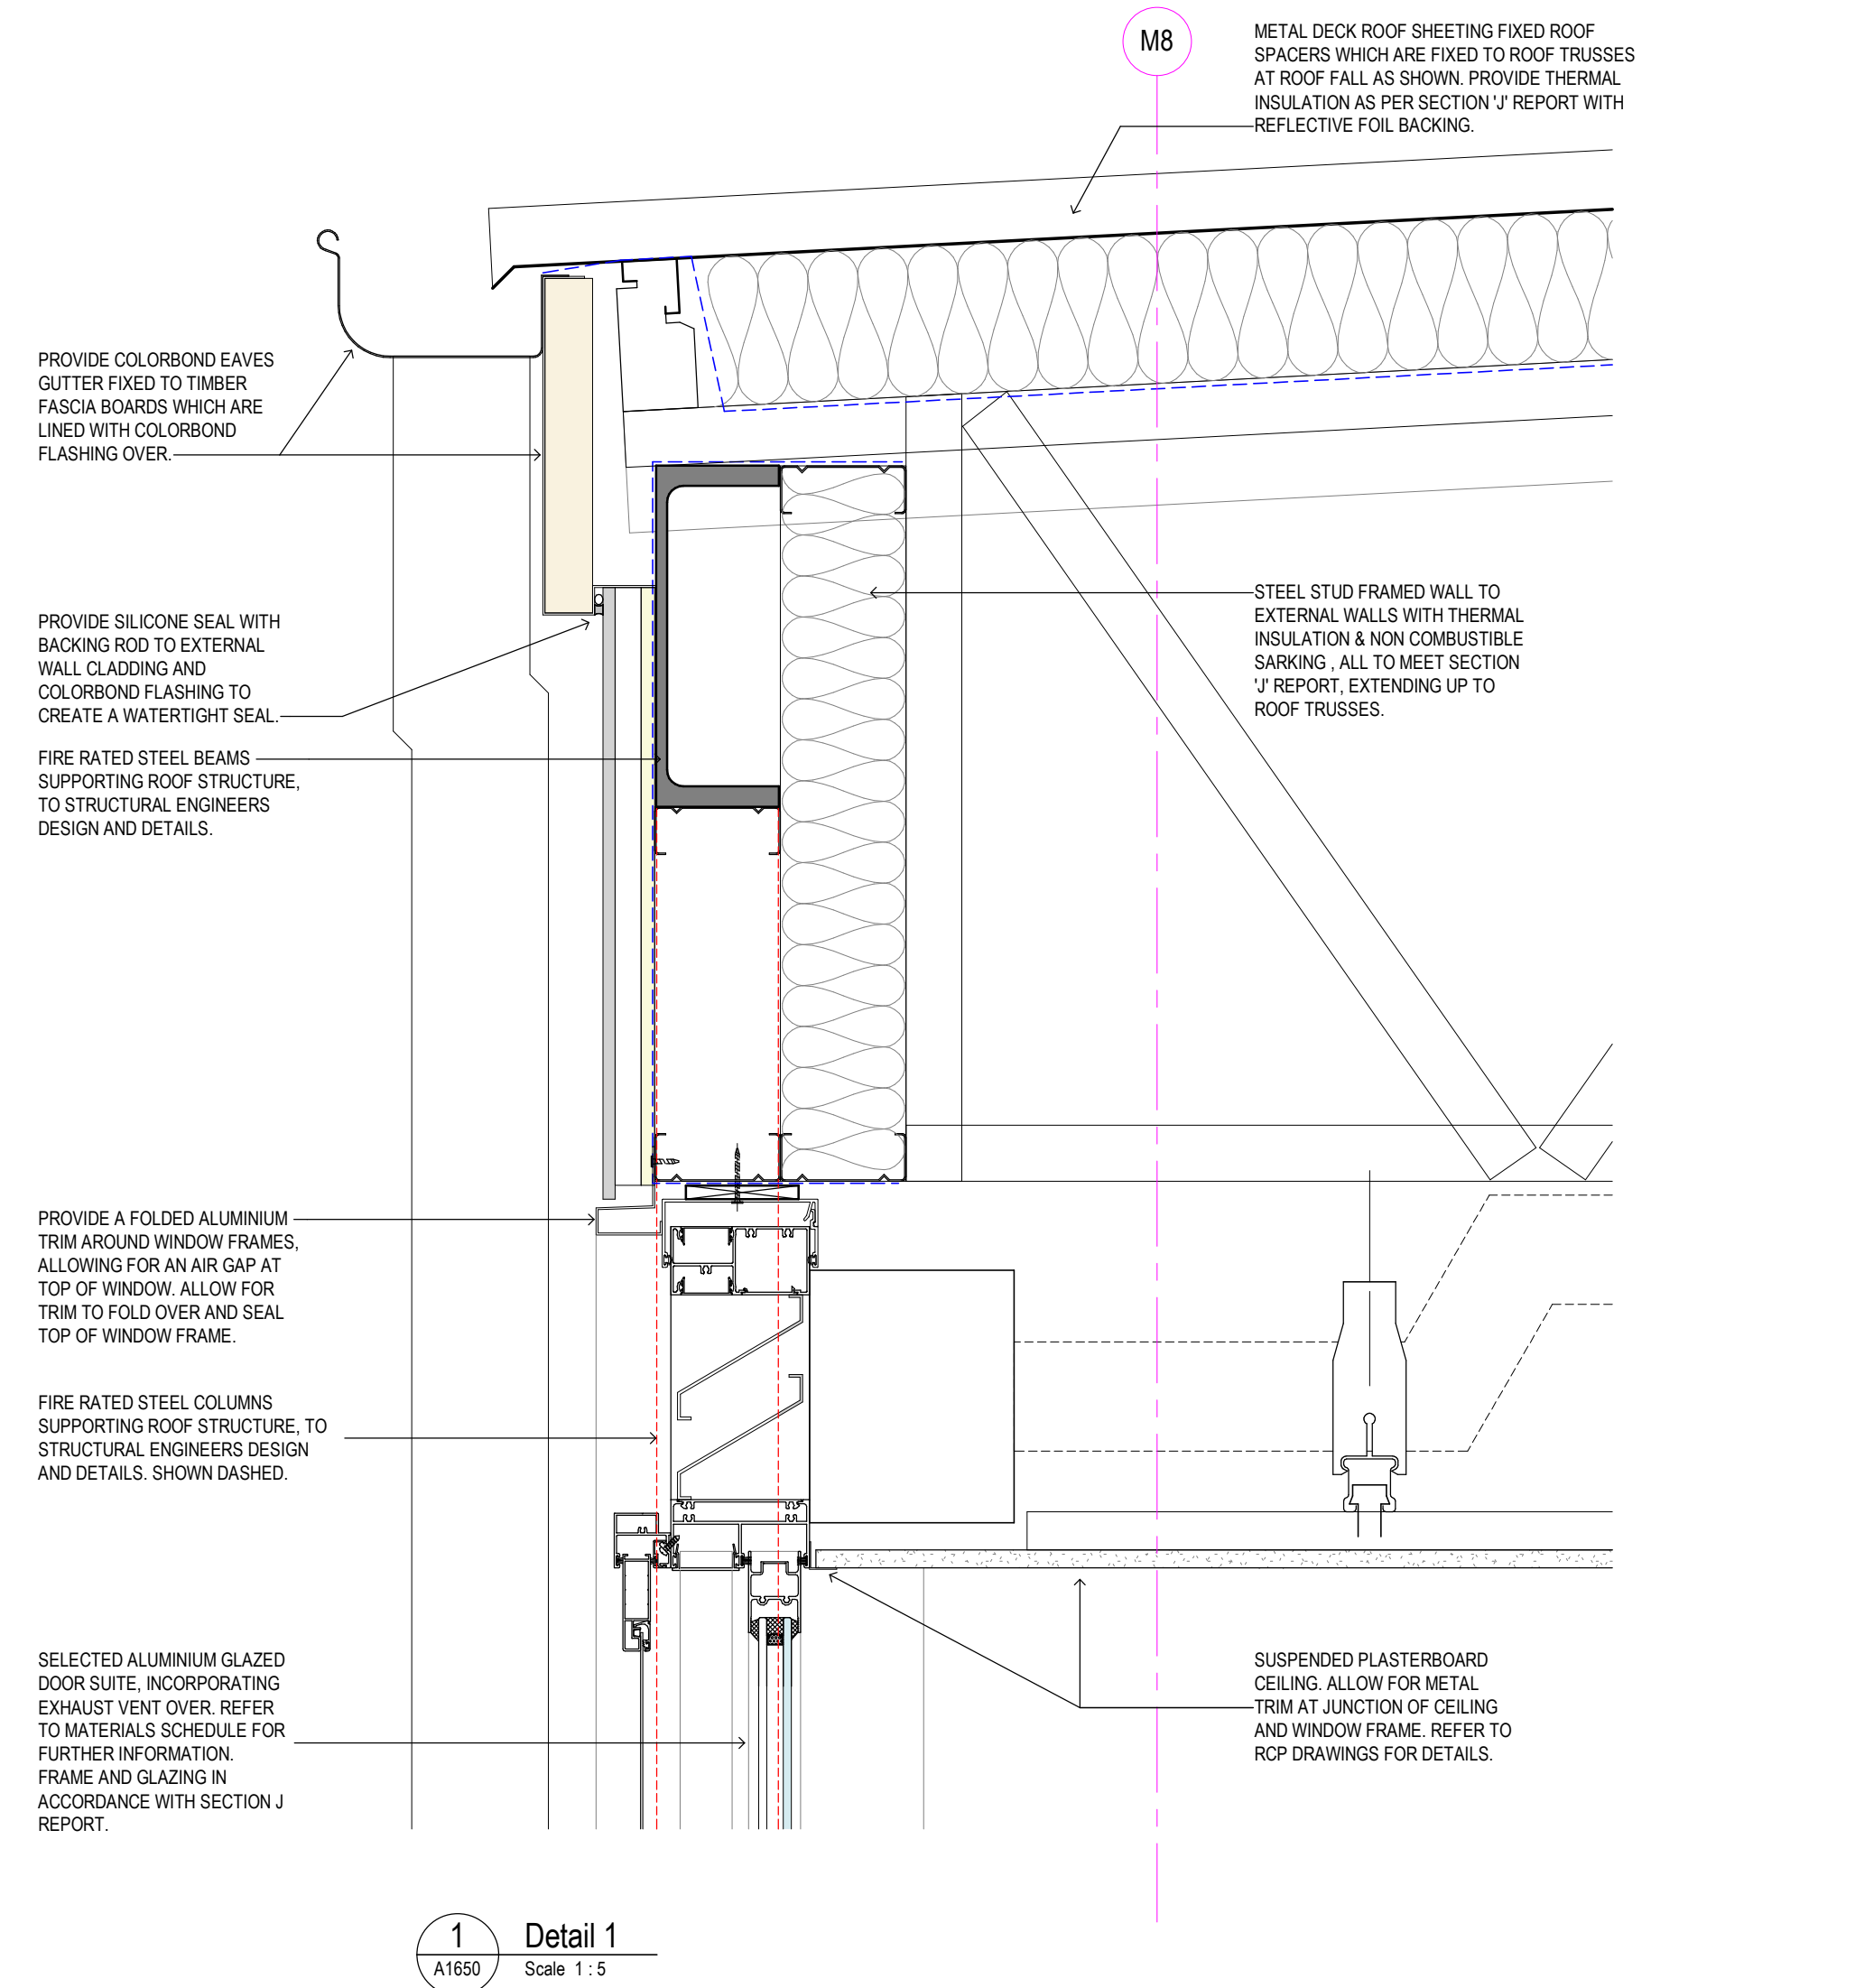

Revision/Issue	Date
P1 ISSUE FOR CONTRACT	2025.10.14
C1 ISSUE FOR CONSTRUCTION	2025.12.19

**Clarke
Hopkins
exhilo**

ClarkeHopkinsClarke
Melbourne | Wurundjeri
L9, Melbourne Connect
700 Swanston Street
Carlton VIC 3063
Telephone (03) 9419 4340
Email studio@chc.com.au
www.chc.com.au

Sydney | Gadigal Country
Suite 3, Ground Floor
91 Campbell Street
Surry Hills NSW 2010
Telephone (02) 9221 9200
Email studio@chc.com.au
www.chc.com.au

Scale	1 : 5 @ A1
Date	01/03/2024
Drawn	SG
Architect	EL

Project
Summerset Oakleigh
52 Golf Road, Oakleigh South, VIC

Drawing
Section Details - Sheet 1

Drawing No.
230185/A1700
C1

FOR CONSTRUCTION