




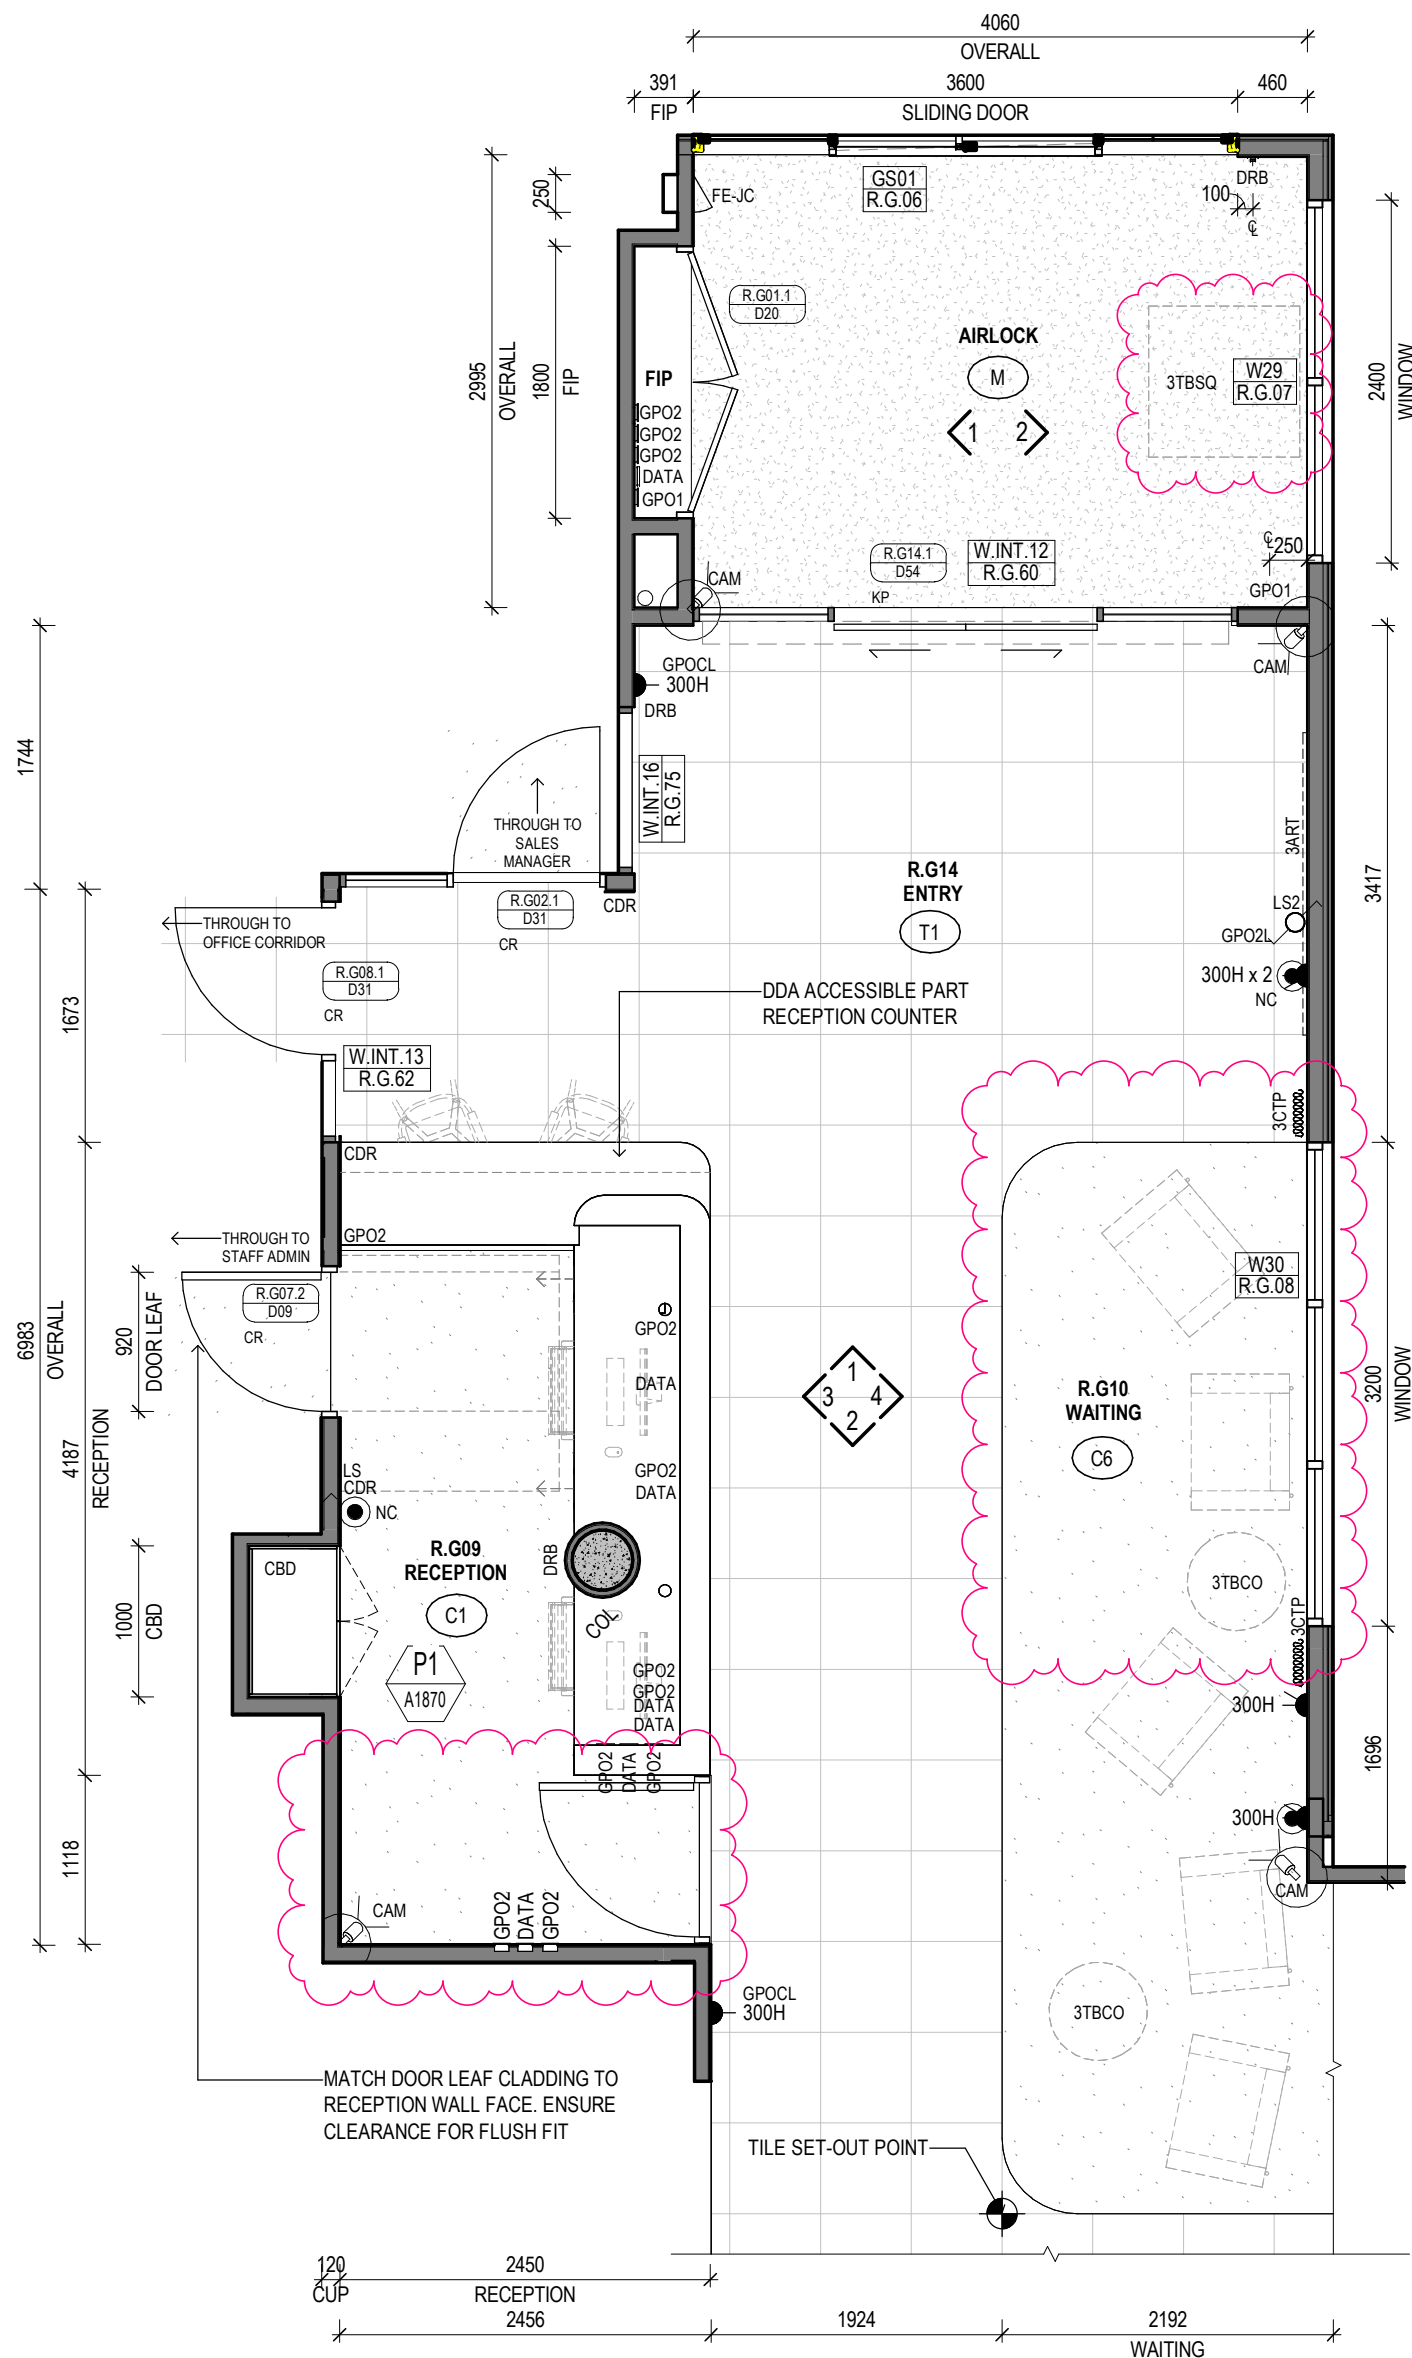


1 VILLAGE ARRIVALS - AIRLOCK, RECEPTION, LOBBY & WAITING
Scale 1: 50

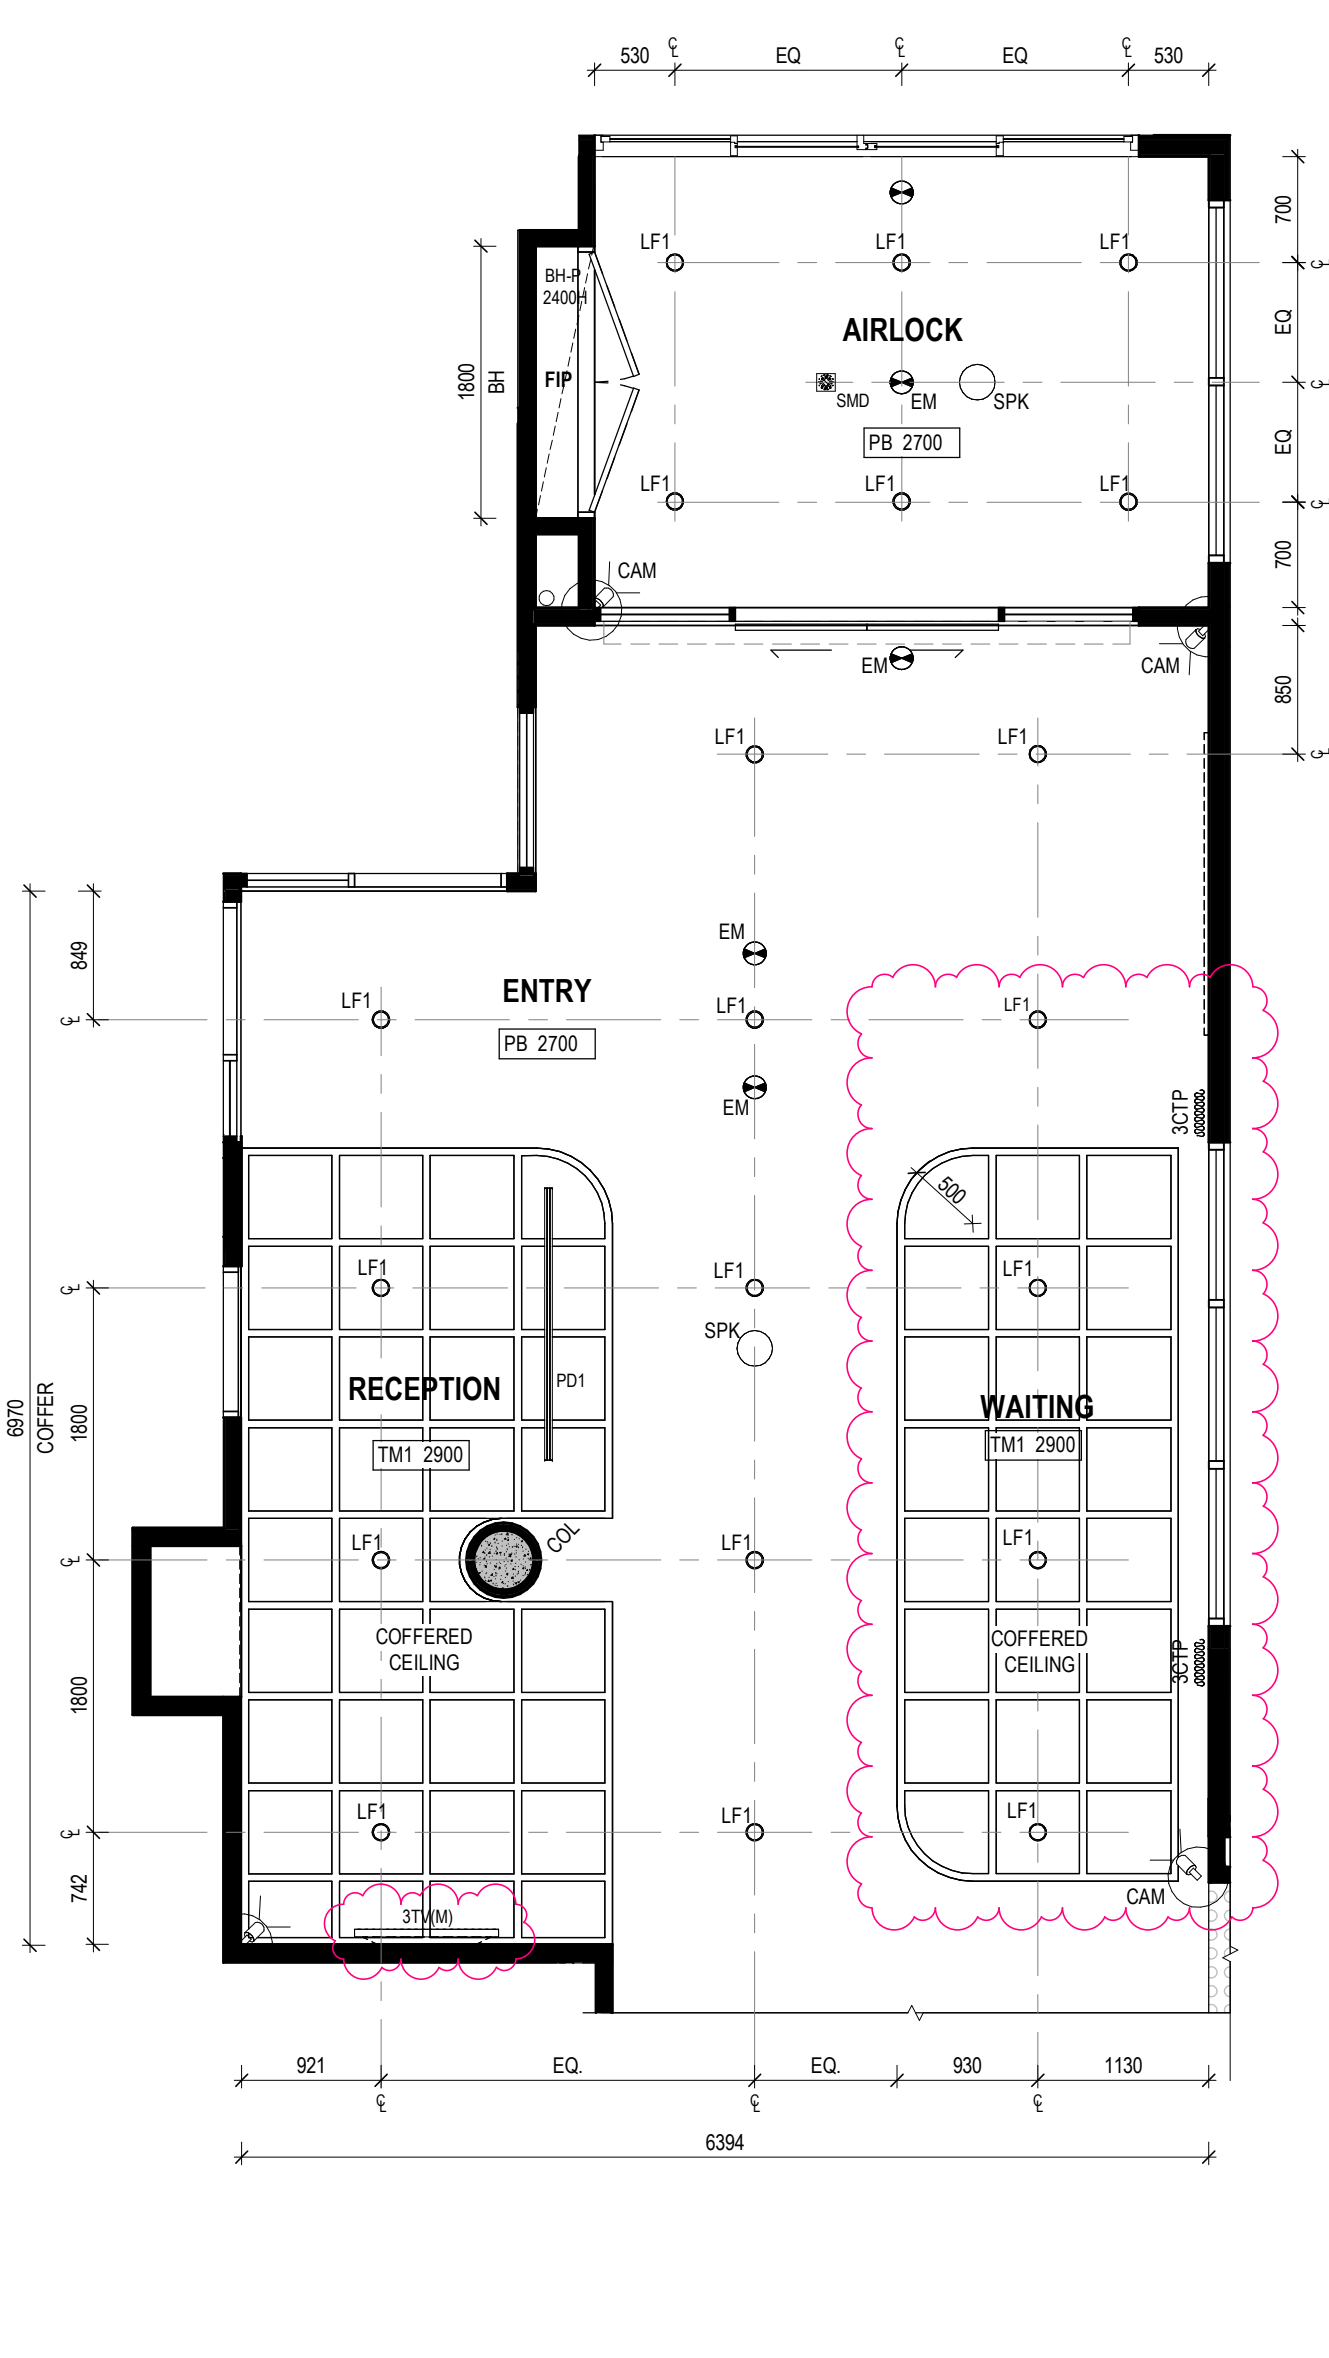


2 RCP - VILLAGE ARRIVALS - AIRLOCK, RECEPTION, LOBBY & WAITING
Scale 1: 50

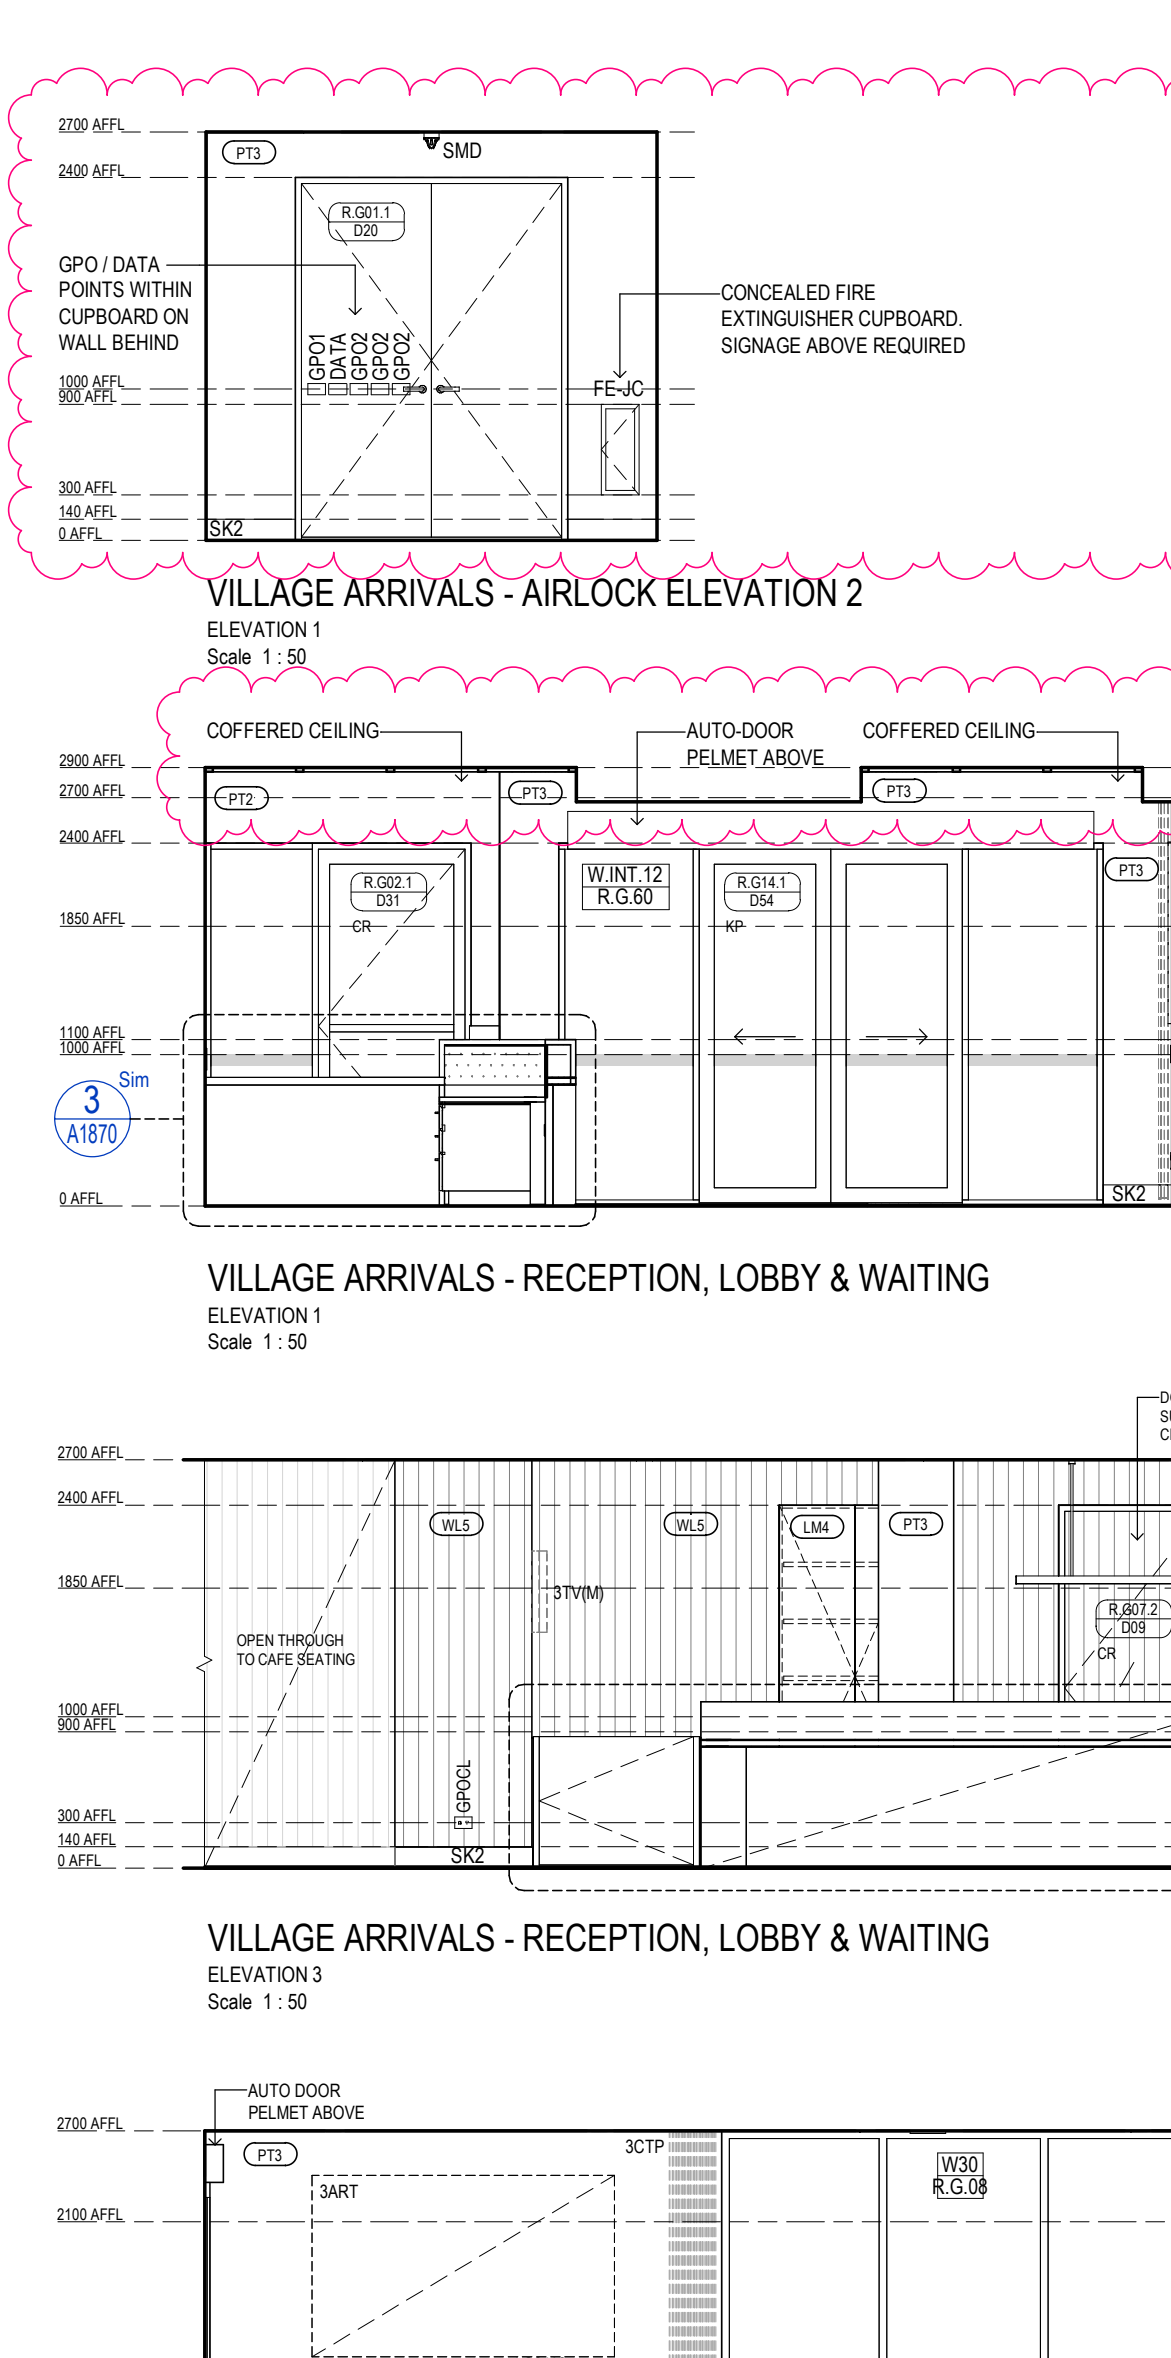


VILLAGE ARRIVALS - RECEPTION, LOBBY & WAITING
Scale 1: 50

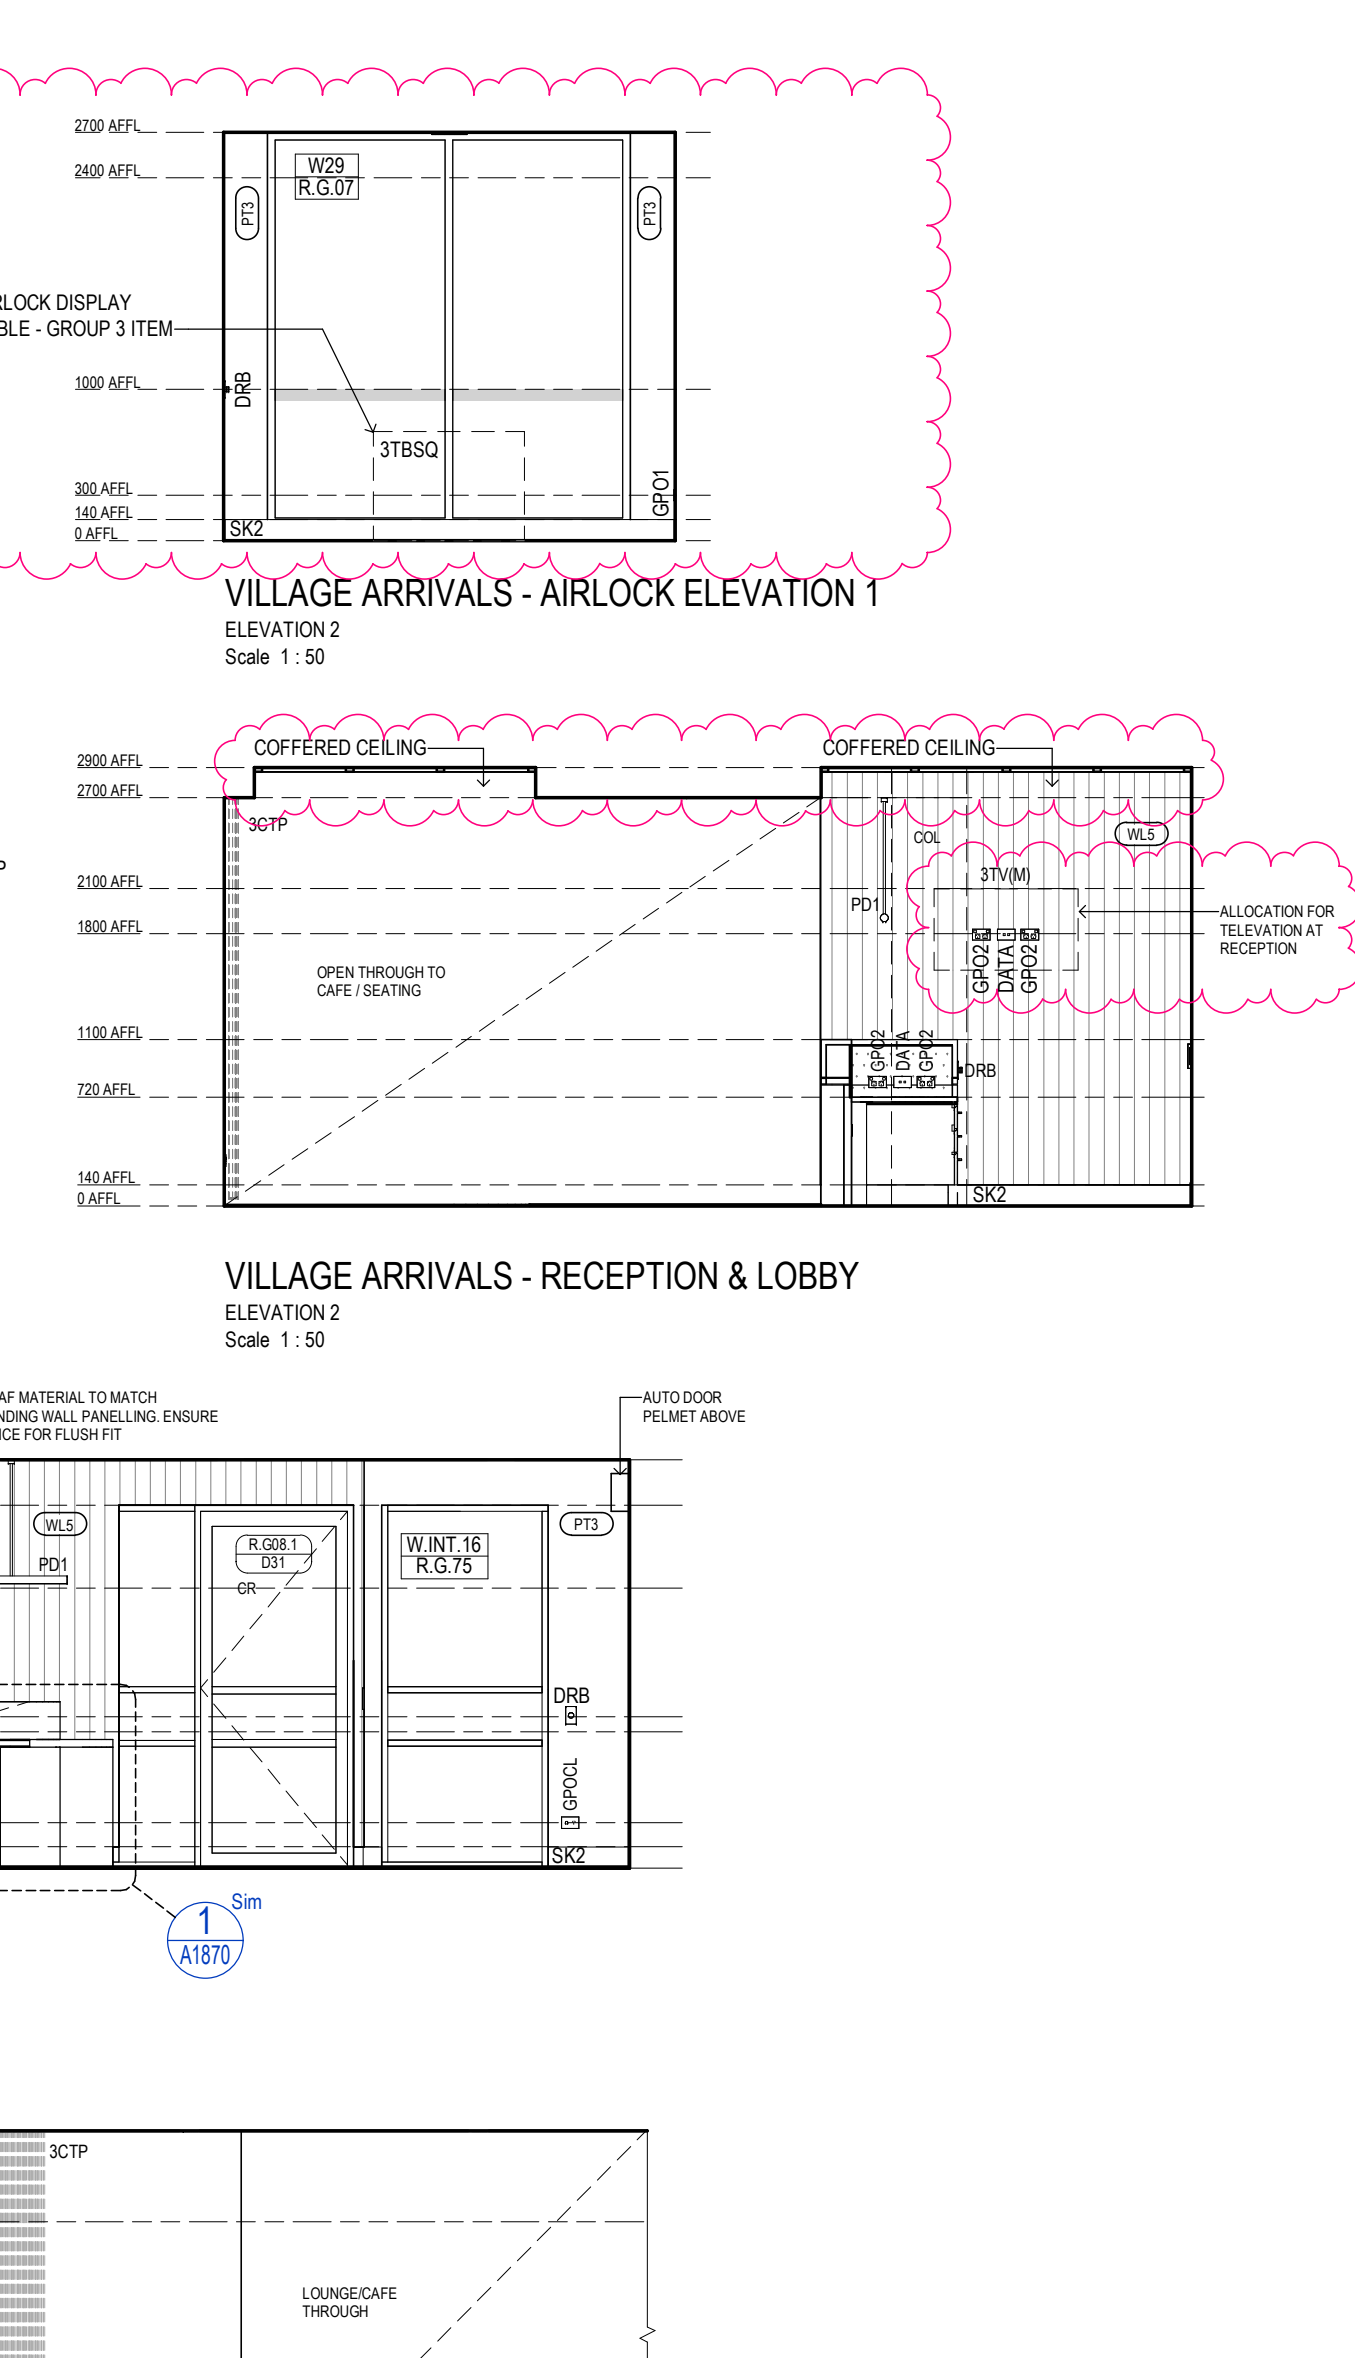


VILLAGE ARRIVALS - RECEPTION, LOBBY & WAITING
Scale 1: 50

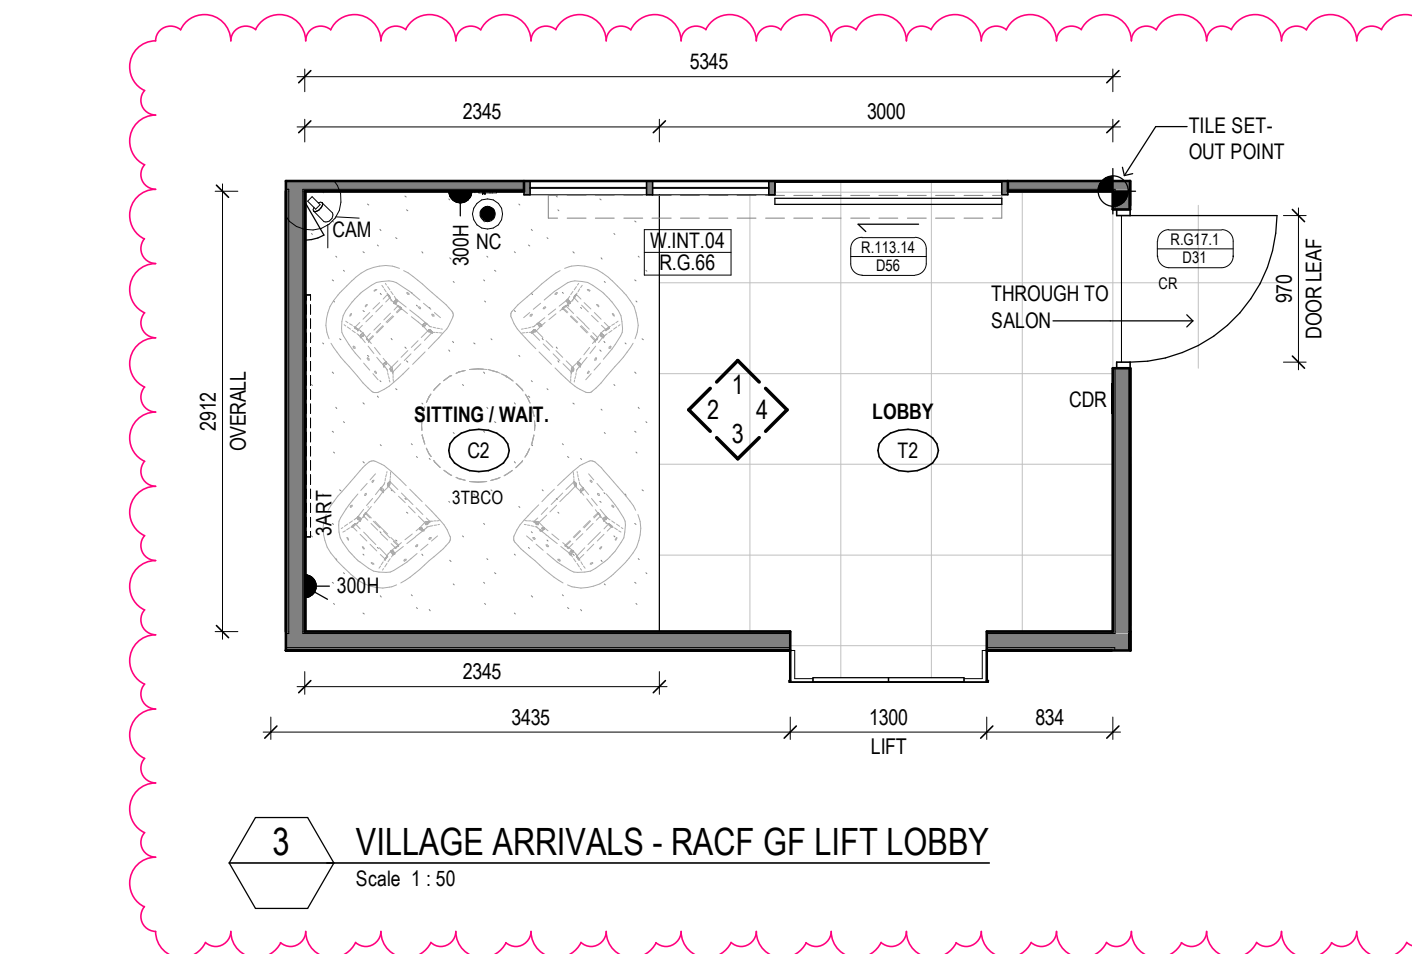


3 VILLAGE ARRIVALS - RACF GF LIFT LOBBY
Scale 1: 50

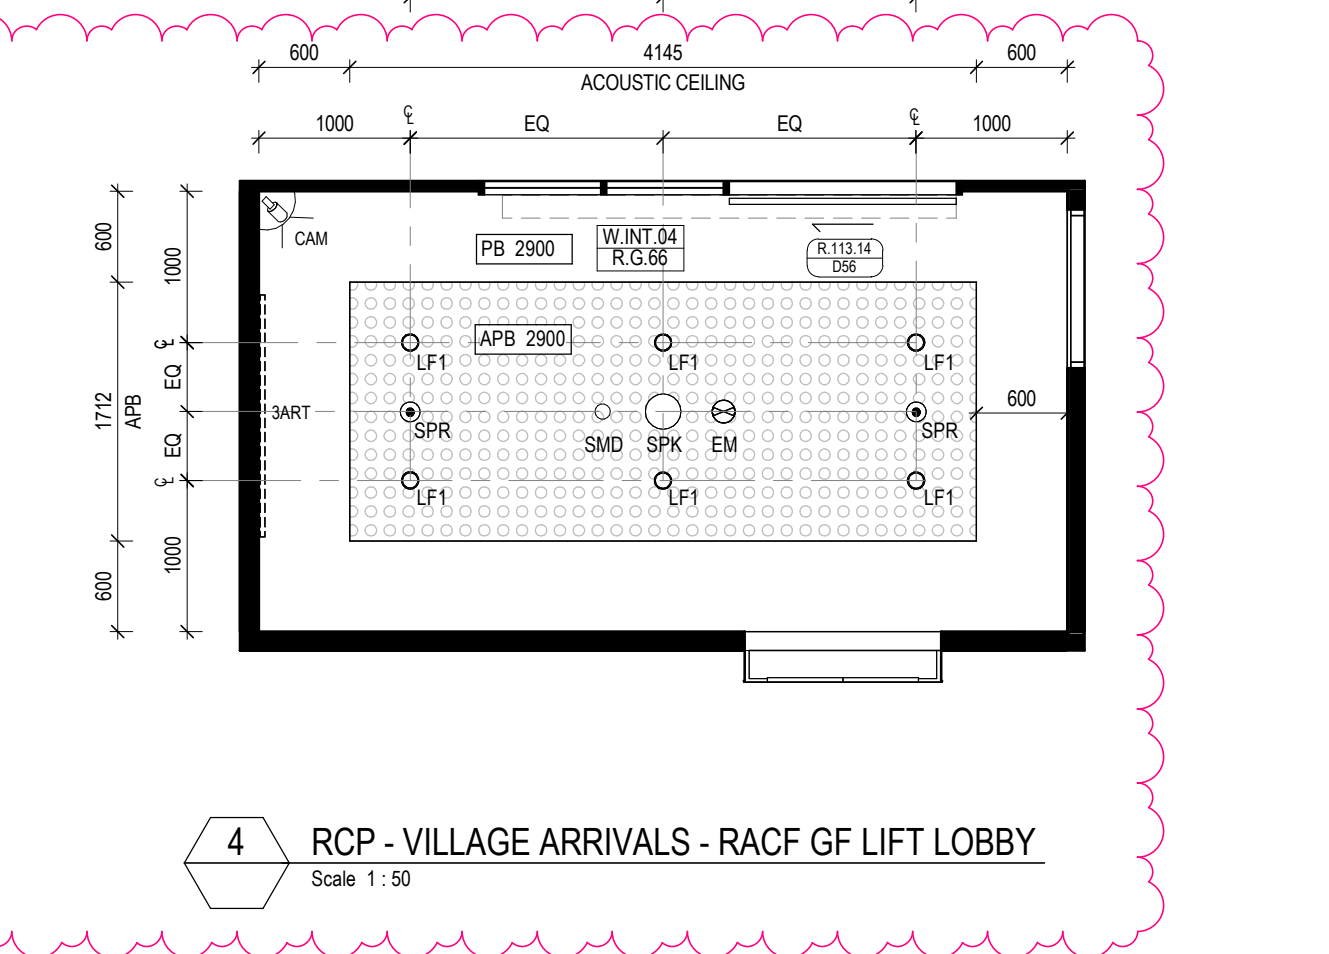

4 RCP - VILLAGE ARRIVALS - RACF GF LIFT LOBBY
Scale 1: 50

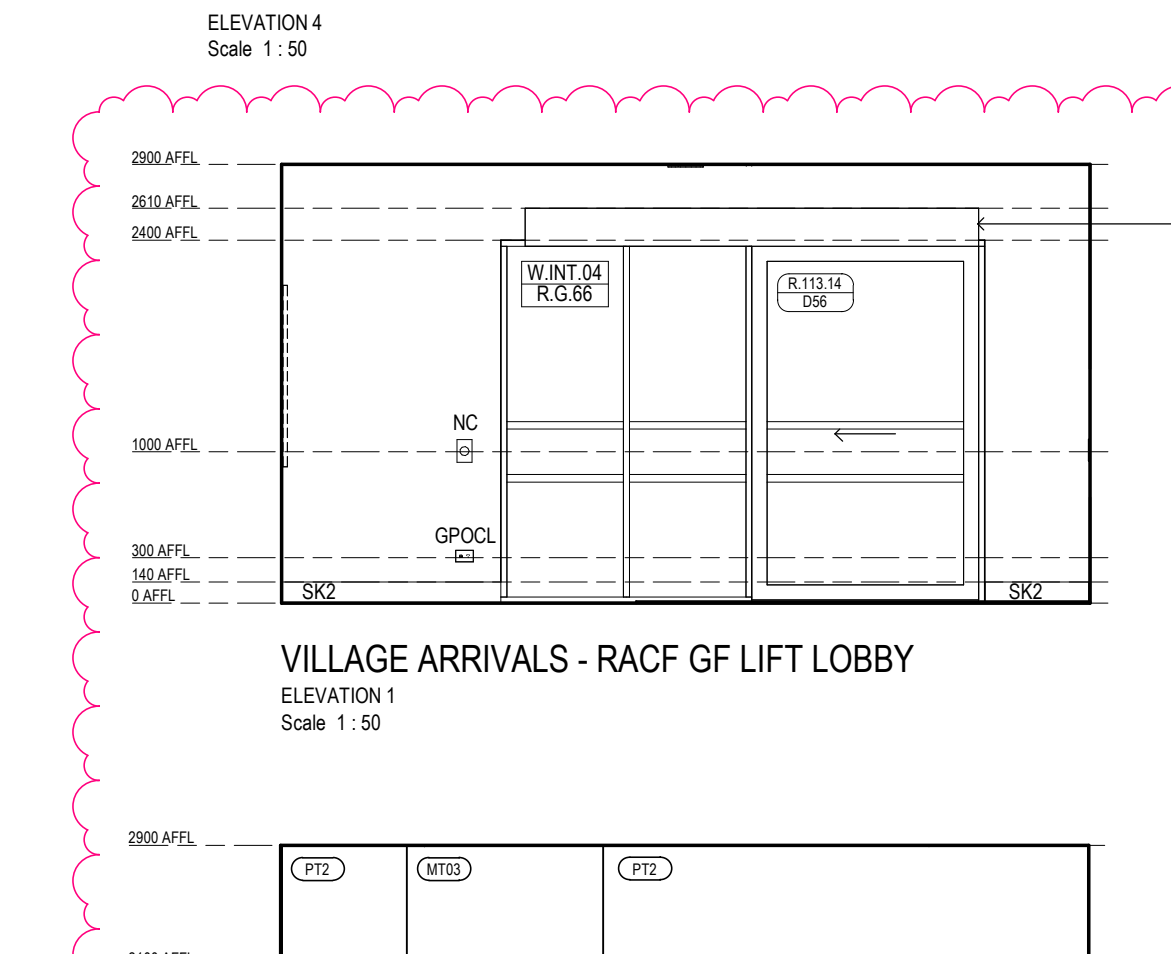

VILLAGE ARRIVALS - RACF GF LIFT LOBBY
Scale 1: 50

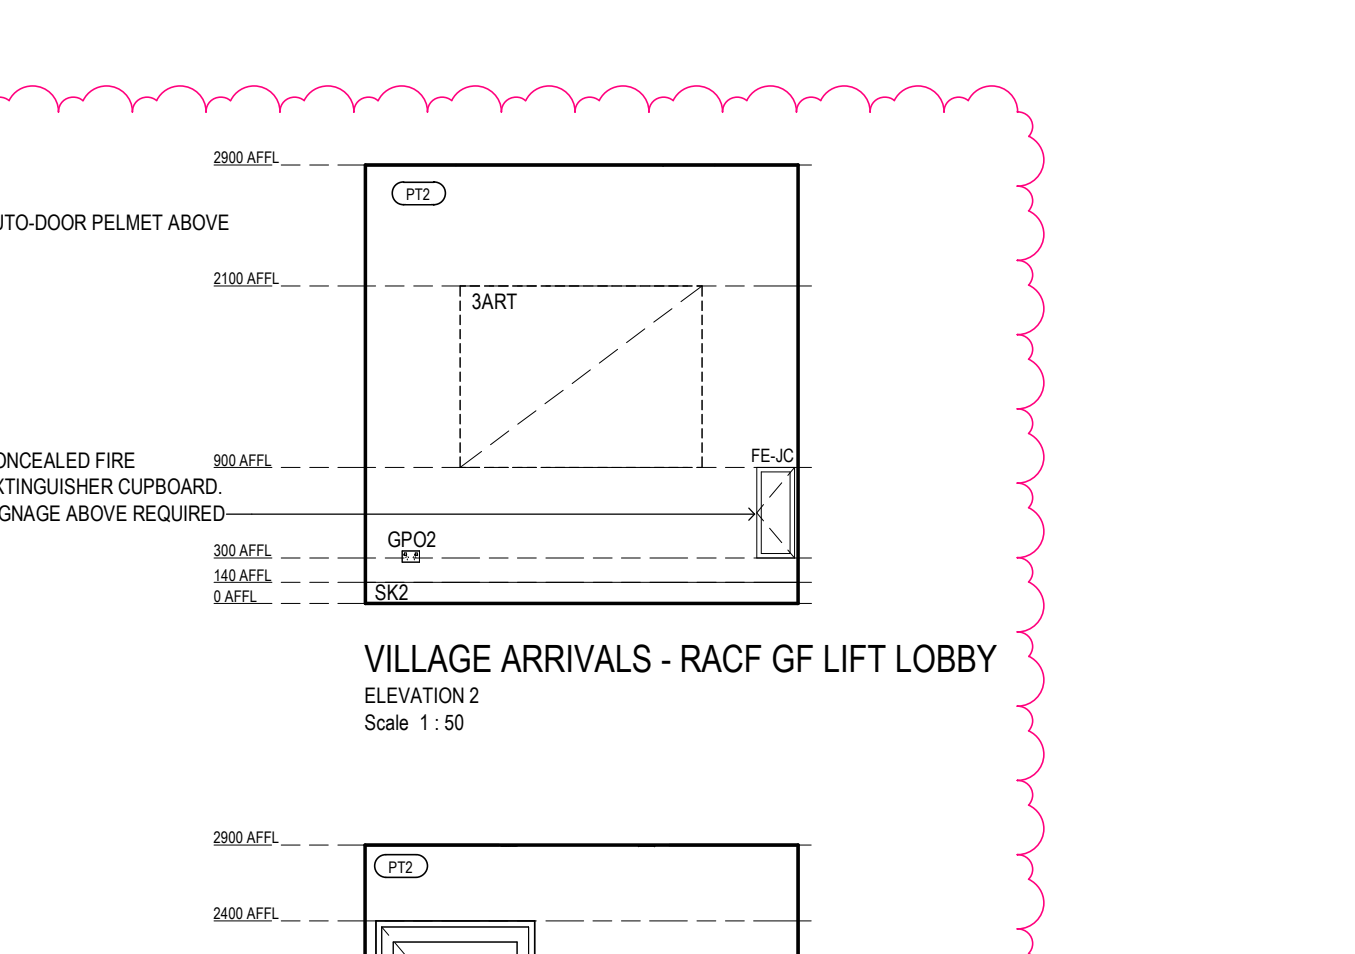

VILLAGE ARRIVALS - RACF GF LIFT LOBBY
Scale 1: 50

Legend - Internal Elevations

DRAWINGS TO BE READ IN CONJUNCTION WITH ARCHITECTURAL SPECIFICATION & MATERIALS, PRODUCTS & FINISHES SCHEDULE.
PT# PAINT FINISH TO ALL WALLS WITHIN NEW & AFFECTED ROOMS/ AREAS UNLESS OTHERWISE SHOWN

- CSE CONCRETE SEALER
- DPR DOOR PROTECTION
- GD GRAPHIC FILM
- LM LAMINATE
- MI MIRROR
- PBD PINBOARD
- PT PAINT FINISH
- REN RENDER FINISH
- SB SPLASHBACK
- ST STONE
- WB WHITEBOARD
- WP WALL PROTECTION
- WT WALL TILE
- WV WALL VINYL

NOTES:
1. LAMINATE CARCASS FOR ALL VISIBLE OPEN SHELVING, UNLESS OTHERWISE NOTED
2. MELAMINETO ALL INTERNAL CARCASS OF JOINERY, UNLESS OTHERWISE NOTED.

Legend - Floor Finishes

- C CARPET
- CO CONCRETE
- E EPOXY FINISH
- L LINOLEUM
- M MATTING
- PU PAVING UNIT - TBC WITH LANDSCAPE
- R RUBBER FLOORING
- T TILING
- TF TIMBER FLOORING
- V VINYL
- LVT LUXURY VINYL TILE PLANK

- PROTECTION RAILS OR CRASH RAILS - REFER TO MATERIAL SCHEDULE FOR DETAILS
- WL1 - REFER TO MATERIAL SCHEDULE FOR DETAILS
- WL2 - REFER TO MATERIAL SCHEDULE FOR DETAILS


NOTE:
FALLS TO ALL FLOOR WASTES IN ACCORDANCE WITH AS 3740.

Keynote Legend

- 3ART ARTWORK - GROUP 3
- 3CTP CURTAINS - GROUP 3
- 3TBCO COFFEE TABLE - GROUP 3
- 3TBSQ SQUARE TABLE - GROUP 3
- 3TV(M) TELEVISION SCREEN 55 INCH - GROUP 3
- 3H4P BULKHEAD - PLASTERBOARD TYPE
- CCTV CAMERA
- CUPBOARD
- CDR CARD READER
- COL COLUMN
- DATA DATA OUTLET
- DRB DOOR RELEASE BUTTON
- EM EMERGENCY LIGHT
- FE-JC FIRE EXTINGUISHER IN JOINERY CUPBOARD
- GP01 POWER OUTLET - SINGLE
- GP02 POWER OUTLET - DOUBLE
- GP02L POWER OUTLET - DOUBLE - LARGE PLATE
- GP0CL POWER OUTLET - CLEANERS
- LF1 LIGHT FITTING - REFER TO ELECTRICAL ENGINEER SPECIFICATION
- LS LIGHT SWITCH
- LS2 LIGHT SWITCH - TWO WAY
- NC NURSE CALL
- PD1 PENDANT LIGHT - TYPE 1
- SK2 SKIRTING - TYPE 2
- SMD SMOKE DETECTOR
- SPK ANUNCIATOR
- SPR SPRINKLER

FOR CONSTRUCTION

Revision/Issue	Date
a Issued for Coordination - 100% DD	2024.04.12
P1 Consolidated Set-to-date / SMG Comments	2025.08.15
P2 Tender Pack Issue	2025.09.05
P3 ISSUE FOR CONTRACT	2025.10.10
G1 ISSUE FOR CONSTRUCTION - INTERIORS	2026.03.26

 

ClarkeHopkinsClarke
Melbourne | Wurundjeri
L3, Melbourne Connect
700 Swanston Street
Carlton VIC 3063
Telephone (03) 9419 4340
Email studio@chc.com.au
www.chc.com.au

Sydney | Gadigal Country
Suite 3, Ground Floor
91 Campbell Street
Sunny Hills NSW 2010
Telephone (02) 9221 9200
Email studio@chc.com.au
www.chc.com.au

Scale	1: 50 @ A1
Date	01/03/2024
Drawn	NS / DP
Architect	EL

Project
Summerset Oakleigh
52 Golf Road, Oakleigh South, VIC

Drawing
Internal Elevations - Village Arrivals -
Airlock, Lobby & Reception

Drawing No.
230185/A1801
C1