



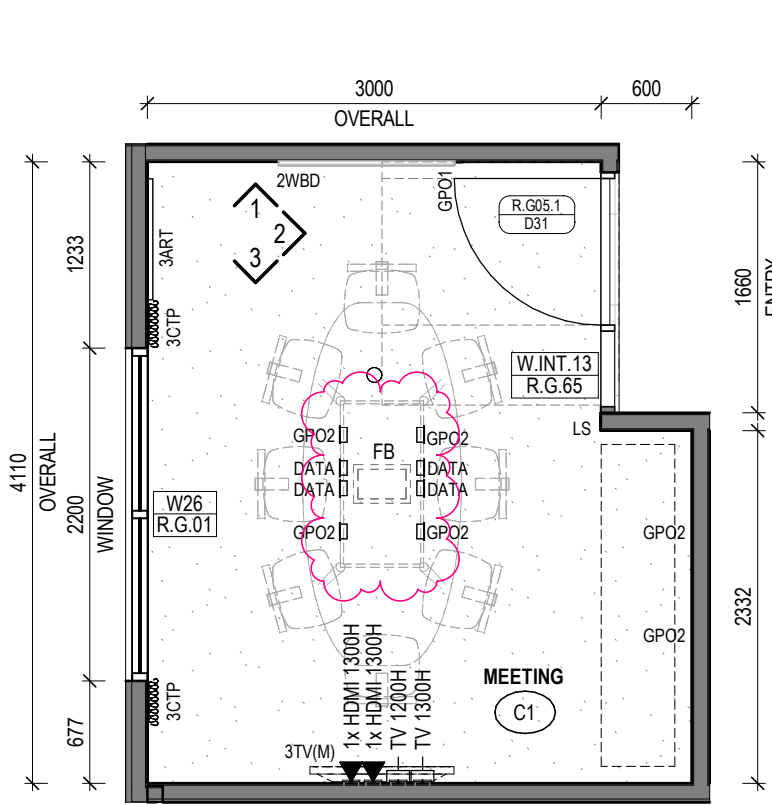

1 VILLAGE ADMIN - MEETING
Scale 1 : 50

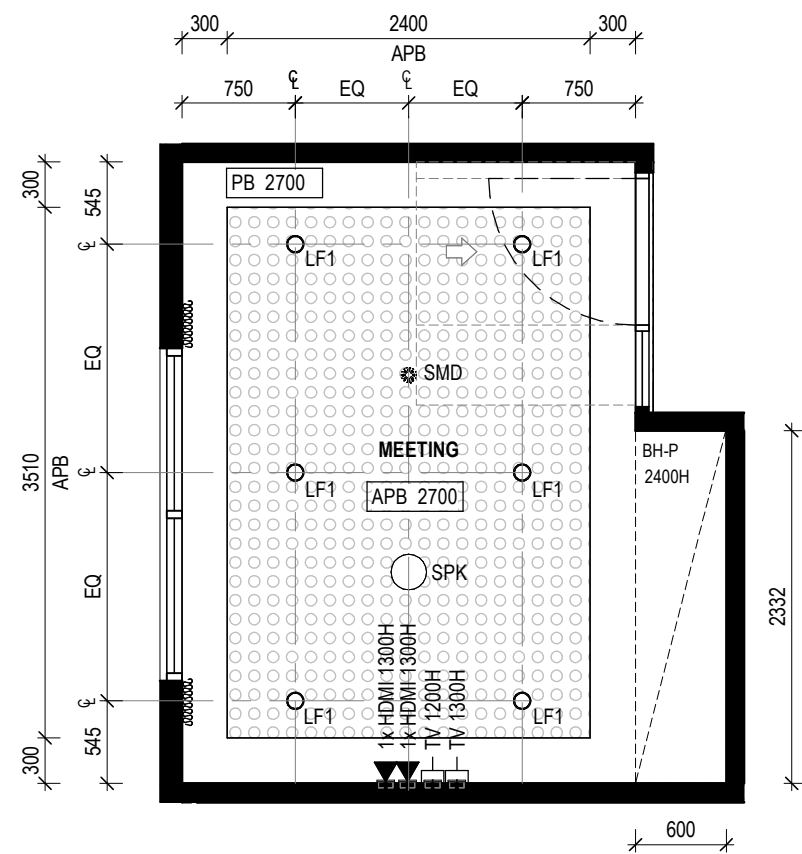


2 RCP - VILLAGE ADMIN - MEETING
Scale 1 : 50


VILLAGE ADMIN - MEETING
ELEVATION 1
Scale 1 : 50

VILLAGE ADMIN - MEETING
ELEVATION 2
Scale 1 : 50

VILLAGE ADMIN - MEETING
ELEVATION 3
Scale 1 : 50

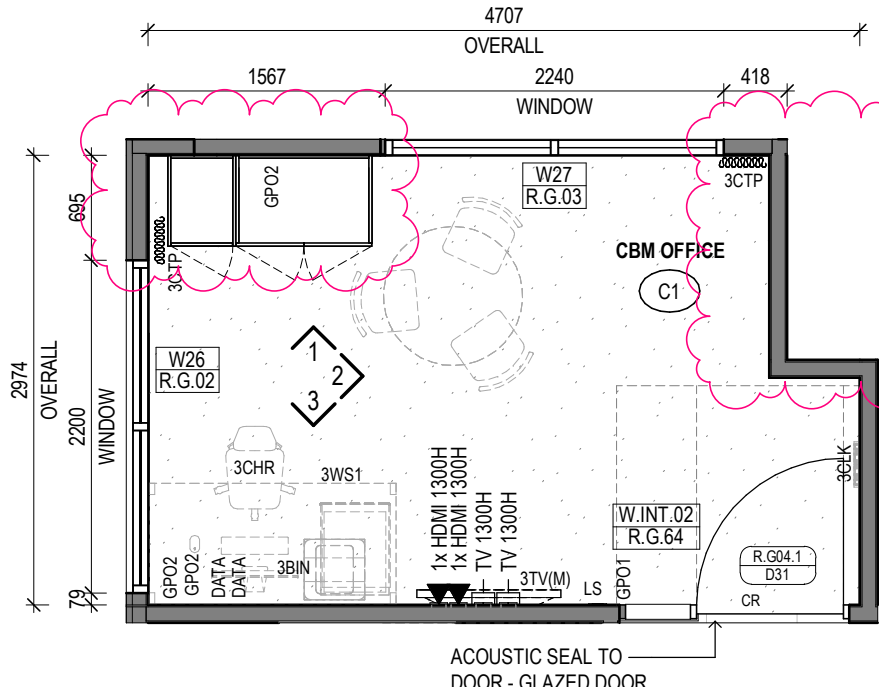

3 VILLAGE ADMIN - CBM OFFICE
Scale 1 : 50

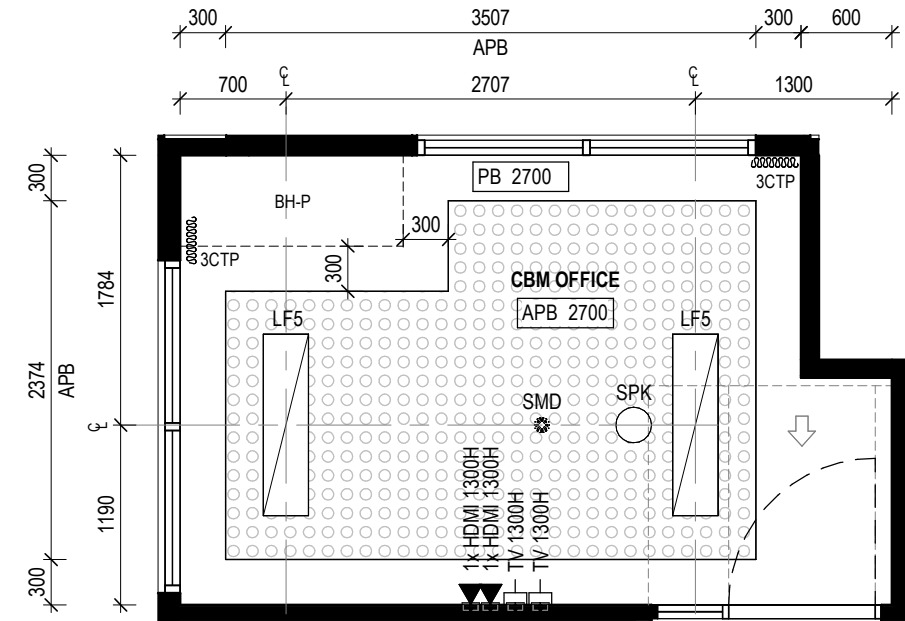


4 RCP - VILLAGE ADMIN - CBM OFFICE
Scale 1 : 50


VILLAGE ADMIN - CBM OFFICE
ELEVATION 1
Scale 1 : 50

VILLAGE ADMIN - CBM OFFICE
ELEVATION 2
Scale 1 : 50

VILLAGE ADMIN - CBM OFFICE
ELEVATION 3
Scale 1 : 50

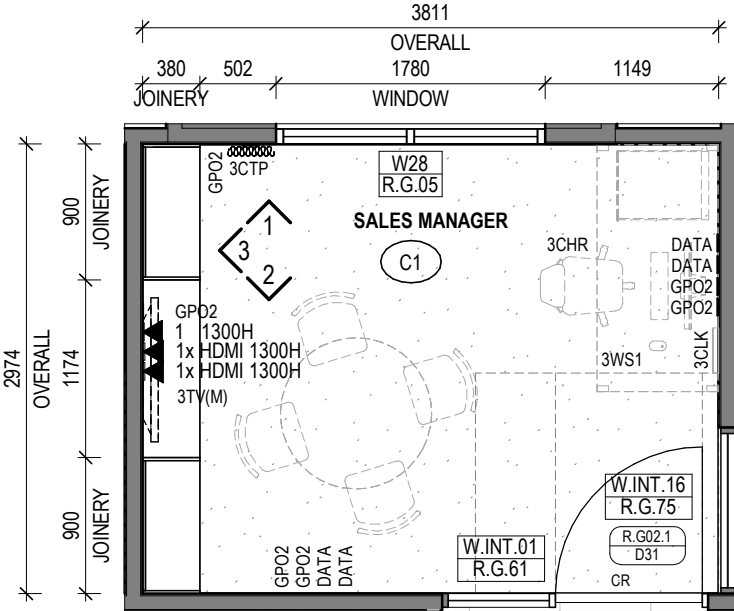

5 VILLAGE ADMIN - SALES MANAGER
Scale 1 : 50

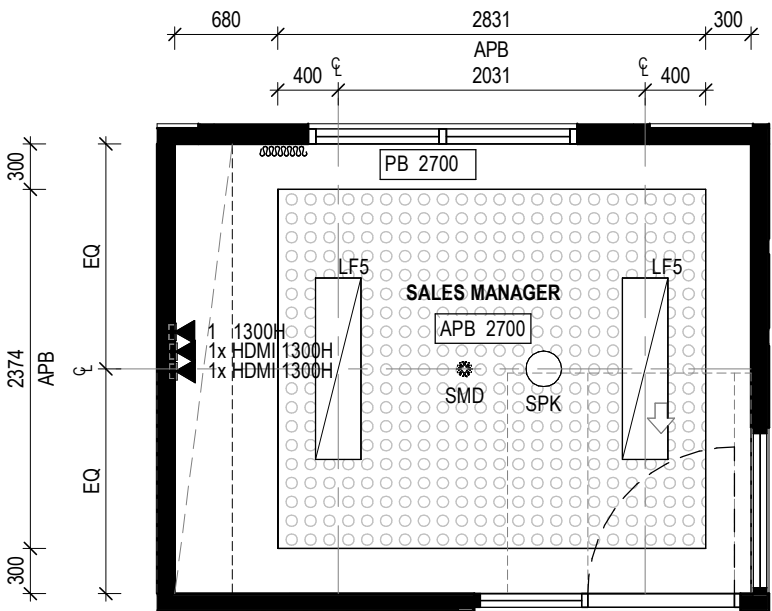


6 RCP - VILLAGE ADMIN - SALES MANAGER
Scale 1 : 50


VILLAGE ADMIN - SALES MANAGER
ELEVATION 1
Scale 1 : 50

VILLAGE ADMIN - SALES MANAGER
ELEVATION 2
Scale 1 : 50

VILLAGE ADMIN - SALES MANAGER
ELEVATION 3
Scale 1 : 50

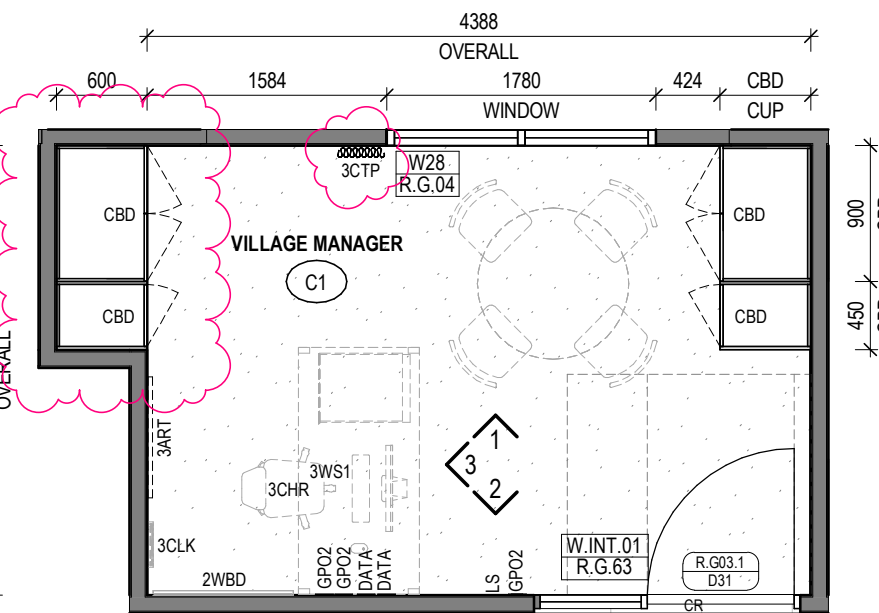

7 VILLAGE ADMIN - VILLAGE MANAGER
Scale 1 : 50

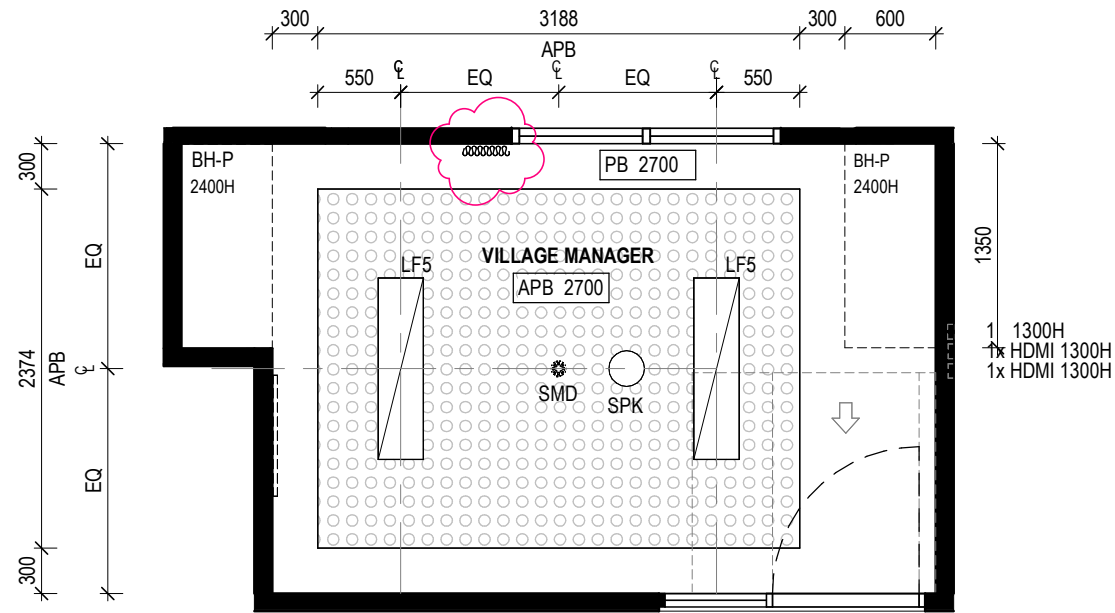

8 RCP - VILLAGE ADMIN - VILLAGE MANAGER
Scale 1 : 50

VILLAGE ADMIN - VILLAGE MANAGER
ELEVATION 1
Scale 1 : 50

VILLAGE ADMIN - VILLAGE MANAGER
ELEVATION 2
Scale 1 : 50

VILLAGE ADMIN - VILLAGE MANAGER
ELEVATION 3
Scale 1 : 50

Legend - Internal Elevations

DRAWINGS TO BE READ IN CONJUNCTION WITH ARCHITECTURAL SPECIFICATION & MATERIALS, PRODUCTS & FINISHES SCHEDULE.

PT# PAINT FINISH TO ALL WALLS WITHIN NEW & AFFECTED ROOMS/ AREAS UNLESS OTHERWISE SHOWN

- CSE CONCRETE SEALER
- DPR DOOR PROTECTION
- GD GRAPHIC FILM
- LM LAMINATE
- MI MIRROR
- PBD PINBOARD
- PT PAINT FINISH
- REN RENDER FINISH
- SB SPLASHBACK
- ST STONE
- WB WHITEBOARD
- WP WALL PROTECTION
- WT WALL TILE
- WV WALL VINYL

NOTES:
1. LAMINATE CARCASS FOR ALL VISIBLE OPEN SHELVING, UNLESS OTHERWISE NOTED
2. MELAMINETO ALL INTERNAL CARCASS OF JOINERY, UNLESS OTHERWISE NOTED.

Legend - Floor Finishes

- C CARPET
- CO CONCRETE
- E EPOXY FINISH
- L LINOLEUM
- M MATTING
- PU PAVING UNIT - TBC WITH LANDSCAPE
- R RUBBER FLOORING
- T TILING
- TF TIMBER FLOORING
- V VINYL
- LVT LUXURY VINYL TILE PLANK

- PROTECTION RAILS OR CRASH RAILS - REFER TO MATERIAL SCHEDULE FOR DETAILS
- WL1 - REFER TO MATERIAL SCHEDULE FOR DETAILS
- WL2 - REFER TO MATERIAL SCHEDULE FOR DETAILS

NOTE:
FALLS TO ALL FLOOR WASTES IN ACCORDANCE WITH AS 3740.

Keynote Legend

- 2WBDO WHITEBOARD - GROUP 2
- 3ART ARTWORK - GROUP 3
- 3BIN WASTE BIN - GROUP 3
- 3CHR ARM CHAIR - GROUP 3
- 3CLK CLOCK - GROUP 3
- 3CTP CURTAINS - GROUP 3
- 3TV(M) TELEVISION SCREEN 55 INCH - GROUP 3
- 3WS1 WORK STATION - GROUP 3
- BH-P BULKHEAD - PLASTERBOARD TYPE
- CBD CURBBOARD
- DATA DATA OUTLET
- FB FLOOR BOX
- GPO1 POWER OUTLET - SINGLE
- GPO2 POWER OUTLET - DOUBLE
- HDMI HDMI OUTLET
- LF1 LIGHT FITTING - REFER TO ELECTRICAL ENGINEER SPECIFICATION
- LF5 LIGHT FITTING - TYPE 5
- LS LIGHT SWITCH
- LS SHELF
- SK2 SKIRTING - TYPE 2
- SMD SMOKE DETECTOR
- SPK ANUNCIATOR
- TV TELEVISION COAXIAL OUTLET

FOR CONSTRUCTION

Revision/Issue	Date
a Issued for Coordination - 100% DD	2024.04.12
P1 Preliminary Internal Elevations - RACF	2025.08.08
P2 Consolidated Set-to-date / SMG Comments	2025.08.15
P3 ISSUE FOR CONTRACT	2025.10.10
C1 ISSUE FOR CONSTRUCTION - INTERIORS	2026.03.26

Clarke
Hopkins
Clarke

ClarkeHopkinsClarke
Melbourne | Wurundjeri
L3, Melbourne Connect
700 Swanston Street
Carlton VIC 3063
Telephone (03) 9419 4340
Email studio@chc.com.au
www.chc.com.au

Sydney | Gadigal Country
Suite 3, Ground Floor
91 Campbell Street
Surry Hills NSW 2010
Telephone (02) 9221 9200
Email studio@chc.com.au
www.chc.com.au

Scale	1 : 50 @ A1
Date	01/03/2024
Drawn	RO / DP
Architect	EL

Project
Summerset Oakleigh
52 Golf Road, Oakleigh South, VIC

Drawing
Internal Elevations - Village Admin -
Meeting, Village Manager, Sales Manager
and CBM Office

Drawing No.
230185/A1802
C1