

Legend - Internal Elevations

DRAWINGS TO BE READ IN CONJUNCTION WITH ARCHITECTURAL SPECIFICATION & MATERIALS, PRODUCTS & FINISHES SCHEDULE.

PT# PAINT FINISH TO ALL WALLS WITHIN NEW & AFFECTED ROOMS/ AREAS UNLESS OTHERWISE SHOWN

CSE	CONCRETE SEALER
DPR	DOOR PROTECTION
GD	GRAPHIC FILM
LM	LAMINATE
MI	MIRROR
PBD	PINBOARD
PT	PAINT FINISH
REN	RENDER FINISH
SB	SPLASHBACK
ST	STONE
WB	WHITEBOARD
WP	WALL PROTECTION
WT	WALL TILE
WV	WALL VINYL

NOTES:
1. LAMINATE CARCASS FOR ALL VISIBLE OPEN SHELVING, UNLESS OTHERWISE NOTED
2. MELAMINETO ALL INTERNAL CARCASS OF JOINERY, UNLESS OTHERWISE NOTED.

Legend - Floor Finishes

C	CARPET
CO	CONCRETE
E	EPOXY FINISH
L	LINOLEUM
M	MATTING
PU	PAVING UNIT - TBC WITH LANDSCAPE
R	RUBBER FLOORING
T	TILING
TF	TIMBER FLOORING
V	VINYL
LVT	LUXURY VINYL TILE PLANK

---	PROTECTION RAILS OR CRASH RAILS - REFER TO MATERIAL SCHEDULE FOR DETAILS
---	WL1- REFER TO MATERIAL SCHEDULE FOR DETAILS
---	WL2 - REFER TO MATERIAL SCHEDULE FOR DETAILS

NOTE:
FALLS TO ALL FLOOR WASTES IN ACCORDANCE WITH AS 3740.

Keynote Legend


3DSPT	DISPENSER - PAPER TOWEL - GROUP 3
3DSS	SOAP DISPENSER - GROUP 3
BA1	BASIN - TYPE 1
BA11	BASIN - TYPE 11
DR	DRAWER
EM	EMERGENCY LIGHT
EXH	EXHAUST
FDS01	SHOWER BENCH - FOLDING
FW1	FLOOR WASTE - TYPE 1
GP02	POWER OUTLET - DOUBLE
GR1	GRAB RAIL - TYPE 1
GR2	GRAB RAIL - TYPE 2
GR3	GRAB RAIL - TYPE 3
GR5	GRAB RAIL - TYPE 5
GR6	GRAB RAIL - TYPE 6
LF1	LIGHT FITTING - REFER TO ELECTRICAL ENGINEER SPECIFICATION
LS	LIGHT SWITCH
MD	MOTION DETECTOR
M1	MIRROR - TYPE 1
P1	TOILET PAN TYPE 01
P4	TOILET PAN TYPE 04
RBH01	ROBE HOOK - TYPE 1
SD3	SOAP DISPENSER - TYPE 3
SHW1	SHOWER - TYPE 1
SMD	SMOKE DETECTOR
SPK	ANNUNCIATOR
SPR	SPRINKLER
TAP1	TAP - TYPE 1
TAP2	TAP - TYPE 2
TAP7	TAP - TYPE 7
THD	THERMAL DETECTOR
TRH	TOILET ROLL HOLDER

FOR CONSTRUCTION


Drawing No.

230185/A1804


C1

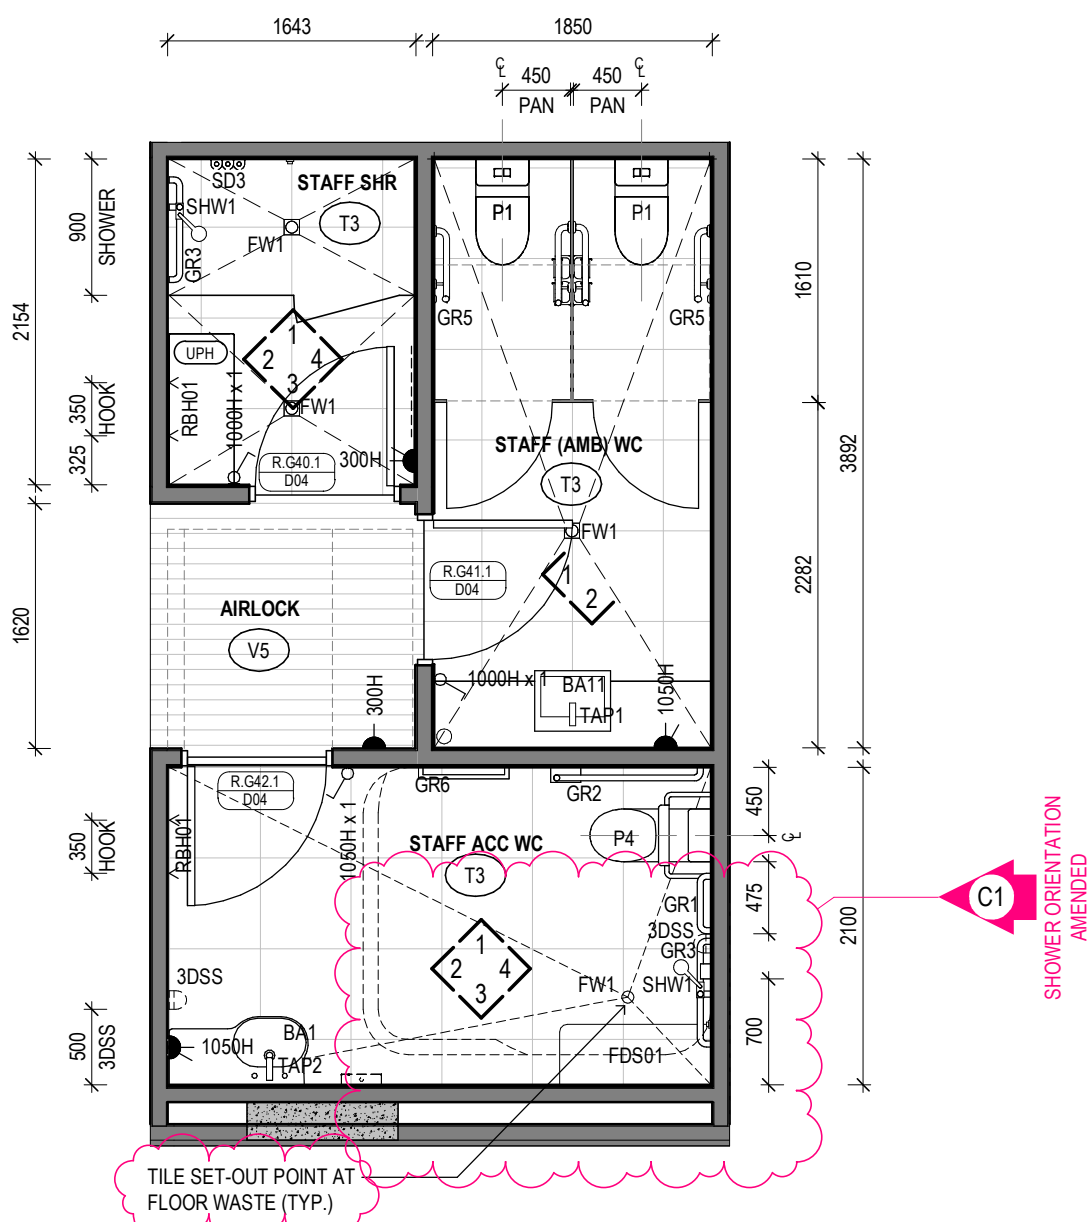


1 VILLAGE ADMIN - STAFF AMENITIES
Scale 1: 50

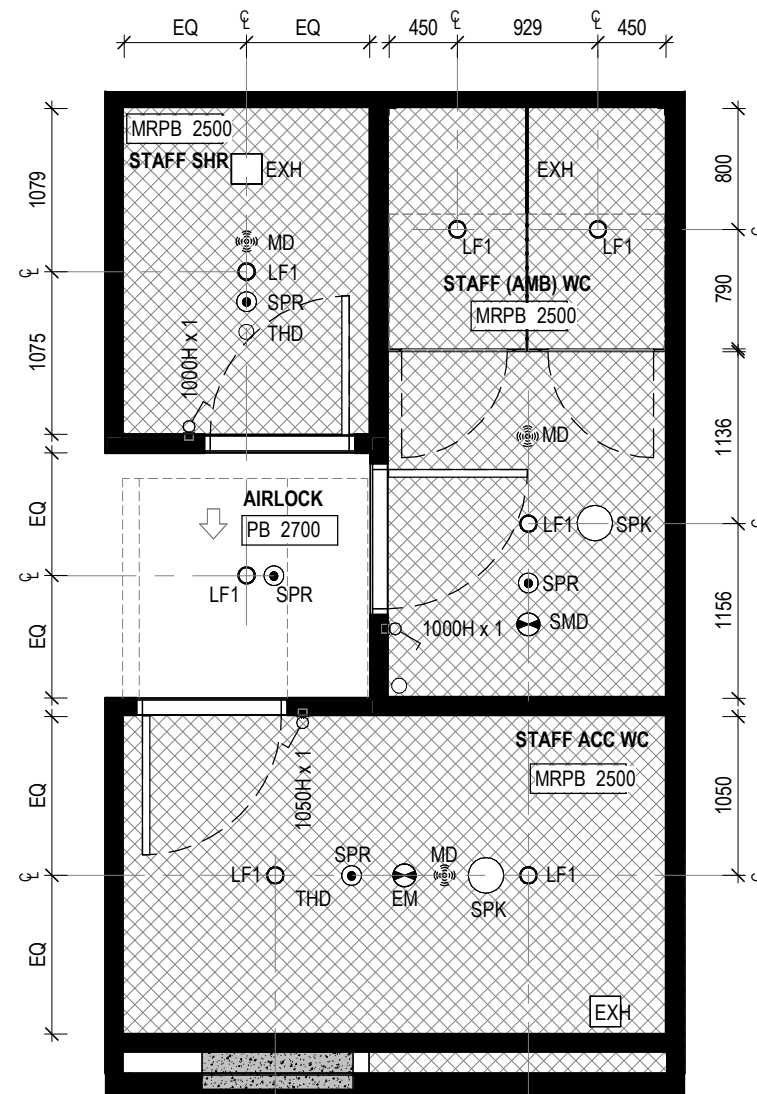


2 RCP - VILLAGE ADMIN - STAFF AMENITIES
Scale 1: 50

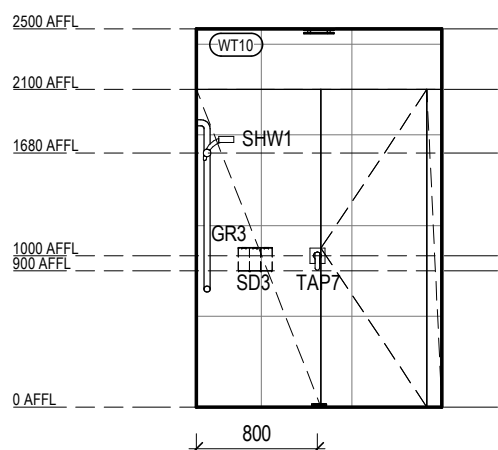


STAFF SHOWER
ELEVATION 1
Scale 1: 50

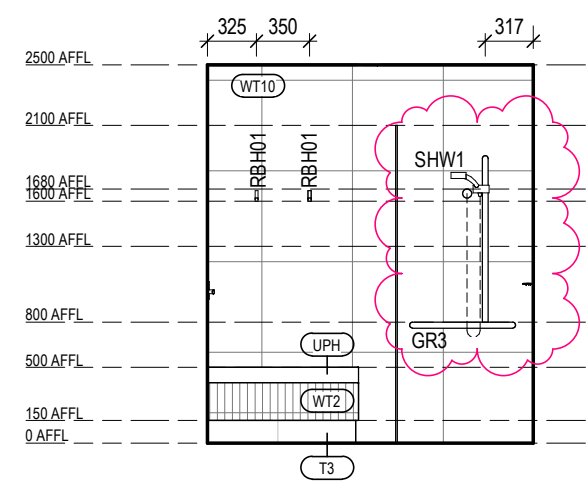


STAFF SHOWER
ELEVATION 2
Scale 1: 50

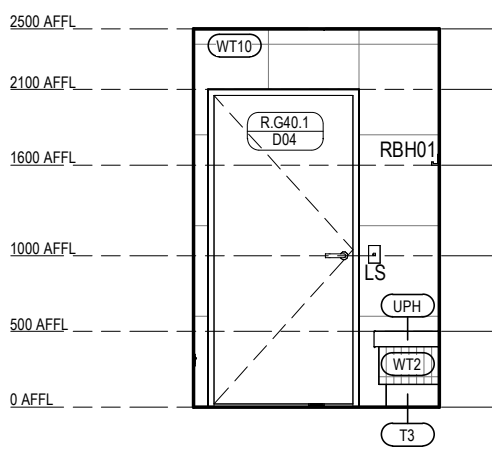


STAFF SHOWER
ELEVATION 3
Scale 1: 50

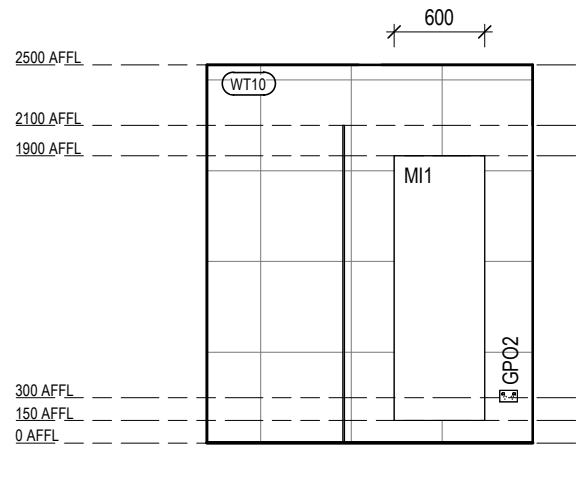


STAFF SHOWER
ELEVATION 4
Scale 1: 50

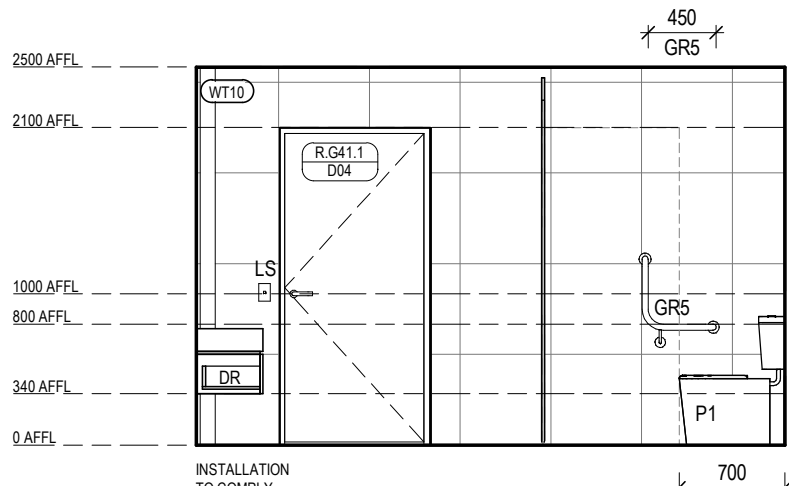


STAFF AMBULANT WC
ELEVATION 1
Scale 1: 50

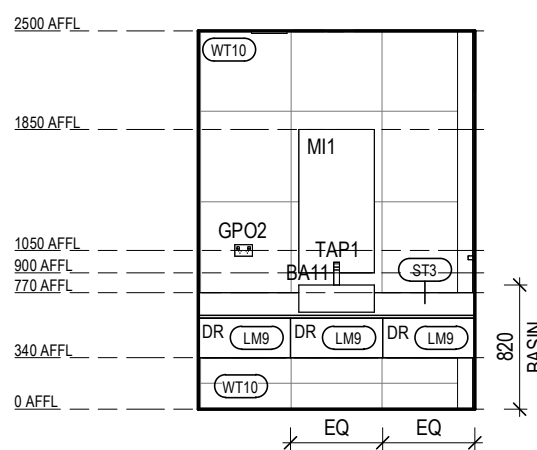


STAFF AMBULANT WC
ELEVATION 2
Scale 1: 50

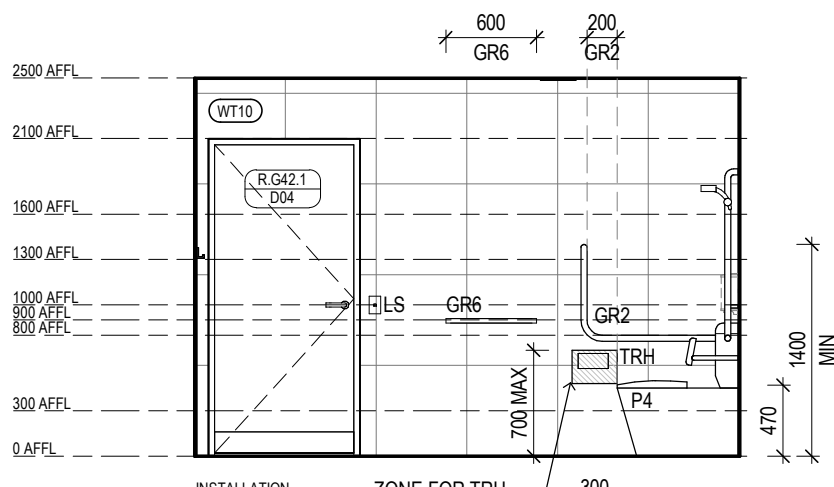


STAFF ACCESSIBLE WC
ELEVATION 1
Scale 1: 50

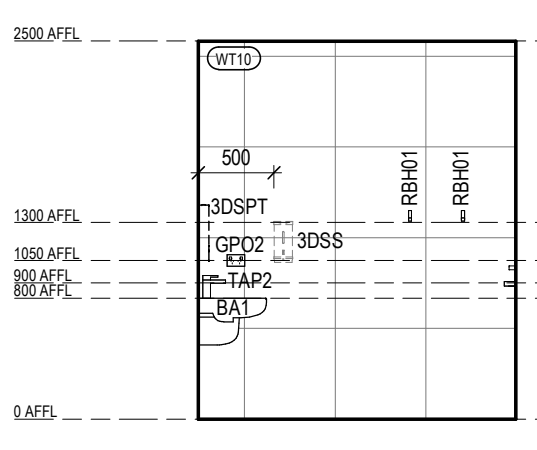

STAFF ACCESSIBLE WC
ELEVATION 2
Scale 1: 50

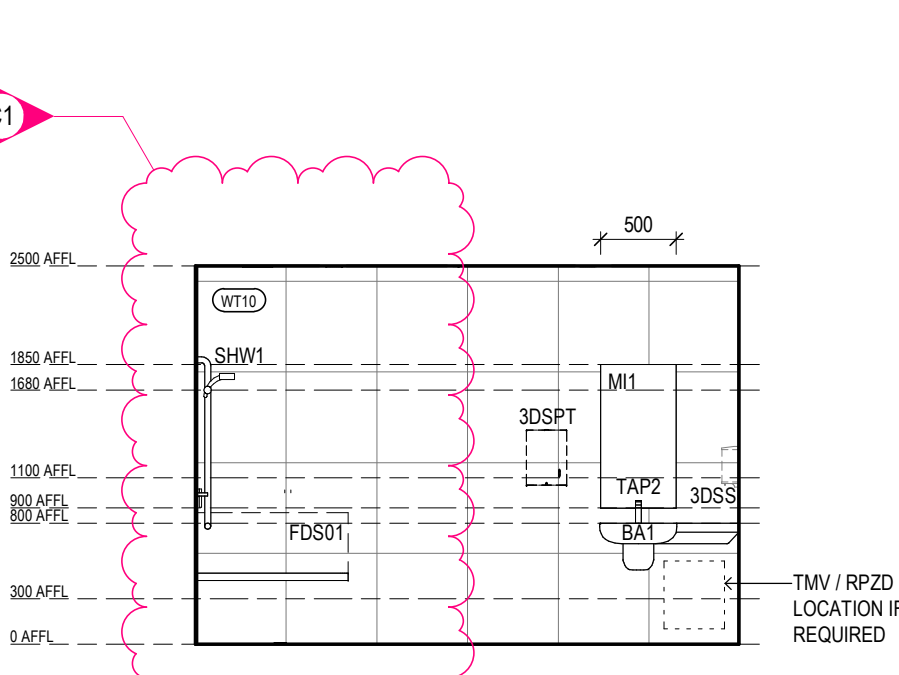

STAFF ACCESSIBLE WC
ELEVATION 3
Scale 1: 50

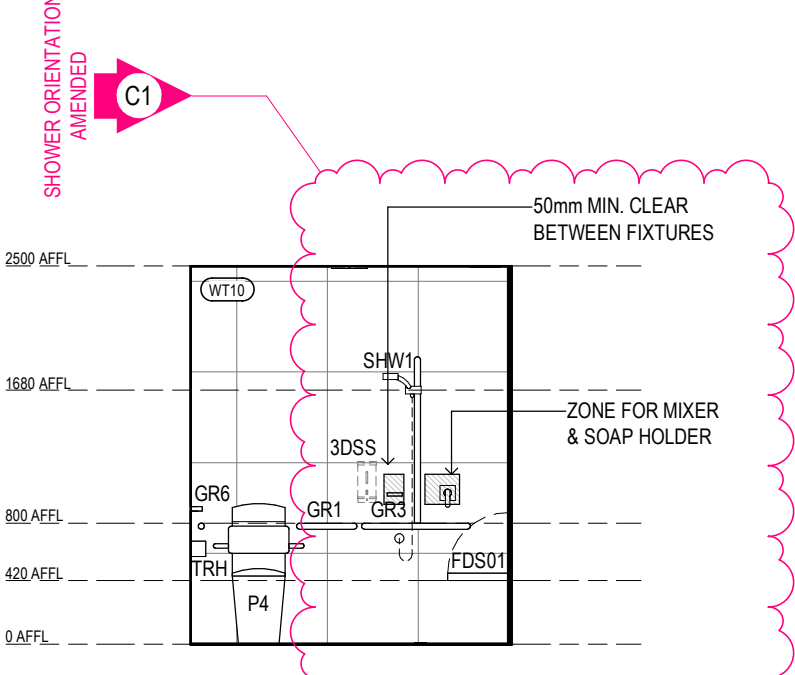

STAFF ACCESSIBLE WC
ELEVATION 4
Scale 1: 50

Clarke
Hopkins
Clarke

ClarkeHopkinsClarke

Melbourne | Wurundjeri
Suite 3, Melbourne Connect
700 Swanston Street
Carlton VIC 3063
Telephone (03) 9419 4340
Email studio@chc.com.au
www.chc.com.au

Sydney | Gadigal Country
Suite 3, Ground Floor
91 Campbell Street
Surry Hills NSW 2010
Telephone (02) 9221 9200
Email studio@chc.com.au
www.chc.com.au

Scale 1: 50 @ A1
Date 01/03/2024
Drawn EL / DP
Architect EL

Project
Summerset Oakleigh
52 Golf Road, Oakleigh South, VIC

Drawing
Internal Elevations - Village Admin - Staff
Amenities

Revision/Issue Date
P1 Preliminary Internal Elevations - RACF 2025.08.08
P2 Consolidated Set-to-date / SMG Comments 2025.08.15
P3 ISSUE FOR CONTRACT 2025.10.10
C1 ISSUE FOR CONSTRUCTION - INTERIORS 2026.03.26