



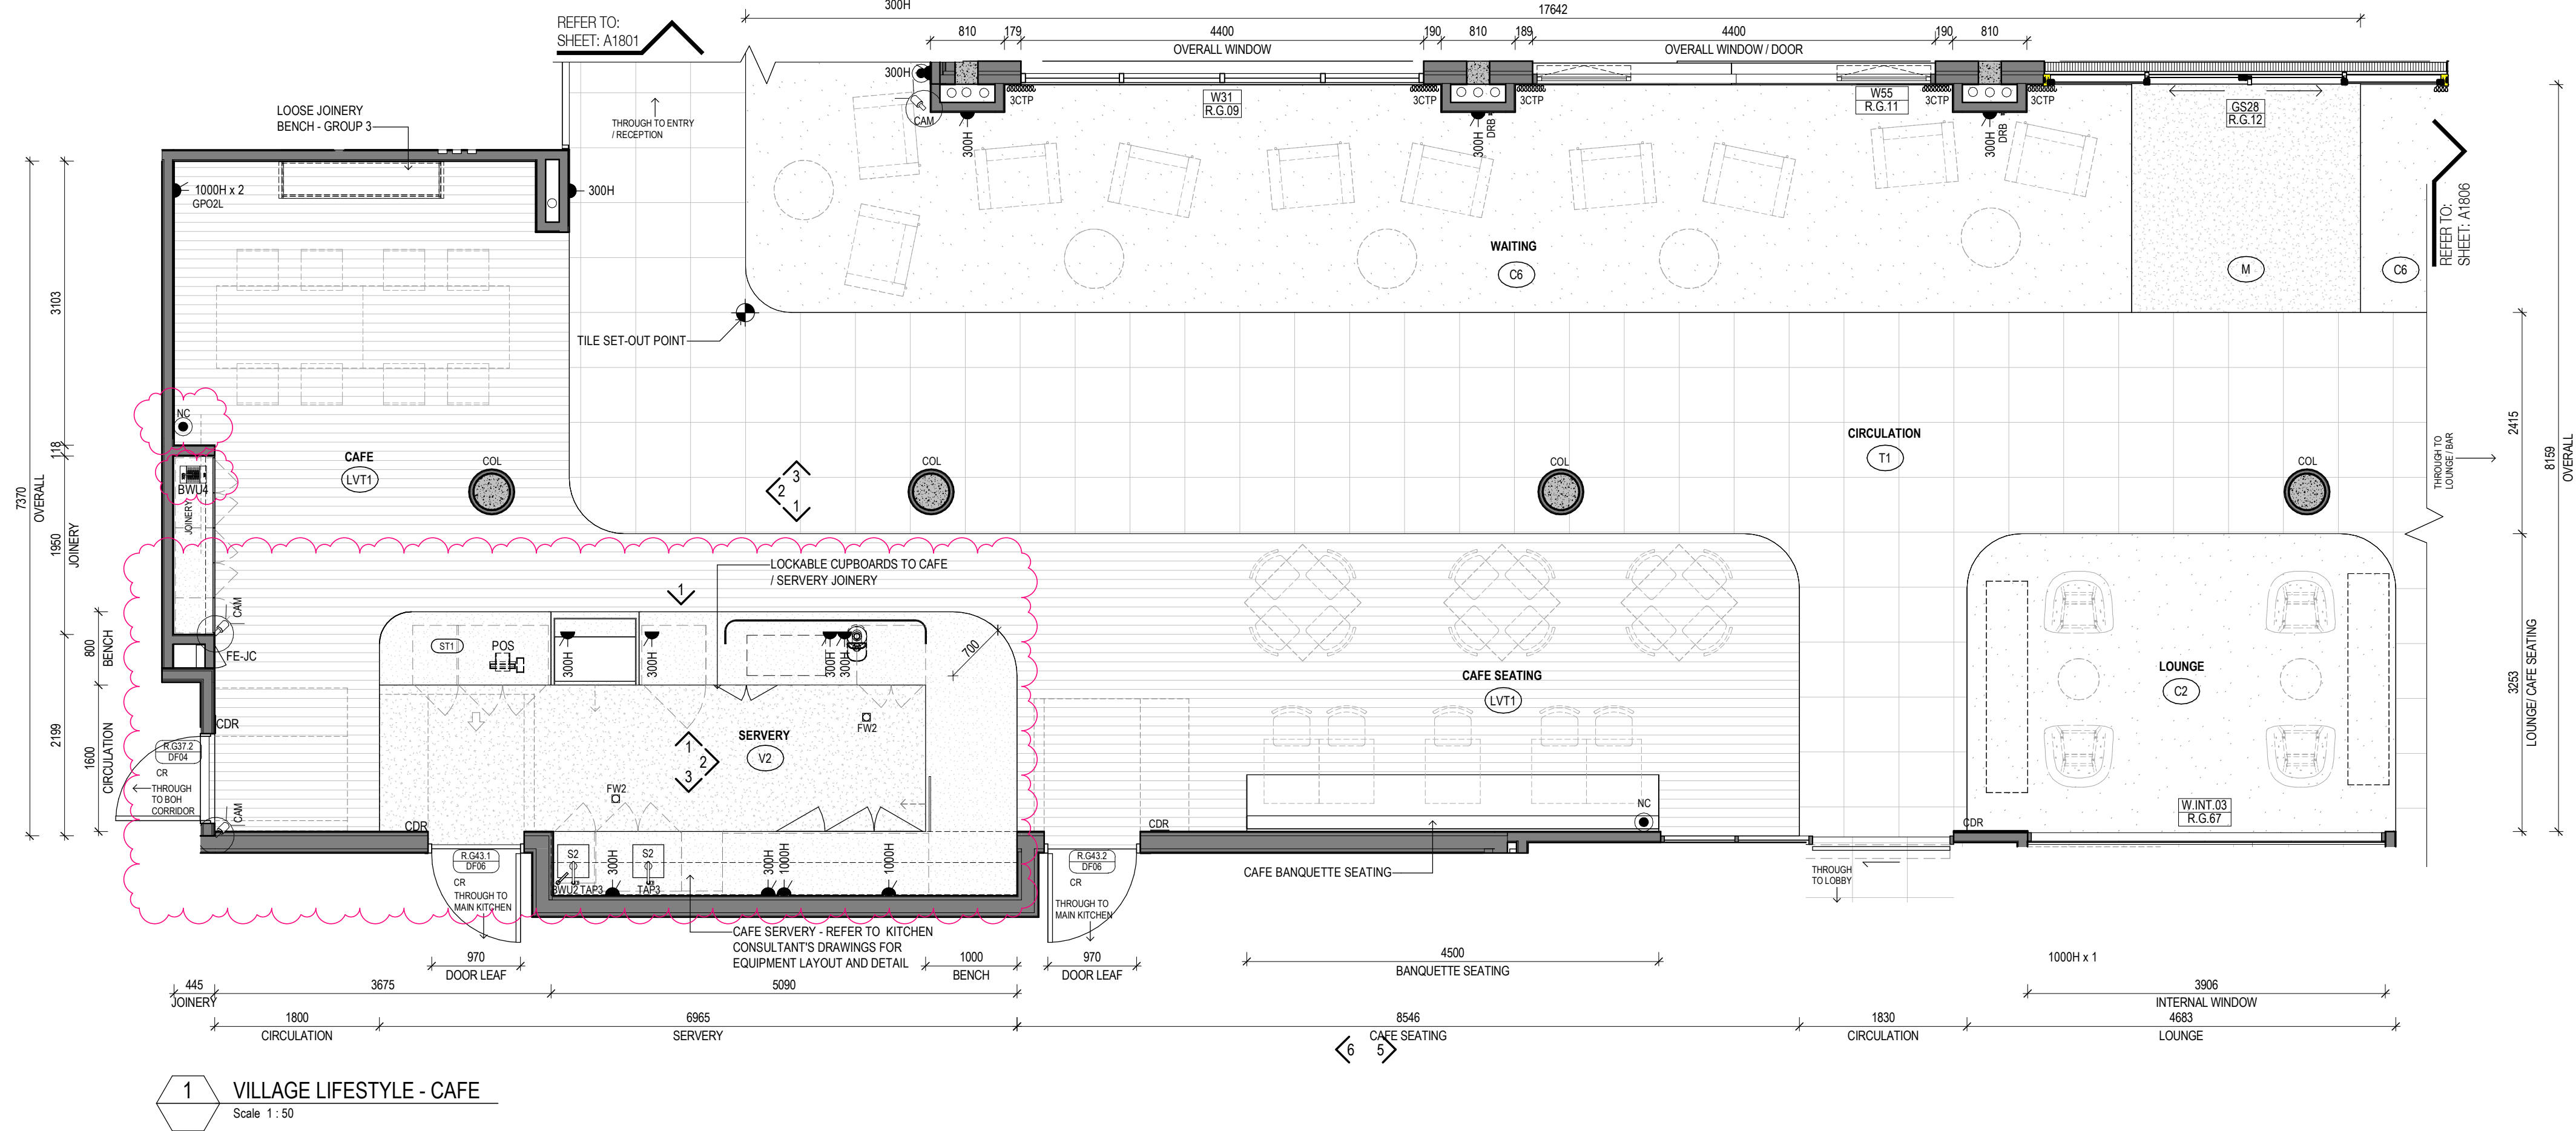


1 VILLAGE LIFESTYLE - CAFE
Scale 1 : 50

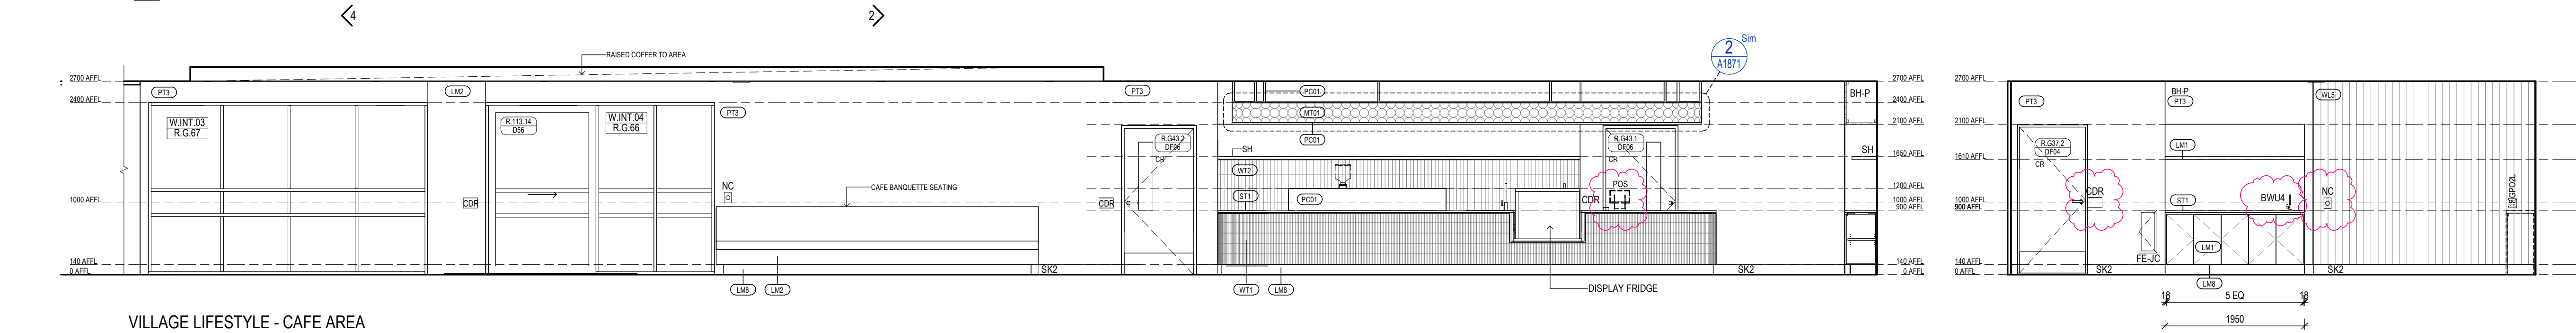


VILLAGE LIFESTYLE - CAFE AREA
ELEVATION 1
Scale 1 : 50


VILLAGE LIFESTYLE - CAFE AREA
ELEVATION 2
Scale 1 : 50

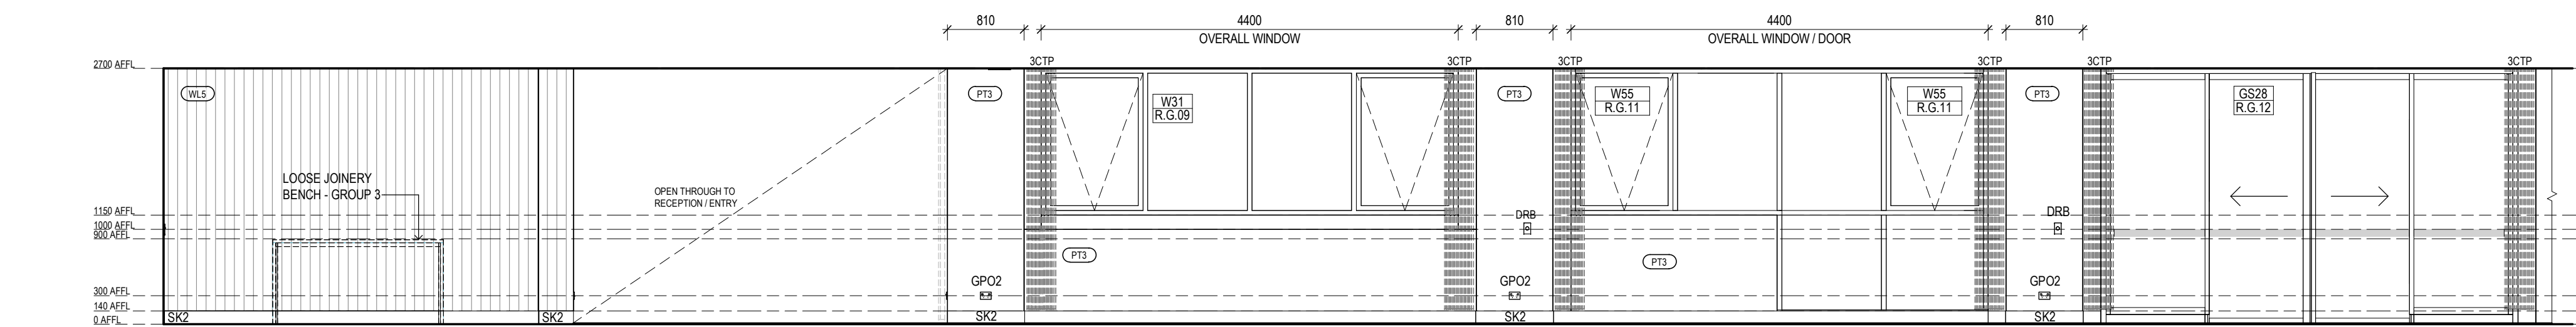


VILLAGE LIFESTYLE - CAFE AREA
ELEVATION 3
Scale 1 : 50

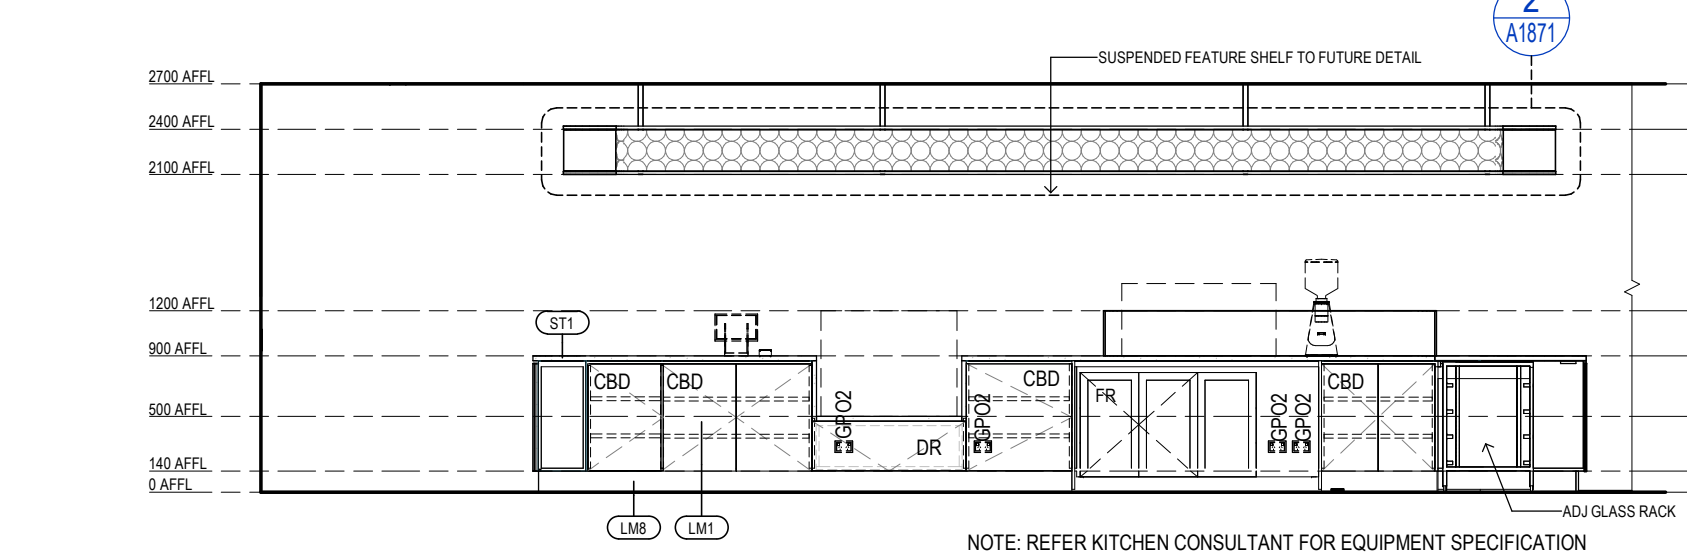

VILLAGE LIFESTYLE - CAFE AREA
ELEVATION 1
Scale 1 : 50

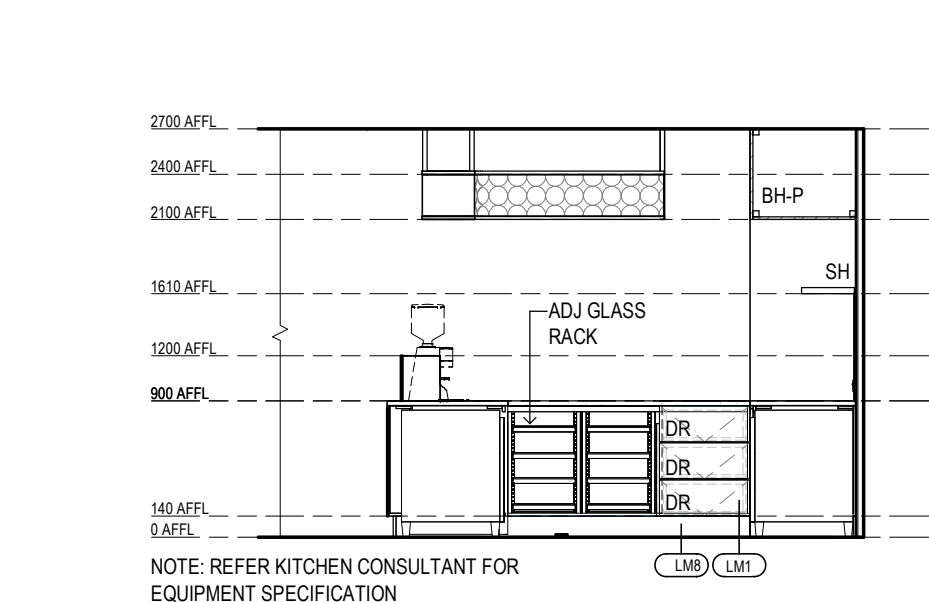

VILLAGE LIFESTYLE - CAFE AREA
ELEVATION 2
Scale 1 : 50

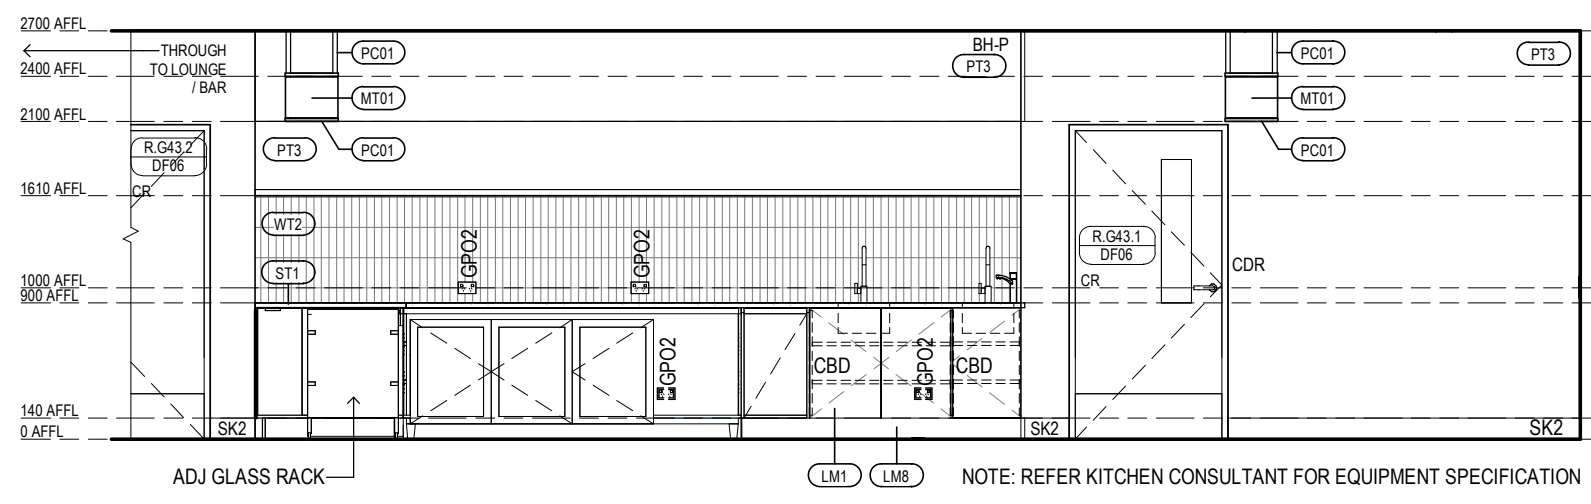

VILLAGE LIFESTYLE - CAFE AREA
ELEVATION 3
Scale 1 : 50

Legend - Internal Elevations

DRAWINGS TO BE READ IN CONJUNCTION WITH ARCHITECTURAL SPECIFICATION & MATERIALS, PRODUCTS & FINISHES SCHEDULE.
PT# PAINT FINISH TO ALL WALLS WITHIN NEW & AFFECTED ROOMS/ AREAS UNLESS OTHERWISE SHOWN

- CSE CONCRETE SEALER
- DPR DOOR PROTECTION
- GD GRAPHIC FILM
- LM LAMINATE
- MI MIRROR
- PBD PINBOARD
- PT PAINT FINISH
- REN RENDER FINISH
- SB SPLASHBACK
- ST STONE
- WB WHITEBOARD
- WP WALL PROTECTION
- WT WALL TILE
- WV WALL VINYL

NOTES:
1. LAMINATE CARCASS FOR ALL VISIBLE OPEN SHELVING, UNLESS OTHERWISE NOTED
2. MELAMINETO ALL INTERNAL CARCASS OF JOINERY, UNLESS OTHERWISE NOTED.

Legend - Floor Finishes

- C CARPET
- CO CONCRETE
- E EPOXY FINISH
- L LINOLEUM
- M MATTING
- PU PAVING UNIT - TBC WITH LANDSCAPE
- R RUBBER FLOORING
- T TILING
- TF TIMBER FLOORING
- V VINYL
- LVT LUXURY VINYL TILE PLANK

- PROTECTION RAILS OR CRASH RAILS - REFER TO MATERIAL SCHEDULE FOR DETAILS
- WL1- REFER TO MATERIAL SCHEDULE FOR DETAILS
- WL2- REFER TO MATERIAL SCHEDULE FOR DETAILS

NOTE:
FALLS TO ALL FLOOR WASTES IN ACCORDANCE WITH AS 3740.

Keynote Legend

- 3CTP CURTAINS - GROUP 3
- BH-P BULKHEAD - PLASTERBOARD TYPE
- BWL2 BOILING WATER UNIT - TYPE 2
- CAM CCTV CAMERA
- CBD CUPBOARD
- CDR CARD READER
- COL COLUMN
- DR DRAWER
- DRB DOOR RELEASE BUTTON
- FE-JC FIRE EXTINGUISHER IN JOINERY CUPBOARD
- FR FRIDGE
- FW2 FLOOR WASTE - TYPE 2
- GPO2 POWER OUTLET - DOUBLE
- GPO2L POWER OUTLET - DOUBLE - LARGE PLATE
- NC NURSE CALL
- POS POINT-OF-SALE
- S2 SINK - TYPE 2
- SH SHELF
- SK2 SKIRTING - TYPE 2
- TAP3 TAP - TYPE 3

FOR CONSTRUCTION

Drawing No.

230185/A1805

C1

Clarke
Hopkins
Clarke

ClarkeHopkinsClarke

Melbourne | Wurundjeri
L9, Melbourne Connect
700 Swanston Street
Carlton VIC 3063
Telephone (03) 9419 4340
Email studio@chc.com.au
www.chc.com.au

Sydney | Gadigal Country
Suite 3, Ground Floor
91 Campbell Street
Surry Hills NSW 2010
Telephone (02) 9221 9200
Email studio@chc.com.au
www.chc.com.au

Scale
Date 1:50 @ A1
01/03/2024
Drawn EL / NS
Architect EL

Project
Summerset Oakleigh
52 Golf Road, Oakleigh South, VIC

Drawing
Internal Elevations - Village Lifestyle - Cafe

Revision/Issue
P1 Consolidated Set-to-date / SMG Comments
P2 Tender Pack Issue
P3 ISSUE FOR CONTRACT
C1 ISSUE FOR CONSTRUCTION - INTERIORS

Date
2025.08.15
2025.09.05
2025.10.10
2026.03.26