

Legend - Internal Elevations

DRAWINGS TO BE READ IN CONJUNCTION WITH ARCHITECTURAL SPECIFICATION & MATERIALS, PRODUCTS & FINISHES SCHEDULE.

PT# PAINT FINISH TO ALL WALLS WITHIN NEW & AFFECTED ROOMS/ AREAS UNLESS OTHERWISE SHOWN

- CSE CONCRETE SEALER
- DPR DOOR PROTECTION
- GD GRAPHIC FILM
- LM LAMINATE
- MI MIRROR
- PBD PINBOARD
- PT PAINT FINISH
- REN RENDER FINISH
- SB SPLASHBACK
- ST STONE
- WB WHITEBOARD
- WP WALL PROTECTION
- WT WALL TILE
- WV WALL VINYL

NOTES:
1. LAMINATE CARCASS FOR ALL VISIBLE OPEN SHELVING, UNLESS OTHERWISE NOTED
2. MELAMINETO ALL INTERNAL CARCASS OF JOINERY, UNLESS OTHERWISE NOTED.

Legend - Floor Finishes

- C CARPET
- CO CONCRETE
- E EPOXY FINISH
- L LINOLEUM
- M MATTING
- PU PAVING UNIT - TBC WITH LANDSCAPE
- R RUBBER FLOORING
- T TILING
- TF TIMBER FLOORING
- V VINYL
- LVT LUXURY VINYL TILE PLANK

PROTECTION RAILS OR CRASH RAILS - REFER TO MATERIAL SCHEDULE FOR DETAILS

WL1- REFER TO MATERIAL SCHEDULE FOR DETAILS

WL2- REFER TO MATERIAL SCHEDULE FOR DETAILS

NOTE:
FALLS TO ALL FLOOR WASTES IN ACCORDANCE WITH AS 3740.

Keynote Legend


- 3ART ARTWORK - GROUP 3
- 3CTP CURTAINS - GROUP 3
- 3TV(M) TELEVISION SCREEN 55 INCH - GROUP 3
- BH-J BULKHEAD - JOINERY TYPE
- CAM CCTV CAMERA
- CDR CARD READER
- DATA DATA OUTLET
- DR DRAWER
- FB FLOOR BOX
- FE-JC FIRE EXTINGUISHER IN JOINERY CUPBOARD
- FP FIRE PLACE
- FW3 FLOOR WASTE - TYPE 3
- GP02 POWER OUTLET - DOUBLE
- GP02L POWER OUTLET - DOUBLE - LARGE PLATE
- GP02L POWER OUTLET - CLEANERS
- HDMI HDMI OUTLET
- LS-L LIGHT SWITCH - LARGE PLATE
- NC NURSE CALL
- OH OVERHEAD CUPBOARD/SHELVING
- POS POINT OF SALE
- S2 SINK - TYPE 2
- SK2 SKIRTING - TYPE 2
- TAP3 TAP - TYPE 3
- TV TELEVISION COAXIAL OUTLET

FOR CONSTRUCTION

Drawing No.


230185/A1806

C1

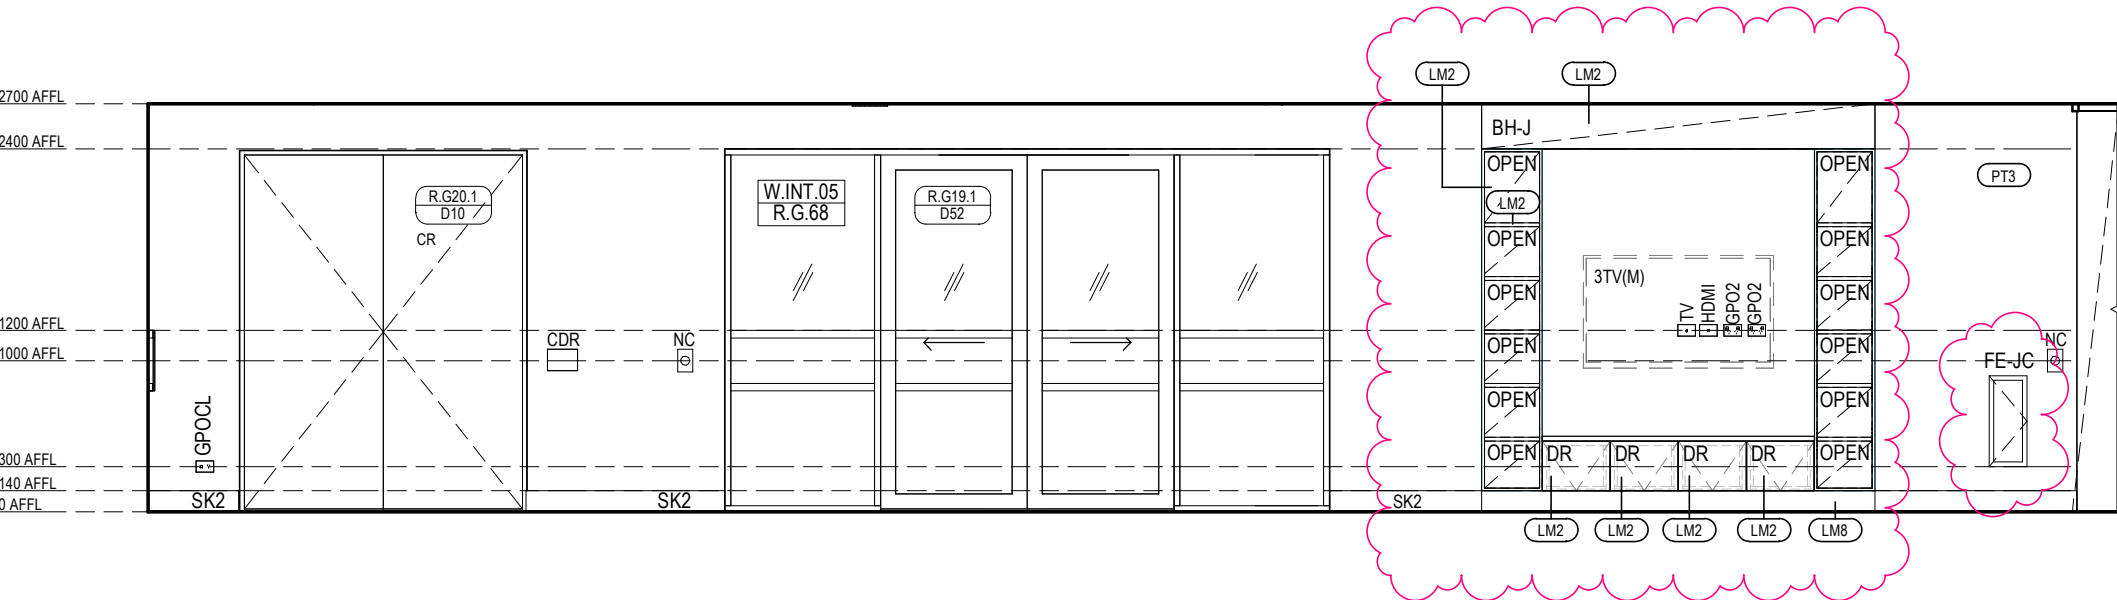


VILLAGE LIFESTYLE - LOUNGE & BAR

ELEVATION 1
Scale 1: 50

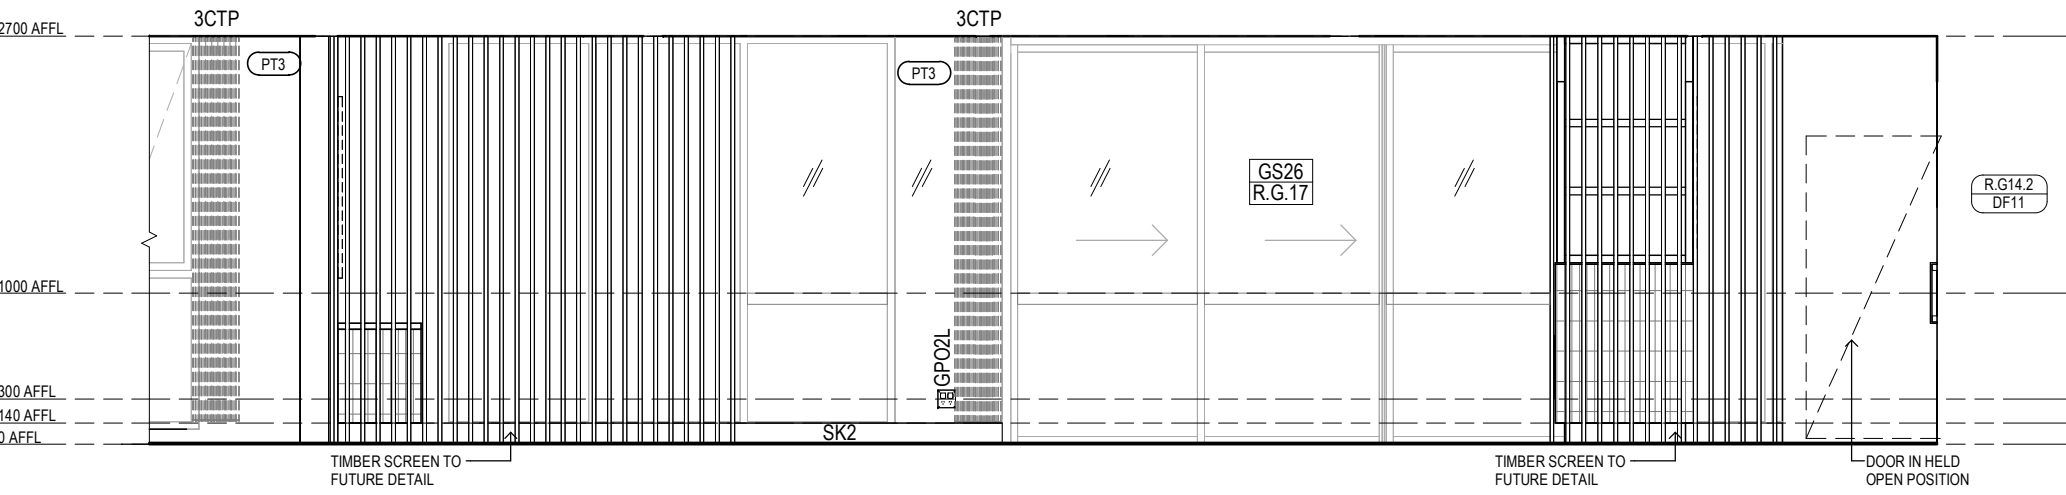


VILLAGE LIFESTYLE - LOUNGE & BAR

ELEVATION 2
Scale 1: 50

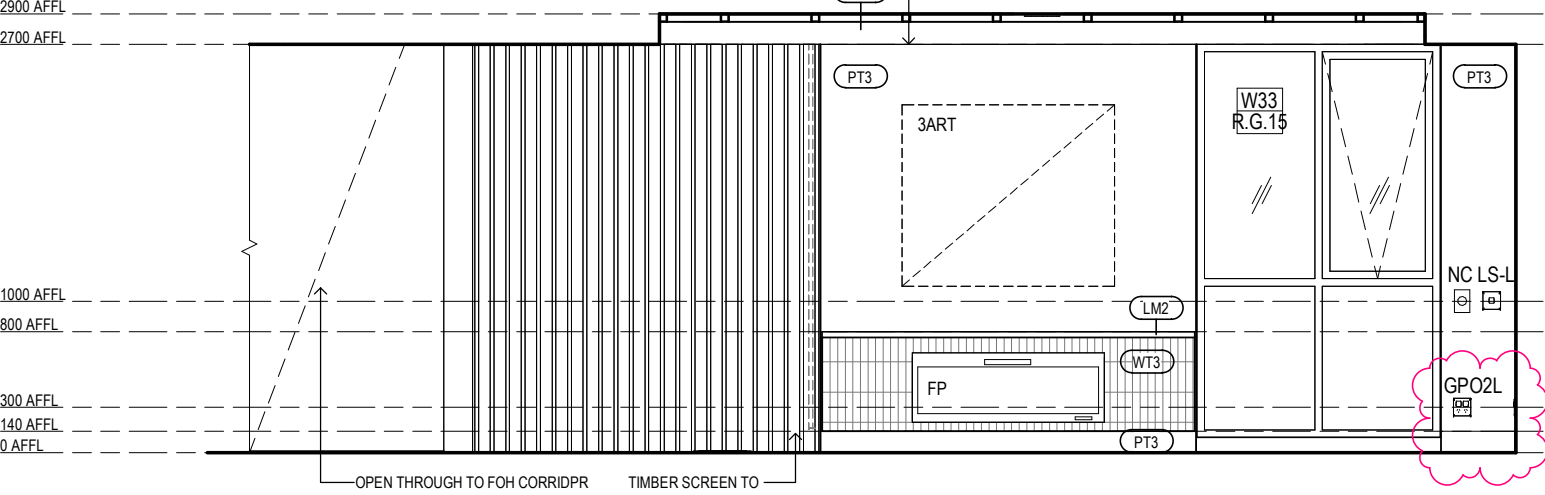


VILLAGE LIFESTYLE - LOUNGE & BAR

ELEVATION 3
Scale 1: 50

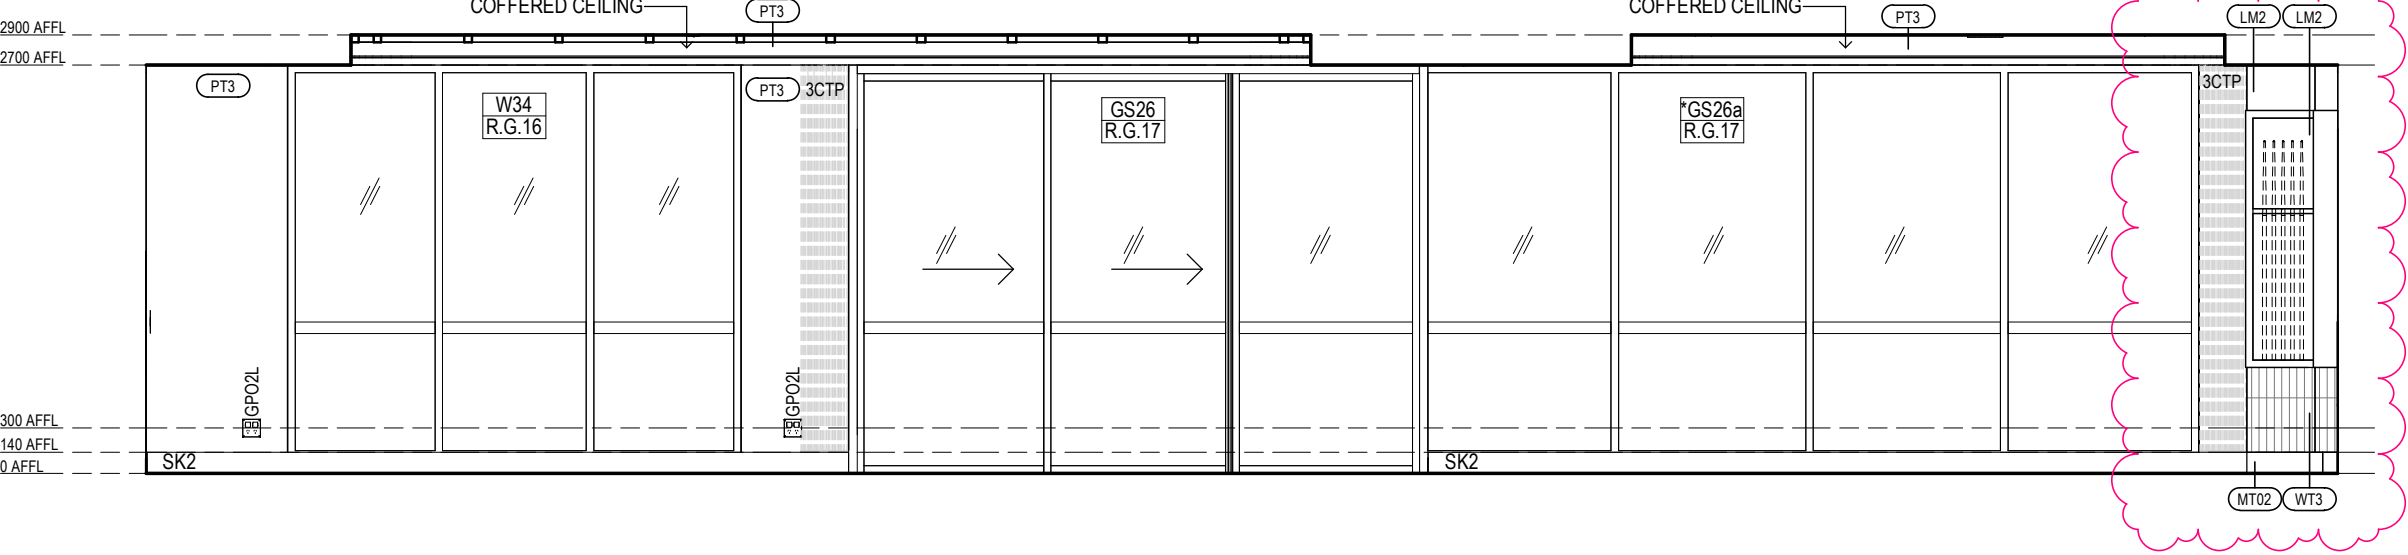


VILLAGE LIFESTYLE - LOUNGE & BAR

ELEVATION 4
Scale 1: 50

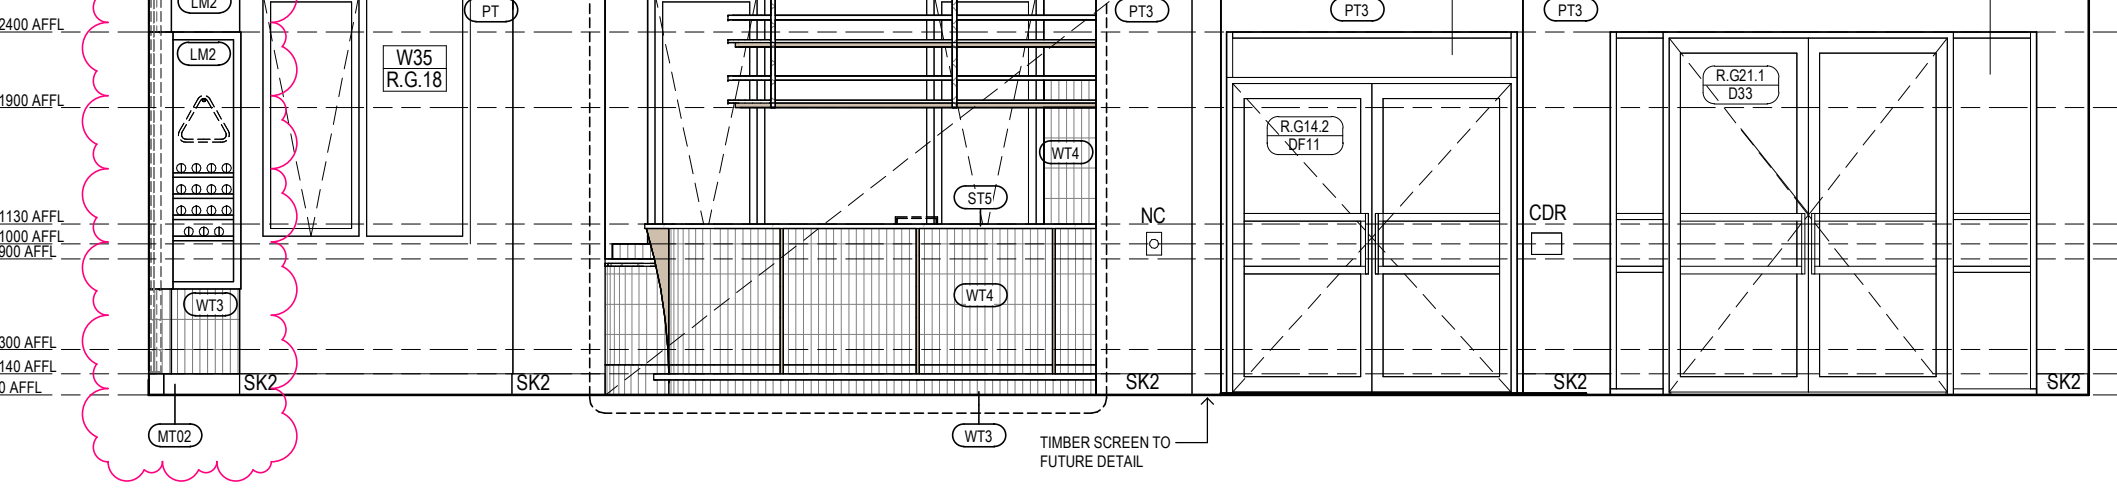


VILLAGE LIFESTYLE - LOUNGE & BAR

ELEVATION 5
Scale 1: 50

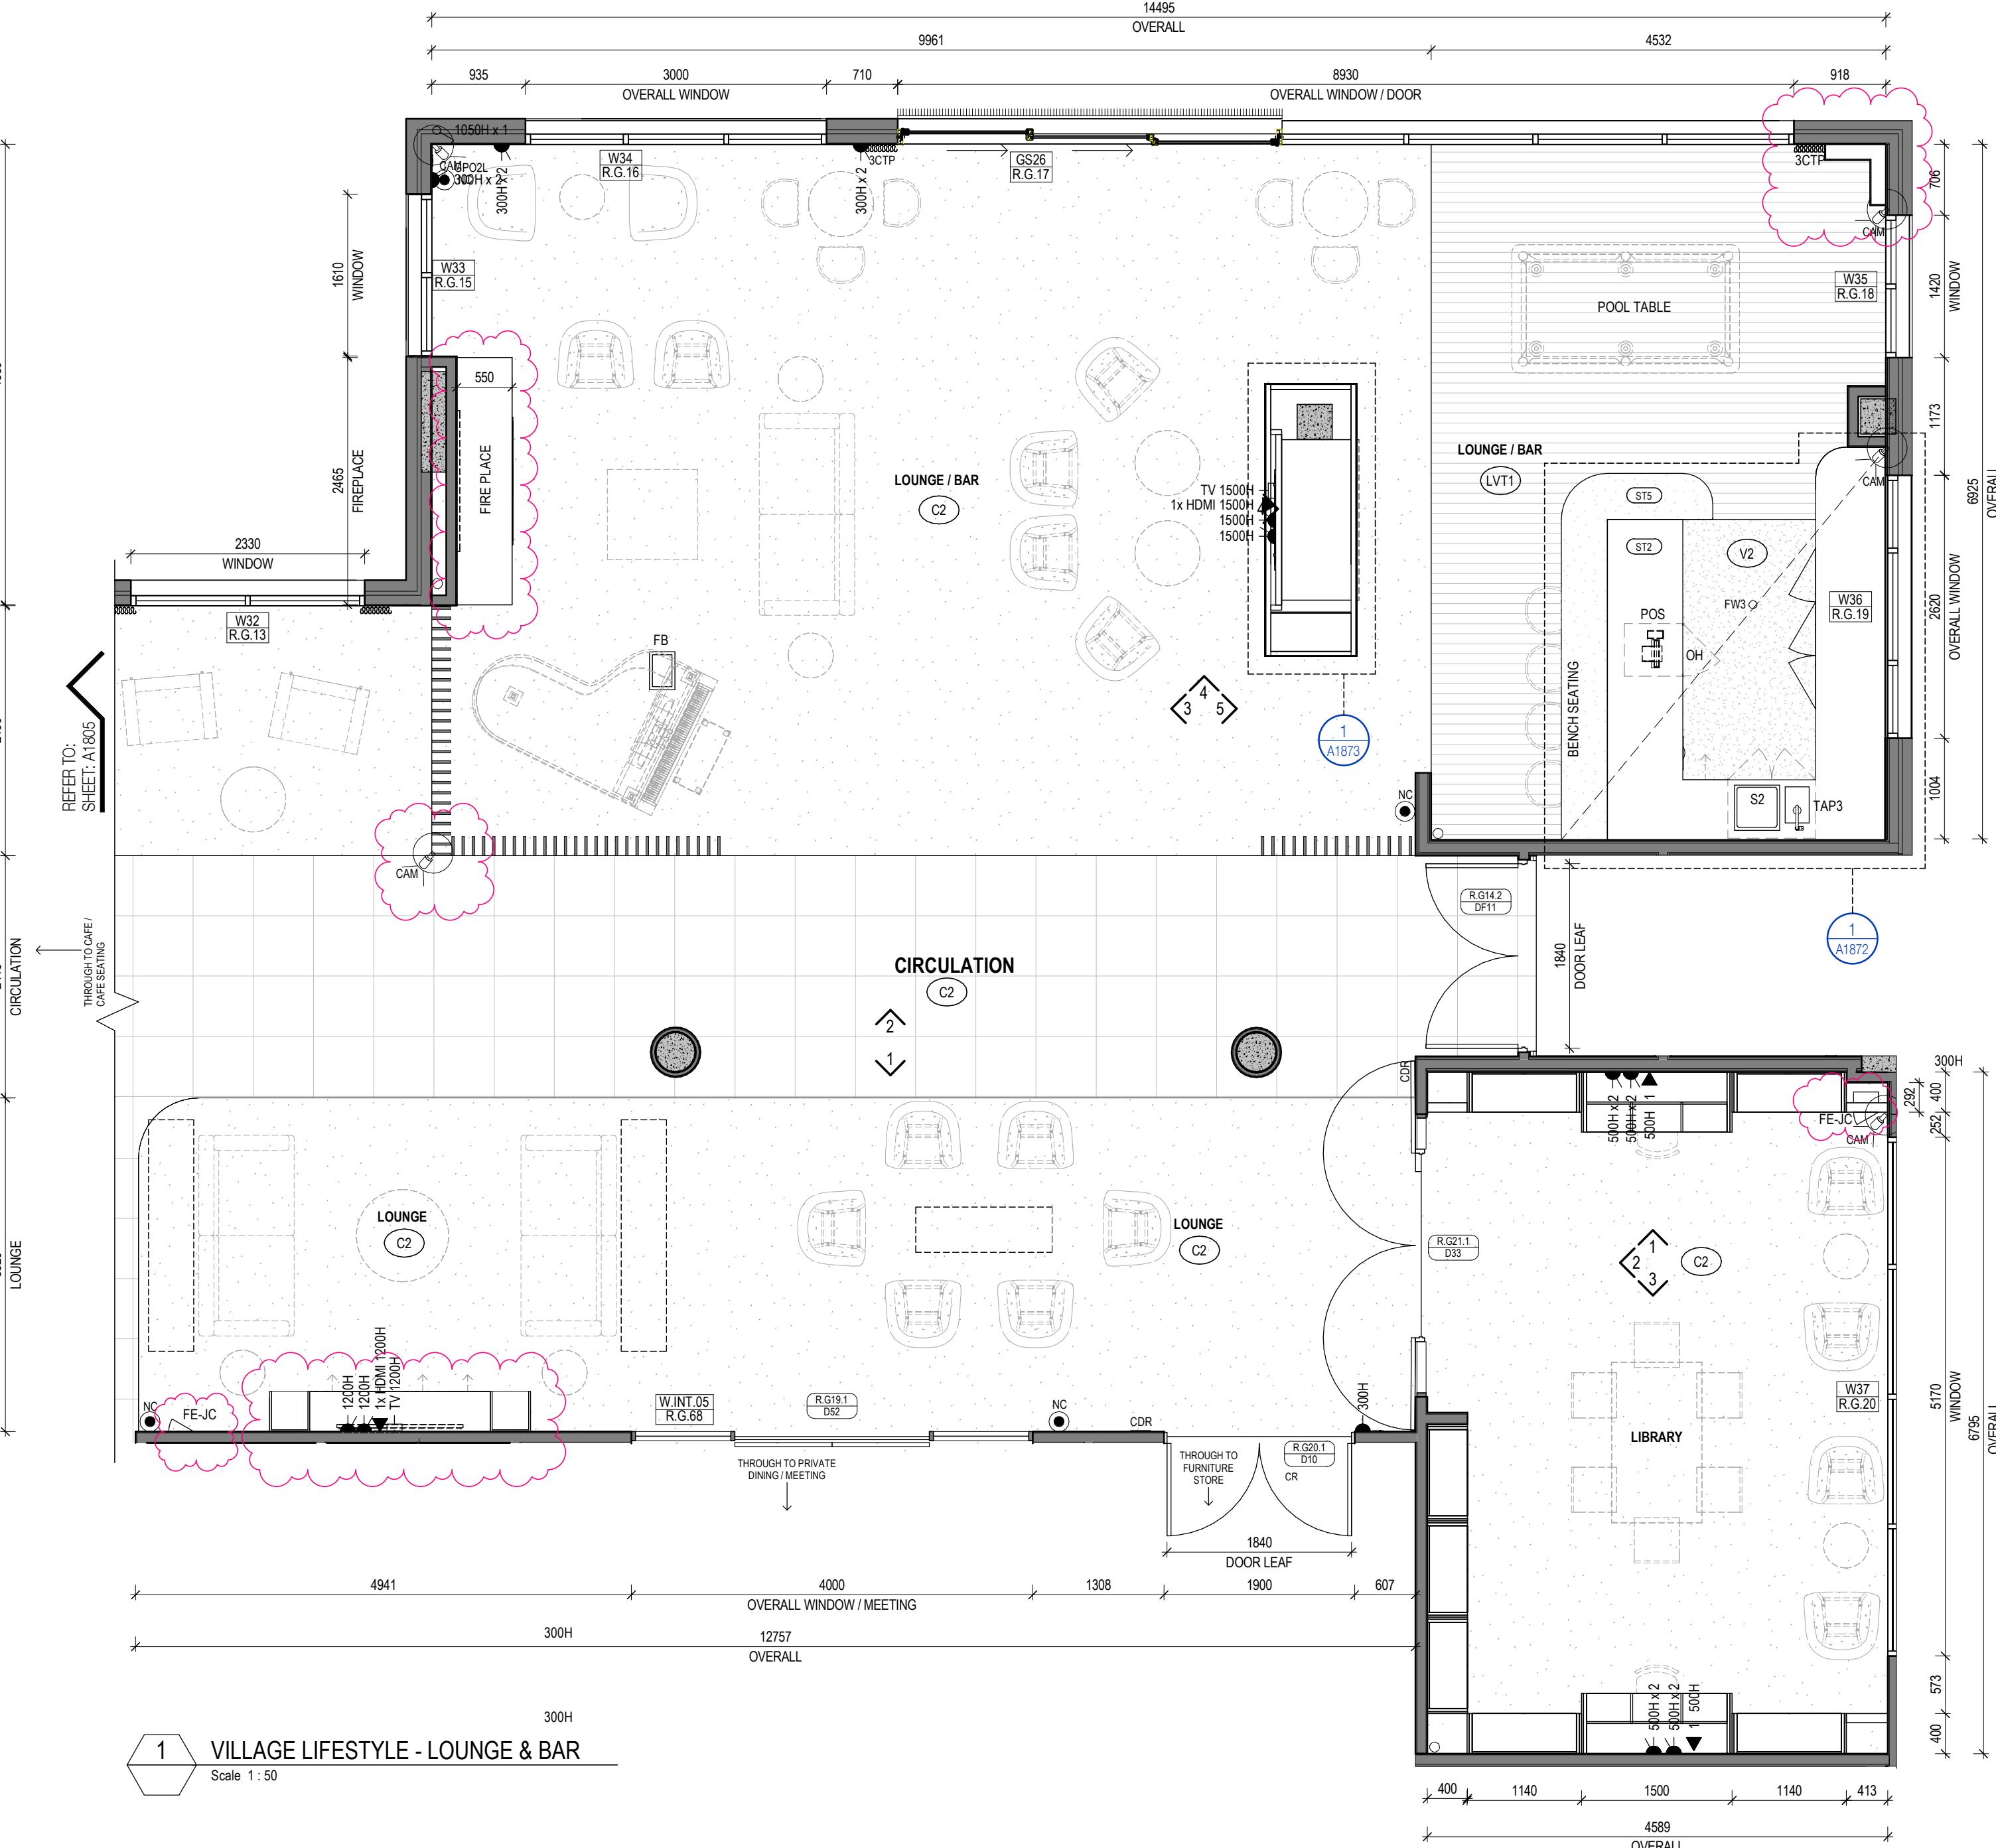

VILLAGE LIFESTYLE - LOUNGE & BAR

Scale 1: 50

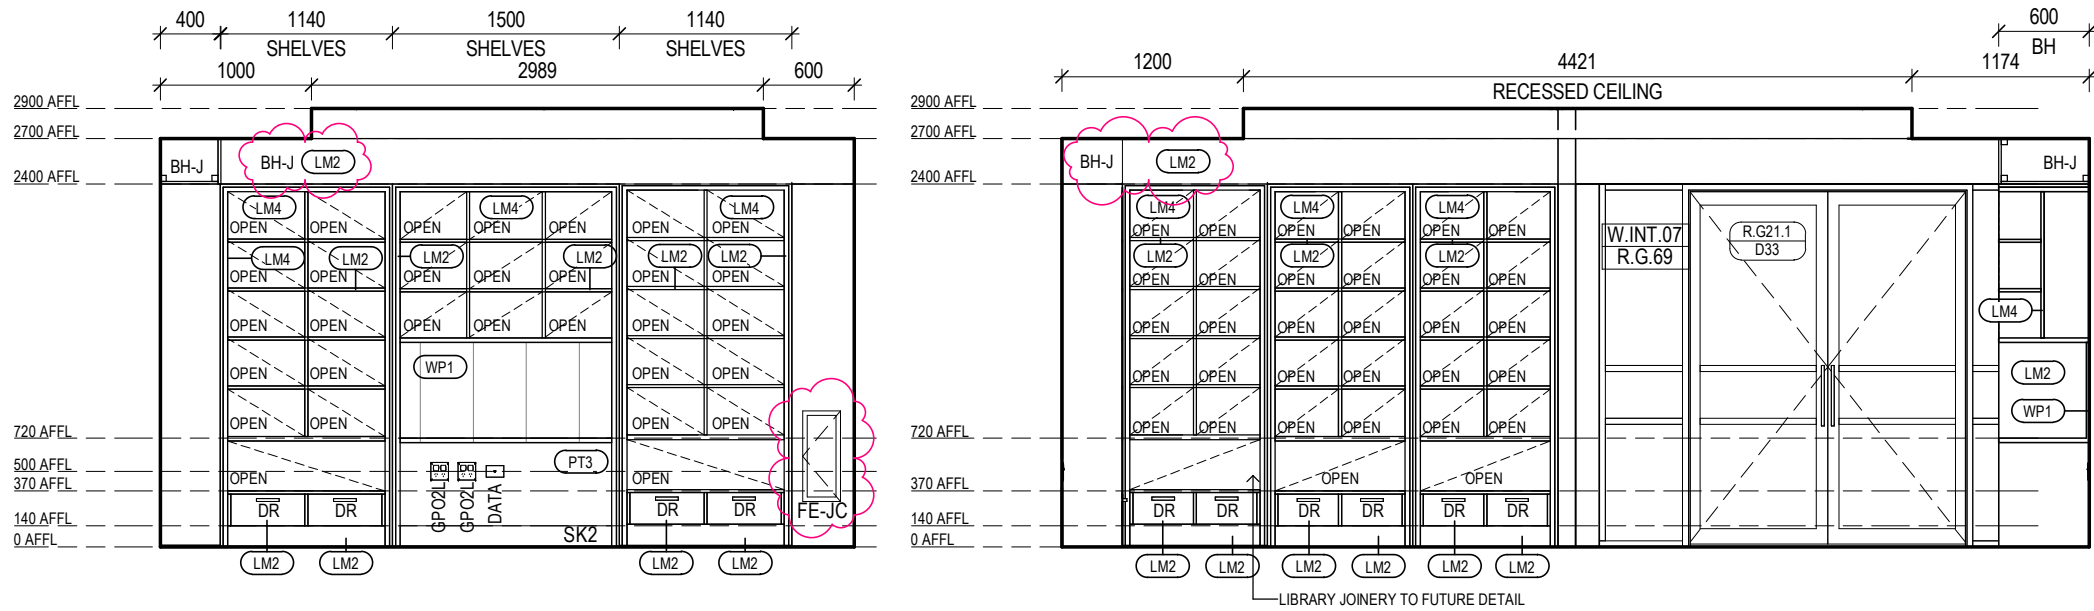


VILLAGE LIFESTYLE - LIBRARY

ELEVATION 1
Scale 1: 50

VILLAGE LIFESTYLE - LIBRARY

ELEVATION 2
Scale 1: 50

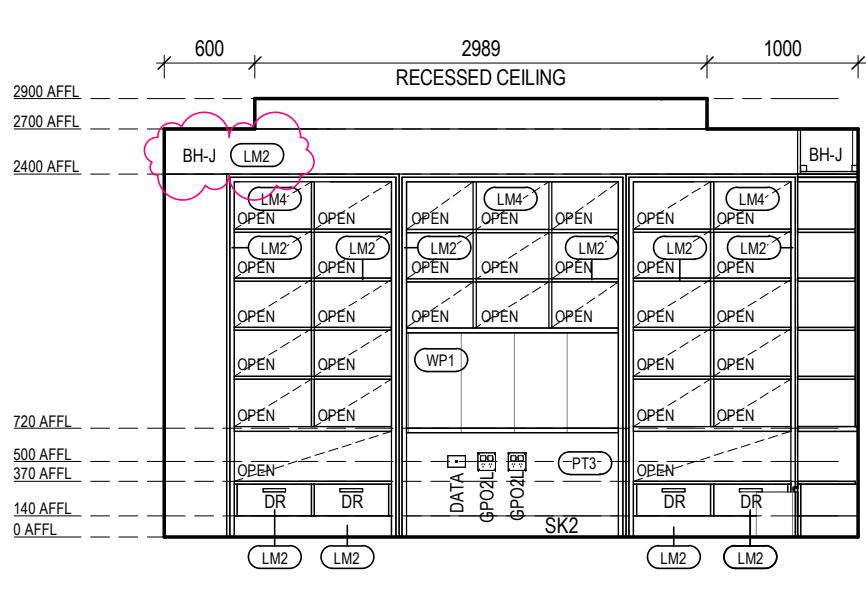

VILLAGE LIFESTYLE - LIBRARY

ELEVATION 3
Scale 1: 50

Clarke
Hopkins
Clarke

ClarkeHopkinsClarke

Melbourne | Wurundjeri

L3, Melbourne Connect

700 Swanston Street

Carlton VIC 3065

Telephone (03) 9419 4340

Email studio@chc.com.au

www.chc.com.au

Sydney | Gadigal Country

Suite 3, Ground Floor

91 Campbell Street

Surry Hills NSW 2010

Telephone (02) 9221 9200

Email studio@chc.com.au

www.chc.com.au

Scale 1: 50 @ A1

Date 01/03/2024

Drawn EL / NS

Architect EL

Project

Summerset Oakleigh

52 Golf Road, Oakleigh South, VIC

Drawing

Internal Elevations - Village Lifestyle -

Lounge & Bar

Drawing No.

230185/A1806

C1