

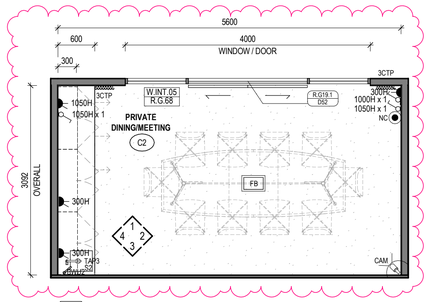



1 VILLAGE LIFESTYLE - PRIVATE DINING
Scale 1 : 50

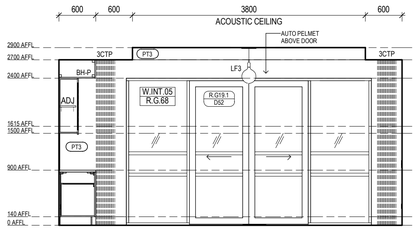


VILLAGE LIFESTYLE - PRIVATE DINING
ELEVATION 1
Scale 1 : 50

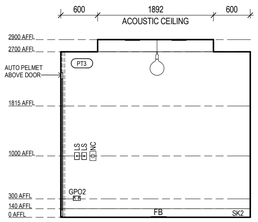


VILLAGE LIFESTYLE - PRIVATE DINING
ELEVATION 2
Scale 1 : 50

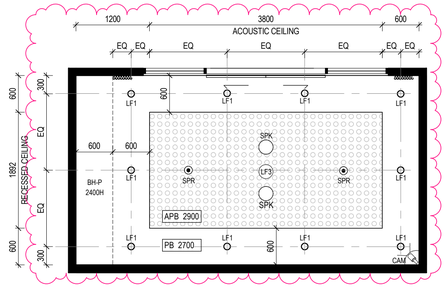


2 RCP - VILLAGE LIFESTYLE - PRIVATE DINING
Scale 1 : 50

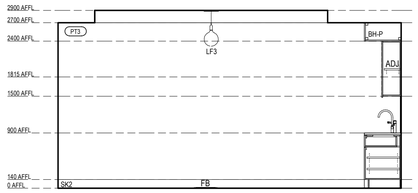


VILLAGE LIFESTYLE - PRIVATE DINING
ELEVATION 3
Scale 1 : 50

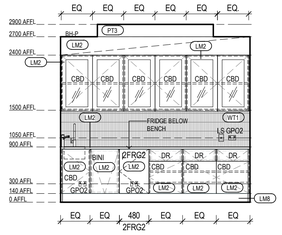


VILLAGE LIFESTYLE - PRIVATE DINING
ELEVATION 4
Scale 1 : 50

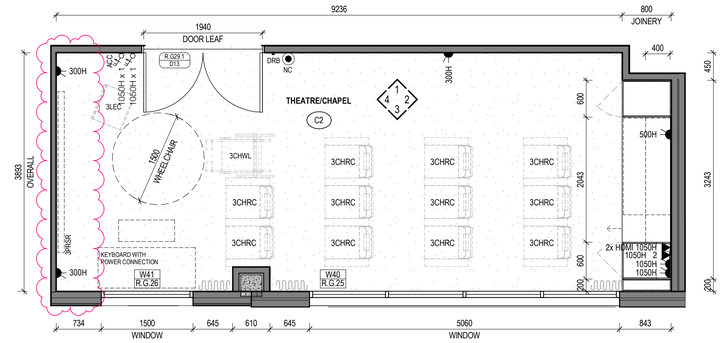


3 VILLAGE LIFESTYLE - THEATRE/ CHAPEL
Scale 1 : 50

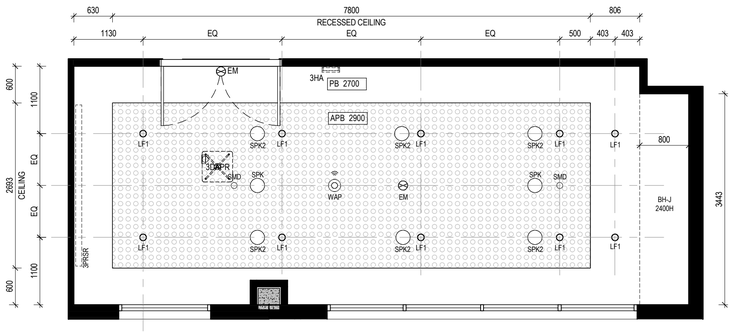


4 RCP - VILLAGE HEALTH & WELLNESS - THEATRE/CHAPEL
Scale 1 : 50

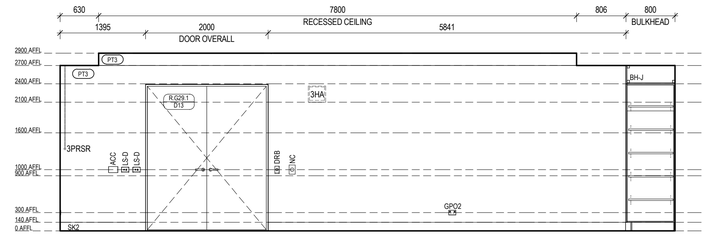


VILLAGE LIFESTYLE - THEATRE/CHAPEL
ELEVATION 1
Scale 1 : 50

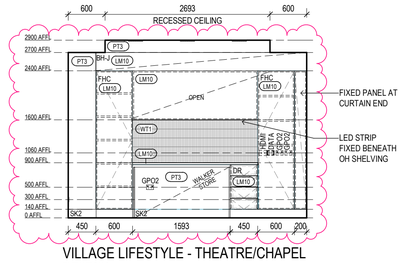

VILLAGE LIFESTYLE - THEATRE/CHAPEL
ELEVATION 2
Scale 1 : 50

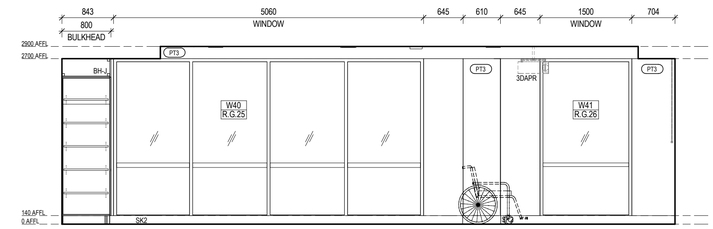

VILLAGE LIFESTYLE - THEATRE/CHAPEL
ELEVATION 3
Scale 1 : 50

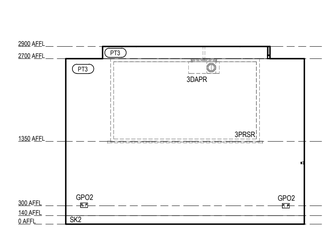

VILLAGE LIFESTYLE - THEATRE/CHAPEL
ELEVATION 4
Scale 1 : 50

Legend - Internal Elevations

DRAWINGS TO BE READ IN CONJUCTION WITH ARCHITECTURAL SPECIFICATION & MATERIALS, PRODUCTS & FINISHES SCHEDULE.

PT# PAINT FINISH TO ALL WALLS WITHIN NEW & AFFECTED ROOMS/ AREAS UNLESS OTHERWISE SHOWN

CSE	CONCRETE SEALER
DPR	DOOR PROTECTION
GD	GRAPHIC FILM
LM	LAMINATE
MI	MIRROR
PBD	PINBOARD
PT	PAINT FINISH
REN	RENDER FINISH
SB	SPLASHBACK
ST	STONE
WB	WHITEBOARD
WP	WALL PROTECTION
WT	WALL TILE
WV	WALL VINYL

NOTES:
1. LAMINATE CARCASS FOR ALL VISIBLE OPEN SHELVING, UNLESS OTHERWISE NOTED
2. MELAMINETO ALL INTERNAL CARCASS OF JOINERY, UNLESS OTHERWISE NOTED.

Legend - Floor Finishes

C	CARPET
CO	CONCRETE
E	EPOXY FINISH
L	LINOLEUM
M	MATTING
PU	PAVING UNIT - TBC WITH LANDSCAPE
R	RUBBER FLOORING
T	TILING
TF	TIMBER FLOORING
V	VINYL
LVT	LUXURY VINYL TILE PLANK

PROTECTION RAILS OR CRASH RAILS - REFER TO MATERIAL SCHEDULE FOR DETAILS

WL1- REFER TO MATERIAL SCHEDULE FOR DETAILS

WL2 - REFER TO MATERIAL SCHEDULE FOR DETAILS

NOTE:

FALLS TO ALL FLOOR WASTES IN ACCORDANCE WITH AS 3740.

Keynote Legend

2FRG2	INTEGRATED BAR FRIDGE - TYPE 2 - GROUP 2
3CHRC	CHAIR - CHAPEL - GROUP 3
3CHWL	WHEELCHAIR - GROUP 3
3CTP	CURTAINS - GROUP 3
3DAPR	DATA PROJECTOR
3HA	HEARING AUGMENTATION - GROUP 3
3LEC	LECTERN - GROUP 3
3PRSR	PROJECTOR SCREEN
ACC	AIR CONDITIONING CONTROL
ADJ	ADJUSTABLE SHELF
BH-J	BULKHEAD - JOINERY TYPE
BH-P	BULKHEAD - PLASTERBOARD TYPE
BINI	BIN - INTEGRATED
BWU2	BOILING WATER UNIT - TYPE 2
CAM	CCTV CAMERA
CBD	CUPBOARD
DATA	DATA OUTLET
DR	DRAWER
DRB	DOOR RELEASE BUTTON
EM	EMERGENCY LIGHT
FB	FLOOR BOX
FHC	FULL HEIGHT CUPBOARD
GPO2	POWER OUTLET - DOUBLE
HDMI	HDMI OUTLET
LF1	LIGHT FITTING - REFER TO ELECTRICAL ENGINEER SPECIFICATION
LF3	LIGHT FITTING - TYPE 3
LS	LIGHT SWITCH
LS-D	LIGHT SWITCH - DIMMER
NC	NURSE CALL
S2	SINK - TYPE 2
SK2	SKIRTING - TYPE 2
SMD	SMOKE DETECTOR
SPK	ANUNCIATOR
SPK2	SPEAKER
SPR	SPRINKLER
TAP3	TAP - TYPE 3
WAP	WIRELESS ACCESS POINT

FOR CONSTRUCTION

Revision/Issue		Date
a	Issued for Coordination - 100% DD	2024.04.12
P1	Consolidated Set-to-date / SMG Comments	2025.08.15
P2	ISSUE FOR CONTRACT	2025.10.10
C1	ISSUE FOR CONSTRUCTION - INTERIORS	2026.03.26

ClarkeHopkinsClarke

Melbourne | Wurundjeri
L9, Melbourne Connect
700 Swanston Street
Carlton VIC 3053
Telephone (03) 9419 4340
Email studio@chc.com.au
www.chc.com.au

Sydney | Gadigal Country
Suite 3, Ground Floor
91 Campbell Street
Surry Hills NSW 2010
Telephone (02) 9221 9200
Email studio@chc.com.au
www.chc.com.au

Scale	1 : 50 @ A1
Date	01/03/2024
Drawn	RO / DP
Architect	EL

Project
Summerset Oakleigh
52 Golf Road, Oakleigh South, VIC

Drawing
Internal Elevations - Village Lifestyle - Private Dining & Cinema

Drawing No.
230185/A1807 C1

A1 Use figured dimensions in preference to scale. Verify dimensions at job before shop fabrication. Read drawing in conjunction with specification.

© ClarkeHopkinsClarke