




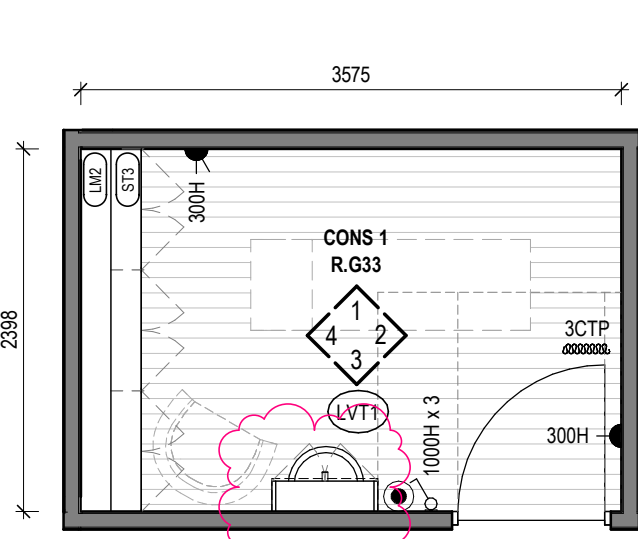


1 VILLAGE HEALTH & WELLNESS - CONSULT 1
Scale 1: 50

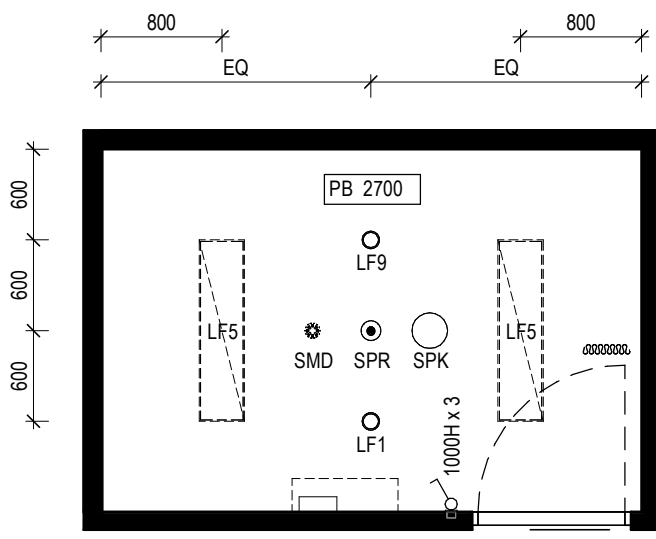


2 RCP - VILLAGE HEALTH & WELLNESS - CONSULT 1
Scale 1: 50

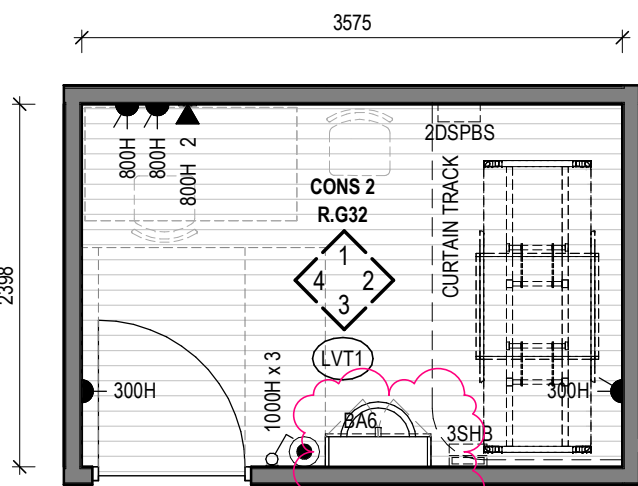


3 VILLAGE HEALTH & WELLNESS - CONSULT 2
Scale 1: 50

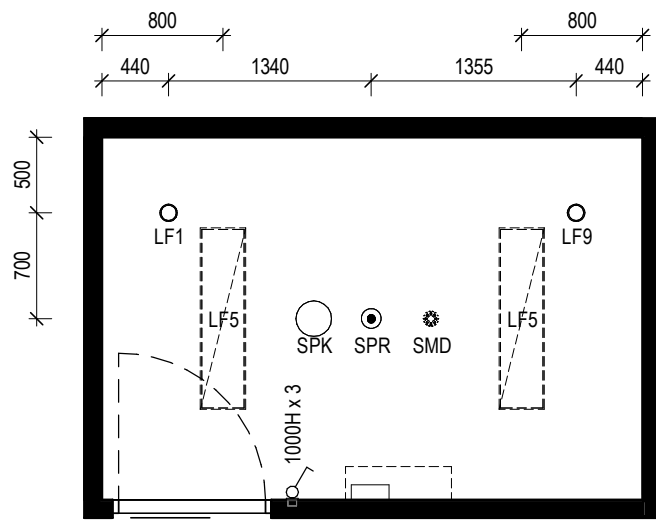


4 RCP - VILLAGE HEALTH & WELLNESS - CONSULT 2
Scale 1: 50

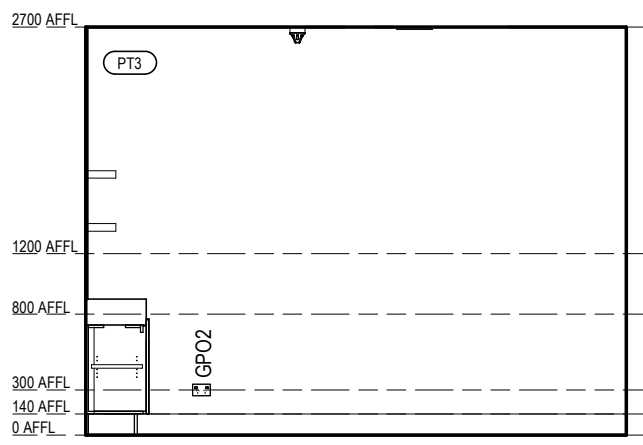


VILLAGE HEALTH & WELLNESS - CONSULT 1
ELEVATION 1
Scale 1: 50

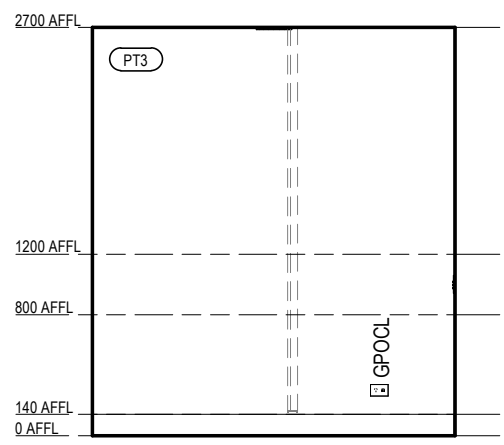


VILLAGE HEALTH & WELLNESS - CONSULT 1
ELEVATION 2
Scale 1: 50

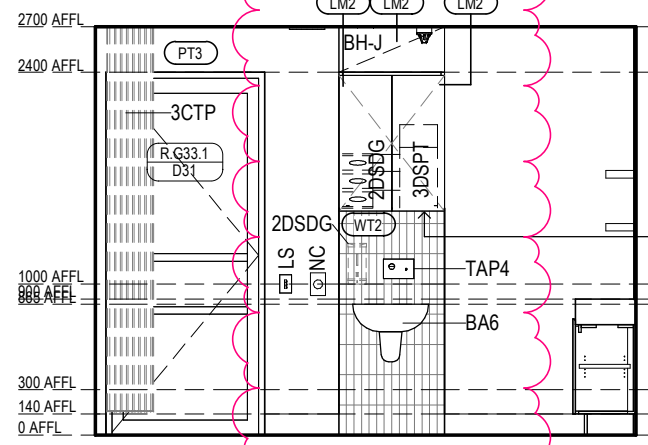


VILLAGE HEALTH & WELLNESS - CONSULT 1
ELEVATION 3
Scale 1: 50

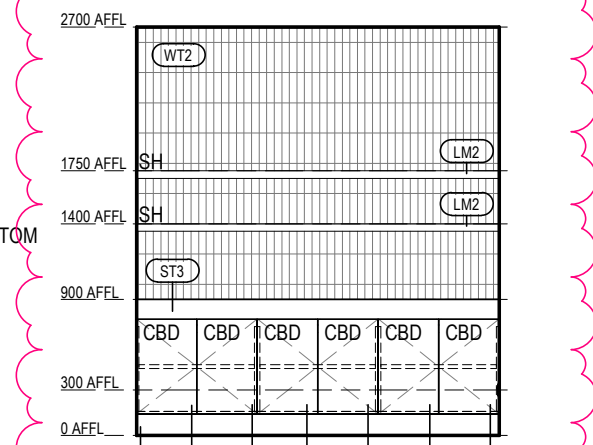


VILLAGE HEALTH & WELLNESS - CONSULT 1
ELEVATION 4
Scale 1: 50

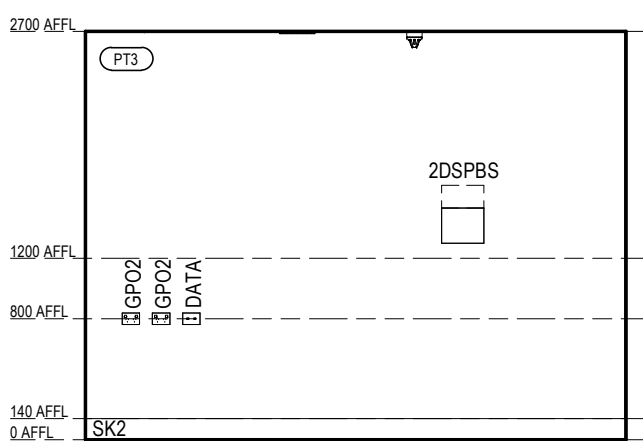


VILLAGE HEALTH & WELLNESS - CONSULT 2
ELEVATION 1
Scale 1: 50

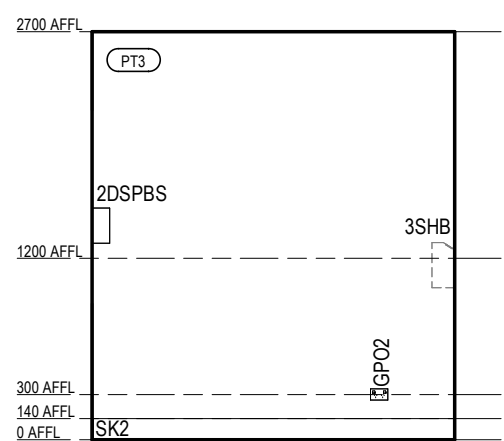

VILLAGE HEALTH & WELLNESS - CONSULT 2
ELEVATION 2
Scale 1: 50

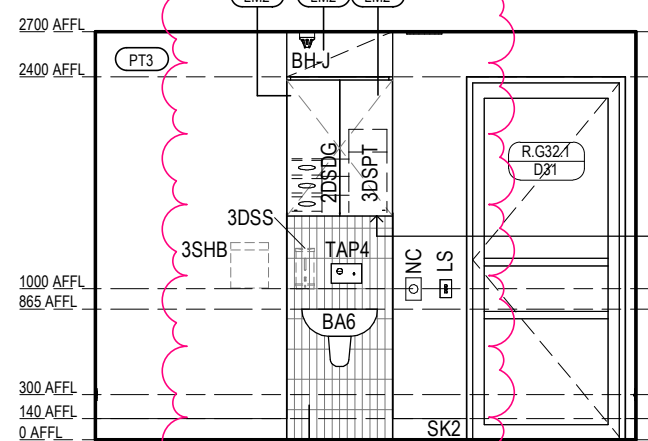

VILLAGE HEALTH & WELLNESS - CONSULT 2
ELEVATION 3
Scale 1: 50

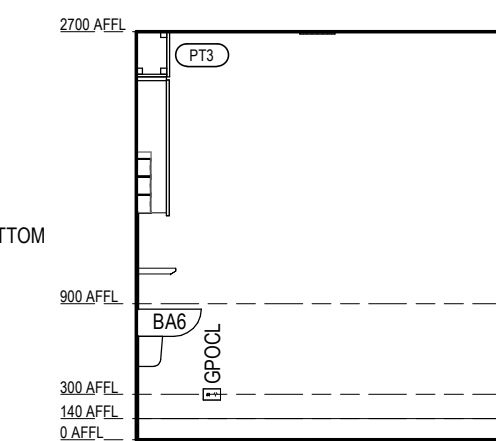

VILLAGE HEALTH & WELLNESS - CONSULT 2
ELEVATION 4
Scale 1: 50

Legend - Internal Elevations

DRAWINGS TO BE READ IN CONJUNCTION WITH ARCHITECTURAL SPECIFICATION & MATERIALS, PRODUCTS & FINISHES SCHEDULE.

PT# PAINT FINISH TO ALL WALLS WITHIN NEW & AFFECTED ROOMS/ AREAS UNLESS OTHERWISE SHOWN

- | | |
|-----|-----------------|
| CSE | CONCRETE SEALER |
| DPR | DOOR PROTECTION |
| GD | GRAPHIC FILM |
| LM | LAMINATE |
| MI | MIRROR |
| PBD | PINBOARD |
| PT | PAINT FINISH |
| REN | RENDER FINISH |
| SB | SPLASHBACK |
| ST | STONE |
| WB | WHITEBOARD |
| WP | WALL PROTECTION |
| WT | WALL TILE |
| WV | WALL VINYL |

NOTES:
1. LAMINATE CARCASS FOR ALL VISIBLE OPEN SHELVING, UNLESS OTHERWISE NOTED
2. MELAMINETO ALL INTERNAL CARCASS OF JOINERY, UNLESS OTHERWISE NOTED.

Legend - Floor Finishes

- | | |
|-----|----------------------------------|
| C | CARPET |
| CO | CONCRETE |
| E | EPOXY FINISH |
| L | LINOLEUM |
| M | MATTING |
| PU | PAVING UNIT - TBC WITH LANDSCAPE |
| R | RUBBER FLOORING |
| T | TILING |
| TF | TIMBER FLOORING |
| V | VINYL |
| LVT | LUXURY VINYL TILE PLANK |

Keynote Legend

- | | |
|--------|--|
| 2DSOG | DISPENSER - DISPOSABLE GLOVE - GROUP 2 |
| 2DSPBS | BEDSHEET DISPENSER - GROUP 2 |
| 3CTP | CURTAINS - GROUP 3 |
| 3DSPT | DISPENSER - PAPER TOWEL - GROUP 3 |
| 3DSS | SOAP DISPENSER - GROUP 3 |
| 3SHB | BIN SHARPS - GROUP 3 |
| BA6 | BASIN - TYPE 6 |
| BH-J | BULKHEAD - JOINERY TYPE |
| CBD | CUPBOARD |
| DATA | DATA OUTLET |
| GPO2 | POWER OUTLET - DOUBLE |
| GPOOL | POWER OUTLET - CLEANERS |
| LF1 | LIGHT FITTING - REFER TO ELECTRICAL ENGINEER SPECIFICATION |
| LF5 | LIGHT FITTING - TYPE 5 |
| LF9 | |
| LS | LIGHT SWITCH |
| NC | NURSE CALL |
| SH | SHELF |
| SK2 | SKIRTING - TYPE 2 |
| SMD | SMOKE DETECTOR |
| SPK | ANUNCIATOR |
| SPR | SPRINKLER |
| TAP4 | TAP - TYPE 4 |

FOR CONSTRUCTION

Revision/Issue
C1 ISSUE FOR CONSTRUCTION - INTERIORS
Date
2026.03.26

Clarke
Hopkins
Clarke

ClarkeHopkinsClarke
Melbourne | Wurundjeri
L9, Melbourne Connect
700 Swanston Street
Carlton VIC 3063
Telephone (03) 9419 4340
Email studio@chc.com.au
www.chc.com.au

Sydney | Gadigal Country
Suite 3, Ground Floor
91 Campbell Street
Sunny Hills NSW 2010
Telephone (02) 9221 9200
Email studio@chc.com.au
www.chc.com.au

Scale
Date
Drawn
Architect
1: 50 @ A1
01/03/2024
TM
EL

Project
Summerset Oakleigh
52 Golf Road, Oakleigh South, VIC

Drawing
Internal Elevations - Village Health & Wellness - Consult

Drawing No.
230185/A1809
C1