



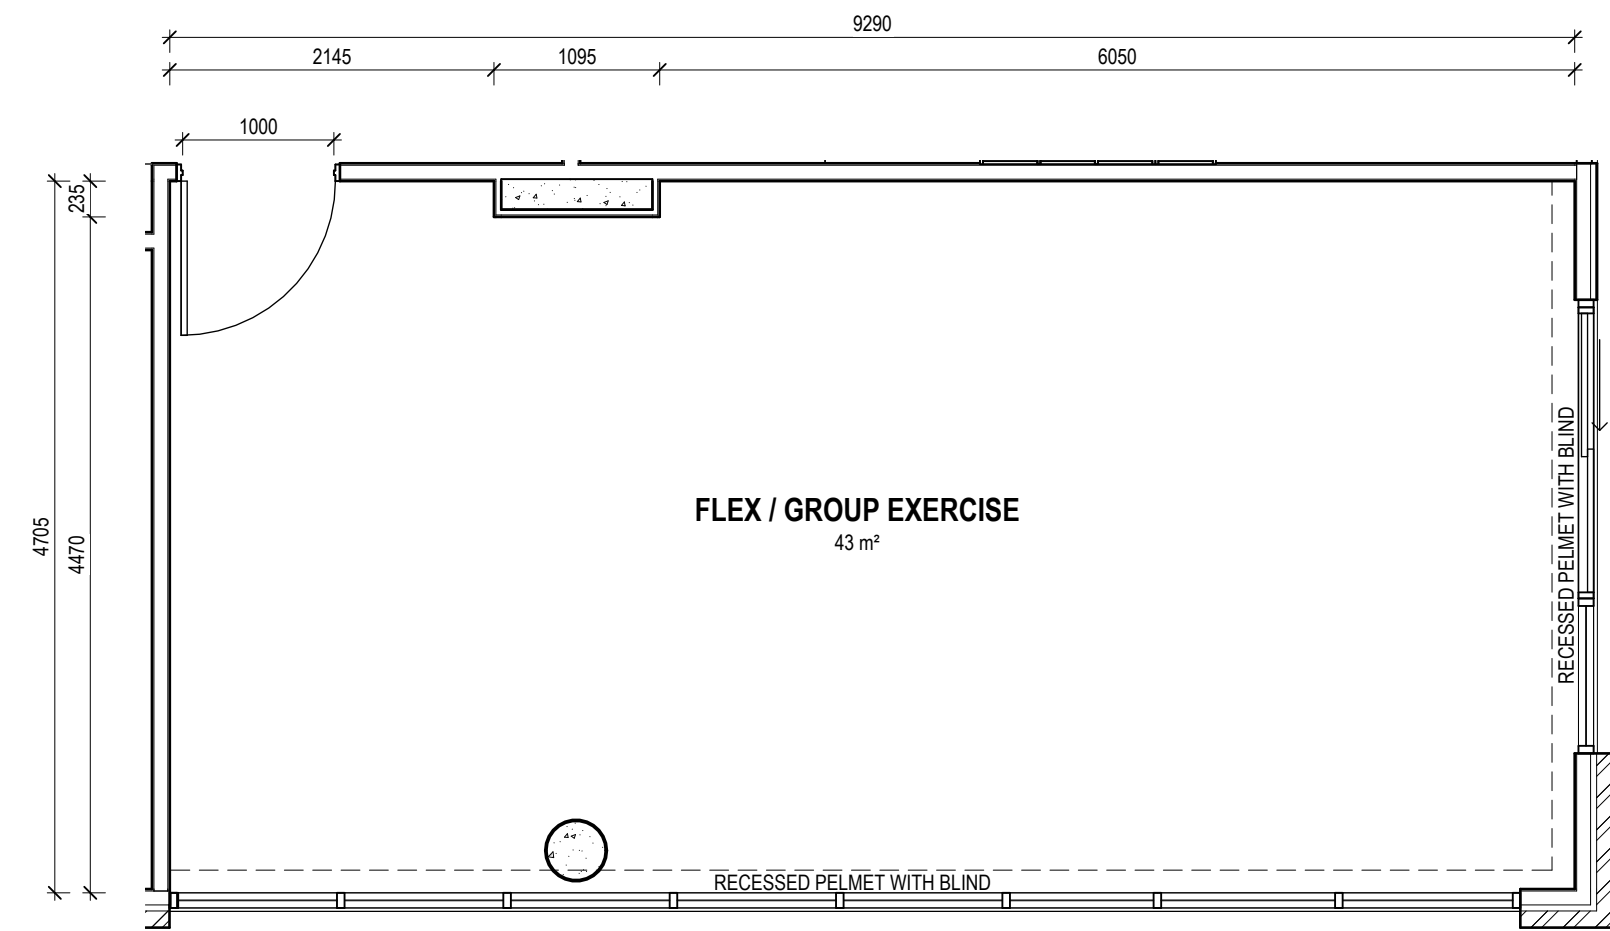


VILLAGE HEALTH & WELLNESS - FLEX/GROUP EXERCISE
Scale 1 : 50

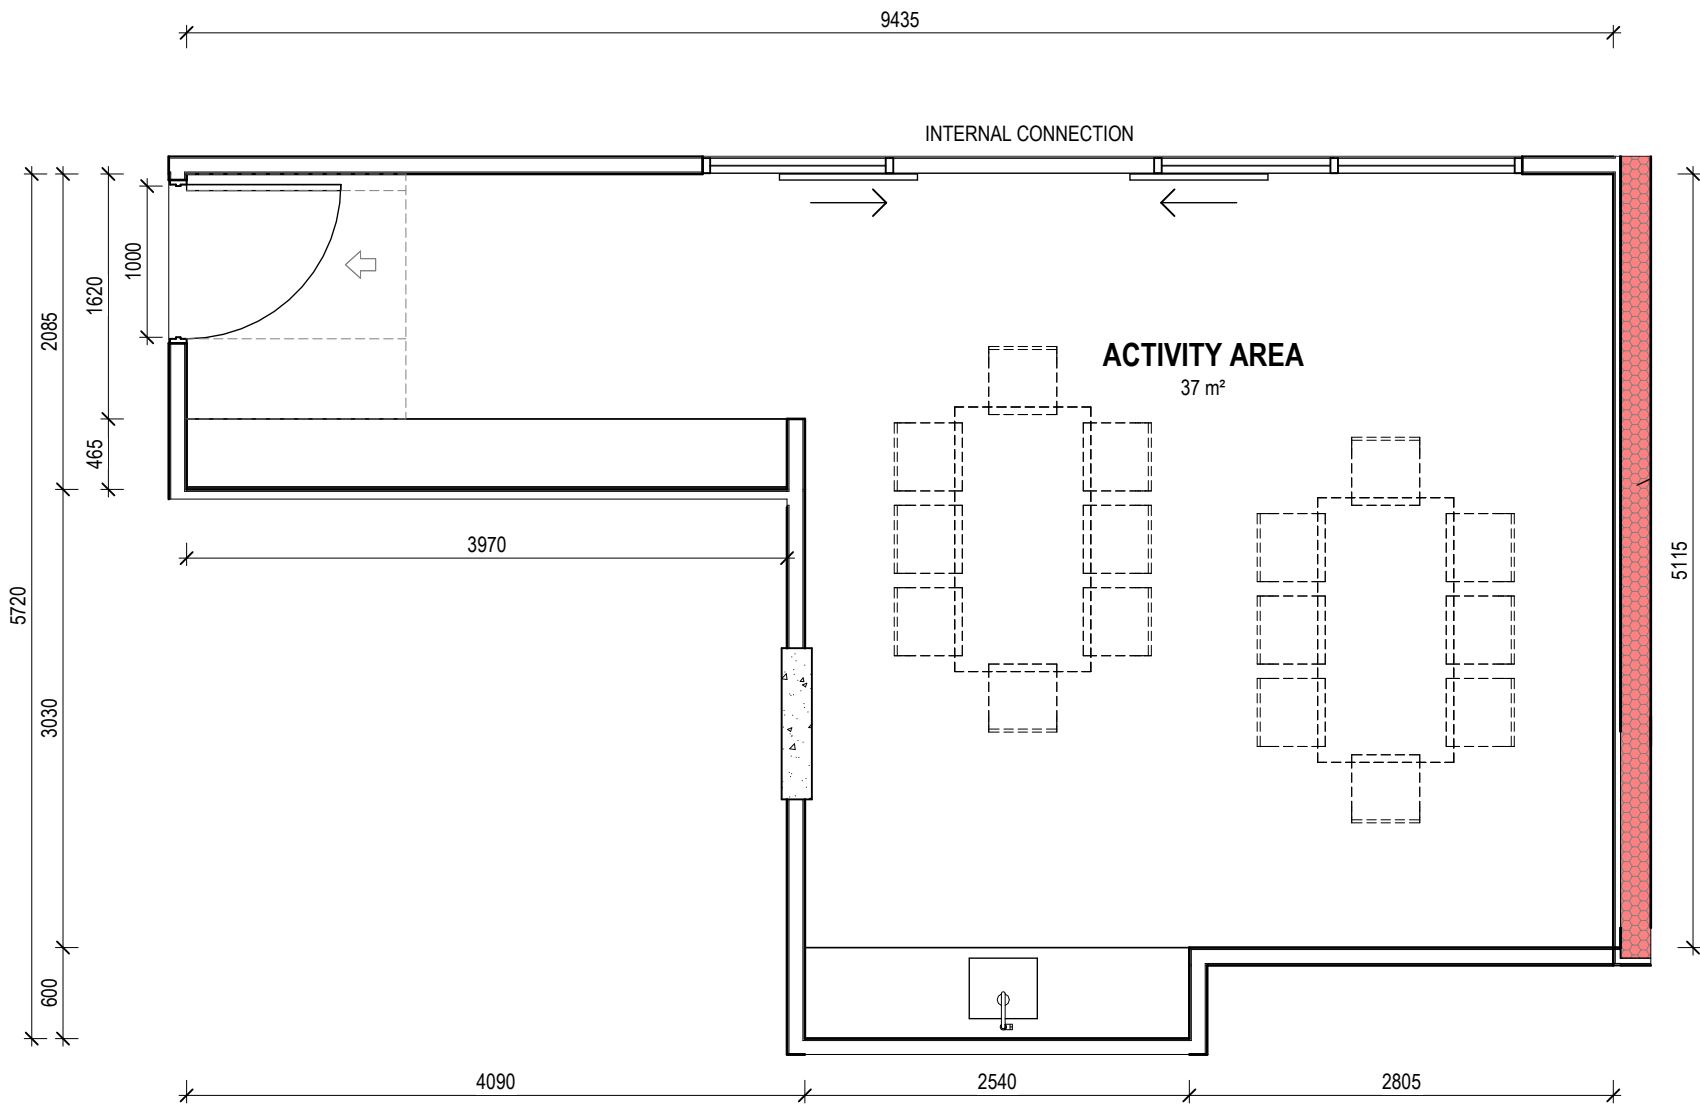

VILLAGE COMMUNAL - ACTIVITY AREA
Scale 1 : 50

Revision/Issue	Date
A Issued for Coordination - 100% DD	2024.04.12

 

**Clarke
Hopkins
Clarke**

ClarkeHopkinsClarke
Melbourne
L9, Melbourne Connect
700 Swanston Street
Carlton Victoria 3053
Telephone (03) 9419 4340
Email studio@chc.com.au
www.chc.com.au

Sydney
3/78 Campbell Street
Sunny Hills NSW 2010
Telephone (02) 9221 9200
Email studio@chc.com.au
www.chc.com.au

Scale	1 : 50 @ A1
Date	
Drawn	
Architect	

Project	Summerset Oakleigh 52 Golf Road, Oakleigh South, VIC
---------	---

Drawing	Internal Elevations - Village Health & Wellness - Sheet 2
---------	--

Drawing No.	230185/A1811	A
-------------	--------------	---

PRELIMINARY