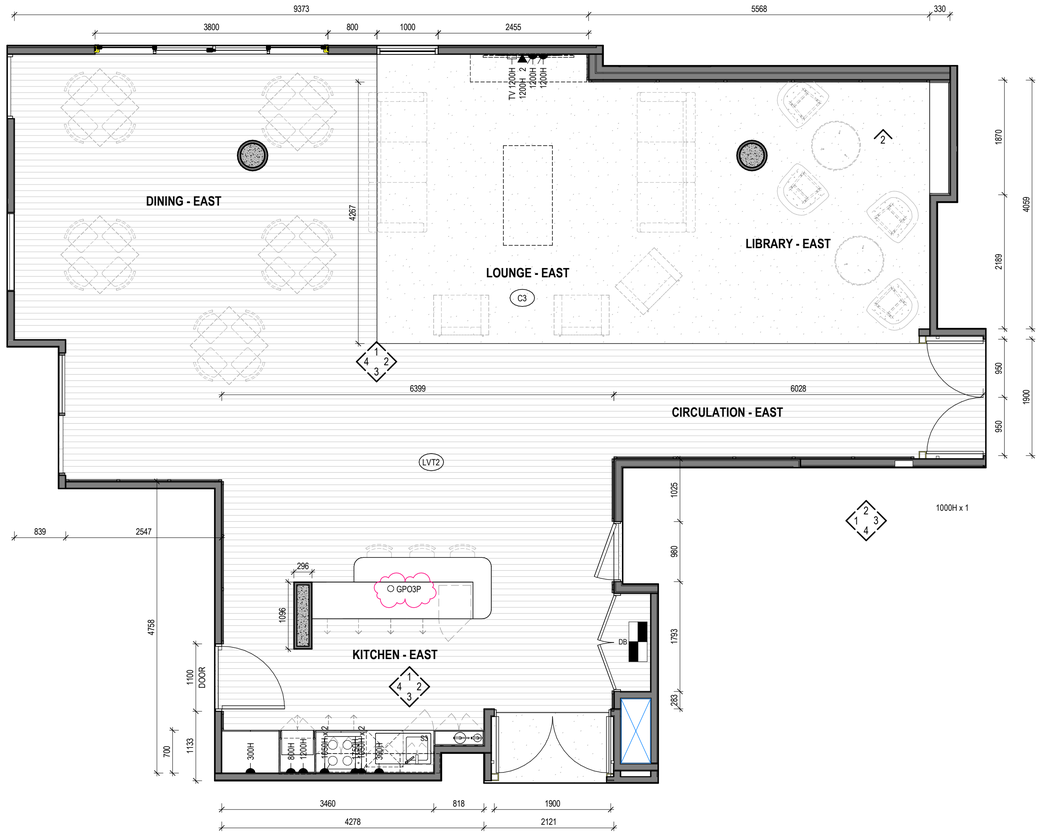

1 RACF Communal Kitchen_Living_Dining - East
Scale 1 : 50

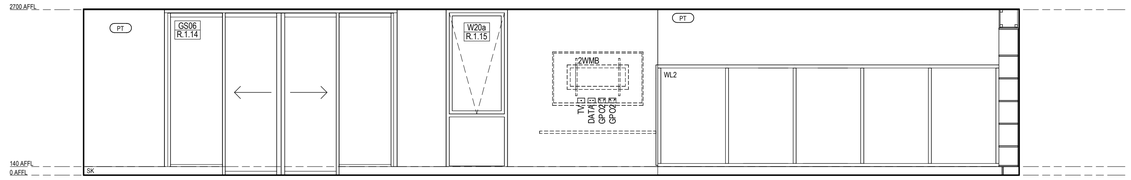

RACF Communal Living, Dining and Library - East - Elevation 1
ELEVATION 1
Scale 1 : 50

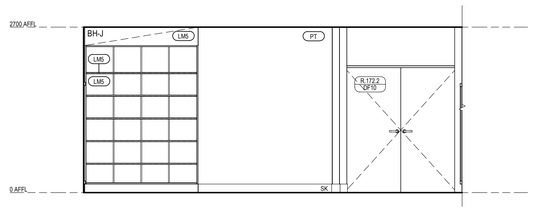

RACF Communal Living, Dining and Library - East - Elevation 2
ELEVATION 2
Scale 1 : 50

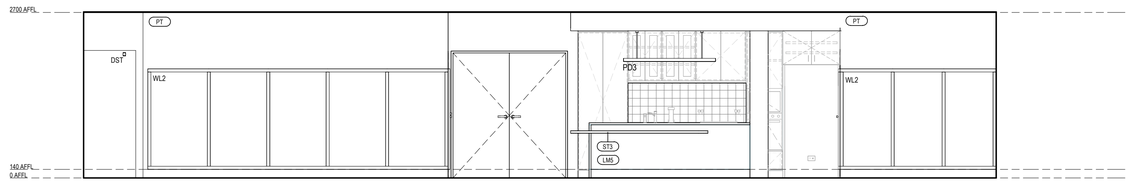

RACF Communal Living, Dining and Library - East - Elevation 3
ELEVATION 3
Scale 1 : 50

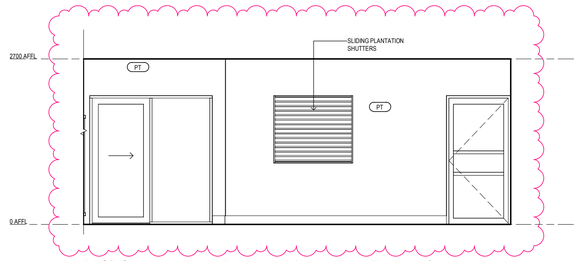

RACF Communal Living, Dining and Library - East - Elevation 4
ELEVATION 4
Scale 1 : 50

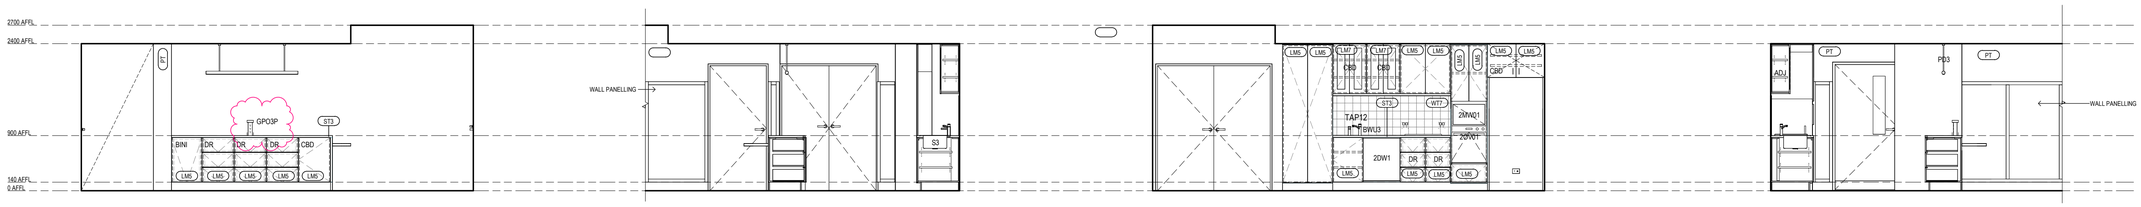

RACF Resident Kitchen - East - Elevation 1
ELEVATION 1
Scale 1 : 50

RACF Resident Kitchen - East - Elevation 2
ELEVATION 2
Scale 1 : 50

RACF Resident Kitchen - East - Elevation 3
ELEVATION 3
Scale 1 : 50

RACF Resident Kitchen - East - Elevation 4
ELEVATION 4
Scale 1 : 50

Legend - Internal Elevations

DRAWINGS TO BE READ IN CONJUCTION WITH ARCHITECTURAL SPECIFICATION & MATERIALS, PRODUCTS & FINISHES SCHEDULE.

PT# PAINT FINISH TO ALL WALLS WITHIN NEW & AFFECTED ROOMS/ AREAS UNLESS OTHERWISE SHOWN

CSE	CONCRETE SEALER
DPR	DOOR PROTECTION
GD	GRAPHIC FILM
LM	LAMINATE
MI	MIRROR
PBD	PINBOARD
PT	PAINT FINISH
REN	RENDER FINISH
SB	SPLASHBACK
ST	STONE
WB	WHITEBOARD
WP	WALL PROTECTION
WT	WALL TILE
WV	WALL VINYL

NOTES:
1. LAMINATE CARCASS FOR ALL VISIBLE OPEN SHELVING, UNLESS OTHERWISE NOTED
2. MELAMINETO ALL INTERNAL CARCASS OF JOINERY, UNLESS OTHERWISE NOTED.

Legend - Floor Finishes

C	CARPET
CO	CONCRETE
E	EPOXY FINISH
L	LINOLEUM
M	MATTING
PU	PAVING UNIT - TBC WITH LANDSCAPE
R	RUBBER FLOORING
T	TILING
TF	TIMBER FLOORING
V	VINYL
LVT	LUXURY VINYL TILE PLANK

PROTECTION RAILS OR CRASH RAILS - REFER TO MATERIAL SCHEDULE FOR DETAILS

WL1- REFER TO MATERIAL SCHEDULE FOR DETAILS

WL2 - REFER TO MATERIAL SCHEDULE FOR DETAILS

NOTE:

FALLS TO ALL FLOOR WASTES IN ACCORDANCE WITH AS 3740.

Keynote Legend

2DW1	DISHWASHER - TYPE 1 - GROUP 2
2MW01	MICROWAVE - TYPE 1 - GROUP 2
2OV01	OVEN - TYPE 1 - GROUP 2
2WMB	TV WALL MOUNTED BRACKET - GROUP 2
ADJ	ADJUSTABLE SHELF
BH-J	BULKHEAD - JOINERY TYPE
BINI	BIN - INTEGRATED
BWU3	BOILING WATER UNIT - TYPE 3
CBD	CUPBOARD
DATA	DATA OUTLET
DB	DISTRIBUTION BOARD
DR	DRAWER
DST	DOOR STOP
GPO2	POWER OUTLET - DOUBLE
GPO3P	POWER OUTLET - TRIPLE, PEDESTAL - REF. SERVICES
PD3	PENDANT LIGHT - TYPE 3
S3	SINK - TYPE 3
TAP12	TAP - TYPE 12
TV	TELEVISION COAXIAL OUTLET
WL2	WALL PANELLING - TYPE 2

FOR CONSTRUCTION

Revision/Issue		Date
P1	Preliminary Internal Elevations - RACF	2025.08.08
P2	Consolidated Set-to-date / SMG Comments	2025.08.15
P3	ISSUE FOR CONTRACT	2025.10.10
C1	ISSUE FOR CONSTRUCTION - INTERIORS	2026.03.30

ClarkeHopkinsClarke

Melbourne | Wurundjeri
L9, Melbourne Connect
700 Swanston Street
Carlton VIC 3053
Telephone (03) 9419 4340
Email studio@chc.com.au
www.chc.com.au

Sydney | Gadigal Country
Suite 3, Ground Floor
91 Campbell Street
Surry Hills NSW 2010
Telephone (02) 9221 9200
Email studio@chc.com.au
www.chc.com.au

Scale	As indicated @ A1
Date	01/03/2024
Drawn	
Architect	

Project
Summerset Oakleigh
52 Golf Road, Oakleigh South, VIC

Drawing
Internal Elevations - RACF Communal - Kitchen, Living & Dining - East

Drawing No.
230185/A1817 C1

A1 Use figured dimensions in preference to scale. Verify dimensions at job before shop fabrication. Read drawing in conjunction with specification.

© ClarkeHopkinsClarke