


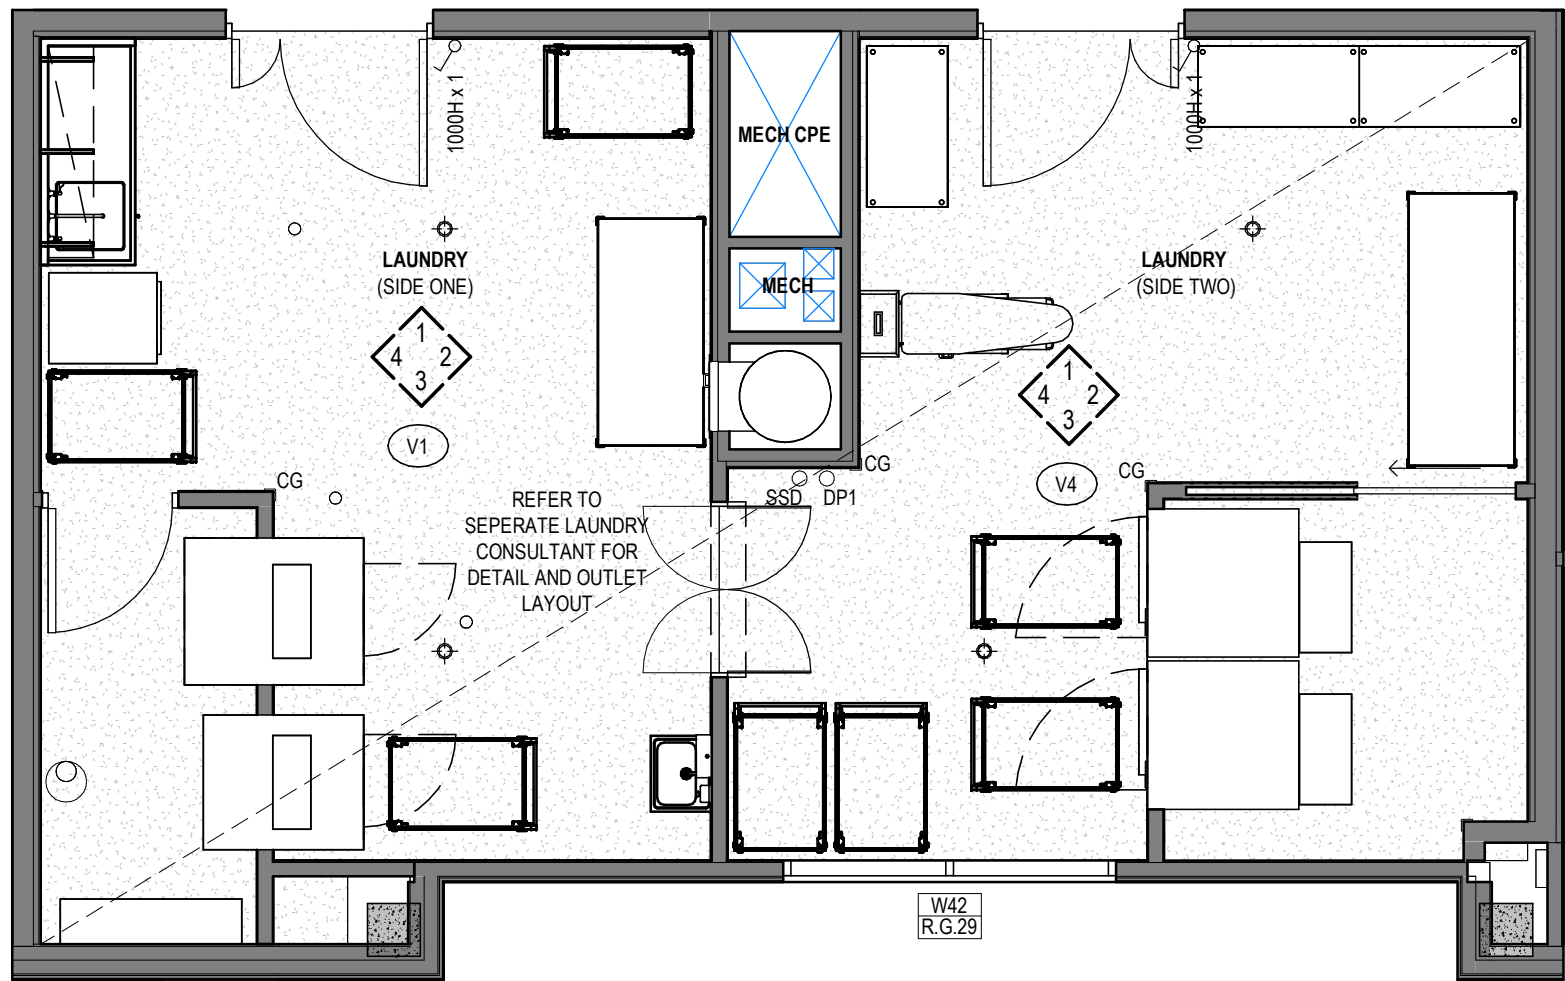

1 LAUNDRY
Scale 1 : 50

Legend - Internal Elevations

DRAWINGS TO BE READ IN CONJUNCTION WITH ARCHITECTURAL SPECIFICATION & MATERIALS, PRODUCTS & FINISHES SCHEDULE.

PT# PAINT FINISH TO ALL WALLS WITHIN NEW & AFFECTED ROOMS/ AREAS UNLESS OTHERWISE SHOWN

- CSE CONCRETE SEALER
- DPR DOOR PROTECTION
- GD GRAPHIC FILM
- LM LAMINATE
- MI MIRROR
- PBD PINBOARD
- PT PAINT FINISH
- REN RENDER FINISH
- SB SPLASHBACK
- ST STONE
- WB WHITEBOARD
- WP WALL PROTECTION
- WT WALL TILE
- WV WALL VINYL


NOTES:
1. LAMINATE CARCASS FOR ALL VISIBLE OPEN SHELVING, UNLESS OTHERWISE NOTED.
2. MELAMINETO ALL INTERNAL CARCASS OF JOINERY, UNLESS OTHERWISE NOTED.

Legend - Floor Finishes

- C CARPET
- CO CONCRETE
- E EPOXY FINISH
- L LINOLEUM
- M MATTING
- PU PAVING UNIT - TBC WITH LANDSCAPE
- R RUBBER FLOORING
- T TILING
- TF TIMBER FLOORING
- V VINYL
- LVT LUXURY VINYL TILE PLANK


Keynote Legend

- CG CORNER GAURO
- DP1 DOWNPIPE - TYPE 1
- LS LIGHT SWITCH
- SKC SKIRTING - COVED
- SSD SEWER STACK DOWNPIPE

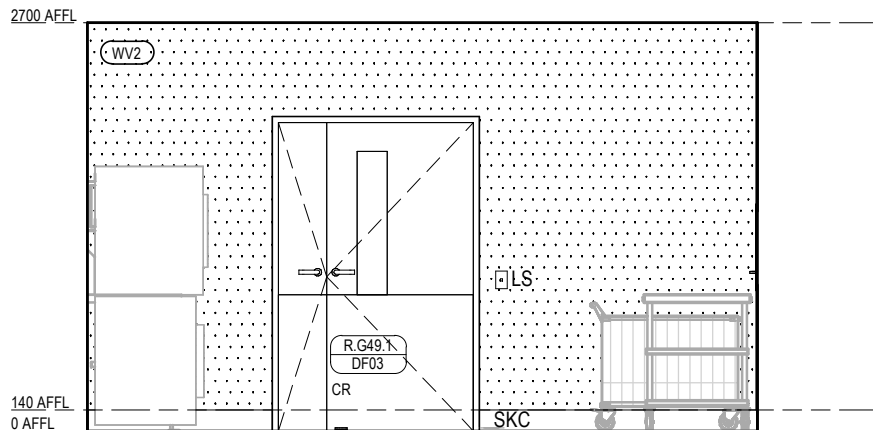


LAUNDRY SIDE 1
ELEVATION 1
Scale 1 : 50

NOTE: REFER LAUNDRY CONSULTANT FOR FURTHER EQUIPMENT DETAIL.
REFER LAUNDRY CONSULTANT & ELECTRICAL FOR OUTLET LAYOUT

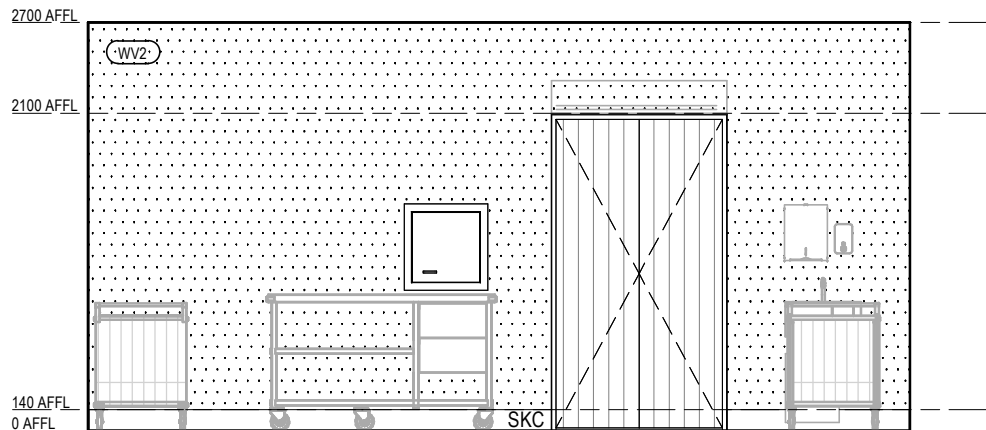


LAUNDRY SIDE 1
ELEVATION 2
Scale 1 : 50

NOTE: REFER LAUNDRY CONSULTANT FOR FURTHER EQUIPMENT DETAIL.
REFER LAUNDRY CONSULTANT & ELECTRICAL FOR OUTLET LAYOUT

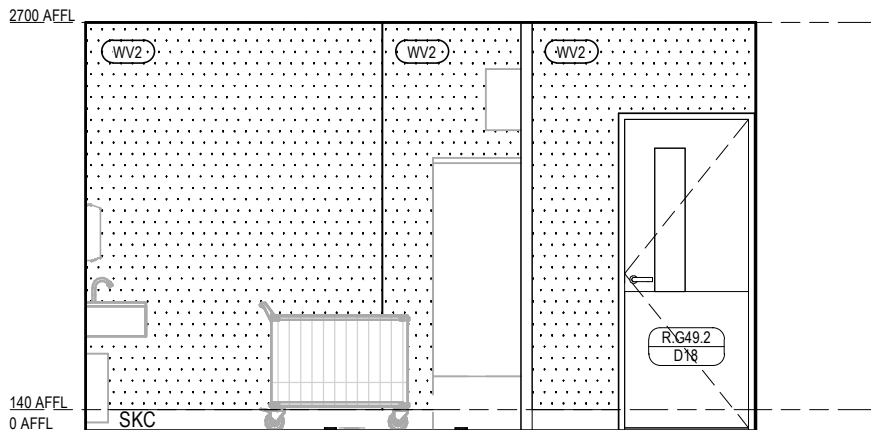


LAUNDRY SIDE 1
ELEVATION 3
Scale 1 : 50

NOTE: REFER LAUNDRY CONSULTANT FOR FURTHER EQUIPMENT DETAIL.
REFER LAUNDRY CONSULTANT & ELECTRICAL FOR OUTLET LAYOUT

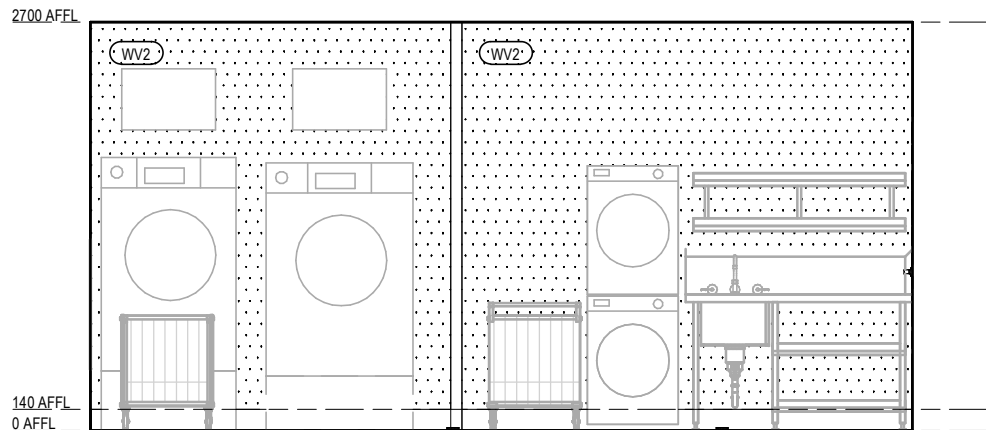


LAUNDRY SIDE 1
ELEVATION 4
Scale 1 : 50

NOTE: REFER LAUNDRY CONSULTANT FOR FURTHER EQUIPMENT DETAIL.
REFER LAUNDRY CONSULTANT & ELECTRICAL FOR OUTLET LAYOUT

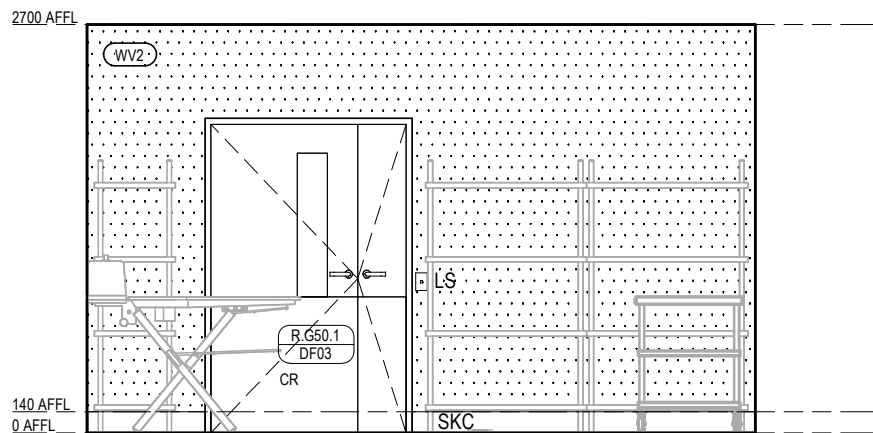


LAUNDRY SIDE 2
ELEVATION 1
Scale 1 : 50

NOTE: REFER LAUNDRY CONSULTANT FOR FURTHER EQUIPMENT DETAIL.
REFER LAUNDRY CONSULTANT & ELECTRICAL FOR OUTLET LAYOUT

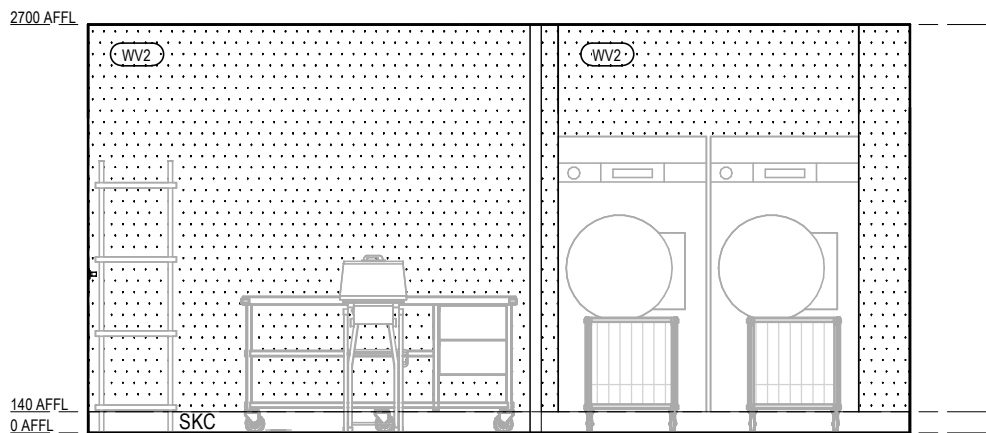


LAUNDRY SIDE 2
ELEVATION 2
Scale 1 : 50

NOTE: REFER LAUNDRY CONSULTANT FOR FURTHER EQUIPMENT DETAIL.
REFER LAUNDRY CONSULTANT & ELECTRICAL FOR OUTLET LAYOUT

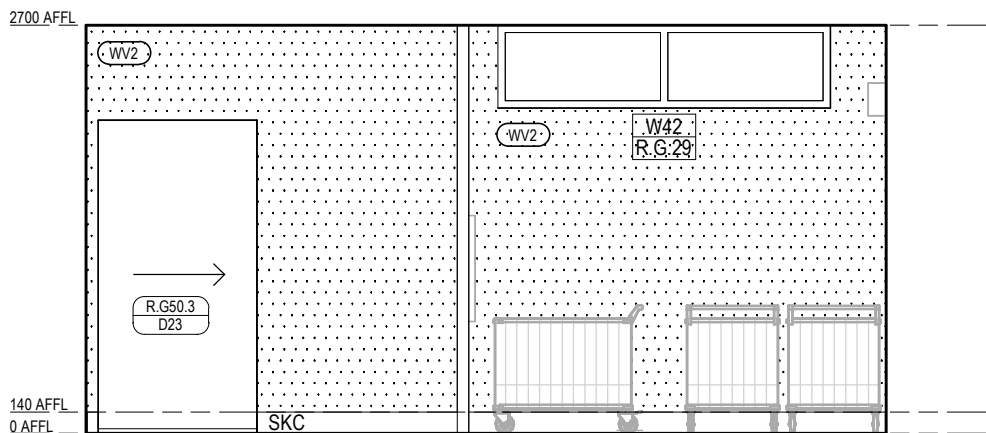

LAUNDRY SIDE 2
ELEVATION 3
Scale 1 : 50

NOTE: REFER LAUNDRY CONSULTANT FOR FURTHER EQUIPMENT DETAIL.
REFER LAUNDRY CONSULTANT & ELECTRICAL FOR OUTLET LAYOUT

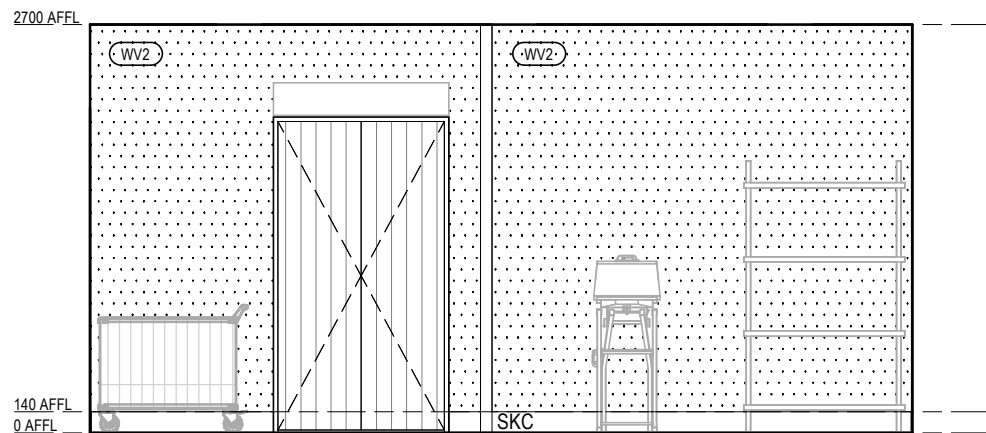

LAUNDRY SIDE 2
ELEVATION 4
Scale 1 : 50

NOTE: REFER LAUNDRY CONSULTANT FOR FURTHER EQUIPMENT DETAIL.
REFER LAUNDRY CONSULTANT & ELECTRICAL FOR OUTLET LAYOUT

FOR CONSTRUCTION

Revision/Issue
C1 ISSUE FOR CONSTRUCTION - INTERIORS
Date
2026.03.26

Clarke
Hopkins
Clarke

ClarkeHopkinsClarke
Melbourne | Wurundjeri
L3, Melbourne Connect
700 Swanston Street
Carlton VIC 3063
Telephone (03) 9419 4340
Email studio@chc.com.au
www.chc.com.au

Sydney | Gadigal Country
Suite 3, Ground Floor
91 Campbell Street
Surry Hills NSW 2010
Telephone (02) 9221 9200
Email studio@chc.com.au
www.chc.com.au

Scale
Date
Drawn
Architect
As indicated @ A1
01/03/2024
TM
EL

Project
Summerset Oakleigh
52 Golf Road, Oakleigh South, VIC

Drawing
Internal Elevations - RACF BOH -
LAUNDRY

Drawing No.
230185/A1823
C1