



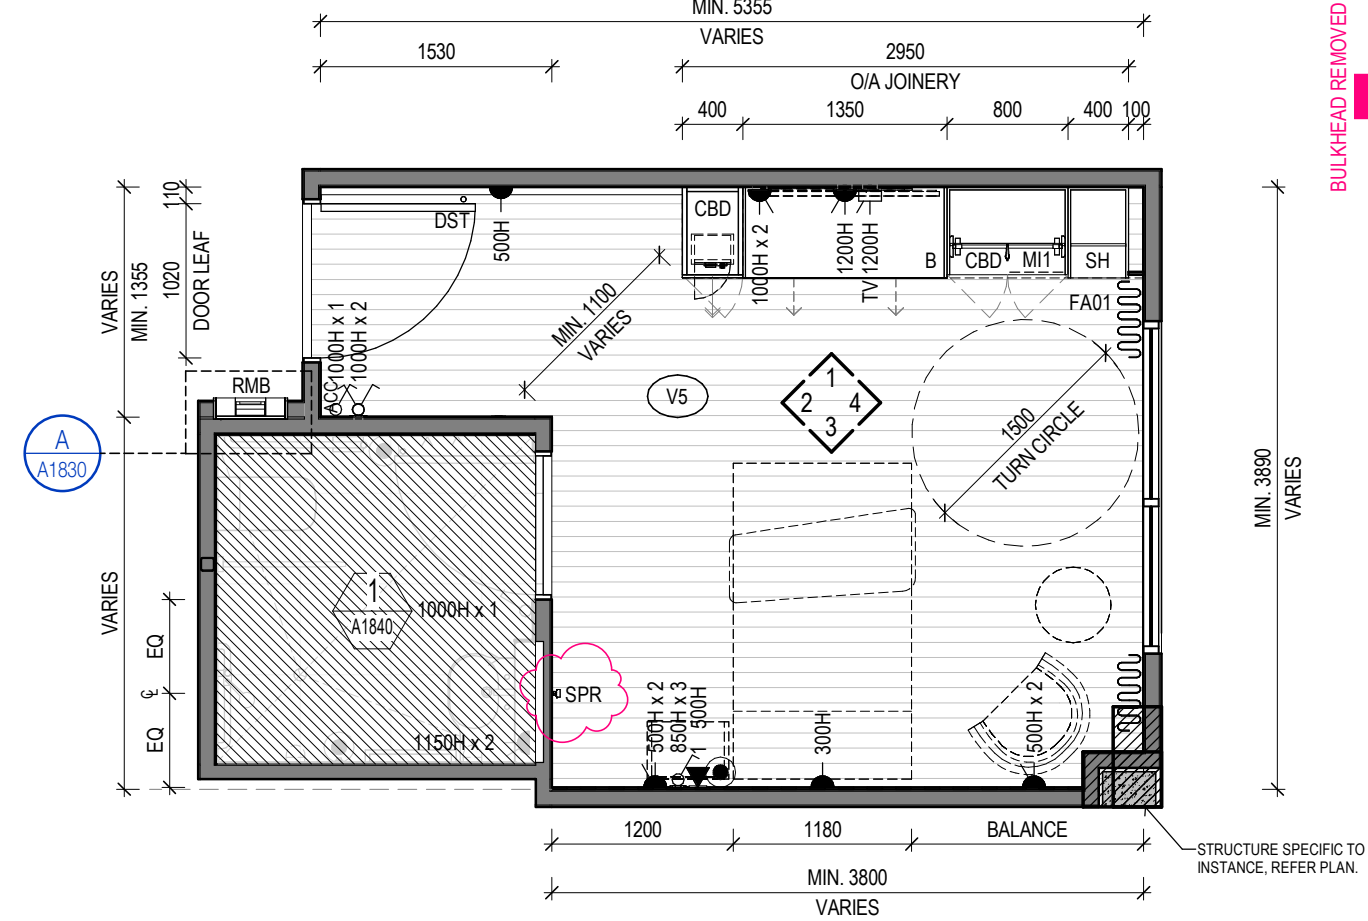


1 RACF STANDARD BEDROOM - TYPE A
Scale 1 : 50

Standard Type A	
Level	Room Number
RACF_Level 1	RM 107
RACF_Level 1	RM 106
RACF_Level 1	RM 119
RACF_Level 1	RM 121
RACF_Level 1	RM 123
RACF_Level 1	RM 115
RACF_Level 1	RM 117
RACF_Level 2	RM 207
RACF_Level 2	RM 212
RACF_Level 2	RM 206
RACF_Level 2	RM 219
RACF_Level 2	RM 221
RACF_Level 2	RM 223
RACF_Level 2	RM 225
RACF_Level 2	RM 227
RACF_Level 2	RM 215
RACF_Level 2	RM 217
S BED (A): 17	


Standard Type A Mirrored	
Level	Room Number
RACF_Level 1	RM 108
RACF_Level 1	RM 120
RACF_Level 1	RM 122
RACF_Level 1	RM 128
RACF_Level 1	RM 126
RACF_Level 1	RM 114
RACF_Level 1	RM 116
RACF_Level 1	RM 205
RACF_Level 2	RM 211
RACF_Level 2	RM 208
RACF_Level 2	RM 220
RACF_Level 2	RM 222
RACF_Level 2	RM 228
RACF_Level 2	RM 226
RACF_Level 2	RM 214
RACF_Level 2	RM 218
RACF_Level 2	RM 216
S BED (A MIR): 18	

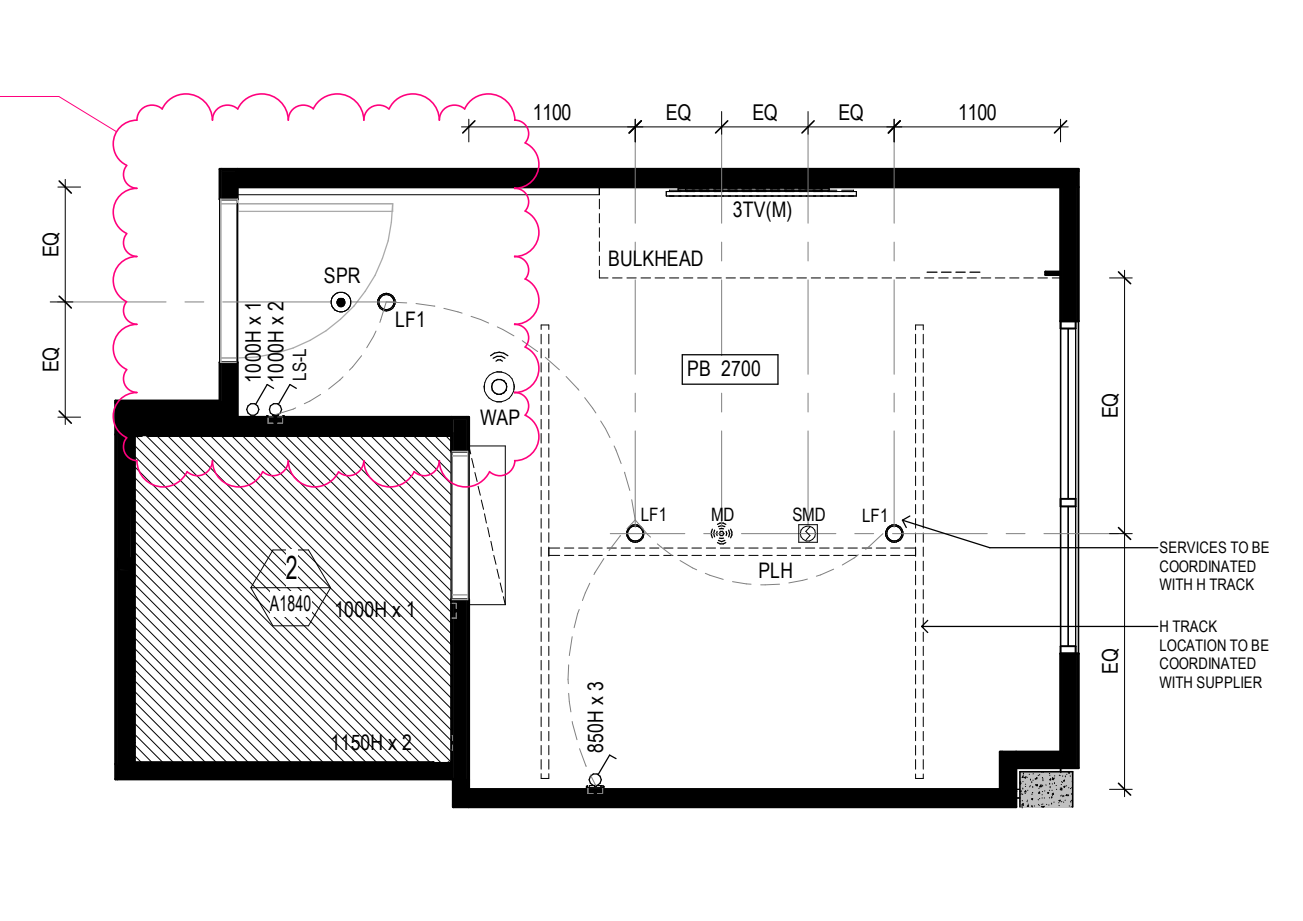


2 RCP-STANDARD BEDROOM - TYPE A
Scale 1 : 50

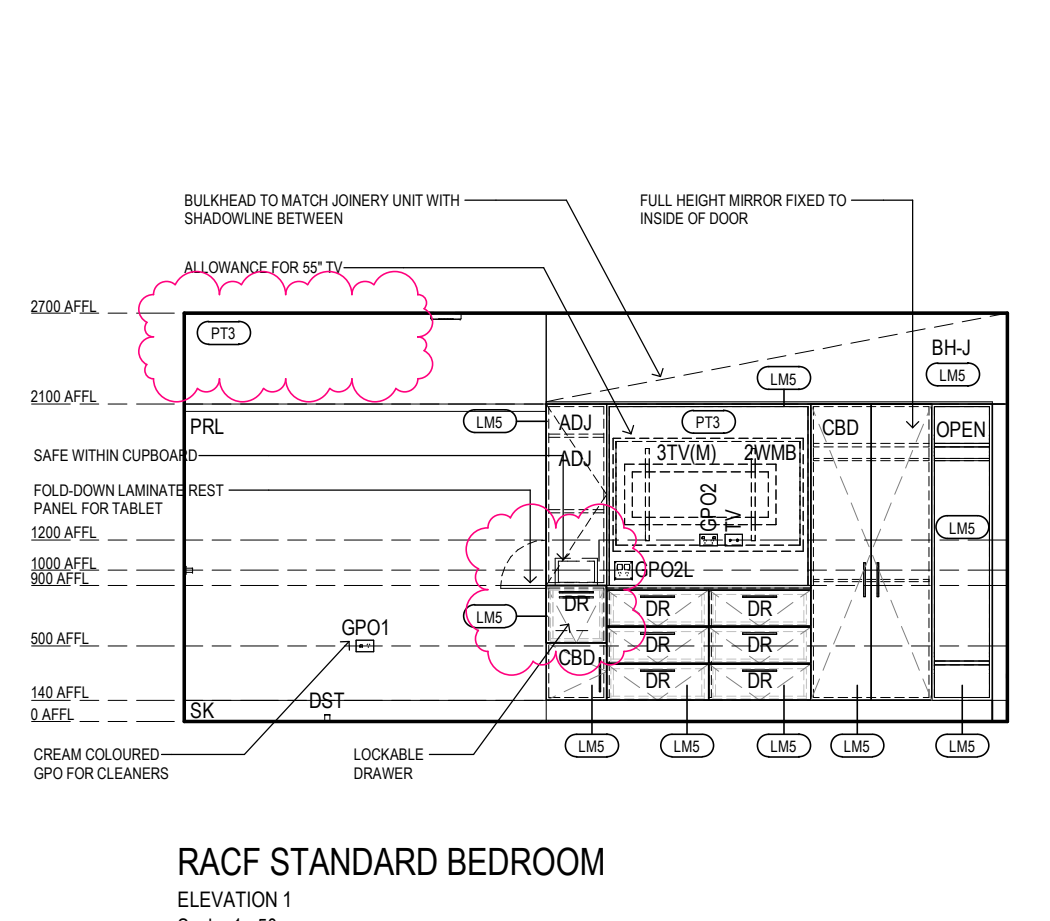


RACF STANDARD BEDROOM
ELEVATION 1
Scale 1 : 50

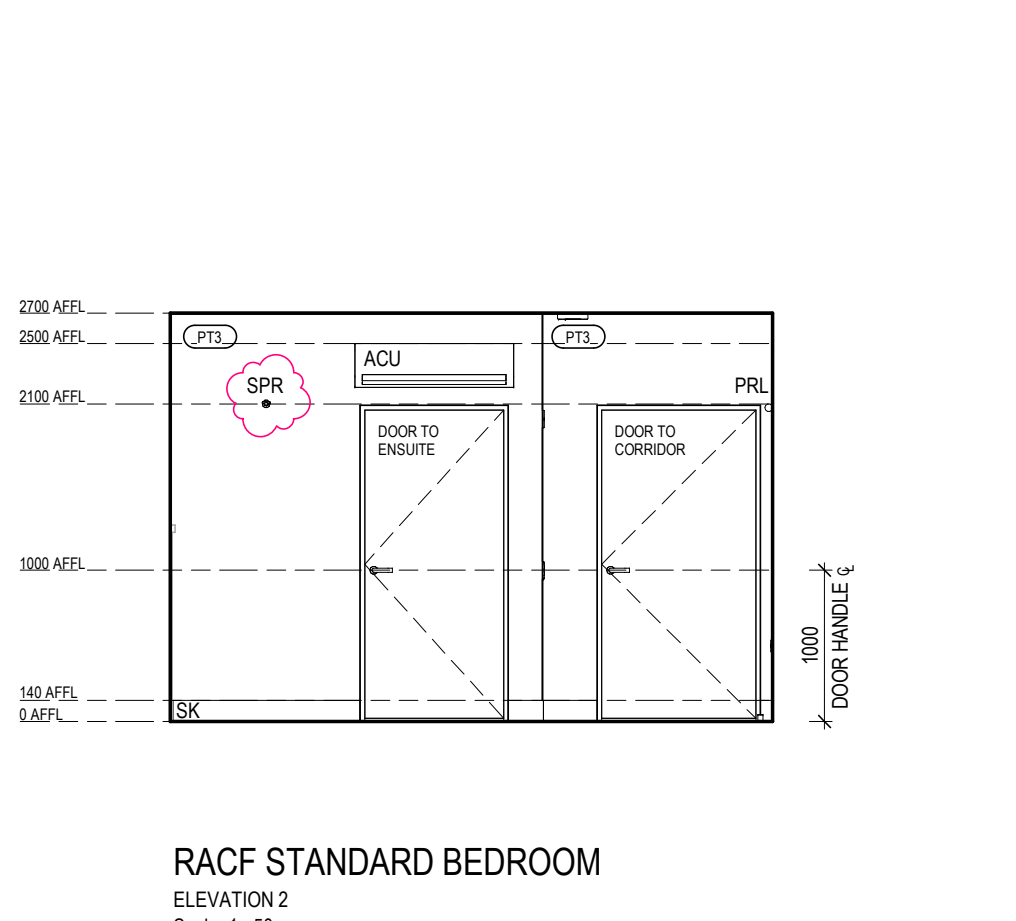


RACF STANDARD BEDROOM
ELEVATION 2
Scale 1 : 50

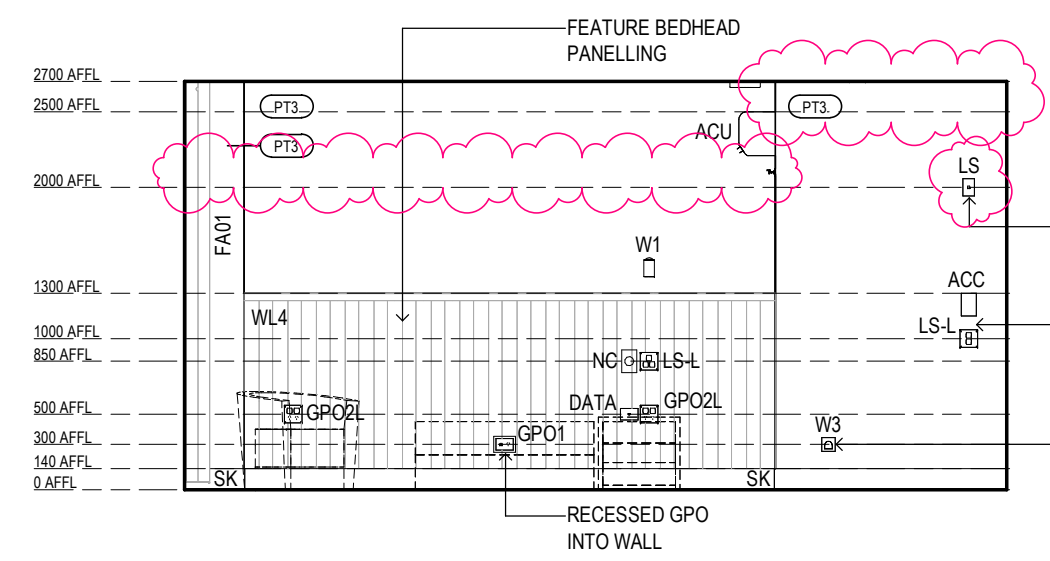

RACF STANDARD BEDROOM
ELEVATION 3
Scale 1 : 50

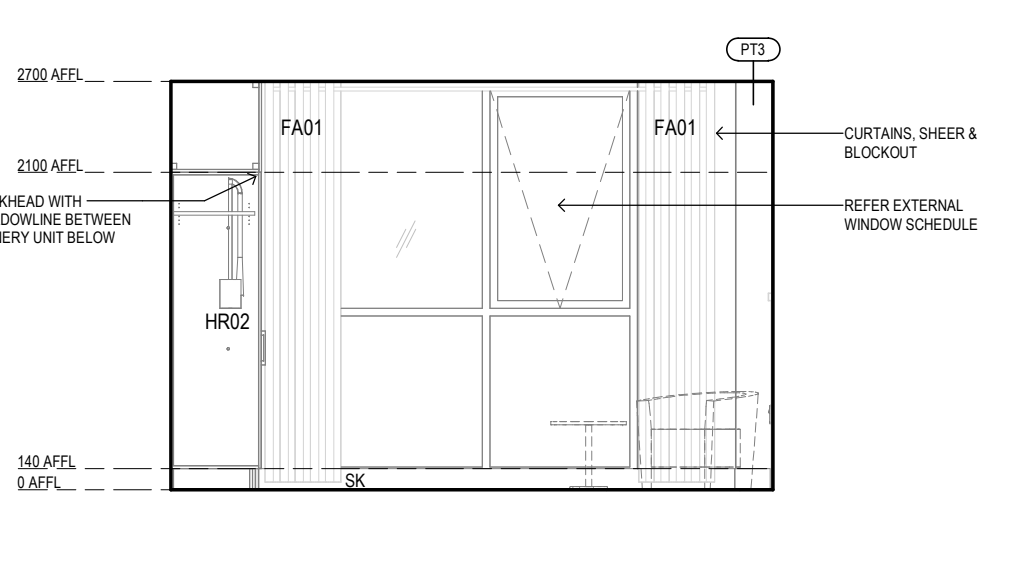

RACF STANDARD BEDROOM
ELEVATION 4
Scale 1 : 50

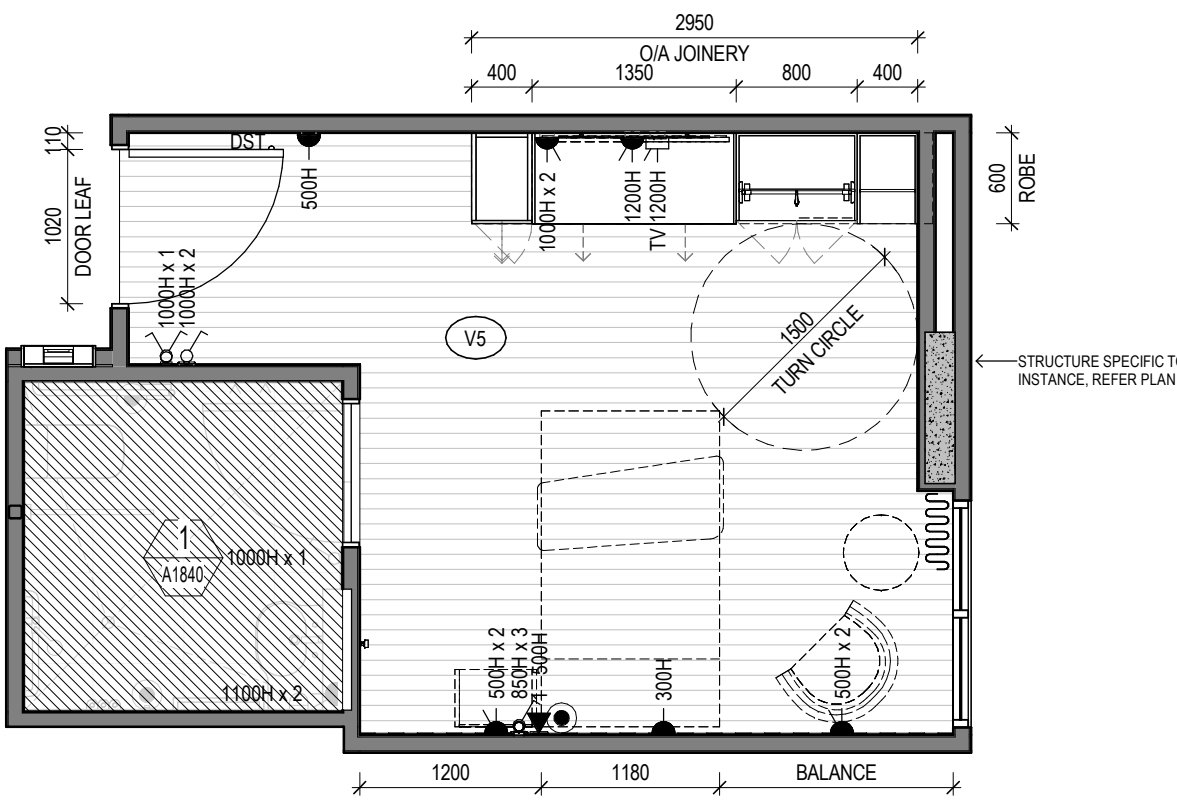


3 RACF STANDARD BEDROOM - TYPE B
Scale 1 : 50

Standard Type B	
Level	Room Number
RACF_Level 1	RM 125
RACF_Level 1	RM 127
S BED (B): 2	

Standard Type B Mirrored	
Level	Room Number
RACF_Level 1	RM 112
RACF_Level 1	RM 111
S BED (C MIR): 2	

NOTE: REFER SIMILAR ELEVATIONS TO STANDARD BEDROOM TYPE A, UNLESS NOTED OTHERWISE

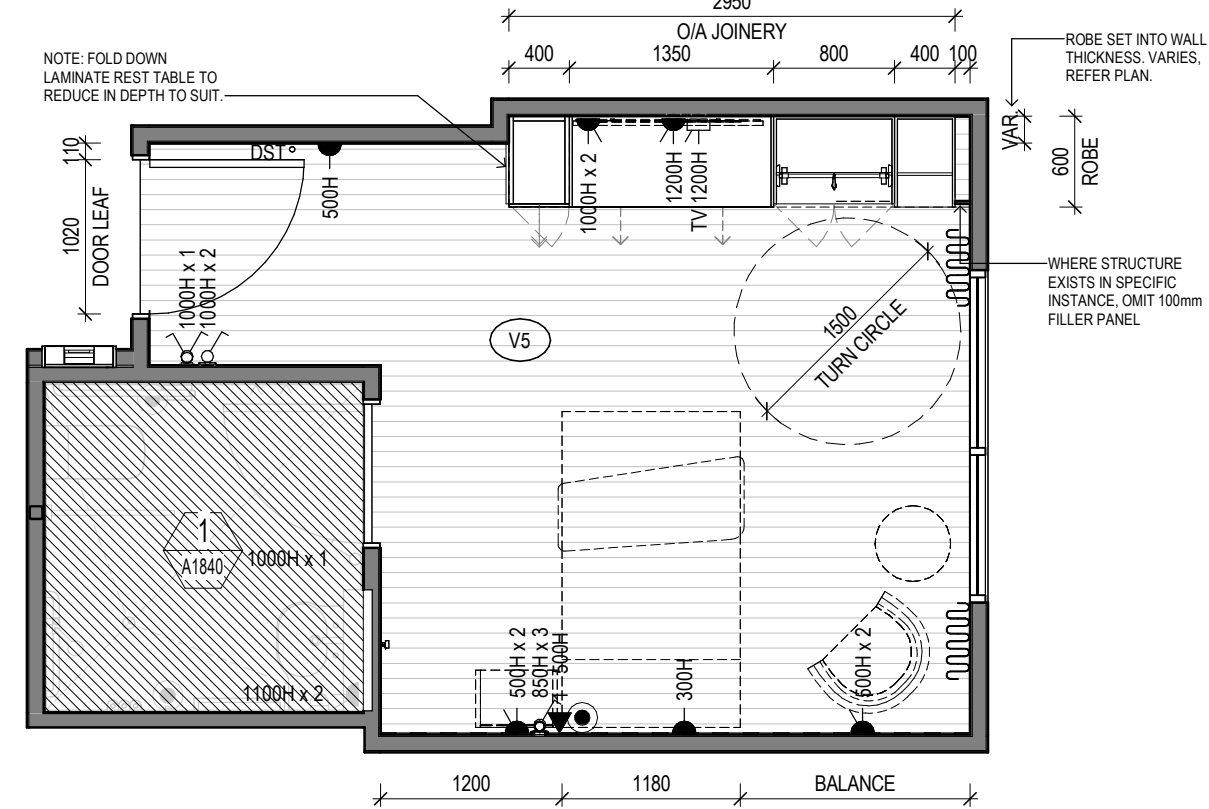


4 RACF STANDARD BEDROOM - TYPE C
Scale 1 : 50

Standard Type C	
Level	Room Number
RACF_Level 1	RM 112
S BED (C): 1	

Standard Type C Mirrored	
Level	Room Number
RACF_Level 1	RM 105
RACF_Level 1	RM 111
S BED (C MIR): 2	

NOTE: REFER SIMILAR ELEVATIONS TO STANDARD BEDROOM TYPE A, UNLESS NOTED OTHERWISE

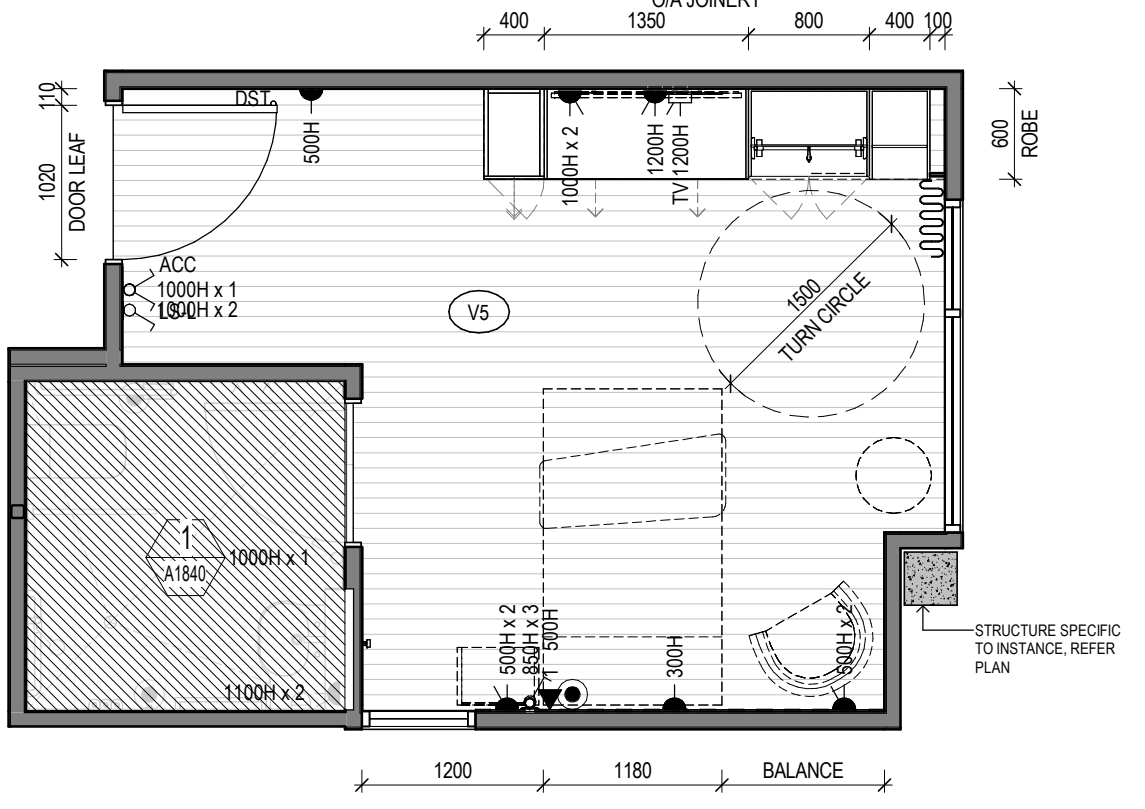


5 RACF STANDARD BEDROOM - TYPE D
Scale 1 : 50


Standard Type D	
Level	Room Number
RACF_Level 1	RM 113
RACF_Level 2	RM 213
S BED (D): 2	

Standard Type D Mirrored	
Level	Room Number
RACF_Level 1	RM 113
RACF_Level 2	RM 213
S BED (D): 2	


NOTE: REFER SIMILAR ELEVATIONS TO STANDARD BEDROOM TYPE A, UNLESS NOTED OTHERWISE

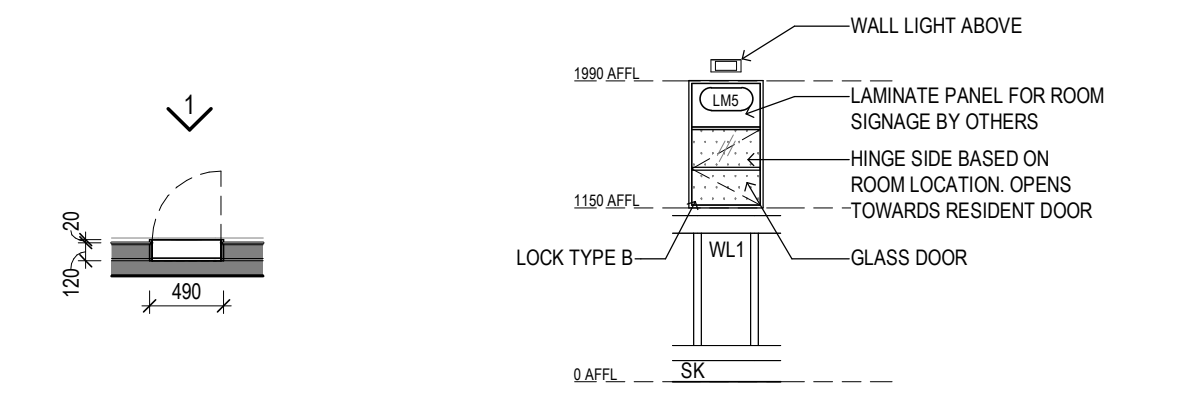


A MEMORY BOX
Scale 1 : 50

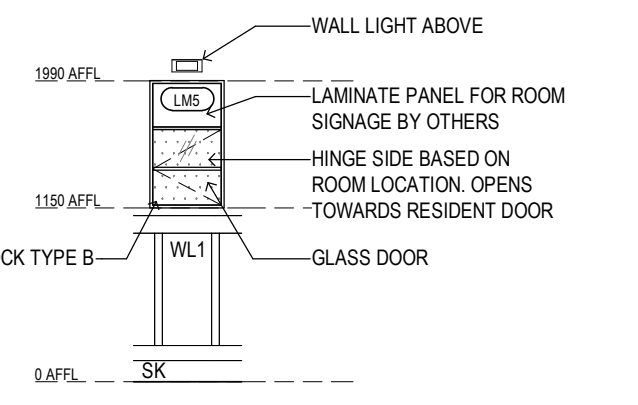

MEMORY BOX
ELEVATION 2
Scale 1 : 50

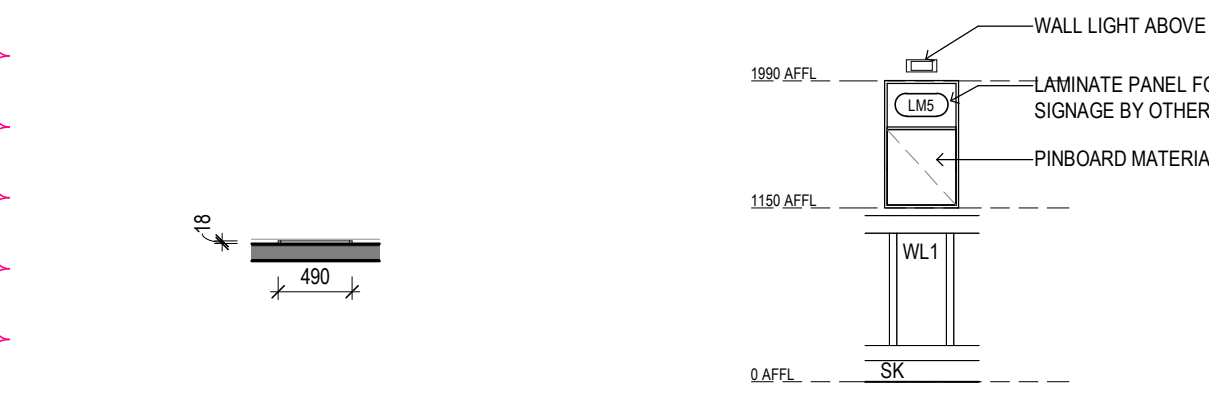

B MEMORY BOX - SLIMLINE
Scale 1 : 50

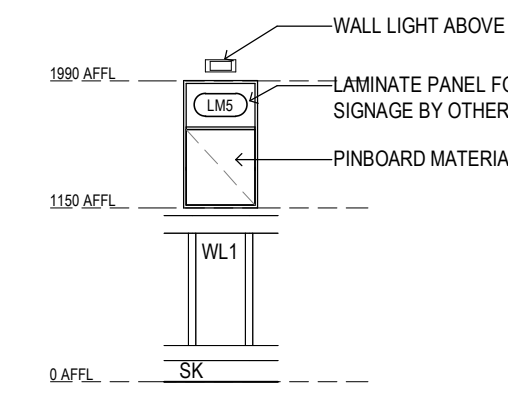

MEMORY BOX - SLIMLINE
ELEVATION 2
Scale 1 : 50

ADDITIONAL MEMORY BOX TYPE

Legend - Internal Elevations

DRAWINGS TO BE READ IN CONJUNCTION WITH ARCHITECTURAL SPECIFICATION & MATERIALS, PRODUCTS & FINISHES SCHEDULE.
PT# PAINT FINISH TO ALL WALLS WITHIN NEW & AFFECTED ROOMS/ AREAS UNLESS OTHERWISE SHOWN

- CSE CONCRETE SEALER
- DPR DOOR PROTECTION
- GD GRAPHIC FILM
- LM LAMINATE
- MI MIRROR
- PBD PINBOARD
- PT PAINT FINISH
- REN RENDER FINISH
- SB SPLASHBACK
- ST STONE
- WB WHITEBOARD
- WP WALL PROTECTION
- WT WALL TILE
- WV WALL VINYL

NOTES:
1. LAMINATE CARCASS FOR ALL VISIBLE OPEN SHELVING, UNLESS OTHERWISE NOTED
2. MELAMINITE TO ALL INTERNAL CARCASS OF JOINERY, UNLESS OTHERWISE NOTED.

Legend - Floor Finishes

- C CARPET
- CO CONCRETE
- E EPOXY FINISH
- L LINOLEUM
- M MATTING
- PU PAVING UNIT - TBC WITH LANDSCAPE
- R RUBBER FLOORING
- T TILING
- TF TIMBER FLOORING
- V VINYL
- LVY LUXURY VINYL TILE PLANK

- PROTECTION RAILS OR CRASH RAILS - REFER TO MATERIAL SCHEDULE FOR DETAILS
- WL1 - REFER TO MATERIAL SCHEDULE FOR DETAILS
- WL2 - REFER TO MATERIAL SCHEDULE FOR DETAILS

NOTE:
FALLS TO ALL FLOOR WASTES IN ACCORDANCE WITH AS 3740.

Keynote Legend

- 2WMB TV WALL MOUNTED BRACKET - GROUP 2
- ACC AIR CONDITIONING CONTROL
- ACU AIR CONDITIONING UNIT
- B BENCH - STANDARD
- BH-J BULKHEAD - JOINERY TYPE
- CBD CURBBOARD
- DATA DATA OUTLET
- DR DRAWER
- DST DOOR STOP
- FA01 SHEER CURTAINS
- GPO1 POWER OUTLET - SINGLE
- GPO2 POWER OUTLET - DOUBLE
- GP02L HANGING RAIL - TYPE 2
- LF1 LIGHT FITTING - REFER TO ELECTRICAL ENGINEER SPECIFICATION
- LS LIGHT SWITCH
- LS-L LIGHT SWITCH - LARGE PLATE
- MD MOTION DETECTOR
- M1 MIRROR - TYPE 1
- NC NURSE CALL
- PLH PATIENT LIFTING HOIST
- PRL PROTECTION RAIL
- RMB RESIDENT MEMORY BOX - JOINERY
- SH SHELF
- SK SKIRTING
- SMD SMOKE DETECTOR
- SPR SPRINKLER
- TV TELEVISION COAXIAL OUTLET
- W1 WALL LIGHT - TYPE 1
- W3 WALL LIGHT - TYPE 3
- WAP WIRELESS ACCESS POINT
- WL1 WALL PANELLING - TYPE 1
- WL4 WALL PANELLING - TYPE 4

FOR CONSTRUCTION

Revision/Issue	Date
P1 Preliminary RACF Room & Ensuite	2025.08.06
P2 Consolidated Set-to-date / SMG Comments	2025.08.15
P3 ISSUE FOR CONTRACT	2025.10.10
C1 ISSUE FOR CONSTRUCTION - INTERIORS	2026.03.30

Clarke Hopkins Clarke
Melbourne | Wurundjeri
L9, Melbourne Connect
700 Swanston Street
Carlton VIC 3063
Telephone (03) 9419 4340
Email studio@chc.com.au
www.chc.com.au

Sydney | Gadigal Country
Suite 3, Ground Floor
91 Campbell Street
Surry Hills NSW 2010
Telephone (02) 9221 9200
Email studio@chc.com.au
www.chc.com.au

Scale	As indicated @ A1
Date	01/03/2024
Drawn	JZ / TM
Architect	EL

Project
Summerset Oakleigh
52 Golf Road, Oakleigh South, VIC

Drawing
Internal Elevations - RACF Standard Bedrooms

Drawing No.
230185/A1830
C1