




3 RACF AMENITIES - ACCESSIBLE WC 01
Scale 1 : 50

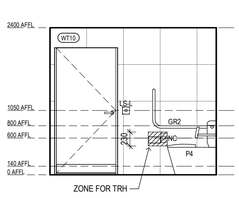


ACCESSIBLE WC 01 - 1

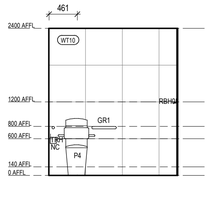


ACCESSIBLE WC 01 - 2

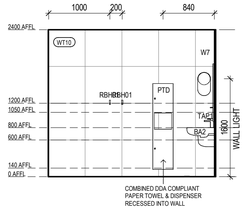


ACCESSIBLE WC 01 - 3

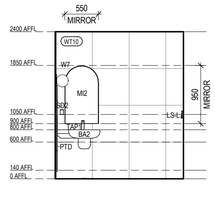


ACCESSIBLE WC 01 - 4

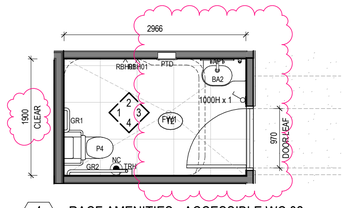

4 RACF AMENITIES - ACCESSIBLE WC 02
Scale 1 : 50

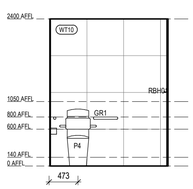


ACCESSIBLE WC 02 - 1

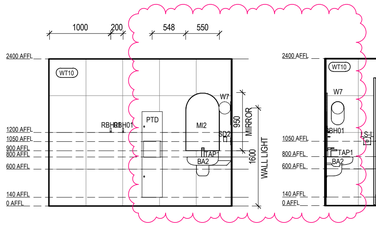


ACCESSIBLE WC 02 - 2

ACCESSIBLE WC 02 - 3

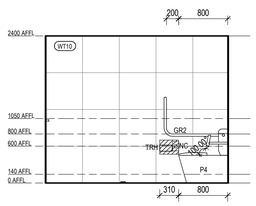


ACCESSIBLE WC 02 - 4

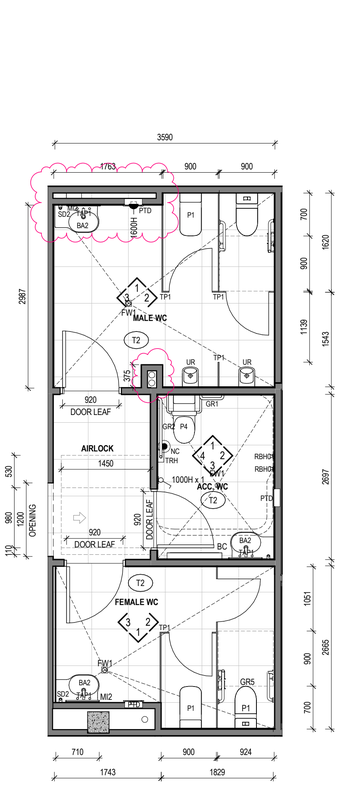

1 VILLAGE LIFESTYLE - AMENITIES
Scale 1 : 50


2 A1400 RCP - VILLAGE LIFESTYLE - AMENITIES
Scale 1 : 50

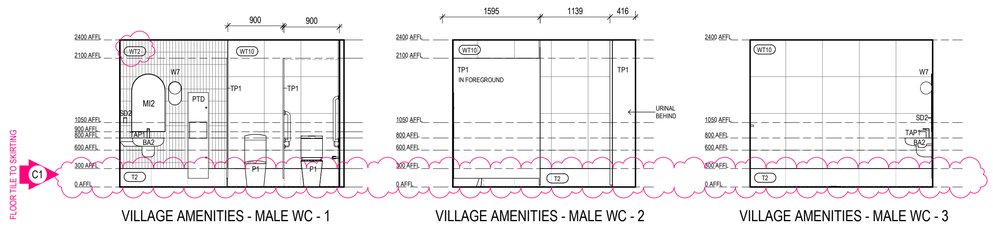

VILLAGE AMENITIES - MALE WC - 1

VILLAGE AMENITIES - MALE WC - 2

VILLAGE AMENITIES - MALE WC - 3

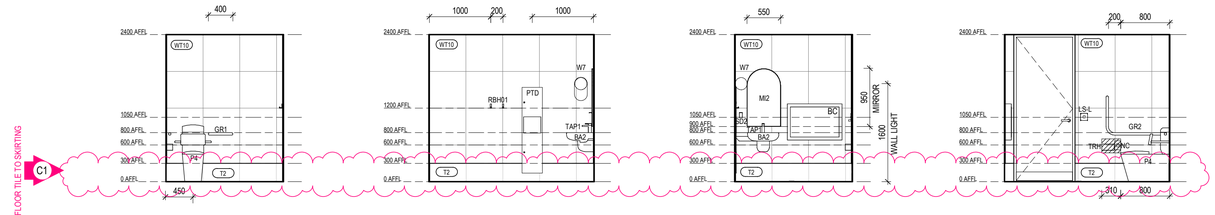


VILLAGE AMENITIES - ACC WC - 1

VILLAGE AMENITIES - ACC WC - 2

VILLAGE AMENITIES - ACC WC - 3

VILLAGE AMENITIES - ACC WC - 4

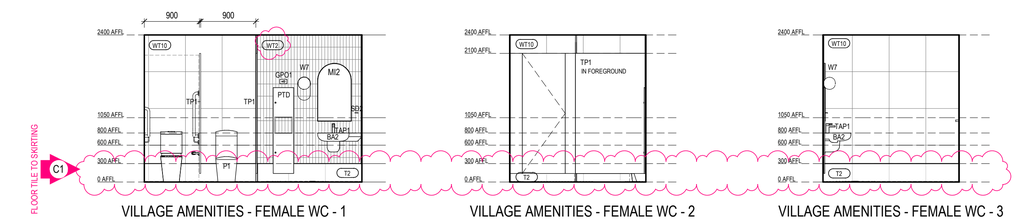

VILLAGE AMENITIES - FEMALE WC - 1

VILLAGE AMENITIES - FEMALE WC - 2

VILLAGE AMENITIES - FEMALE WC - 3

Legend - Internal Elevations

DRAWINGS TO BE READ IN CONJUCTION WITH ARCHITECTURAL SPECIFICATION & MATERIALS, PRODUCTS & FINISHES SCHEDULE.

PT# PAINT FINISH TO ALL WALLS WITHIN NEW & AFFECTED ROOMS/ AREAS UNLESS OTHERWISE SHOWN

CSE	CONCRETE SEALER
DPR	DOOR PROTECTION
GD	GRAPHIC FILM
LM	LAMINATE
MI	MIRROR
PBD	PINBOARD
PT	PAINT FINISH
REN	RENDER FINISH
SB	SPLASHBACK
ST	STONE
WB	WHITEBOARD
WP	WALL PROTECTION
WT	WALL TILE
WV	WALL VINYL

NOTES:
1. LAMINATE CARCASS FOR ALL VISIBLE OPEN SHELVING, UNLESS OTHERWISE NOTED
2. MELAMINETO ALL INTERNAL CARCASS OF JOINERY, UNLESS OTHERWISE NOTED.

Legend - Floor Finishes

C	CARPET
CO	CONCRETE
E	EPOXY FINISH
L	LINOLEUM
M	MATTING
PU	PAVING UNIT - TBC WITH LANDSCAPE
R	RUBBER FLOORING
T	TILING
TF	TIMBER FLOORING
V	VINYL
LVT	LUXURY VINYL TILE PLANK

PROTECTION RAILS OR CRASH RAILS - REFER TO MATERIAL SCHEDULE FOR DETAILS

WL1- REFER TO MATERIAL SCHEDULE FOR DETAILS

WL2 - REFER TO MATERIAL SCHEDULE FOR DETAILS

NOTE:

FALLS TO ALL FLOOR WASTES IN ACCORDANCE WITH AS 3740.

Keynote Legend

BA2	BASIN - TYPE 2
BC	BABY CHANGE TABLE
FW1	FLOOR WASTE - TYPE 1
GPO1	POWER OUTLET - SINGLE
GR1	GRAB RAIL - TYPE 1
GR2	GRAB RAIL - TYPE 2
GR5	GRAB RAIL - TYPE 5
LS-L	LIGHT SWITCH - LARGE PLATE
MI2	MIRROR - TYPE 2
NC	NURSE CALL
P1	TOILET PAN TYPE 01
P4	TOILET PAN TYPE 04
PTD	PAPER TOWEL DISPENSER
RBH01	ROBE HOOK - TYPE 1
SD2	SOAP DISPENSER - TYPE 2
TAP1	TAP - TYPE 1
TP1	TOILET PARTITION - TYPE 1
TRH	TOILET ROLL HOLDER
UR	URINAL
W7	WALL LIGHT - TYPE 7

FOR CONSTRUCTION

Revision/Issue		Date
P1	RACF & ILA WIP Consultant Coordination & Review	2025.06.24
P2	Consolidated Set-to-date / SMG Comments	2025.08.15
P3	ISSUE FOR CONTRACT	2025.10.10
C1	ISSUE FOR CONSTRUCTION - INTERIORS	2026.03.30

ClarkeHopkinsClarke

Melbourne | Wurundjeri
L9, Melbourne Connect
700 Swanston Street
Carlton VIC 3053
Telephone (03) 9419 4340
Email studio@chc.com.au
www.chc.com.au

Sydney | Gadigal Country
Suite 3, Ground Floor
91 Campbell Street
Surry Hills NSW 2010
Telephone (02) 9221 9200
Email studio@chc.com.au
www.chc.com.au

Scale	As indicated @ A1
Date	01/03/2024
Drawn	TT / TM
Architect	EL

Project
Summerset Oakleigh
52 Golf Road, Oakleigh South, VIC

Drawing
Internal Elevations - Amenities

Drawing No.
230185/A1845 C1

A1 Use figured dimensions in preference to scale. Verify dimensions at job before shop fabrication. Read drawing in conjunction with specification.

© ClarkeHopkinsClarke