
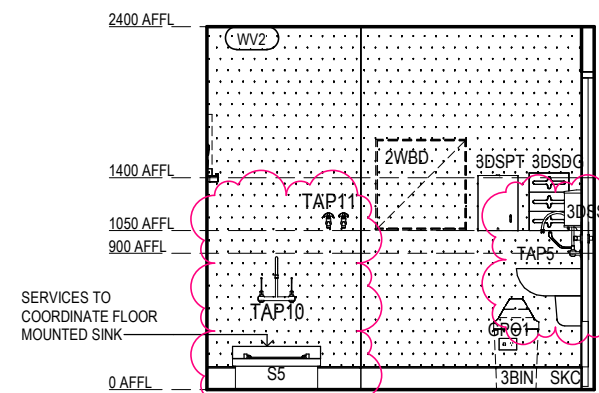
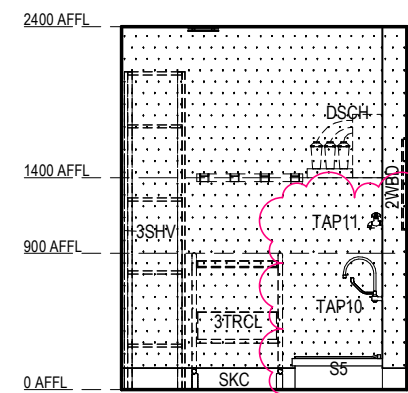
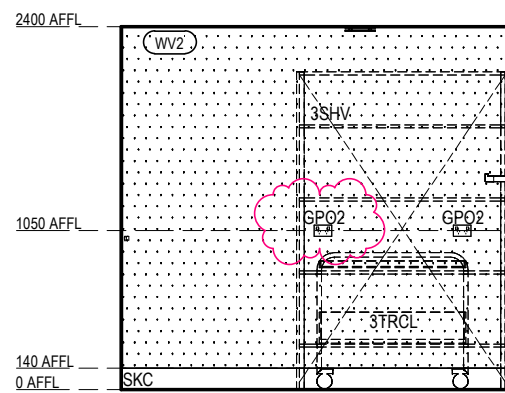
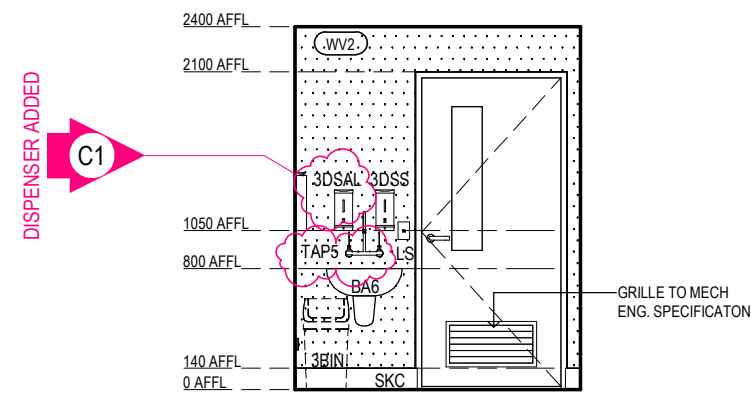
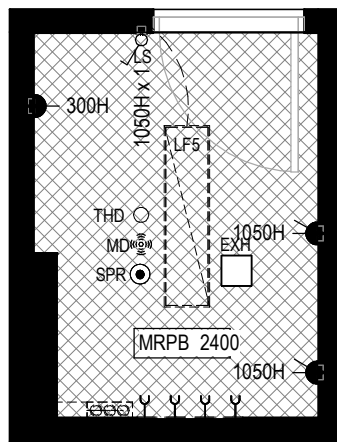


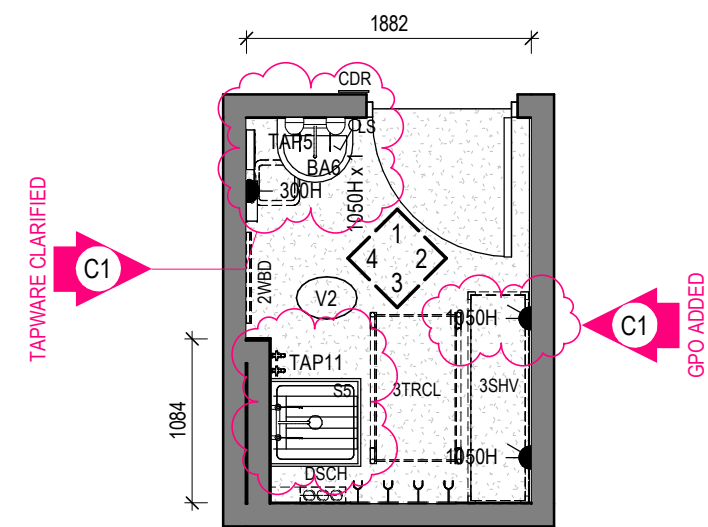

1 RACF-CLEANER - TYPE 1
Scale 1 : 50







2 RCP-CLEANER - TYPE 1
Scale 1 : 50

RACF BOH - CLEANER - TYPE 1
ELEVATION 1
Scale 1 : 50

RACF BOH - CLEANER - TYPE 1
ELEVATION 2
Scale 1 : 50

RACF BOH - CLEANER - TYPE 1
ELEVATION 3
Scale 1 : 50

RACF BOH - CLEANER - TYPE 1
ELEVATION 4
Scale 1 : 50

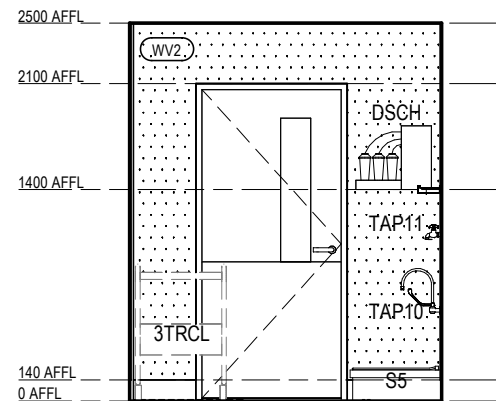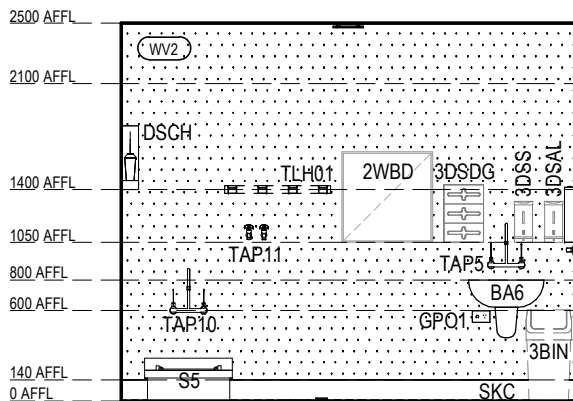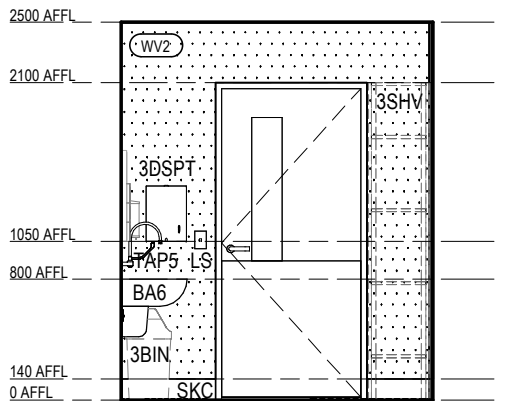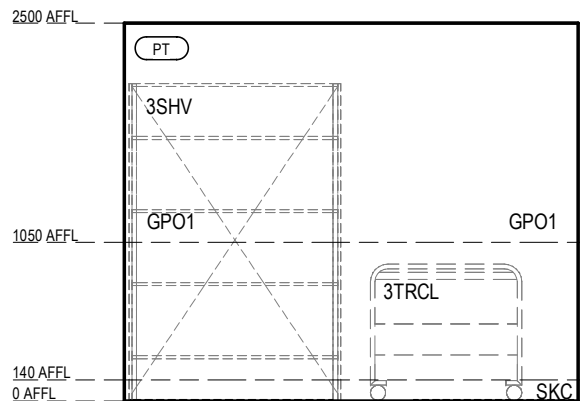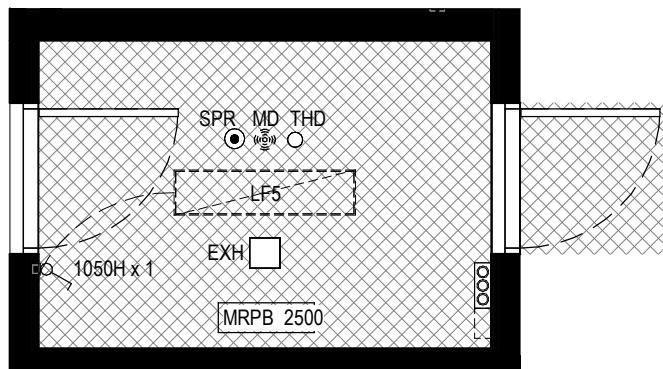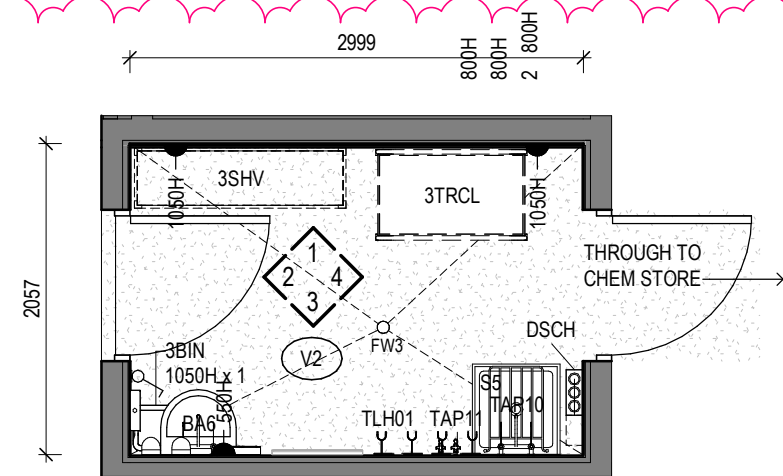

3 RACF-CLEANER - TYPE 2
Scale 1 : 50






4 RCP-CLEANER - TYPE 2
Scale 1 : 50

RACF BOH - CLEANER - TYPE 2
ELEVATION 1
Scale 1 : 50

RACF BOH - CLEANER - TYPE 2
ELEVATION 2
Scale 1 : 50

RACF BOH - CLEANER - TYPE 2
ELEVATION 3
Scale 1 : 50

RACF BOH - CLEANER - TYPE 2
ELEVATION 4
Scale 1 : 50

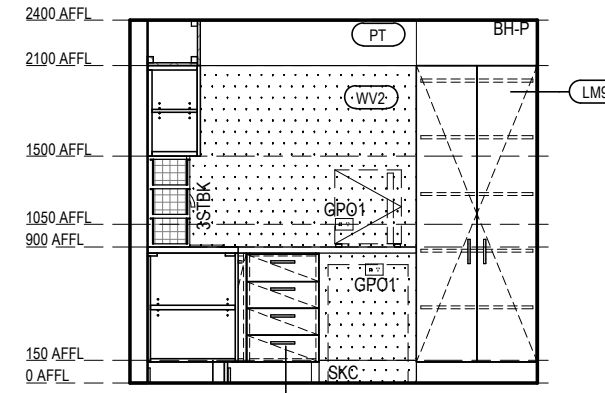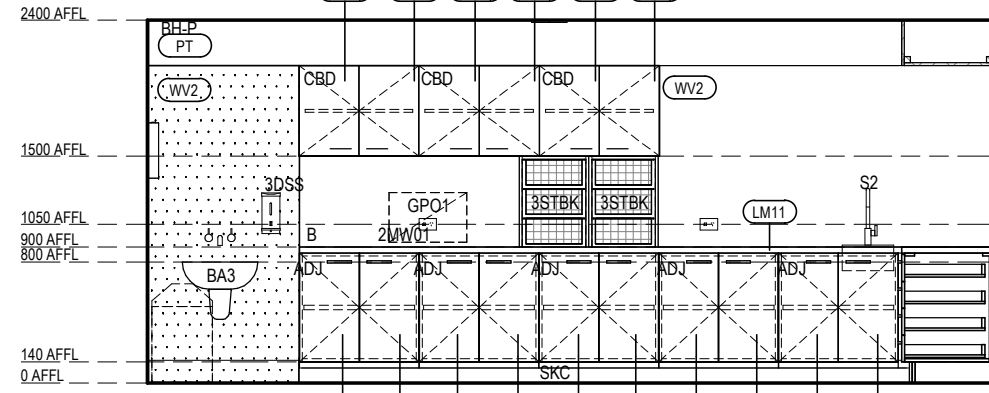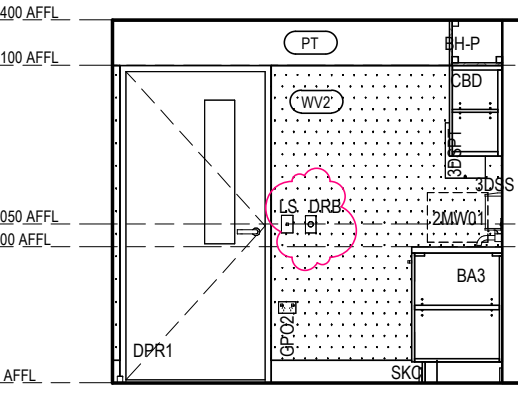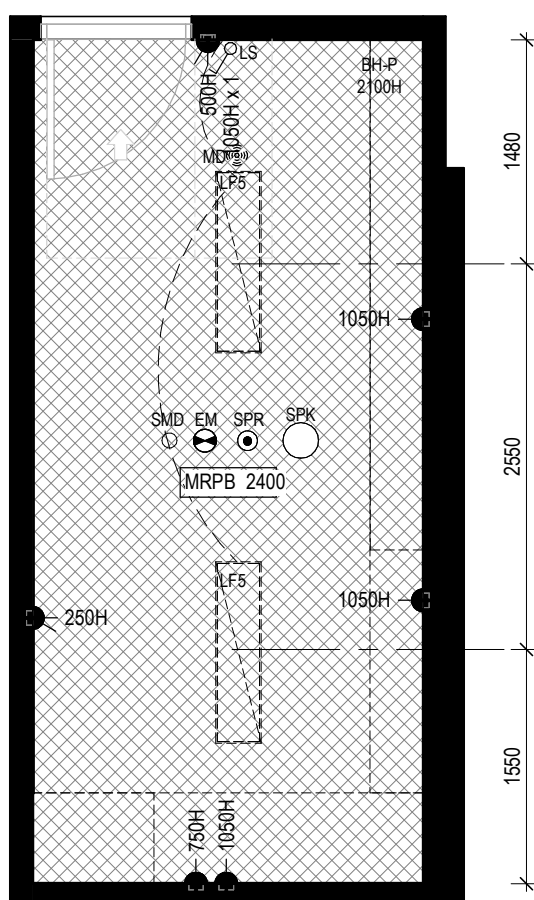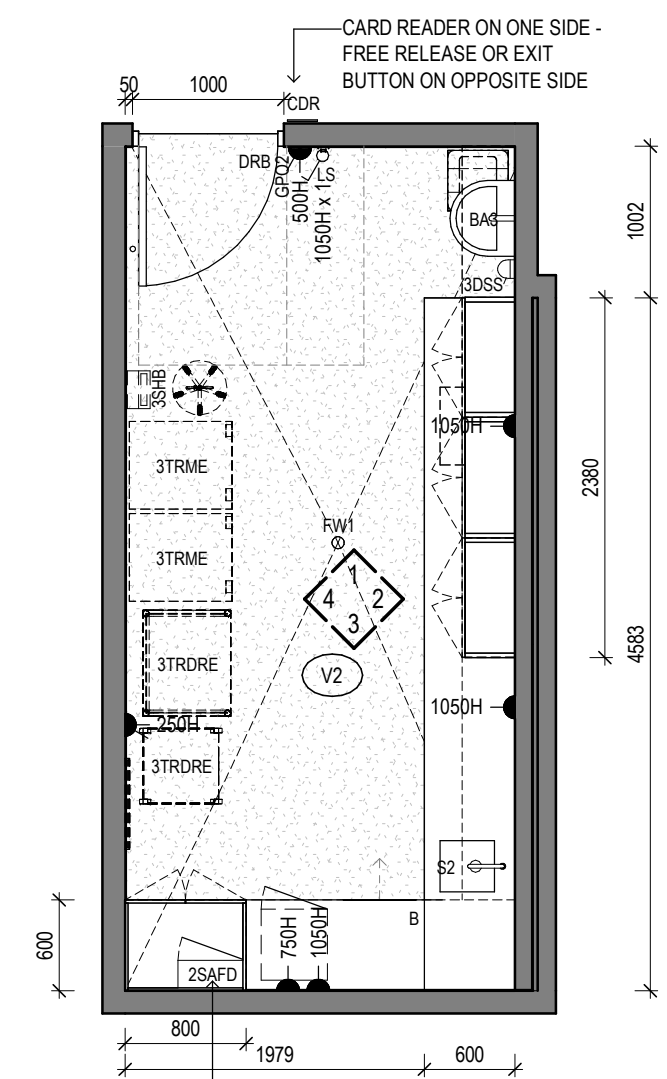





RACF BOH - TREATMENT
ELEVATION 1
Scale 1 : 50

RACF BOH - TREATMENT
ELEVATION 2
Scale 1 : 50

RACF BOH - TREATMENT
ELEVATION 3
Scale 1 : 50

5 RACF-TREATMENT
Scale 1 : 50

6 RCP-TREATMENT
Scale 1 : 50

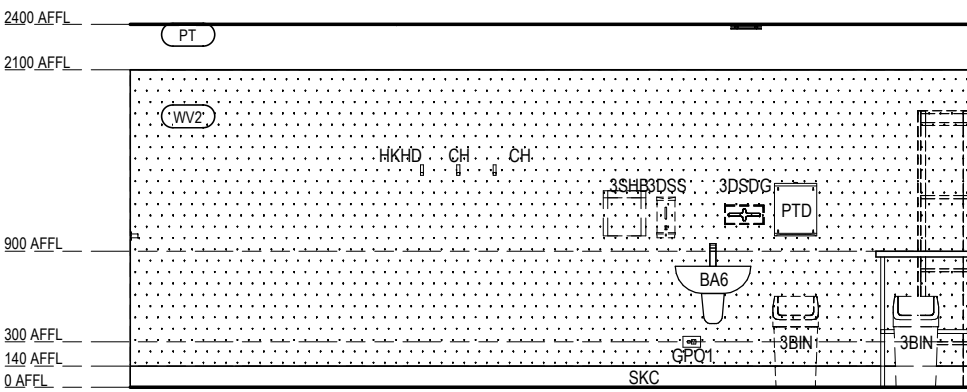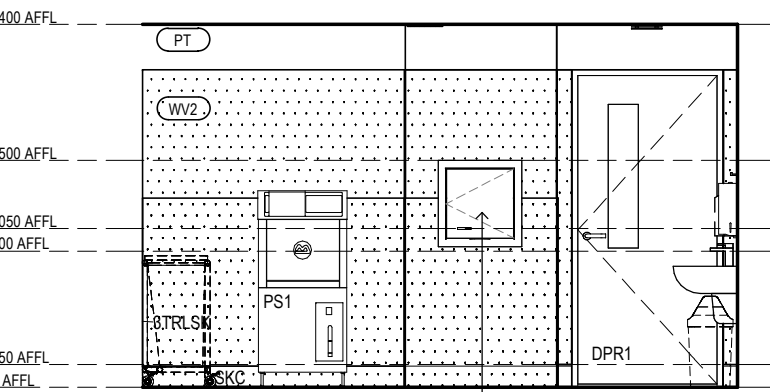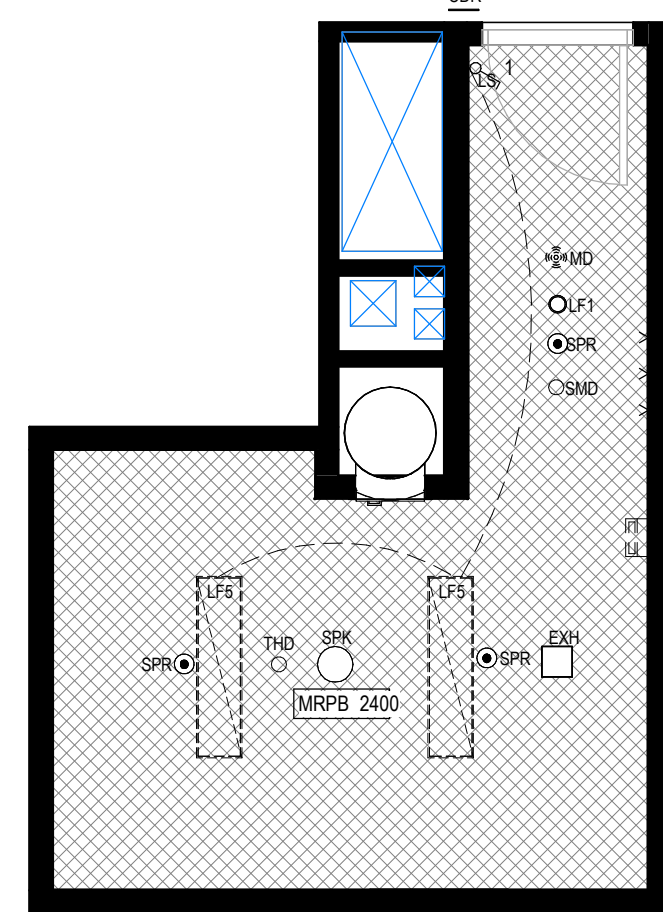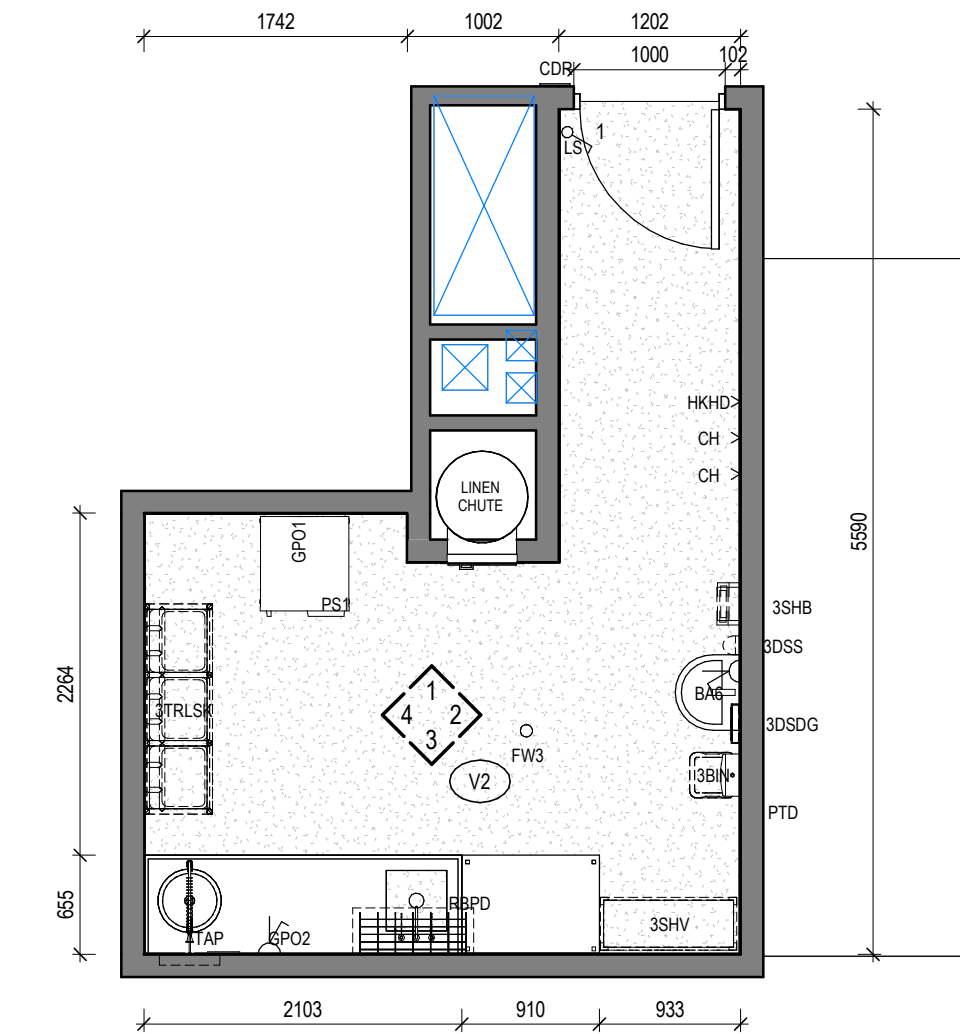

RACF BOH - SLUICE
ELEVATION 1
Scale 1 : 50

RACF BOH - SLUICE
ELEVATION 2
Scale 1 : 50

7 RACF-SLUICE
Scale 1 : 50

8 RCP-SLUICE
Scale 1 : 50

RACF BOH - SLUICE
ELEVATION 3
Scale 1 : 50

RACF BOH - SLUICE
ELEVATION 4
Scale 1 : 50

Legend - Internal Elevations

DRAWINGS TO BE READ IN CONJUNCTION WITH ARCHITECTURAL SPECIFICATION & MATERIALS, PRODUCTS & FINISHES SCHEDULE.

PT# PAINT FINISH TO ALL WALLS WITHIN NEW & AFFECTED ROOMS/ AREAS UNLESS OTHERWISE SHOWN

- CSE CONCRETE SEALER
- DPR DOOR PROTECTION
- GD GRAPHIC FILM
- LM LAMINATE
- MI MIRROR
- PBD PINBOARD
- PT PAINT FINISH
- REN RENDER FINISH
- SB SPLASHBACK
- ST STONE
- WB WHITEBOARD
- WP WALL PROTECTION
- WT WALL TILE
- VV WALL VINYL

NOTES:
1. LAMINATE CARCASS FOR ALL VISIBLE OPEN SHELVING, UNLESS OTHERWISE NOTED
2. MELAMINETO ALL INTERNAL CARCASS OF JOINERY, UNLESS OTHERWISE NOTED.

Legend - Floor Finishes

- C CARPET
- CO CONCRETE
- E EPOXY FINISH
- L LINOLEUM
- M MATTING
- PU PAVING UNIT - TBC WITH LANDSCAPE
- R RUBBER FLOORING
- T TILING
- TF TIMBER FLOORING
- V VINYL
- LV LUXURY VINYL TILE PLANK

Keynote Legend

- 2MW01 MICROWAVE - TYPE 1 - GROUP 2
- 2SAFD DRUG SAFE - TYPE 1 - GROUP 2
- 2WBD WHITEBOARD - GROUP 2
- 3BIN WASTE BIN - GROUP 3
- 3DSAL ALCOHOL HAND RUB DISPENSER - GROUP 3
- 3DSDG GLOVE DISPENSER - GROUP 3
- 3DSP1 DISPENSER - PAPER TOWEL - GROUP 3
- 3DSS SOAP DISPENSER - GROUP 3
- 3SHB BIN SHARPS - GROUP 3
- 3SHV SHELVING - GROUP 3
- 3STBK STORAGE BASKET - GROUP 3
- 3TRCL TROLLEY CLEANERS - GROUP 3
- 3TRDRE TROLLEY DRESSING - GROUP 3
- 3TRLK TROLLEY LINEN SKIP - GROUP 3
- 3TRME TROLLEY MEDICATION - GROUP 3
- ADJ ADJUSTABLE SHELF
- B BENCH - STANDARD
- B-SS BENCH - STAINLESS STEEL
- BA3 BASIN - TYPE 3
- BA6 BASIN - TYPE 6
- BH-P BULKHEAD - PLASTERBOARD TYPE
- CBP CUPBOARD
- CDR CARD READER
- CH CLOTHES HOOK
- DPR1 DOOR PROTECTION - TYPE 1
- DRB DOOR RELEASE BUTTON
- DSCH DISPENSER - CHEMICAL MIXER
- EM EMERGENCY LIGHT
- EXH EXHAUST
- FW1 FLOOR WASTE - TYPE 1
- FW3 FLOOR WASTE - TYPE 3
- GP01 POWER OUTLET - SINGLE
- GP02 POWER OUTLET - DOUBLE
- HKHD HOOK - HEAVY DUTY
- LF1 LIGHT FITTING - REFER TO ELECTRICAL ENGINEER SPECIFICATION
- LF5 LIGHT FITTING - TYPE 5
- LS LIGHT SWITCH
- MD MOTION DETECTOR
- PS1 PAN SANITISER
- PTD PAPER TOWEL DISPENSER
- RPDP RACK BEDPAN WITH DRIP TRAY
- S2 SINK - TYPE 2
- S4 SINK - TYPE 4
- S5 SINK - TYPE 5
- SKC SKIRTING - COVED
- SMD SMOKE DETECTOR
- SPK ANUNCIATOR
- SPR SPRINKLER
- TAP TAP
- TAP5 TAP - TYPE 5
- TAP10 TAP - TYPE 10
- TAP11 TAP - TYPE 11
- THD THERMAL DETECTOR
- TLH01 TOOL HOLDER - WALL MOUNTED

FOR CONSTRUCTION

Drawing No.

230185/A1820

C1

Clarke
Hopkins
Clarke

ClarkeHopkinsClarke

Melbourne | Wurundjeri

L3, Melbourne Connect

700 Swanston Street

Carlton VIC 3063

Telephone (03) 9419 4340

Email studio@chc.com.au

www.chc.com.au

Sydney | Gadigal Country

Suite 3, Ground Floor

91 Campbell Street

Surry Hills NSW 2101

Telephone (02) 9221 9200

Email studio@chc.com.au

www.chc.com.au

Scale As indicated @ A1

Date 01/03/2024

Drawn RM

Architect EL

Project

Summerset Oakleigh

52 Golf Road, Oakleigh South, VIC

Drawing

Internal Elevations - RACF BOH - Clean,

Treatment & Sluice

Revision/Issue

P1 Preliminary Internal Elevations - RACF

P2 Consolidated Set-to-date / SMG Comments

P3 ISSUE FOR CONTRACT

C1 ISSUE FOR CONSTRUCTION - INTERIORS

Date

2025.08.08

2025.08.15

2025.10.10

2026.03.30

Use figured dimensions in preference to scale. Verify dimensions at job before shop fabrication. Read drawing in conjunction with specification.

© ClarkeHopkinsClarke