


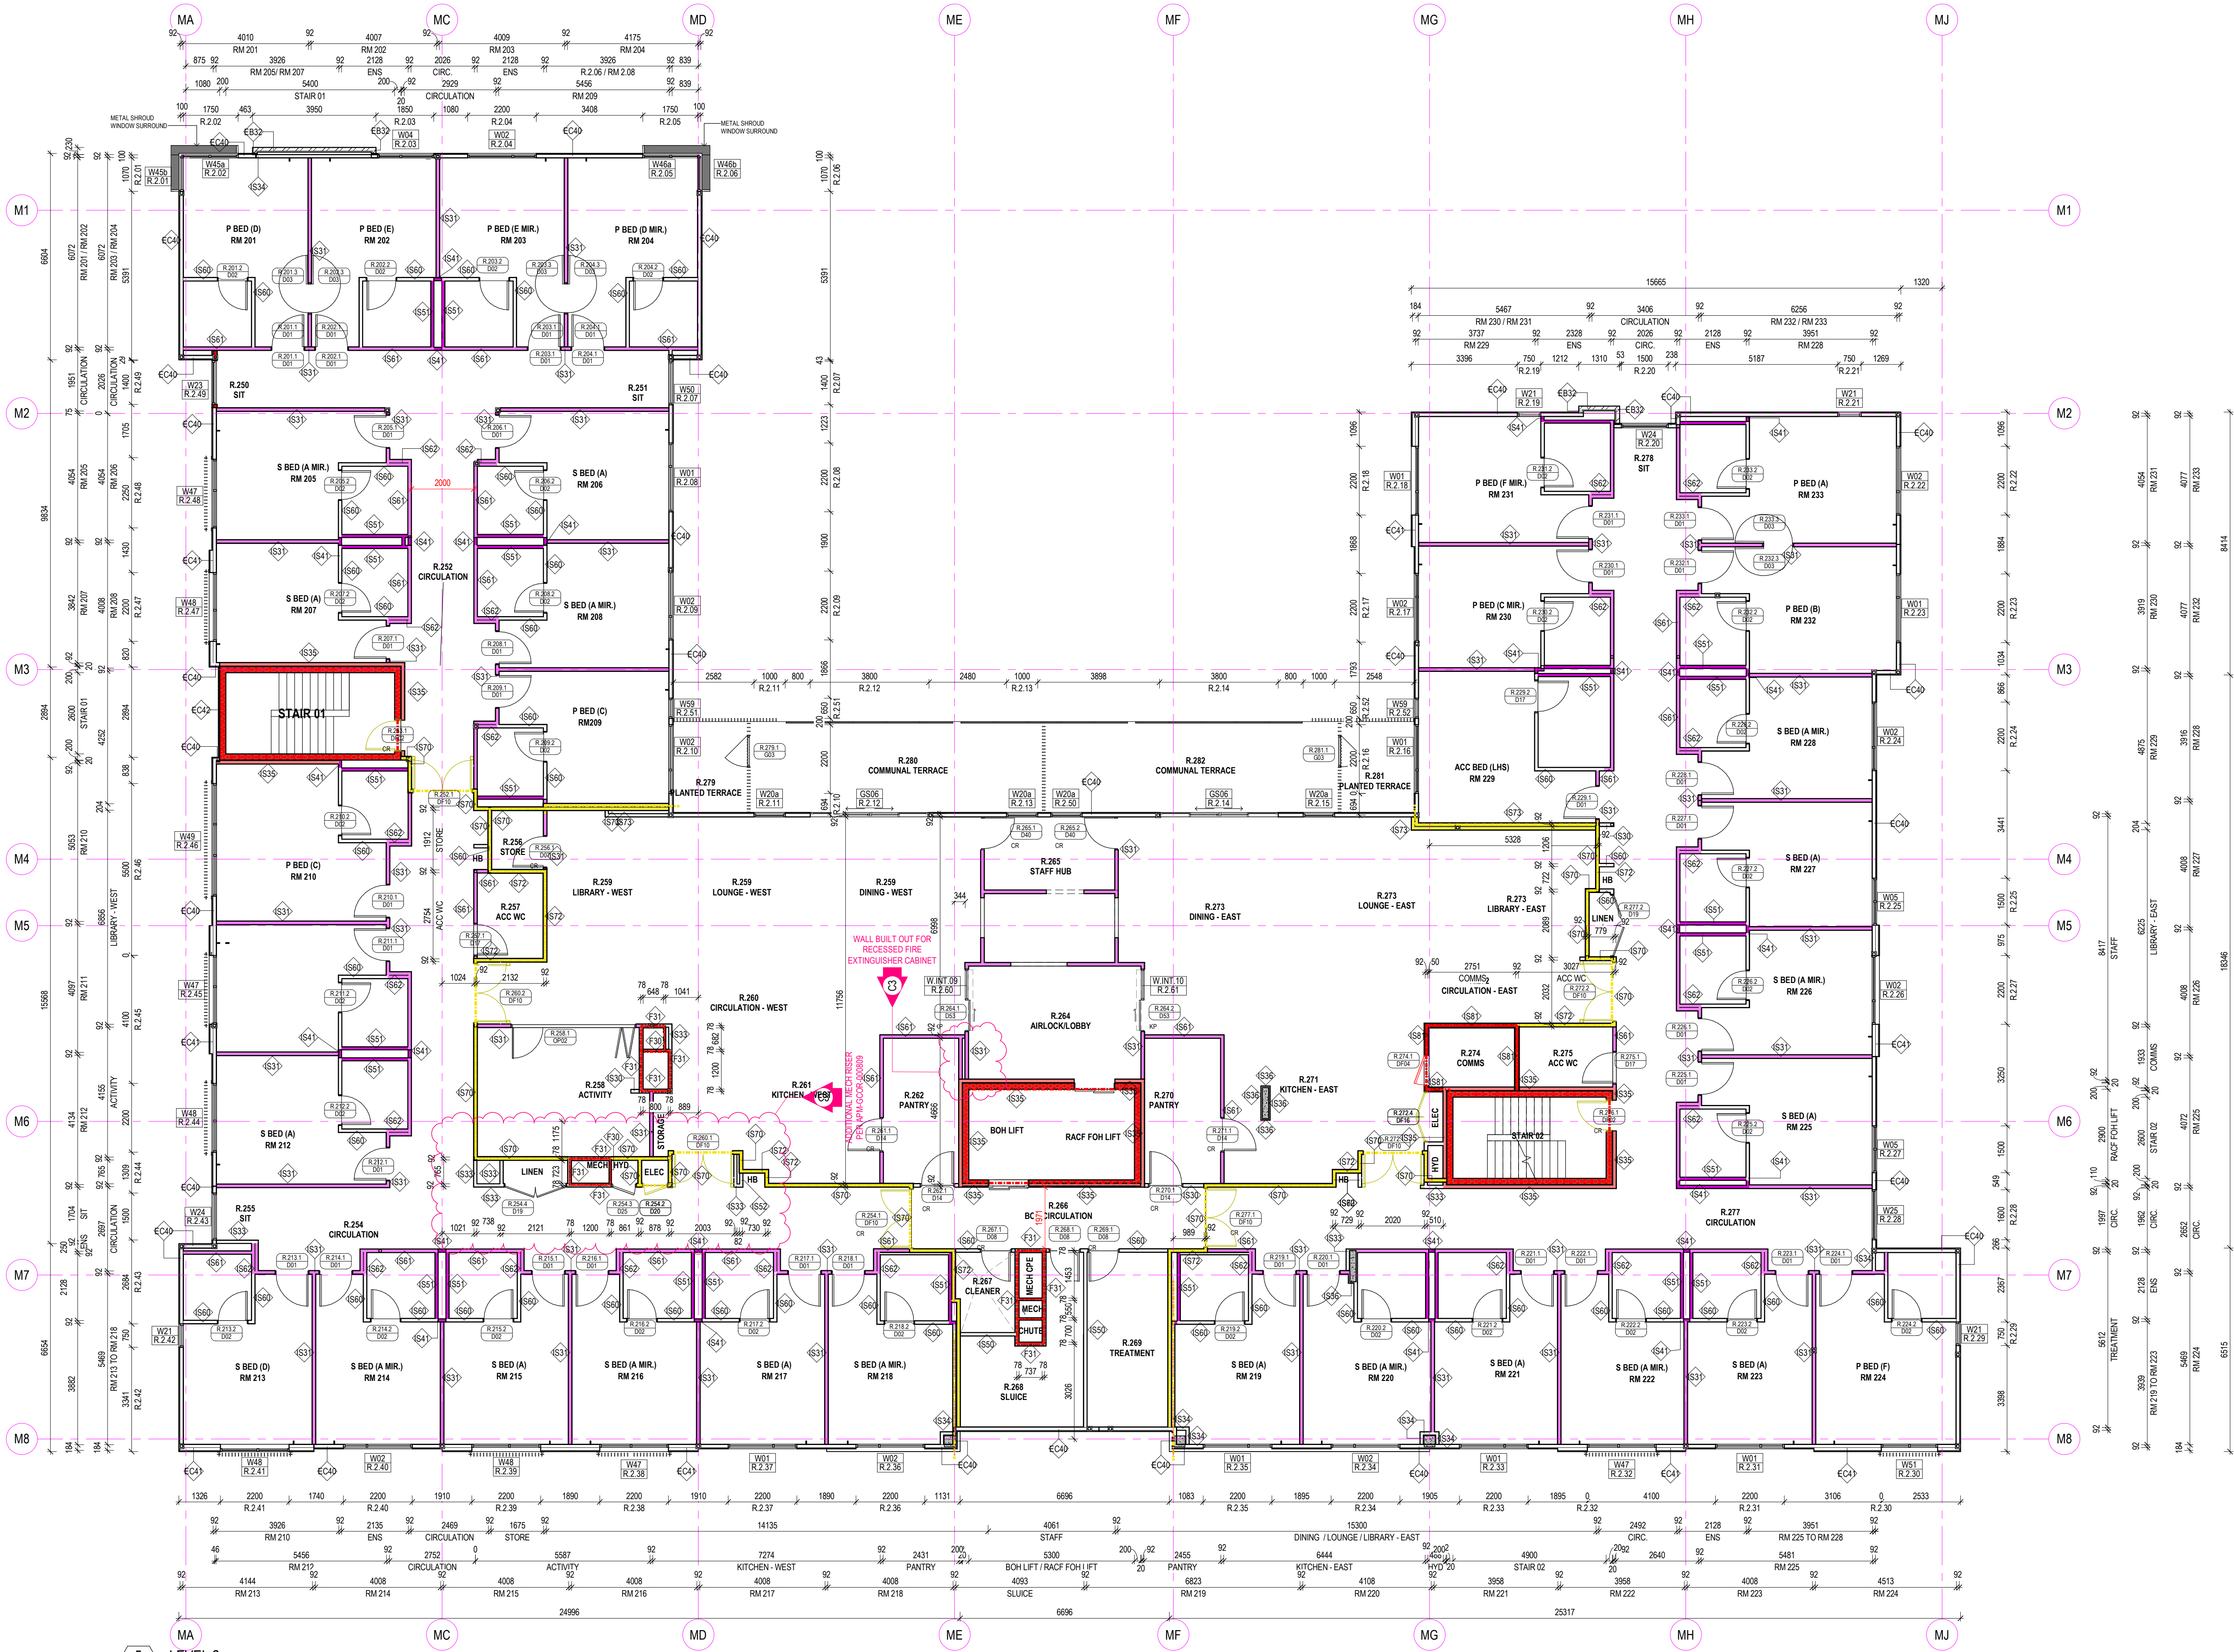

### Legend - Wall Types

- STUD WALL
- PRECAST CONCRETE WALL
- CONCRETE
- BLOCK WALL
- BRICK VENEER WALL
- WALL TYPES REFER TO A9200 SERIES WALL SCHEDULE. READ THIS DRAWING & WALL TYPES IN CONJUNCTION WITH ACOUSTIC AND ESD SPECIFICATION.
- DOORS**
  - DOOR NUMBER (BUILDING ROOM NUMBER)
  - DOOR TYPE
  - ELECTRONIC ACCESS CONTROL (REF. DOOR SCHEDULE)
- WINDOWS**
  - WINDOW TYPE
  - WINDOW NUMBER (BUILDING LEVEL NUMBER)
  - ELECTRONIC ACCESS CONTROL (REF. DOOR SCHEDULE)

- MINIMUM FIRE RATINGS:**  
THE FIRE RATING LEGEND BELOW INDICATE THE MINIMUM REQUIRED FIRE RATINGS AS INDICATED BY THE BUILDING SURVEYOR. SOME WALL TYPES MAY ACHIEVE HIGHER RATINGS THROUGH THE NATURE OF THEIR CONSTRUCTION.
- FIRE RATED WALL 60/60/60
  - FIRE RATED WALL 120/120/120
  - FIRE RATED WALL 90/90/90 FOR LOAD BEARING AND -60/60 FOR NON-LOAD BEARING
  - SMOKE WALL
- NOTE (RAC BUILDING):**  
ALL SMOKE WALLS IDENTIFIED BY THE BUILDING SURVEYOR IN THE RAC BUILDING HAVE BEEN UPGRADED TO A 60/60/60 FIRE WALL TO ALIGN WITH SSG OPERATIONAL PROCEDURES.
- NOTE (STEEL COLUMNS):**  
ALL LOAD BEARING STEEL COLUMNS AND STRUCTURE SHALL BE WRAPPED IN PYROMAT TO ACHIEVE THE FOLLOWING:  
• RAC BUILDING: 120/120/120  
• ILA BUILDING: 90/90/90  
• LNK: 120/120/120

- MINIMUM ACOUSTIC RATINGS:**  
REFER ALSO ACOUSTIC REPORT PREPARED BY ACOUSTIC LOGIC.
- THE ACOUSTIC RATING LEGEND BELOW INDICATE THE MINIMUM REQUIRED ACOUSTIC RATINGS AS INDICATED BY THE ACOUSTIC LOGIC. SOME WALL TYPES MAY ACHIEVE HIGHER RATINGS THROUGH THE NATURE OF THEIR CONSTRUCTION.
- REFER ACOUSTIC LOGIC REPORT DETAILS AC012 & AC013 FOR THE ACOUSTIC TREATMENT ABOVE BATHROOM, ENSUITE, POWDER-ROOMS, LAUNDRIES, AND UNDER HYDRAULIC PIPEWORK.
- R<sub>w</sub>45
  - R<sub>w</sub>50
  - R<sub>w</sub> + C<sub>w</sub>40
  - R<sub>w</sub> + C<sub>w</sub>50
- THERMAL PERFORMANCE:**  
REFER ALSO TO THE SUSTAINABILITY MANAGEMENT PLAN (SMP) PREPARED BY GIW FOR THE THERMAL PERFORMANCE OF:  
• FACADE ELEMENTS  
• WALL BETWEEN HABITABLE AND NON HABITABLE SPACES  
• THERMAL PERFORMANCE OF ROOF ELEMENTS  
• THERMAL PERFORMANCE BETWEEN BASEMENT AND GROUND FLOOR HABITABLE ROOMS.

- WALL AND DOOR PROTECTION:**  
REFER DOOR SCHEDULE FOR DOOR PROTECTION TYPES AND HEIGHTS.
- CRASH RAILS TO BOH WALLS, REFER SCHEDULE.
- CORNER PROTECTION WHERE INDICATED.

### Legend - Door Types

- SMOKE DOORS
- 2HR FIRE DOORS
- 1HR FIRE DOORS

DOOR SEQUENCE SELECTORS TO SUIT FOR ALL SMOKE AND FIRE DOORS. REFER TO DOOR HARDWARE SCHEDULE.


# FOR CONSTRUCTION

| Revision/Issue                            | Date       |
|-------------------------------------------|------------|
| P5 ISSUE FOR CONTRACT                     | 2025.10.10 |
| C1 ISSUE FOR CONSTRUCTION                 | 2025.12.19 |
| C2 ISSUE FOR CONSTRUCTION - DOOR SCHEDULE | 2026.03.16 |
| C3 ISSUE FOR CONSTRUCTION                 | 2026.03.24 |

**Clarke Hopkins Clarke**  
Melbourne | Wurundjeri  
L3, Melbourne Connect  
700 Swanston Street  
Carlton VIC 3063  
Telephone (03) 9419 4340  
Email studio@chc.com.au  
www.chc.com.au

Sydney | Gadigal Country  
Suite 3, Ground Floor  
91 Campbell Street  
Sunny Hills NSW 2010  
Telephone (02) 9221 9200  
Email studio@chc.com.au  
www.chc.com.au

|           |            |
|-----------|------------|
| Scale     | 1:100 @ A1 |
| Date      | 01/03/2024 |
| Drawn     | AC         |
| Architect | EL         |

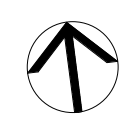

Project  
**Summerset Oakleigh**  
52 Golf Road, Oakleigh South, VIC

Drawing  
**Wall Set out Plan - Second Floor**

Drawing No.  
**230185/A1244**

C3