


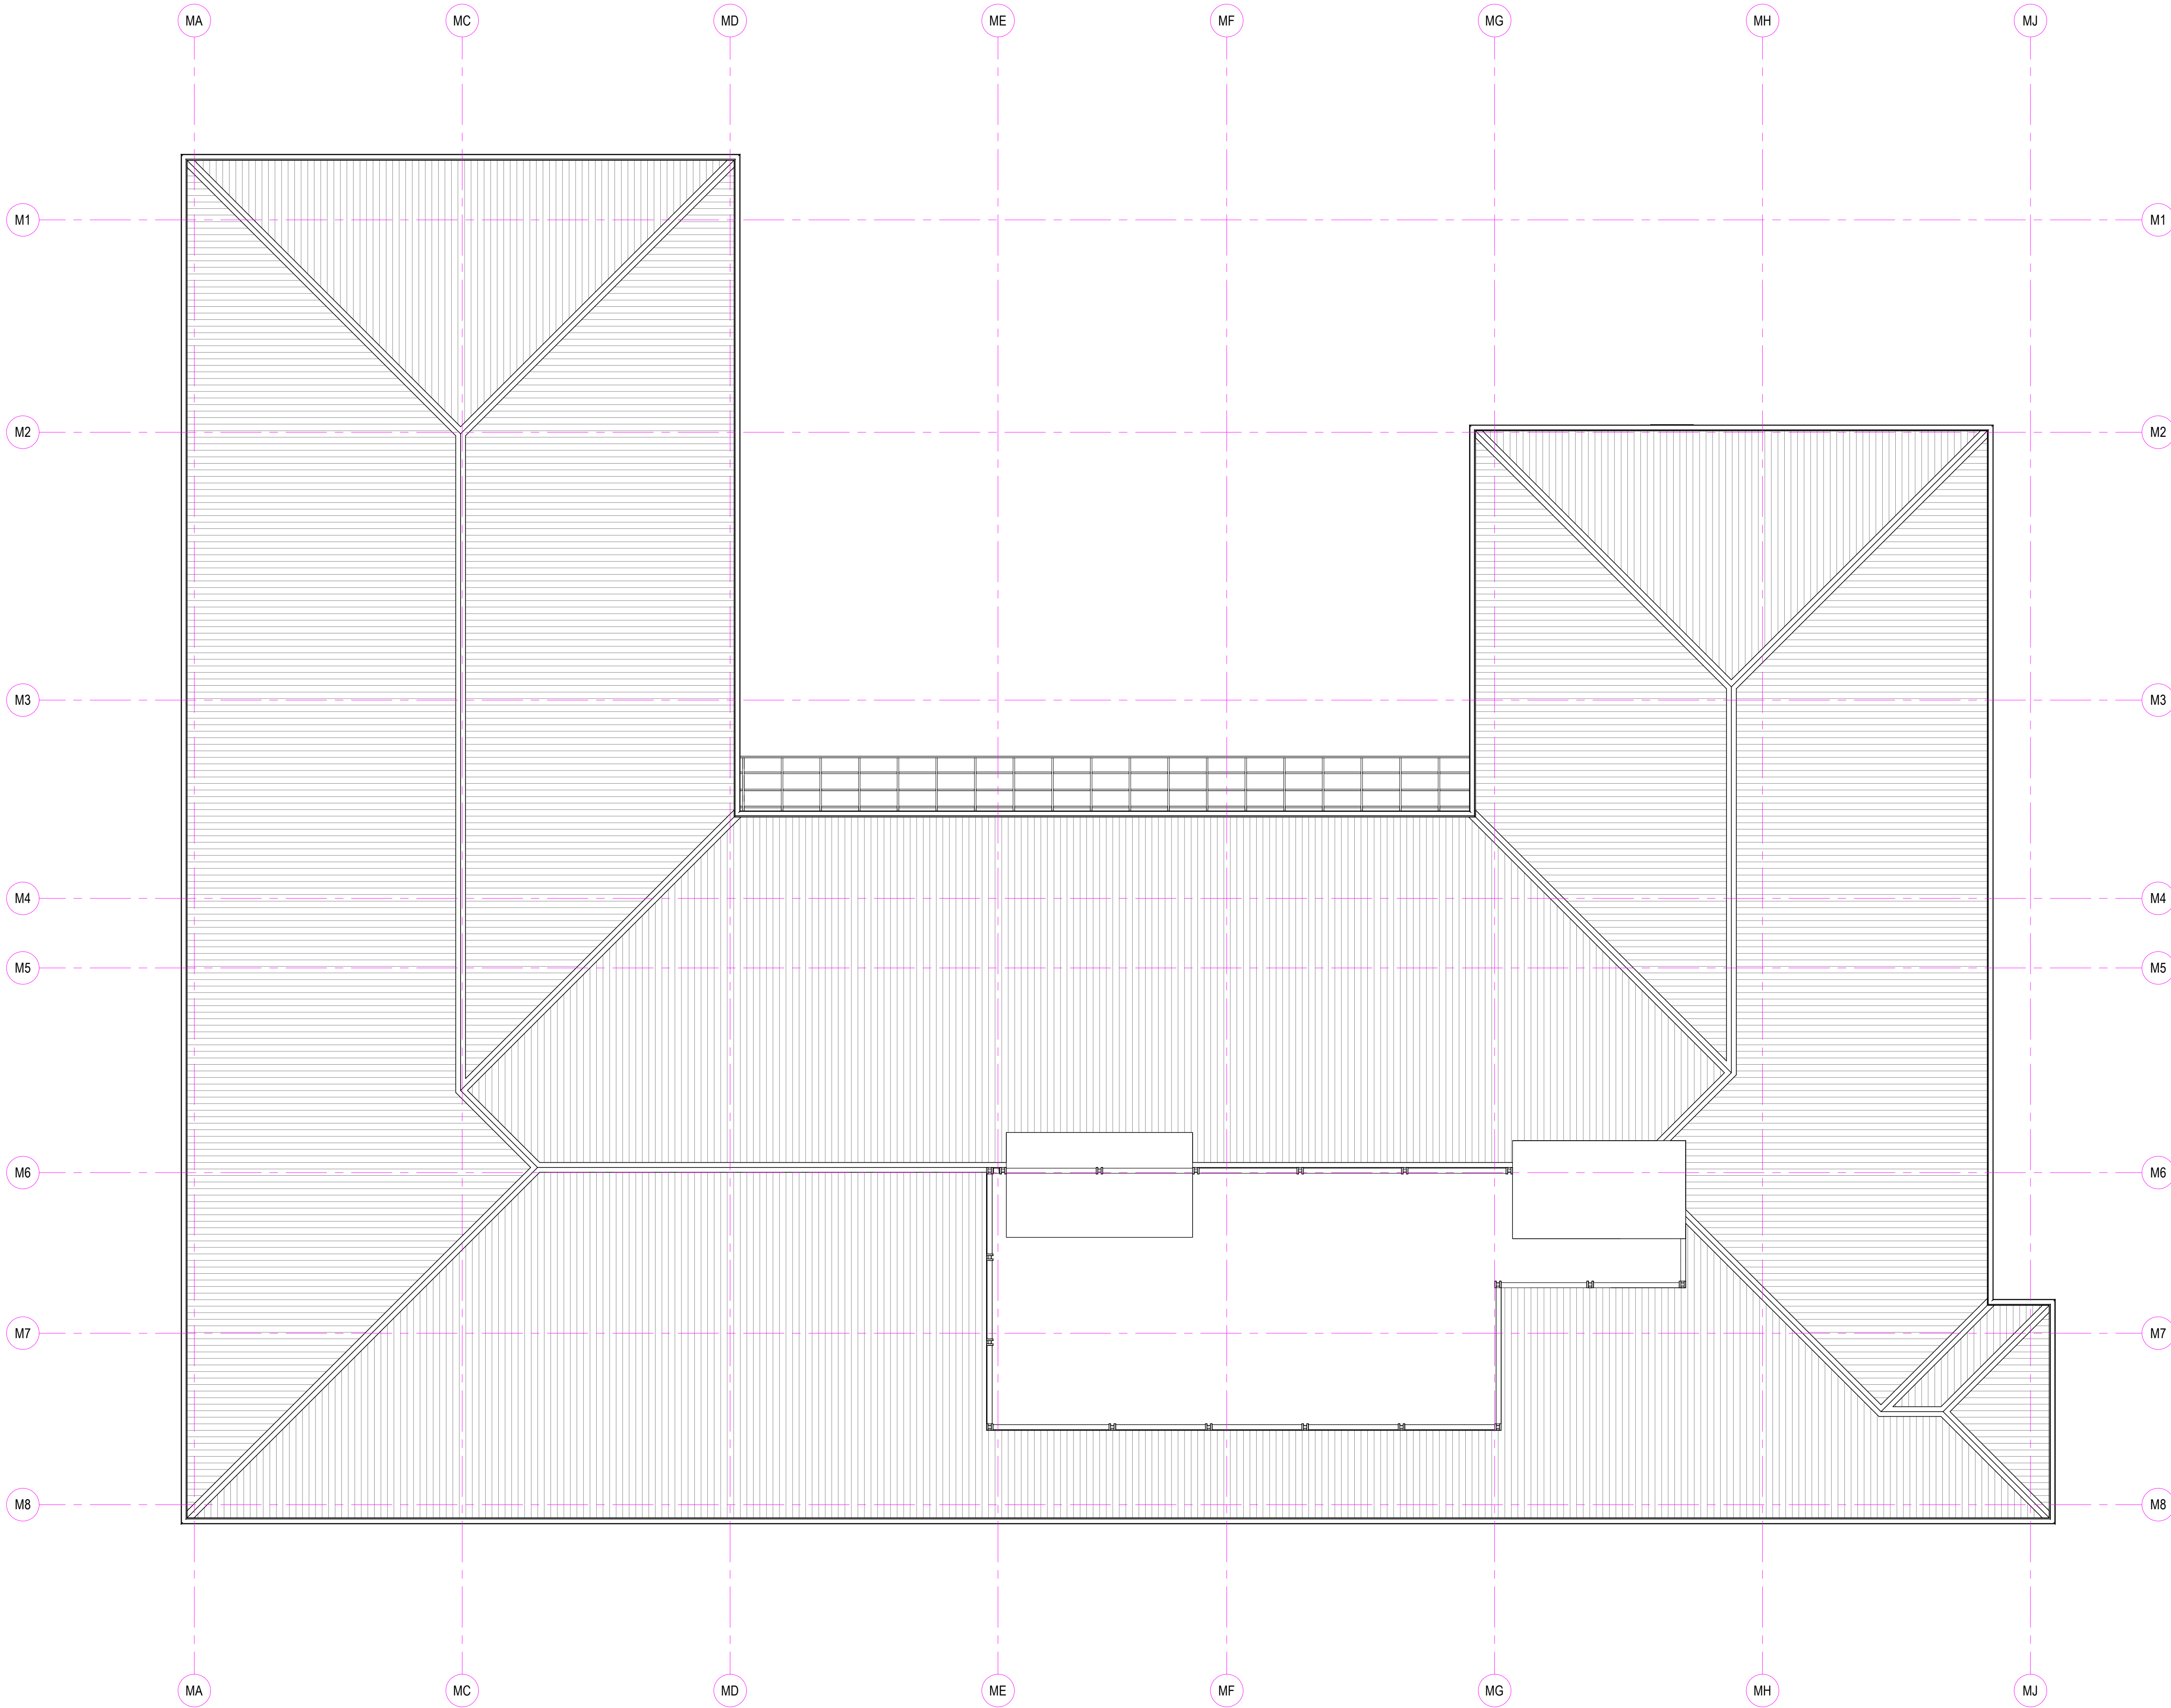

6 ROOF PLAN
Scale 1 : 100

Revision/Issue	Date
a Issue for Coordination - 90% DD	2024.03.28
P1 Consolidated Set-to-date / SMG Comments	2025.08.15
P2 ISSUE FOR CONTRACT	2025.10.10

**Clarke
Hopkins
Clarke**

ClarkeHopkinsClarke

Melbourne
L9, Melbourne Connect
700 Swanston Street
Carlton Victoria 3053
Telephone (03) 9419 4340
Email studio@chc.com.au
www.chc.com.au

Sydney
3/78 Campbell Street
Sunny Hills NSW 2010
Telephone (02) 9221 9200
Email studio@chc.com.au
www.chc.com.au

Scale	1 : 100 @ A1
Date	01/03/2024
Drawn	
Architect	



Project
Summerset Oakleigh
52 Golf Road, Oakleigh South, VIC

Drawing
Wall Set out Plan - Roof Floor

Drawing No.
230185/A1245

P2

FOR CONTRACT